



平面図

S=1:500

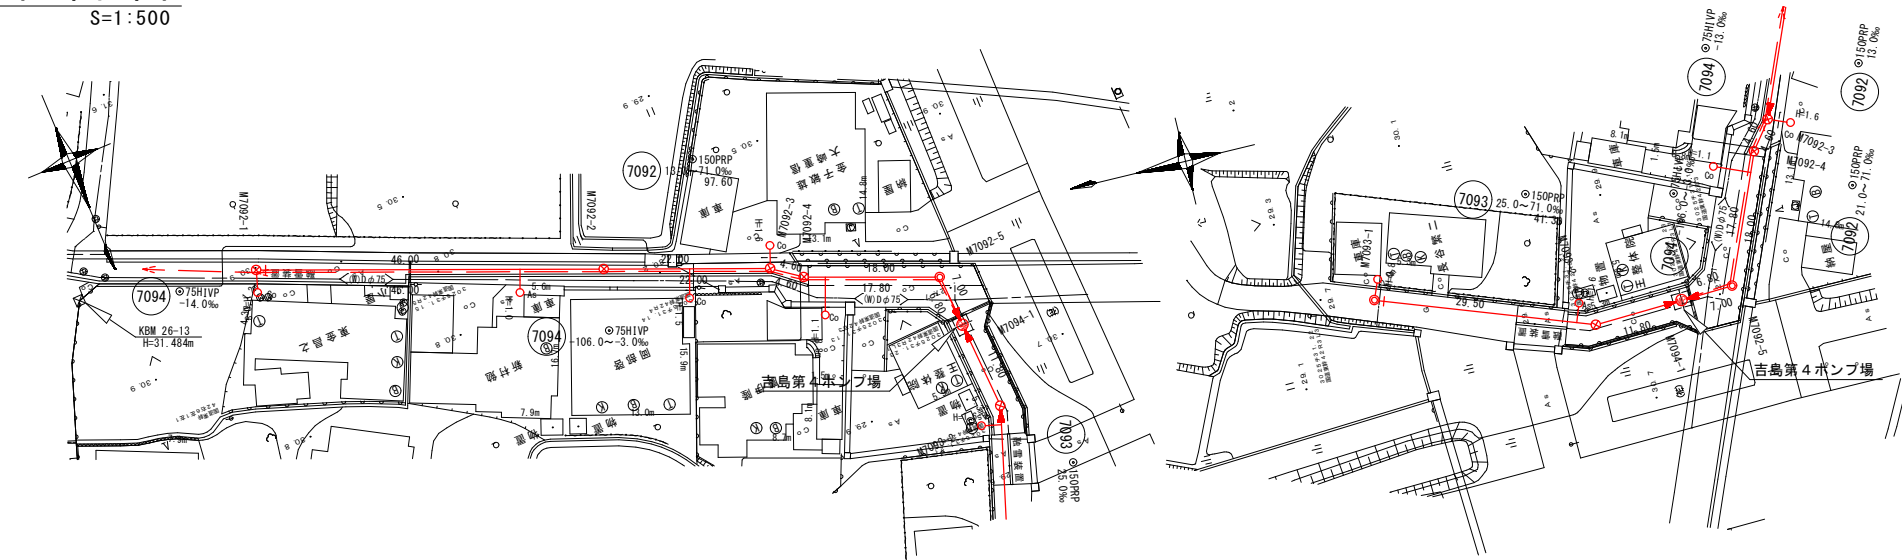

縦断面図

V=1:100
H=1:500

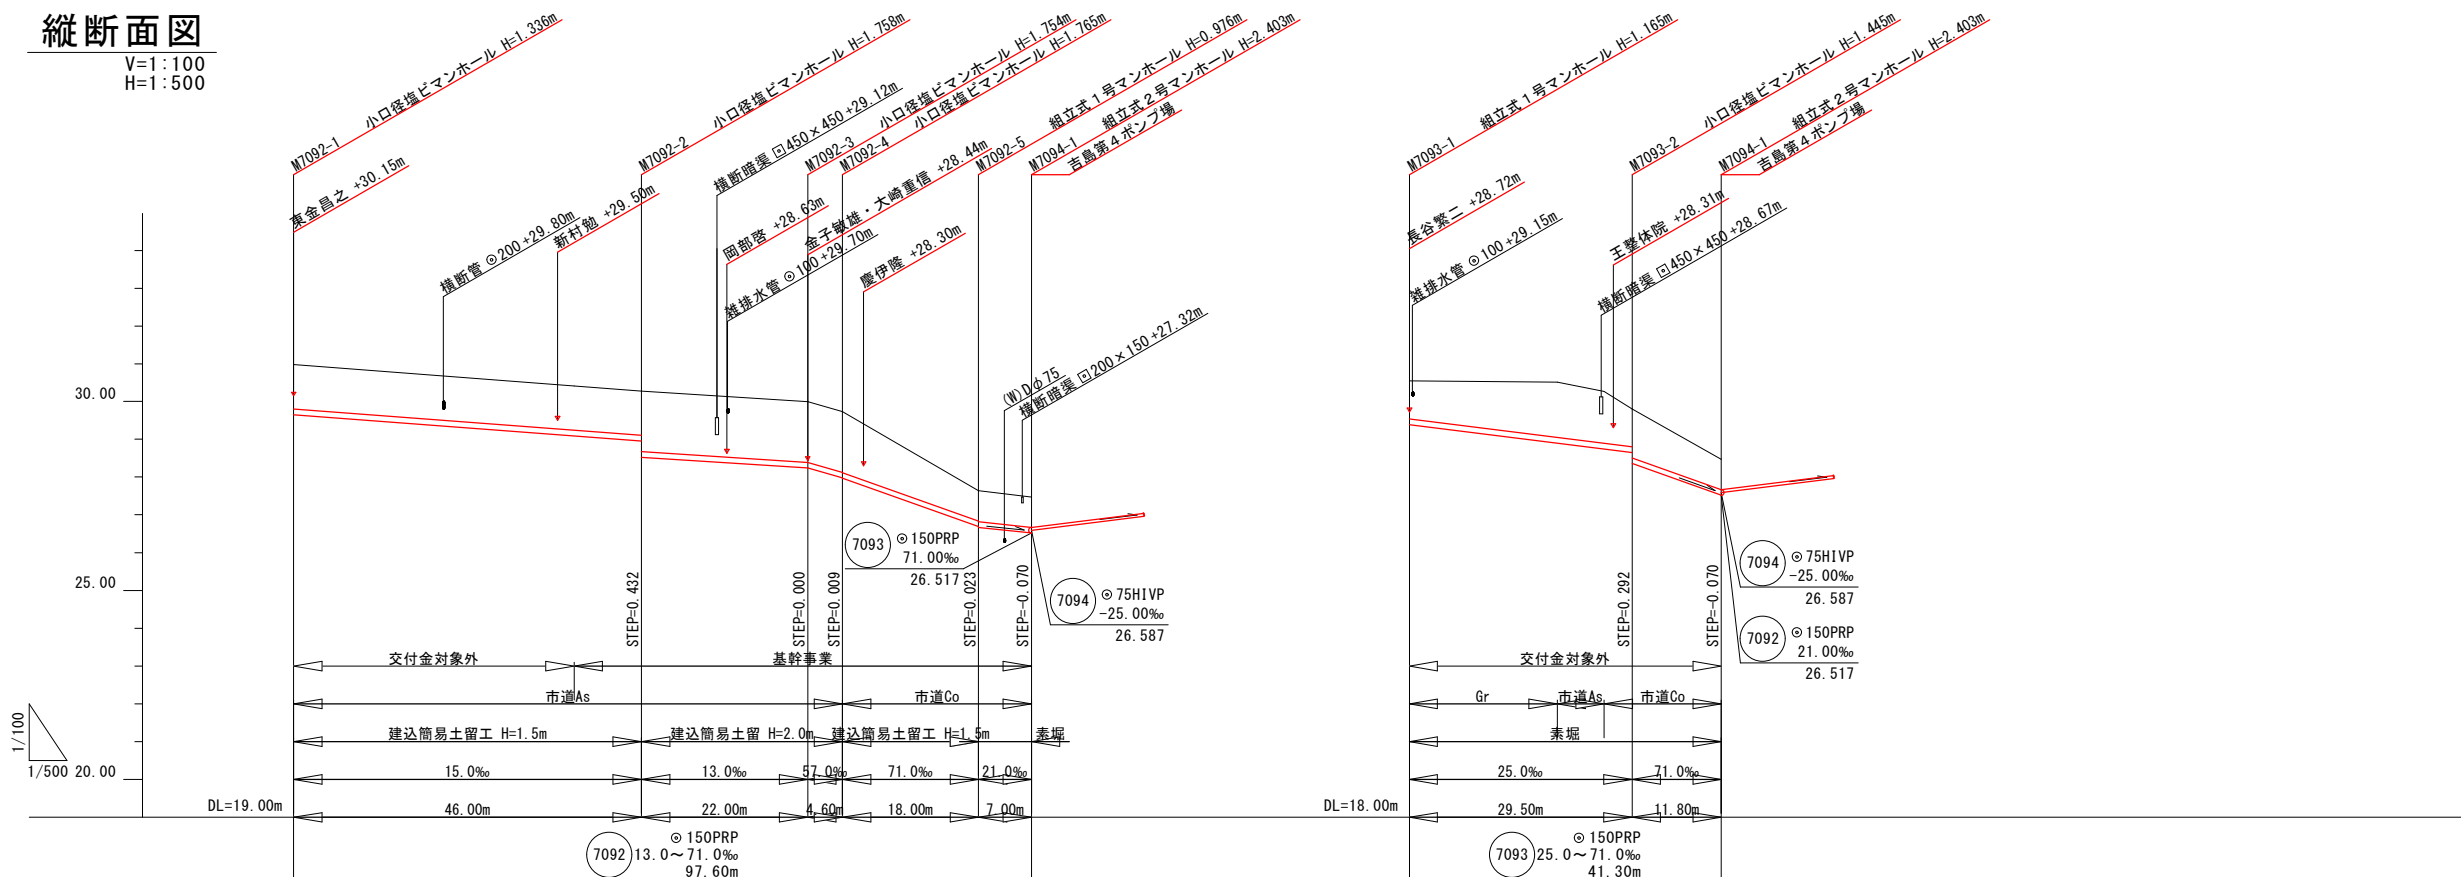

凡 例	
記 号	名 称
—○—	既 設 管 路
—○—	計 画 管 路
---○---	将 来 計 画
◎	1 号 マンホール
⊙	構 円 マンホール
Ⓜ	マンホールポンプ場
⊗	φ小口径塩ビ製マンホール
⊙	副管付マンホール
—○—	汚水樹

土 被 り	1.18	1.18	1.17 1.61	1.60	1.60 0.80 0.82	0.80	1.01	1.47	1.38 1.00 1.29	0.80
掘 削 深	1.44	1.44	1.43 1.86	1.86 1.87	1.06 1.06 1.06	1.06	1.27	1.73	1.63 1.26 1.55	1.06
管 底 高	29.644	29.088	28.954 28.522	28.236 27.974 27.965	26.687 26.664 26.517 26.587	26.517 26.587	28.385	27.895	29.27 27.740 27.647 27.355	26.517 26.587
現況地盤高	30.98	30.42	30.28	29.99 29.73	27.64 27.47	27.47	29.55	29.52	28.80	27.47
追加距離	0.00	37.10	46.00	68.00 72.60	90.60 97.60	97.60	0.00	19.60	25.80 29.50	41.30
単 距 離	0.00	37.10	8.90	22.00 4.60	18.00 7.00	7.00	0.00	19.60	6.20 3.70	11.80
測 点	M7092-1	+37.10 M7092-2	M7092-3 M7092-4	M7092-5 M7094-1	M7093-1	M7093-2	M7094-1			


7092

7093

平成27年度 魚津市特定環境保全公共下水道事業				
工 事 名	市道吉島8号線管渠築造工事（その3） (管路番号)			
工事場所	吉島 地内	縮 尺	縦 横	S=1:100 S=1:500
図 面 名	平面縦断面図 (6/15)			
課 長	係 長	設 計	製 図	図 面 番 号
				No. 11 / 31
魚津市上下水道局下水道課				


平面図

S=1:500

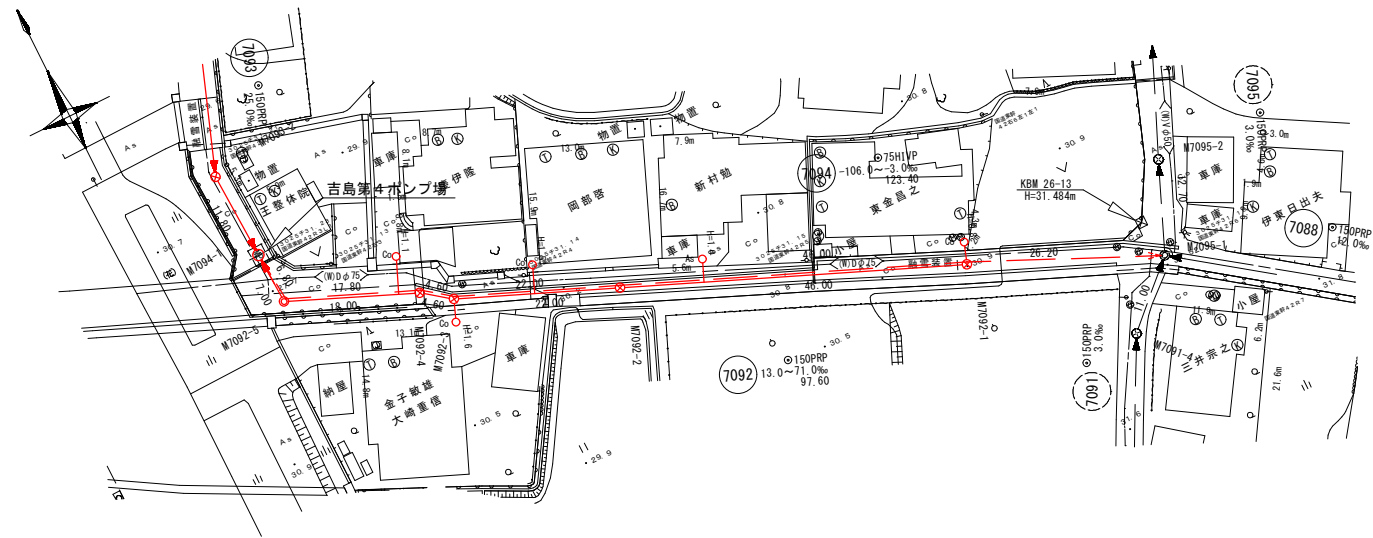

縦断面図

V=1:100
H=1:500











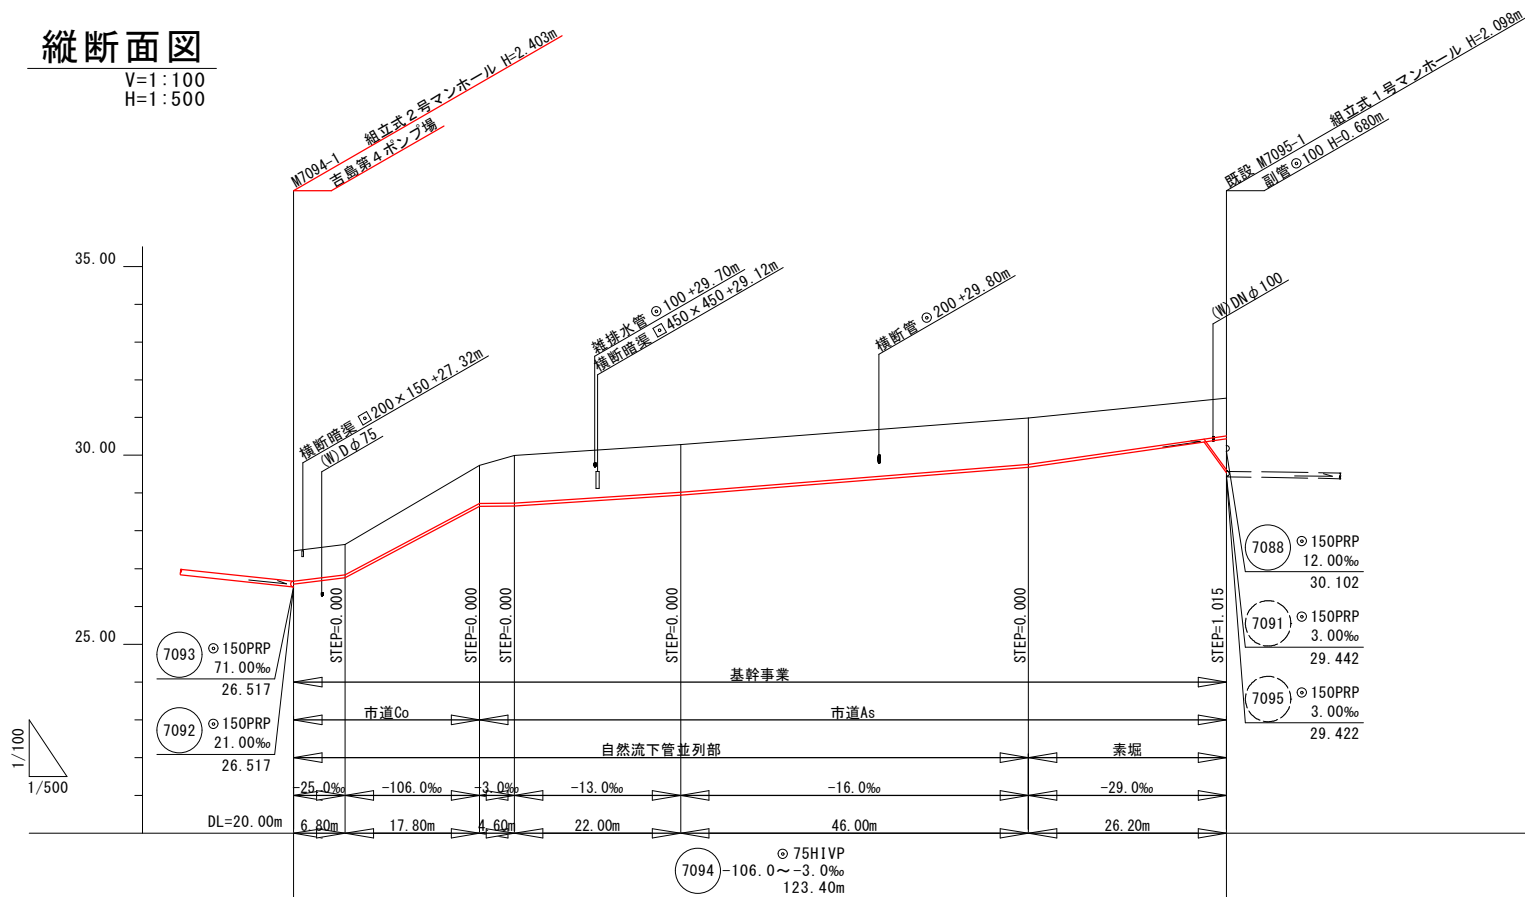


凡 例	
記 号	名 称
—○—	既 設 管 路
—○—	計 画 管 路
---○---	将 来 計 画
◎	1 号 マ ン ホ ー ル
⊙	構 円 マ ン ホ ー ル
MP	マンホールポンプ場
⊗	φ小口径塩ビ製マンホール
⊙	副管付マンホール
—○	汚水樹

土 被 り	0.80	0.80	1.00	1.25	1.22	1.00
掘 削 深	0.99	0.99	1.19	1.44	1.41	1.19
管 底 高	26.517 26.587	26.757	28.647 28.659	28.945	29.681	30.437 29.422
現況地盤高	27.47	27.64	29.73 29.99	30.28	30.98	31.52
追加距離	0.00	6.80	24.60 29.20	51.20	97.20	123.40
単 距 離	0.00	6.80	17.80 4.60	22.00	46.00	26.20
測 点	M7094-1					M7095-1

7094


平成27年度 魚津市特定環境保全公共下水道事業					
工 事 名	市道吉島8号線管渠築造工事（その3）				
	(管路番号)				
工事場所	吉島 地内	縮 尺	縦 横	S=1:100 S=1:500	
図 面 名	平面縦断面図 (7/15)				
課 長	係 長	設 計	製 図	図 面 番 号	
				No. 12	31
魚津市上下水道局下水道課					

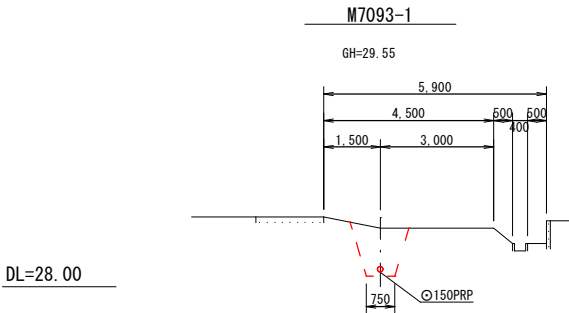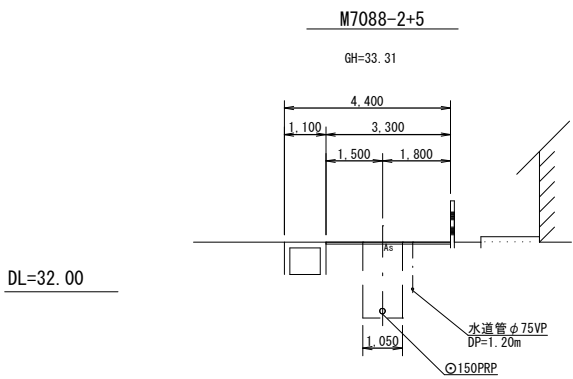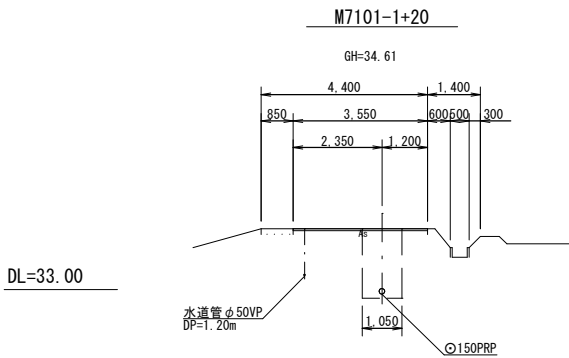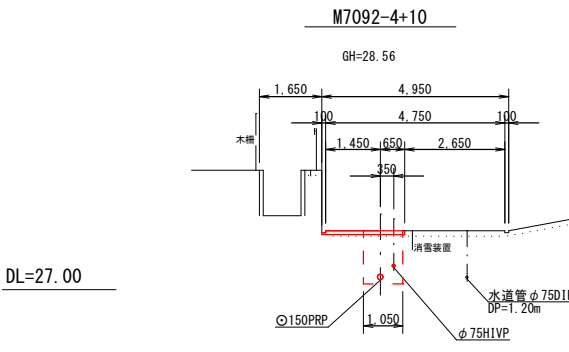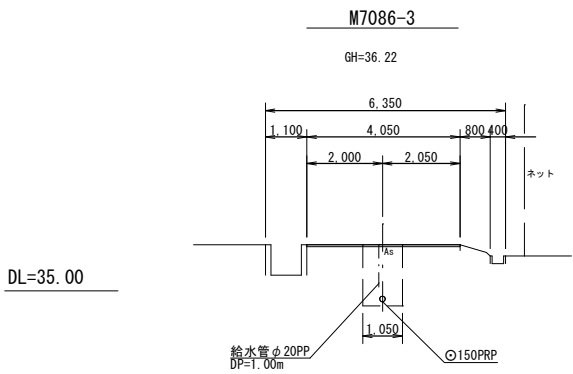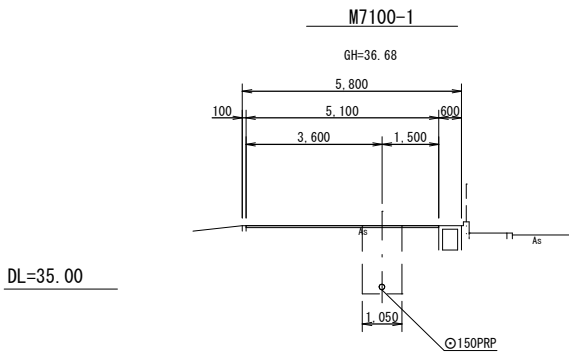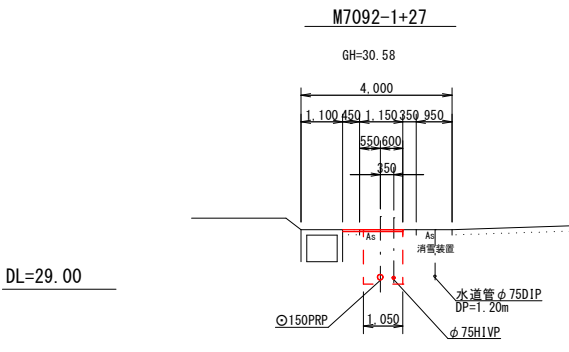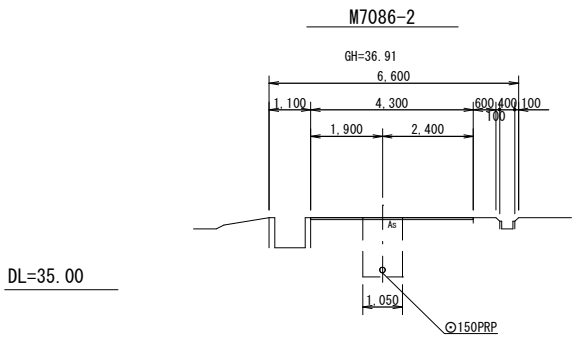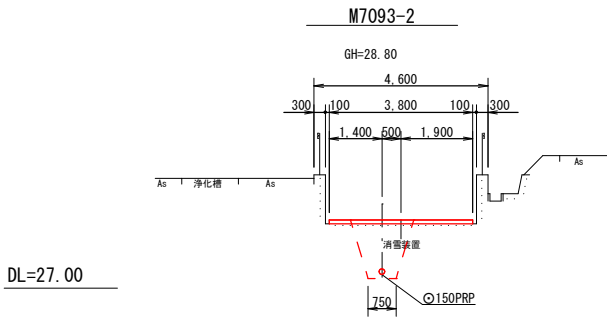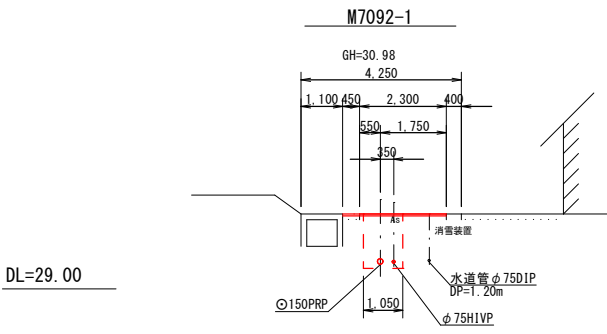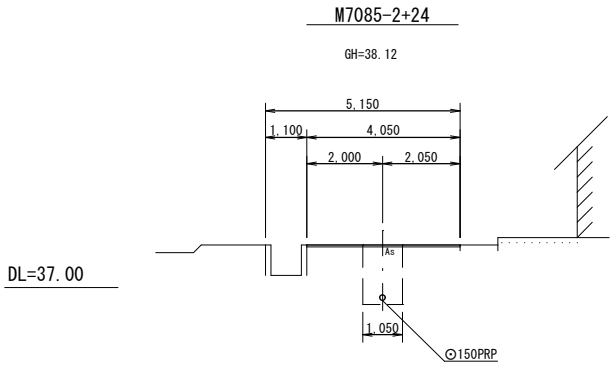

平成 27 年度 魚津市特定環境保全公共下水道事業				
工 事 名	市道吉島 8 号線管渠築造工事 (その 3)			
工事場所	吉島	地内	縮 尺	S=1:100
図 面 名	横断面図 (2/4)			
課 長	係 長	設 計	製 図	図 面 番 号
				No. 22 / 31
魚津市上下水道局下水道課				


圧送管詳細図（管番号7094）

配管平面図
S = 1 : 200

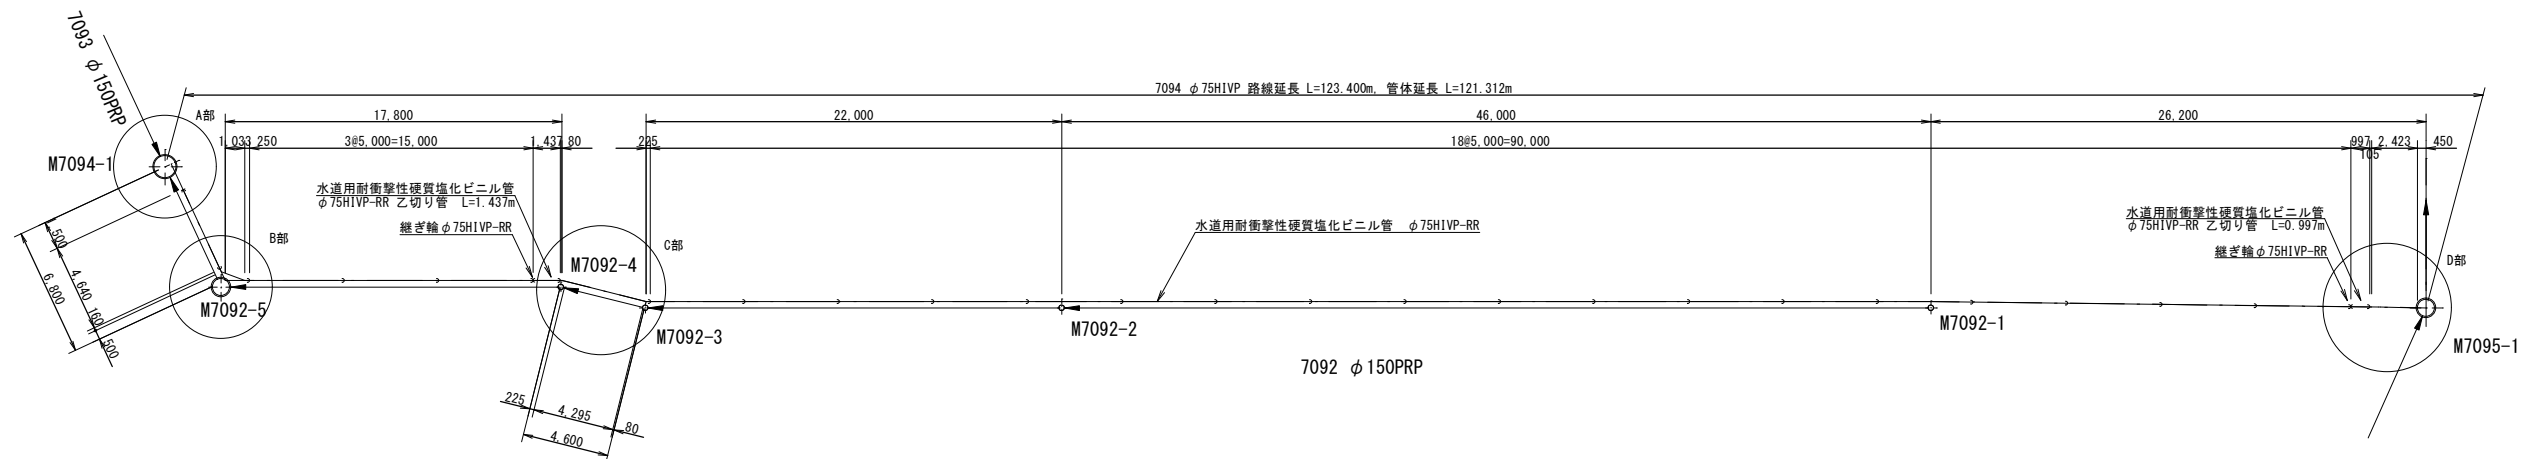


D部詳細図
S = 1 : 50

断面図

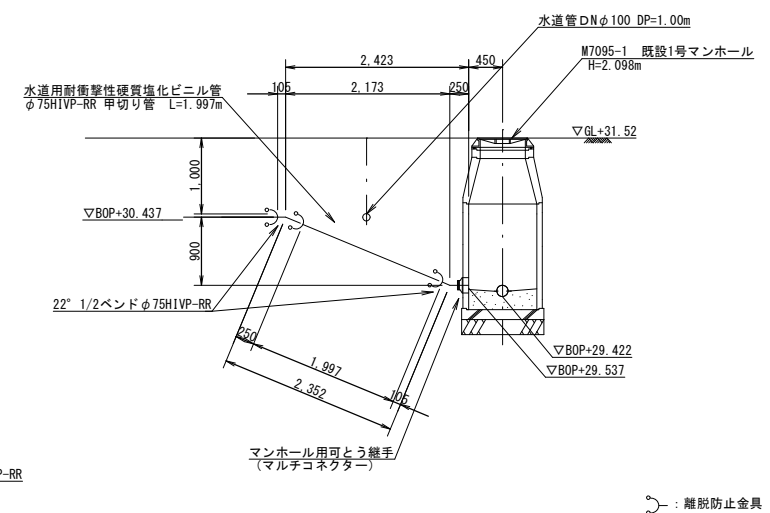


A部詳細図
S = 1 : 50

平面図

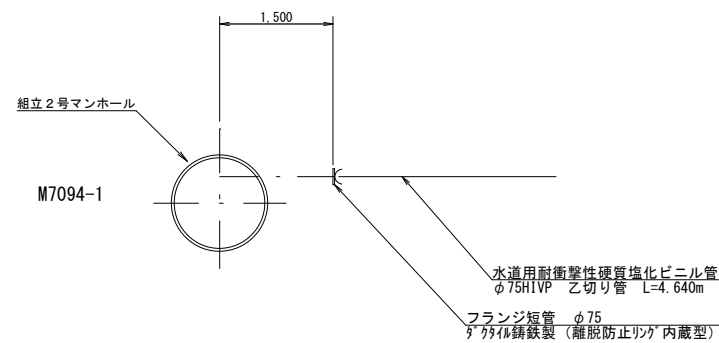


B部詳細図
S = 1 : 50

平面図

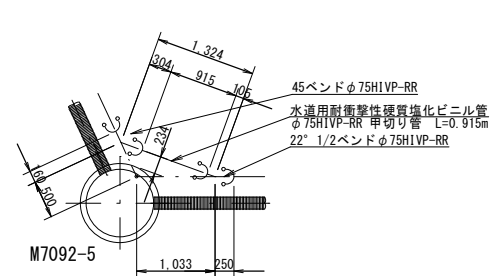

C部詳細図
S = 1 : 50

平面図

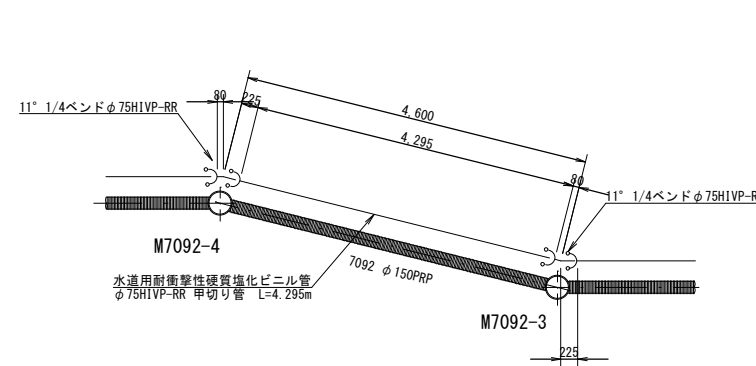


平成 27 年度 魚津市特定環境保全公共下水道事業					
工 事 名		市道吉島8号線管渠築造工事（その3） (管路番号)			
工事場所		吉島	地内	縮 尺	図示
図 面 名		圧送管詳細図			
課 長	係 長	設 計	製 図	図 面 番 号	
				No. 25	31
魚津市上下水道局下水道課					

压送管土工断面図

S=1 : 20


压送管单独部

(素堀部)

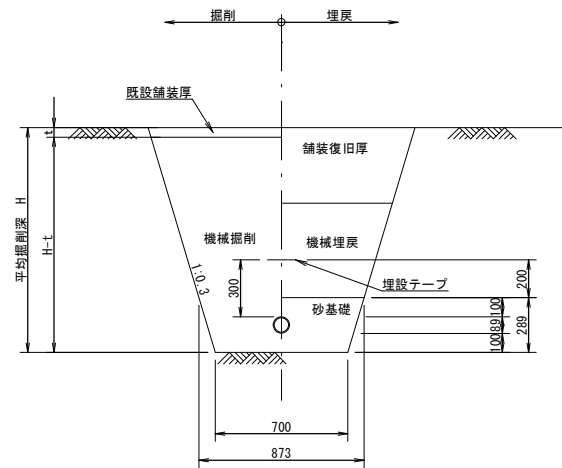


压送管・自然流下管並列部

(素堀部)

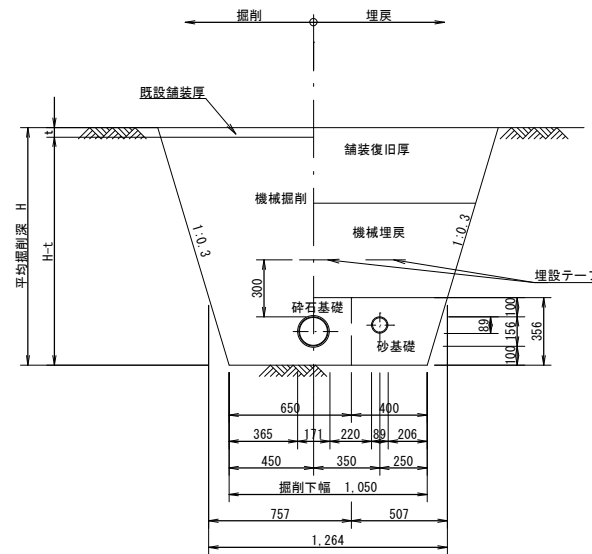


压送管・自然流下管並列部

(建込簡易土留 H=1.50m)

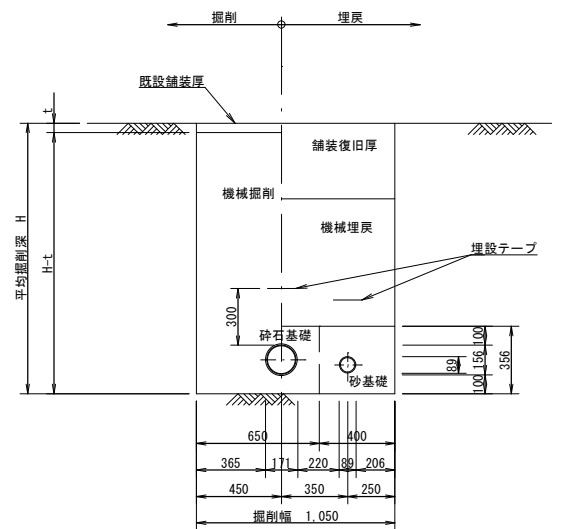

压送管・自然流下管並列部

(建込簡易土留 H=2.00m)

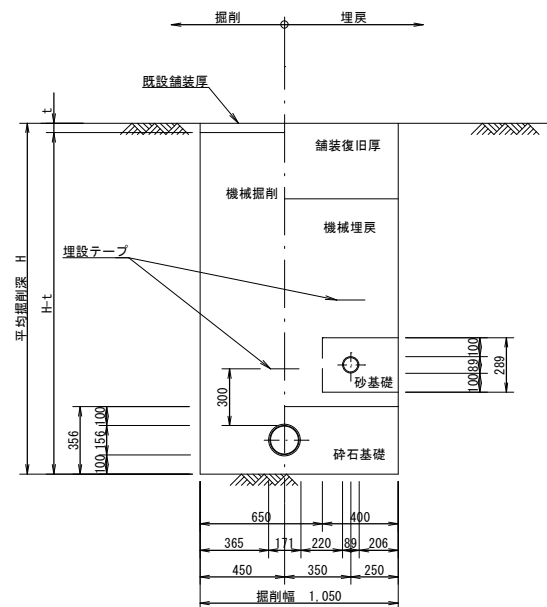

平成 27 年度 魚津市特定環境保全公共下水道事業				
工 事 名	市道吉島 8 号線管渠築造工事 (その 3) (管路 番号)			
工事場所	吉 島	地 内	縮 尺	S=1:20
図 面 名	压送管土工断面図			
課 長	係 長	設 計	製 図	図 面 番 号
				No. 26 / 31
魚津市上下水道局下水道課				


消雪工標準図

S=1 : 20


付帯工平面図

S=1 : 200



断面図

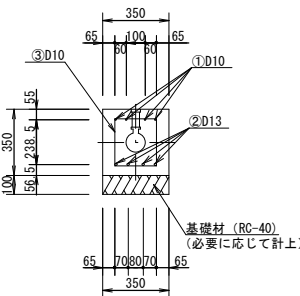

側面図

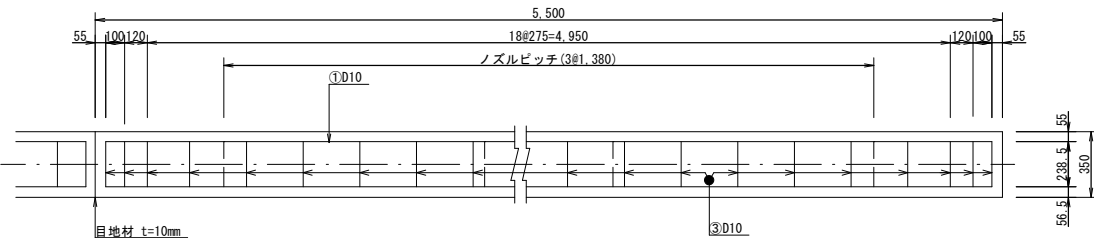

平面図

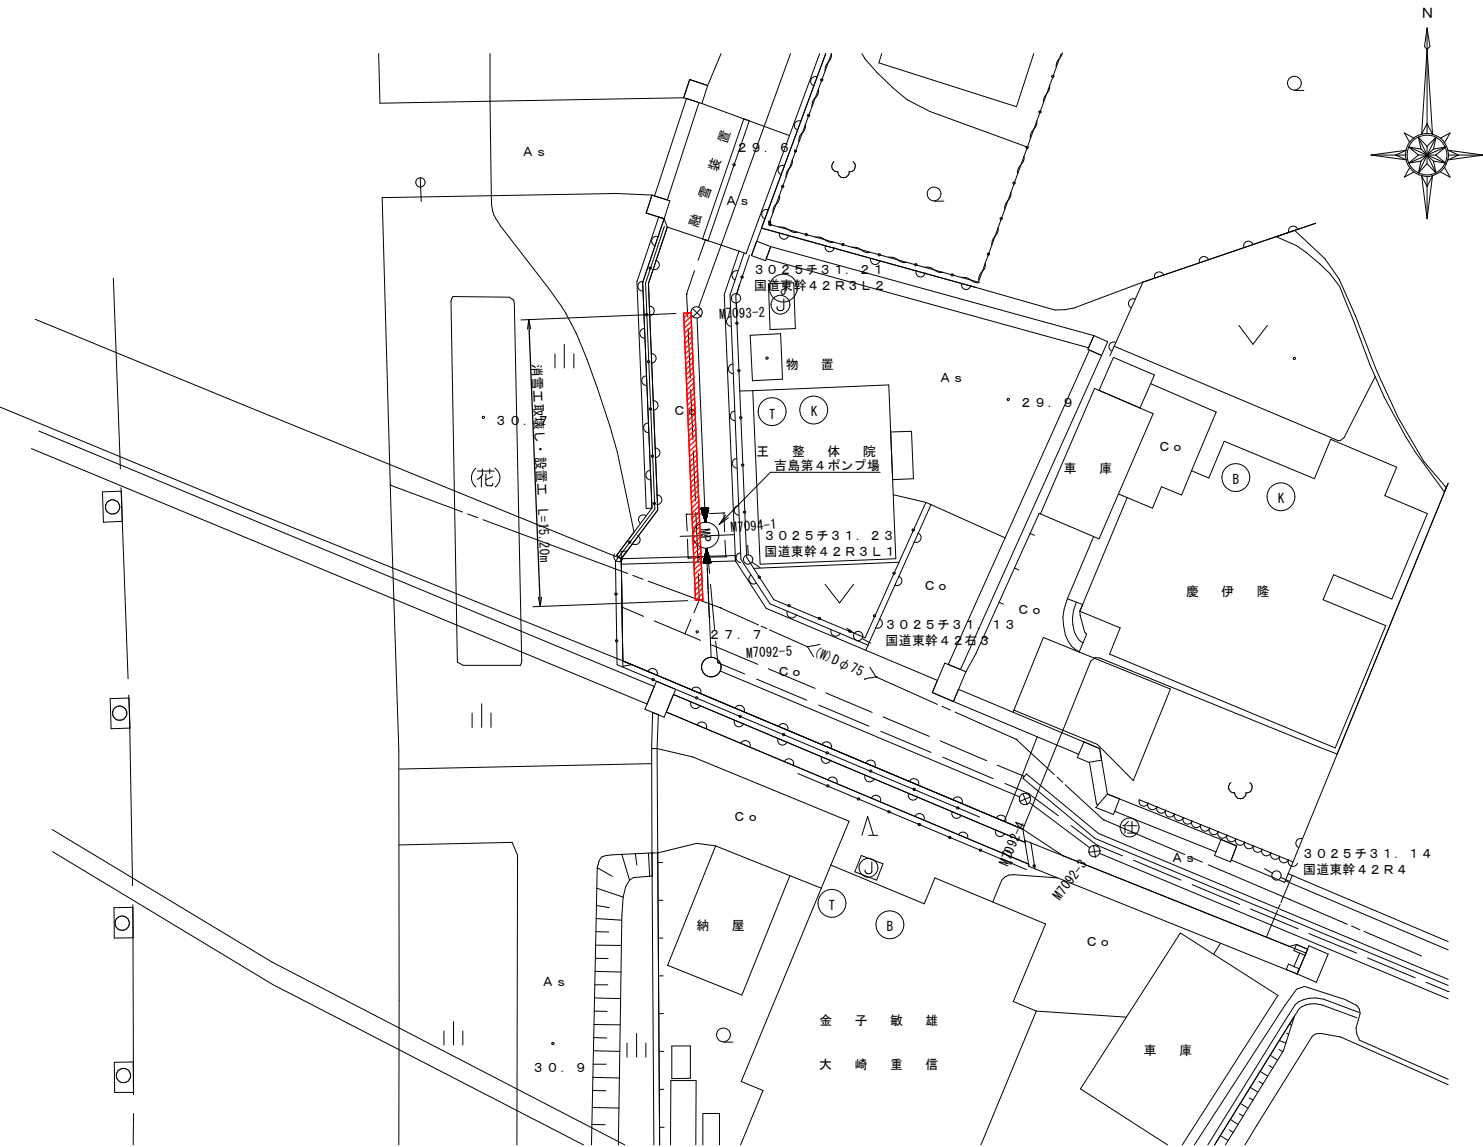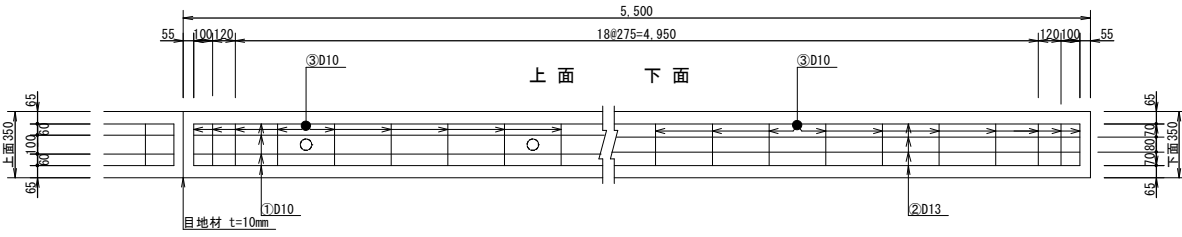


平成 27 年度 魚津市特定環境保全公共下水道事業					
工 事 名		市道吉島8号線管渠築造工事（その3） (管路番号)			
工事場所		吉島	地内	縮 尺	図示
図 面 名		付帯工図			
課 長	係 長	設 計	製 図	図 面 番 号	
				No. 27 / 31	
魚津市上下水道局下水道課					


吉島第4ポンプ場構造図

S=1 : 30


平面図

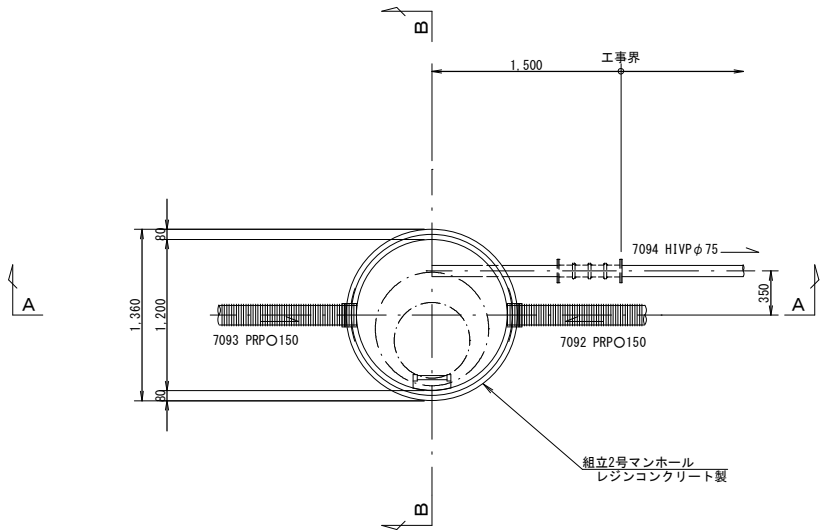

A-A断面図

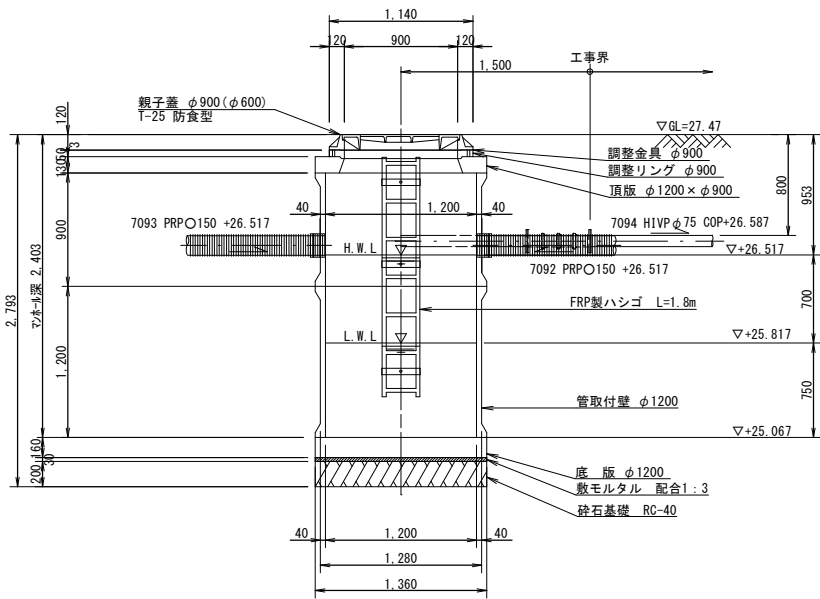


B-B断面図

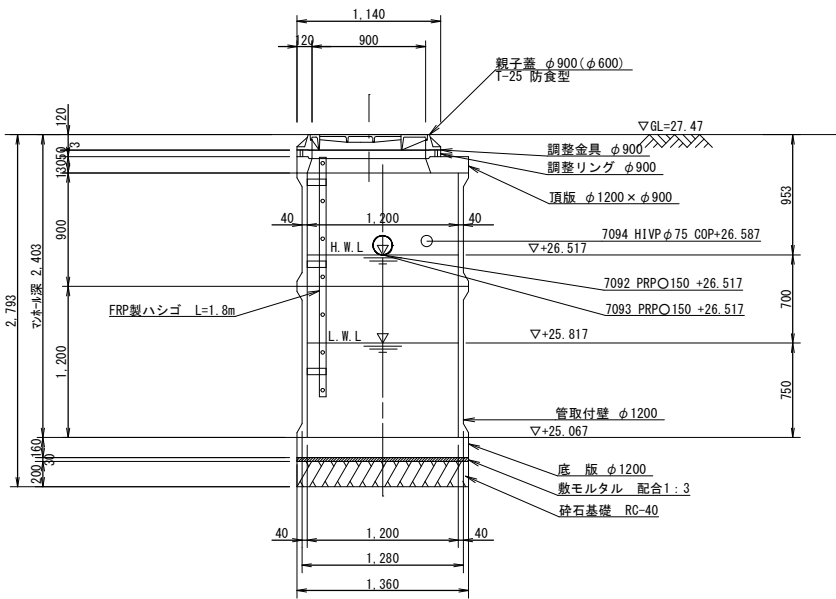


立坑仮設図

S=1 : 30

平面図

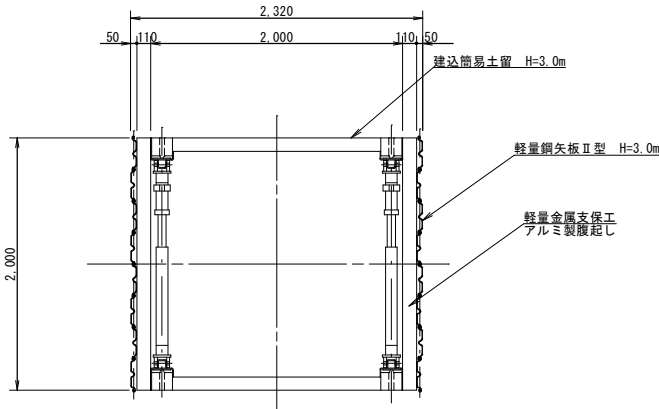


断面図

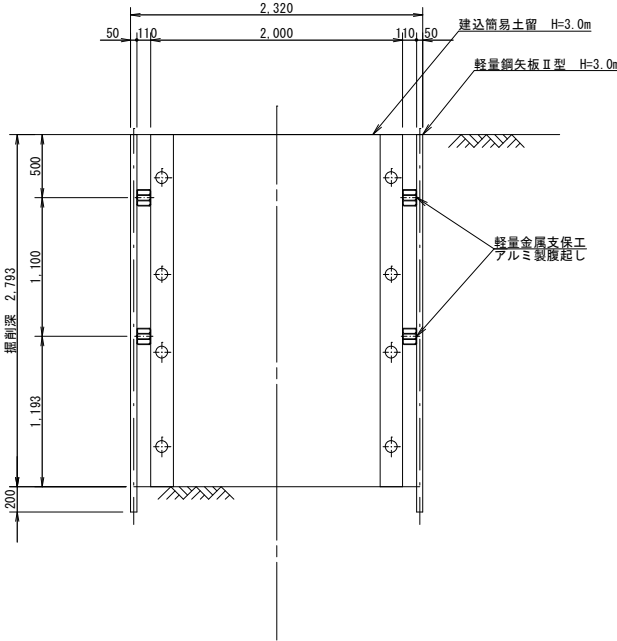


平成 27 年度 魚津市特定環境保全公共下水道事業					
工 事 名		市道吉島 8 号線管渠築造工事（その 3） (管路番号)			
工事場所		吉島 地内	縮 尺	S=1:30	
図 面 名		吉島第 4 ポンプ場構造図			
課 長	係 長	設 計	製 図	図 面 番 号	
				No. 28 / 31	
魚津市上下水道局下水道課					


平 面 図

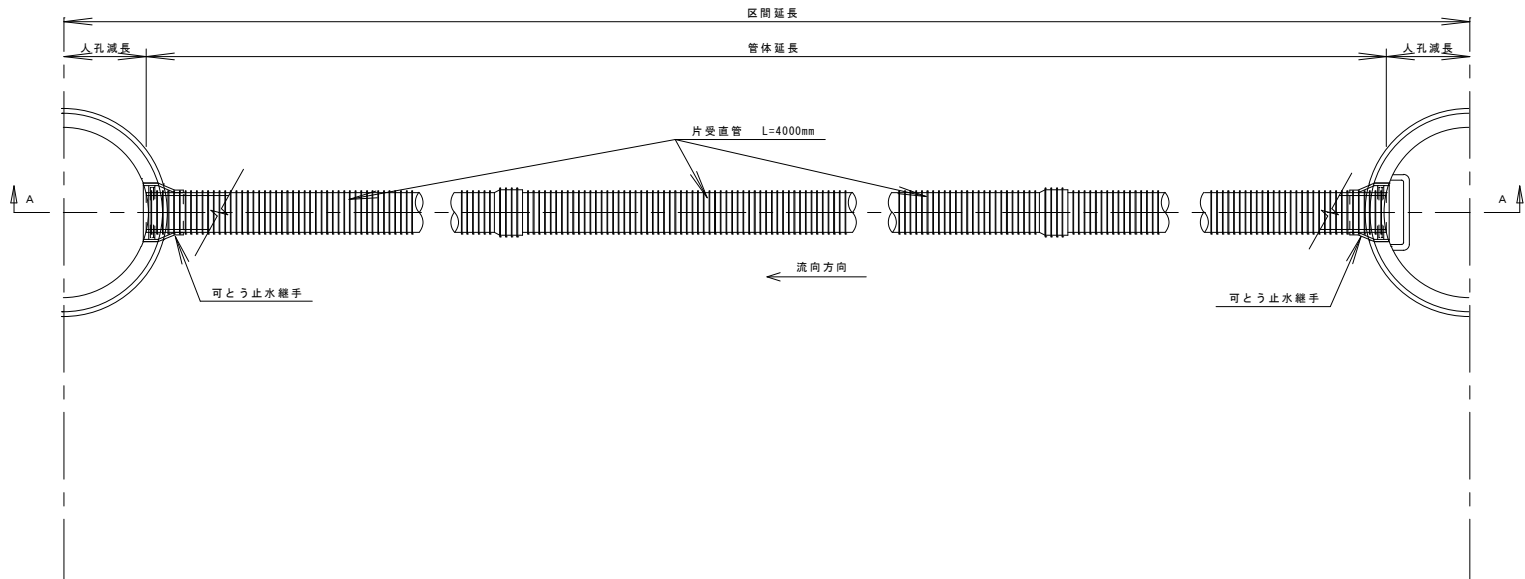


A—A 断 面 図

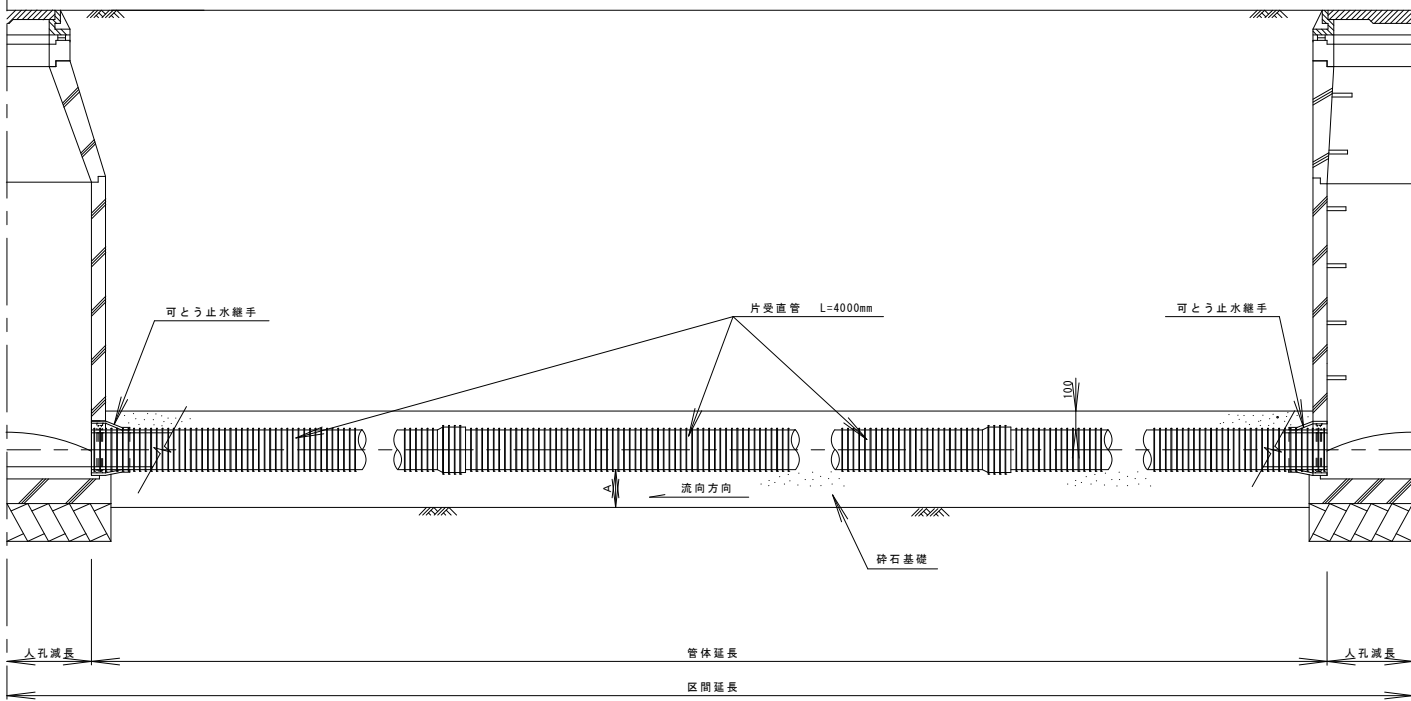

掘削深 H ≥ 1.50m

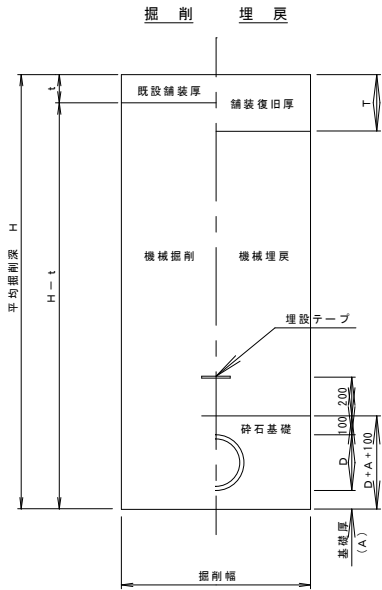


掘削深 H < 1.50m

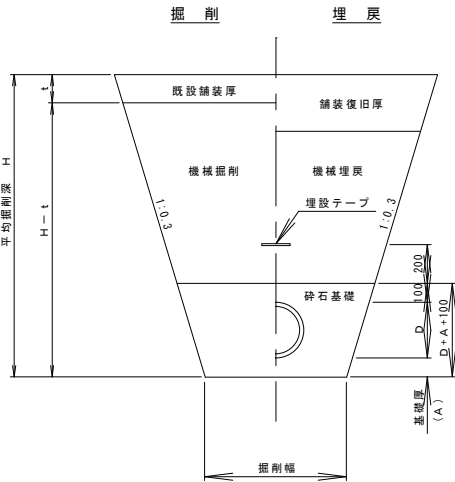


リブ付硬質塩化ビニル管寸法図

断 面 図

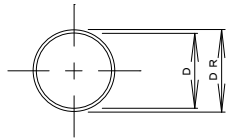

側 面 図

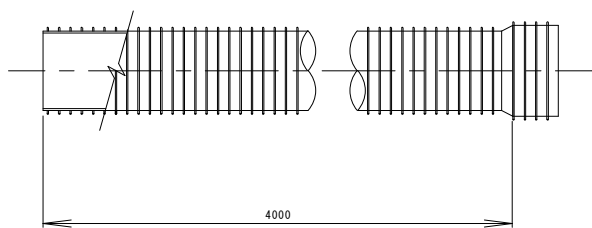


管渠寸法表

名 称	記 号	呼 び 径	D	D R	t	掘削幅	A
リブ付硬質塩化ビニル管	PRP	150	155.5	171.0	2.4	1050	100
リブ付硬質塩化ビニル管	PRP	200	205.5	228.8	2.4	1050	100
リブ付硬質塩化ビニル管	PRP	250	256.1	286.2	2.7	1050	150
リブ付硬質塩化ビニル管	PRP	300	307.1	343.6	3.0	1050	150
リブ付硬質塩化ビニル管	PRP	350	357.4	400.6	3.1	1100	150

管据付寸法表

名 称	H	a	b	H R	人孔せん孔径
φ 150	11	160	154	8	262
φ 200	14	215	204	12	314
φ 250	18	268	254	15	366
φ 300	22	322	305	18	420
φ 350	25	376	355	22	474

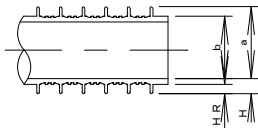

平成 2 7 年 度 魚 津 市 特 定 環 境 保 全 公 共 下 水 道 事 業

工 事 名 (管路 _____)
番号 _____

工事場所 地 内 縮 尺 1/20

図 面 名 リブ付硬質塩化ビニル管布設標準図


課 長 係 長 設 計 製 図 図 面 番 号

N o ①

魚 津 市 上 下 水 道 局 下 水 道 課


1号組立マンホール標準図

S=1/20

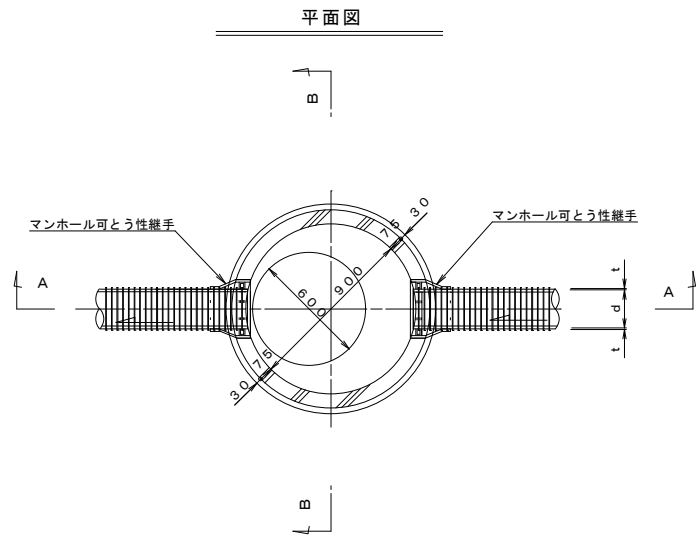


鉄蓋詳細図


S=1/10

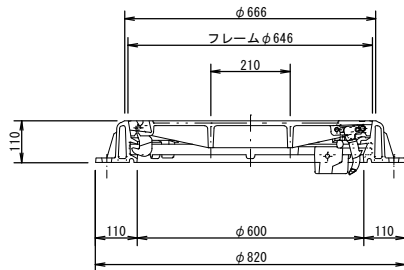

A-A断面図

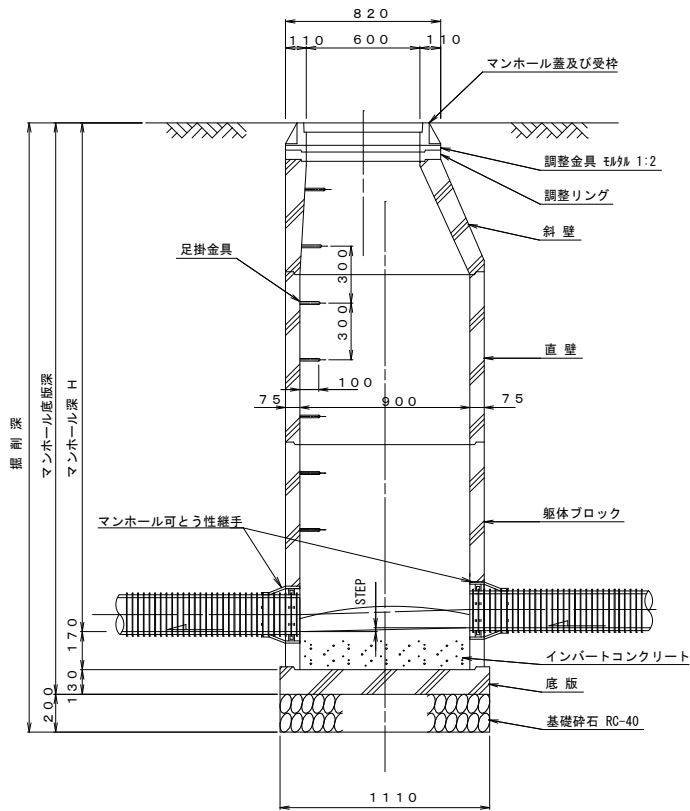


B-B断面図

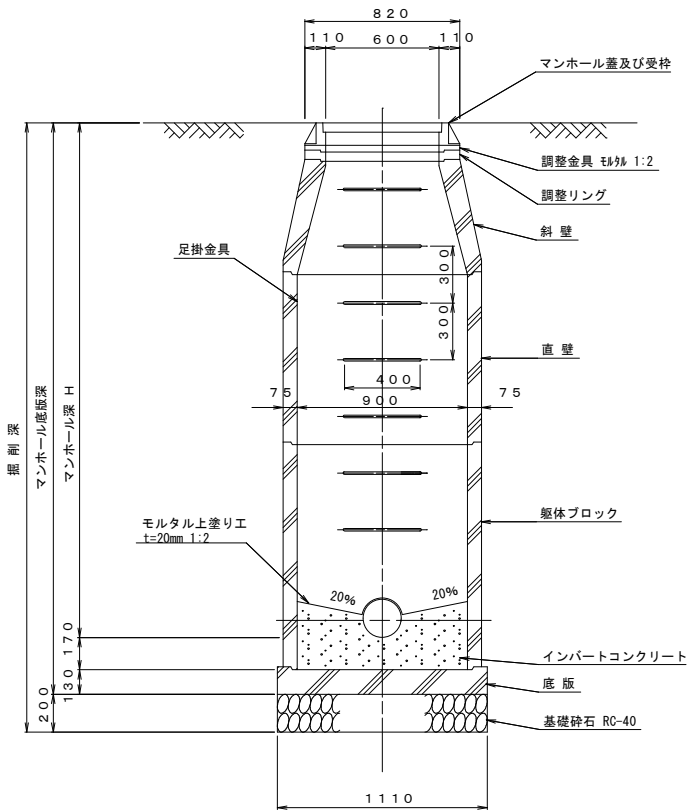


副管工詳細図

S=1/20

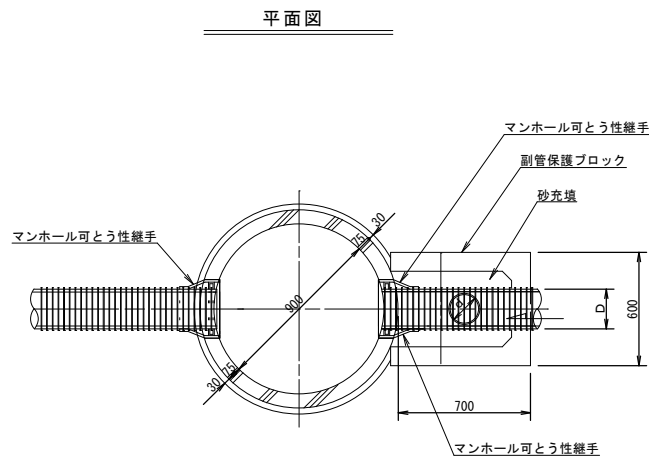

断面図

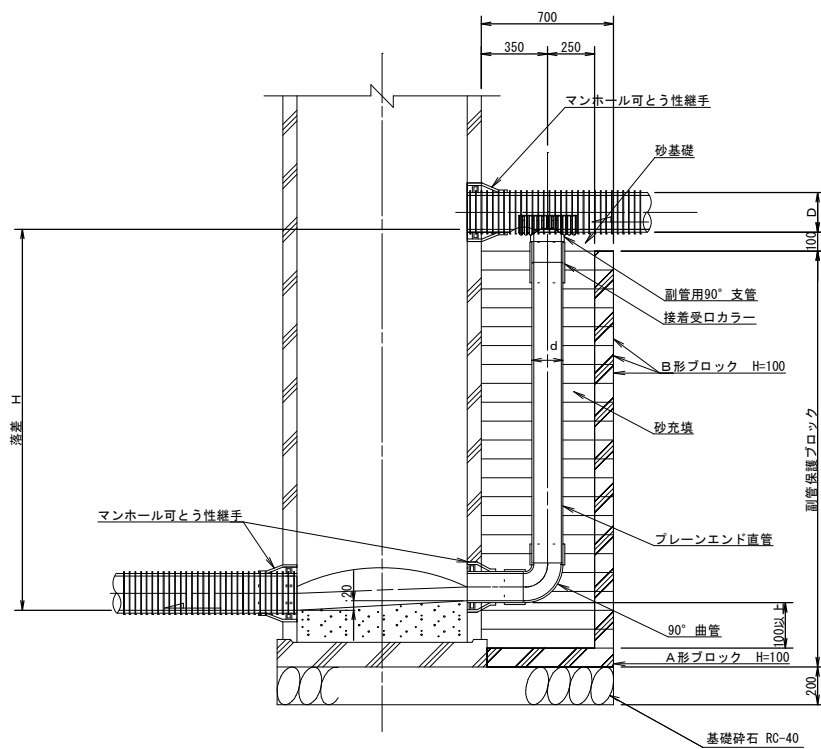


本管径	副管径	D	d
PRP φ150	VU φ100	156	114
PRP φ200	VU φ150	206	165
PRP φ250	VU φ200	256	216

平成27年度 魚津市特定環境保全公共下水道事業


工事名	(管路番号)		
工事場所	大海寺野 地内	縮尺	図示
図面名	1号組立マンホール標準図		
課長	係長	設計	製図 図面番号
			No. ②
魚津市上下水道局下水道課			

塩ビ製小型マンホール構造図


縦断面図
S=1:20

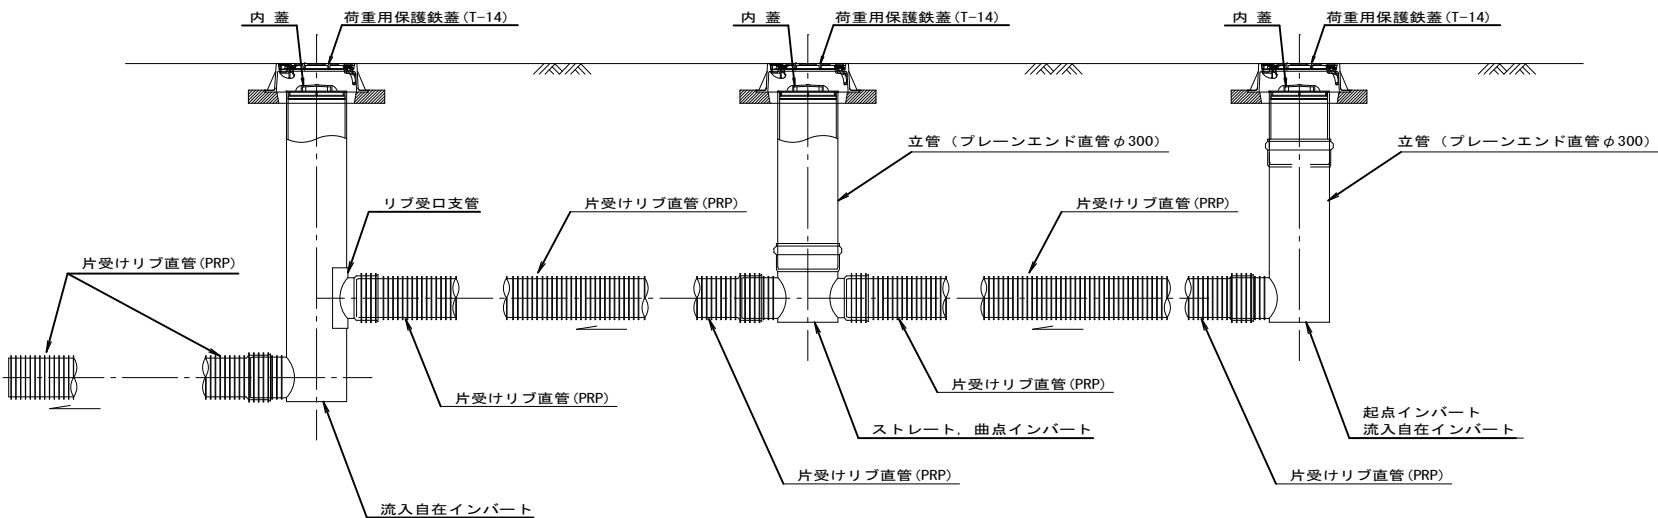



荷重用保護鉄蓋 (T-14)
Nonscale

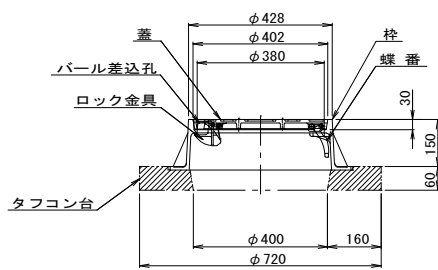

内蓋



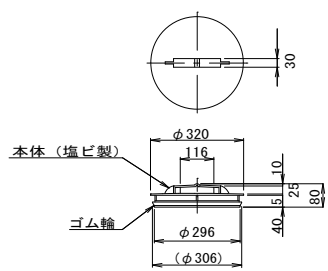


インバート平面図
S=1:10

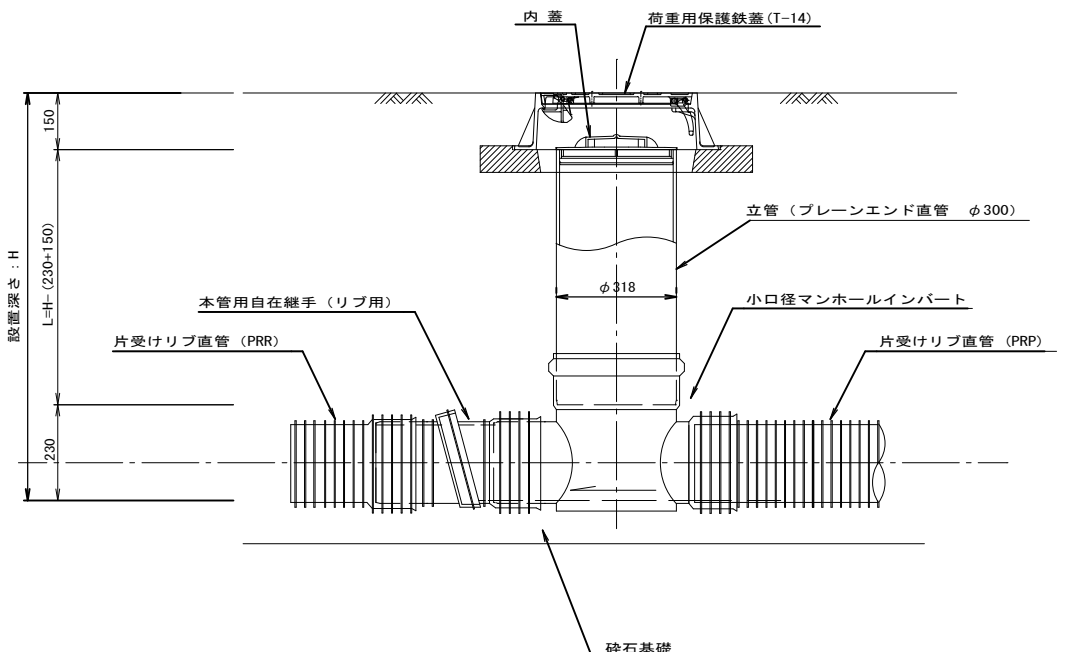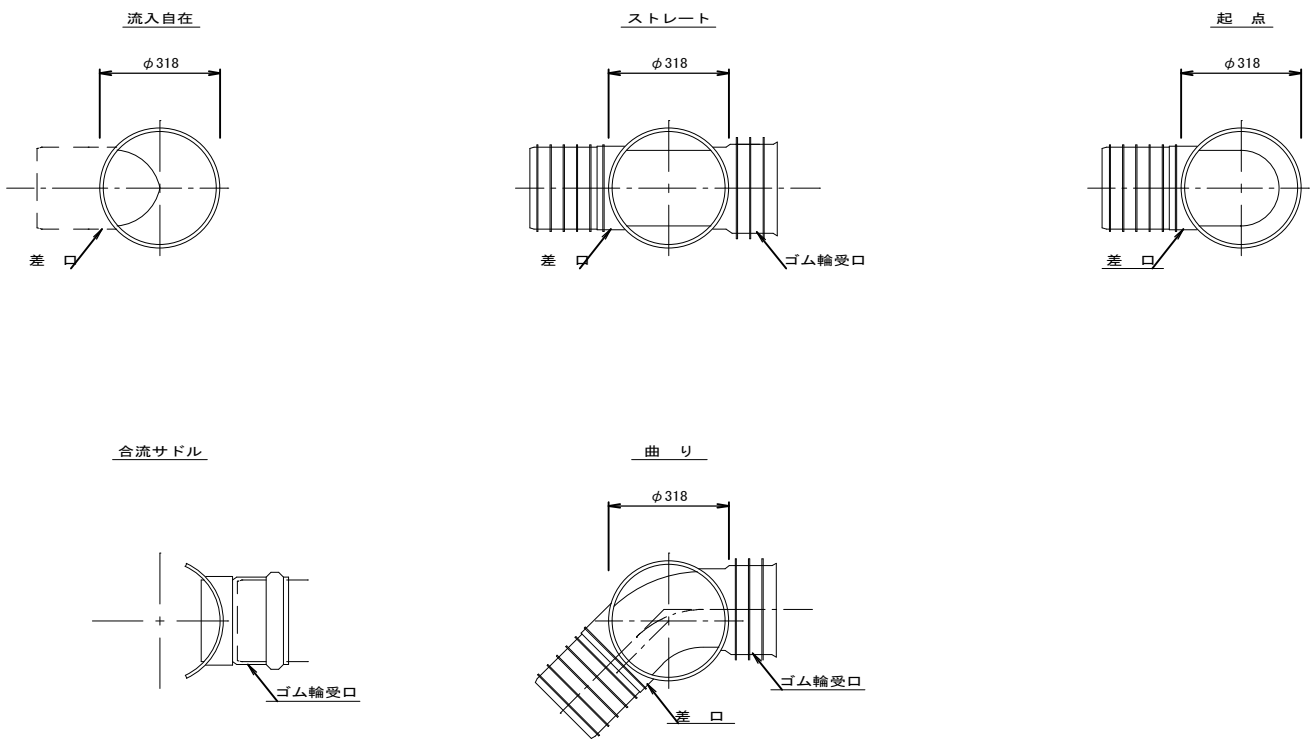

平成27年度 魚津市特定環境保全公共下水道事業					
工 事 名					
工 事 場 所		地 内		縮 尺	図 示
図 面 名		塩ビ製小口径マンホール構造図			
課 長	係 長	設 計	製 図	図 面 番 号	
				No. ③	
魚津市上下水道局下水道課					

取付管布設標準図

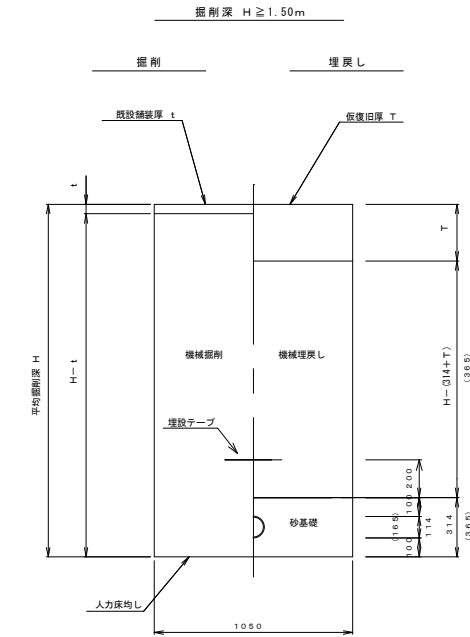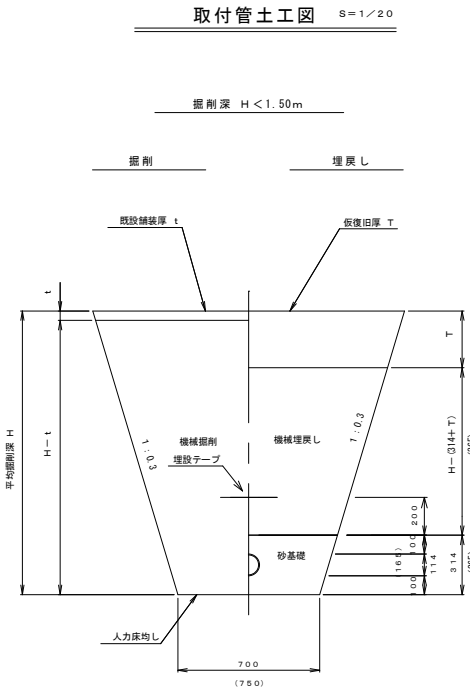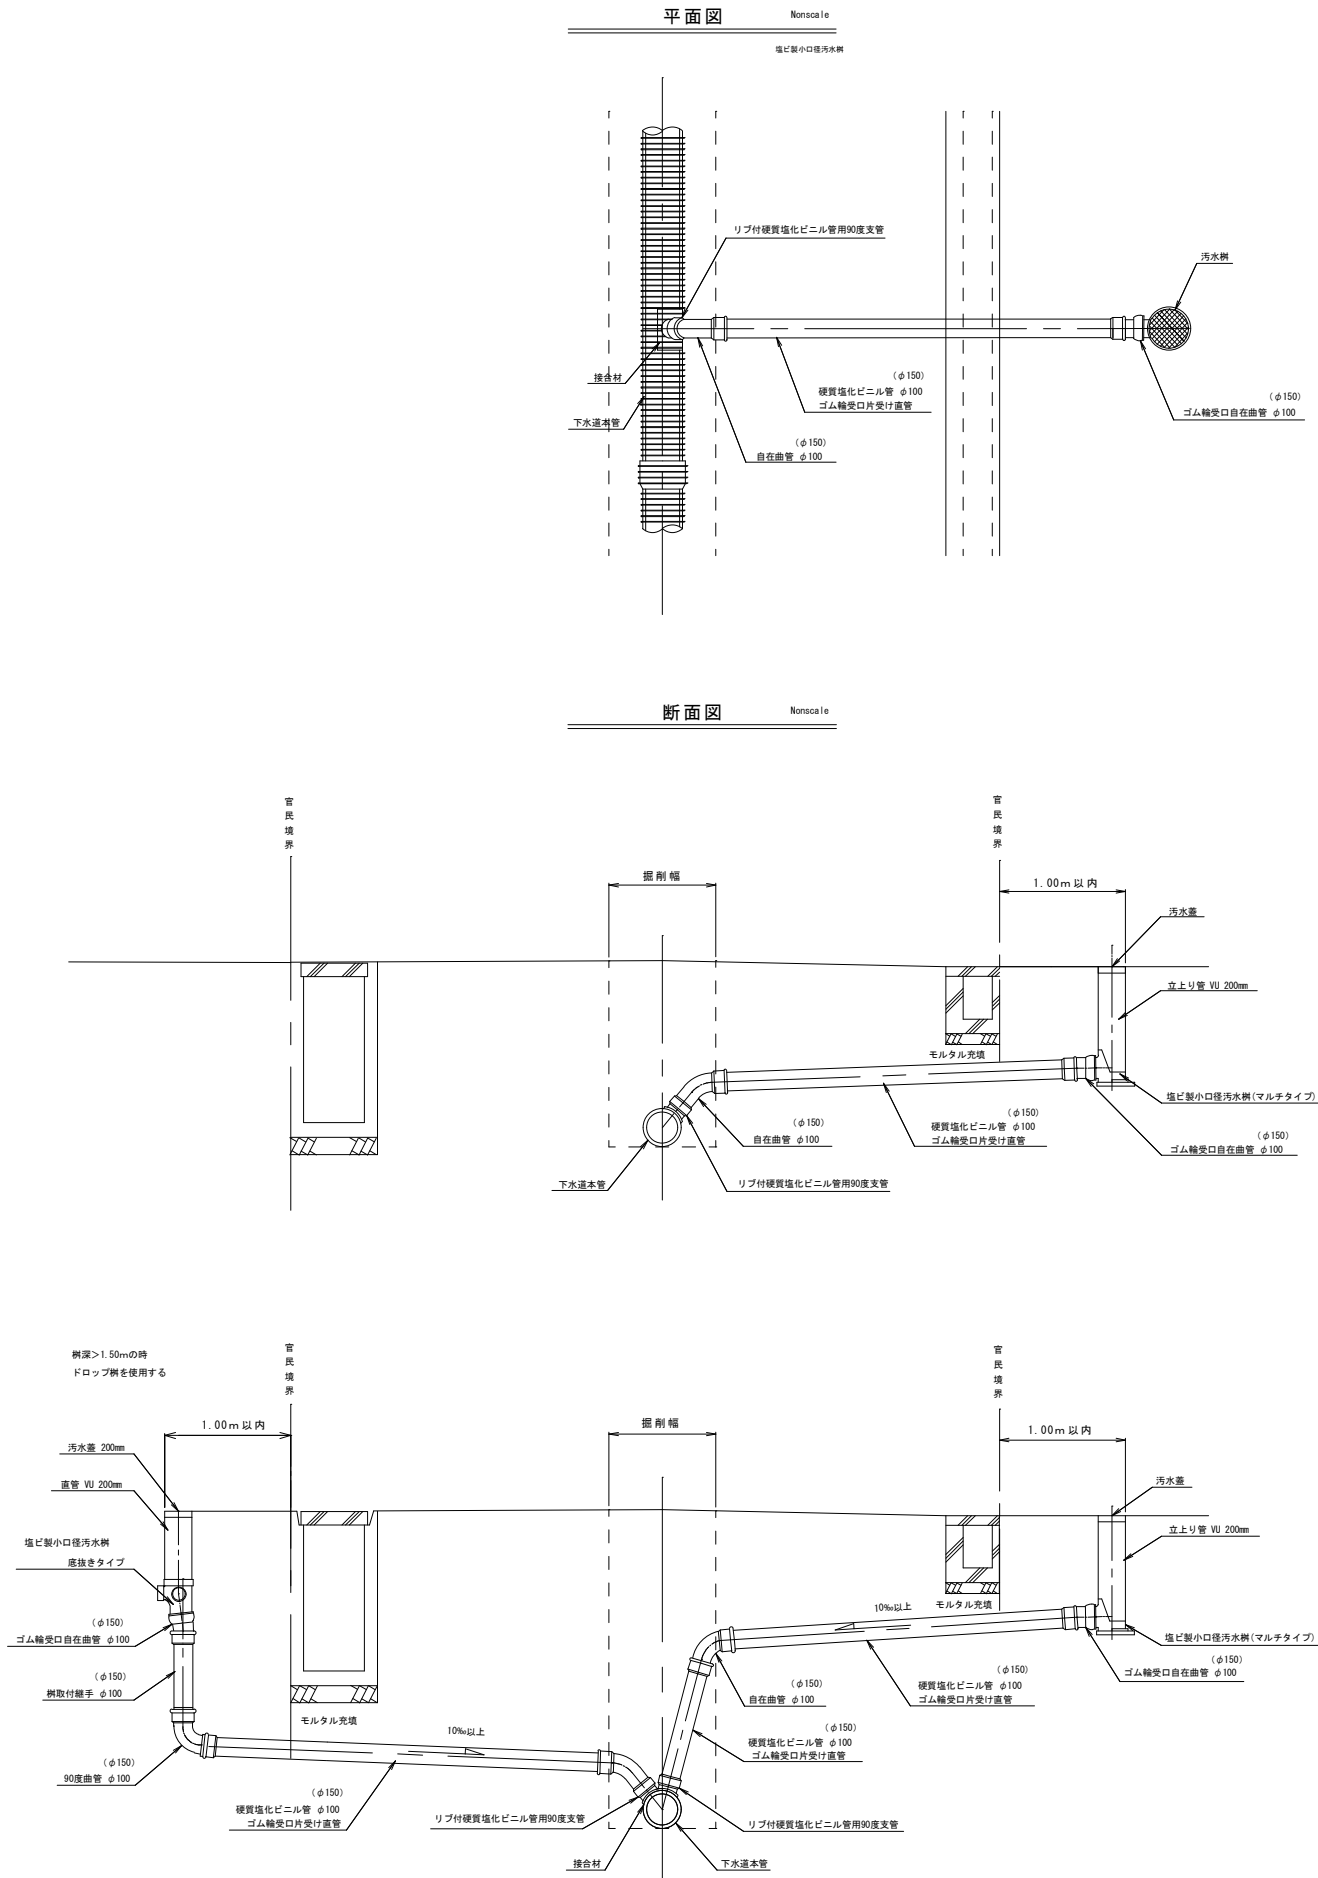


- 特記事項
- 支管は下水道本管の材質によって、使い分けること。
 - 汚水樹は各家屋並びに、地下水・側溝の状況に応じて使い分けること。
 - 消雪パイプ・側溝等の下で転圧が充分に出来ないところは、モルタル等を注入し不平等沈下しないようにすること。

平成27年度 魚津市特定環境保全公共下水道事業					
工 事 名					
工 事 場 所		地 内		縮 尺	図 示
図 面 名		取付管布設標準図			
課 長	係 長	設 計	製 図	図 面 番 号	
				No. ④	
魚津市上下水道局下水道課					


建込簡易土留工

断面図


掘削深 3.00m以下

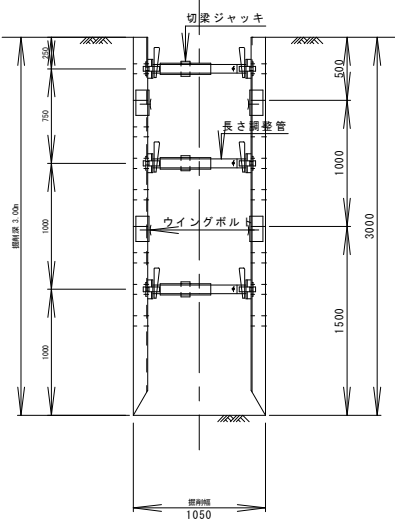


掘削深 3.50m以下

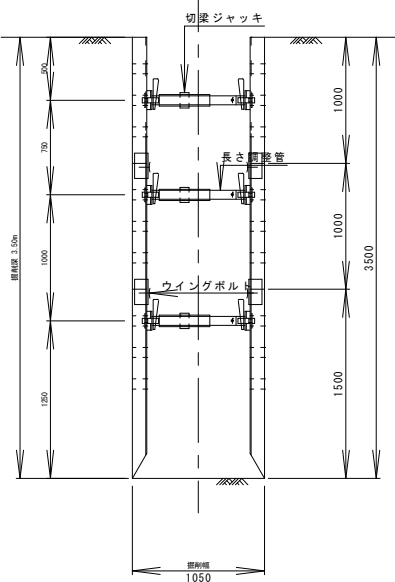

掘削深 4.00m以下

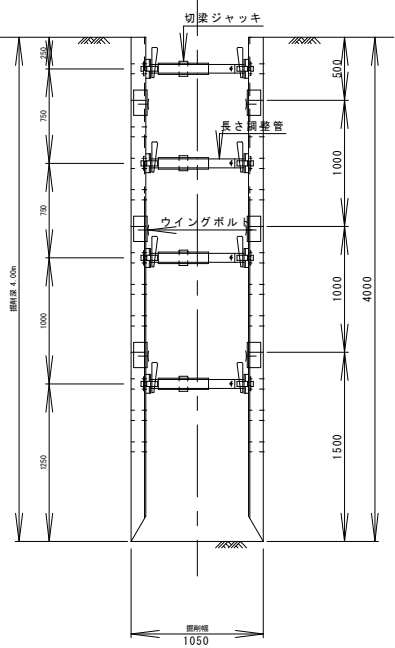


平面図

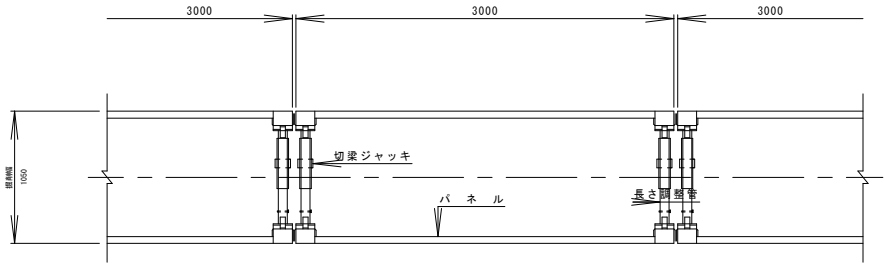


軽量鋼矢板土留工

断面図


掘削深 2.80m以下

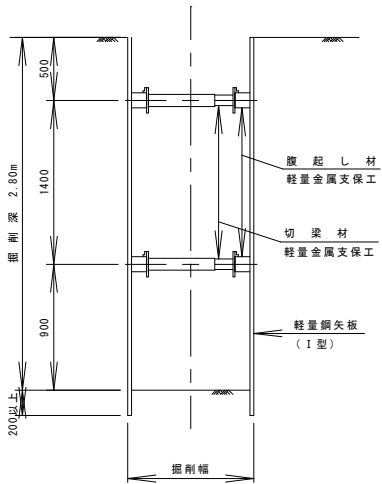

掘削深 3.80m以下

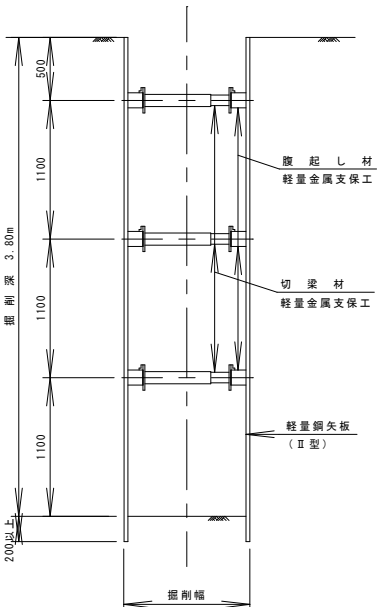


平面図

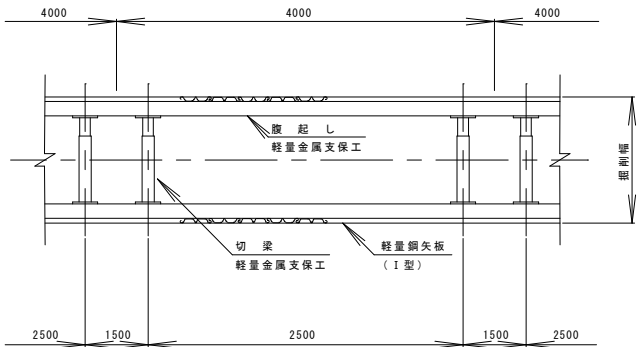

軽量鋼矢板設置基準

掘削深	支保工段数	腹起し	切梁	矢板
1.80m以上 2.30m未満	2 段	軽量金属 支保工	軽量金属 支保工	軽量鋼矢板 I 型
2.30m以上 2.80m未満				
2.80m以上 3.30m未満	3 段	軽量金属 支保工	軽量金属 支保工	軽量鋼矢板 II 型
3.30m以上 3.80m未満				

軽量鋼矢板標準図（参考図）

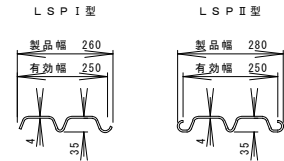

型 式	重 量	
	矢板1枚当り (kg/m)	壁幅1枚当り (kg/m ²)
LSP I型	10.4	41.6
LSP II型	11.8	47.2


※注 使用する軽量鋼矢板は、土質により異なる。

平成27年度 魚津市特定環境保全公共下水道事業				
工 事 名	(管路 _____)			
工事場所	地 内	縮 尺	図 示	
図 面 名	土留工標準図			
課 長	係 長	設 計	製 図	図 面 番 号
				N o . ⑤
魚津市上下水道局下水道課				


舗装復旧標準図

S = 1 : 2 0


県 道（A 交通）

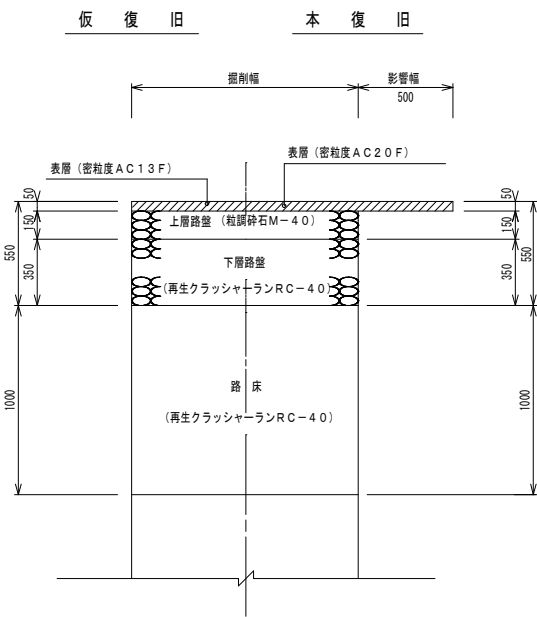


県 道（B 交通）

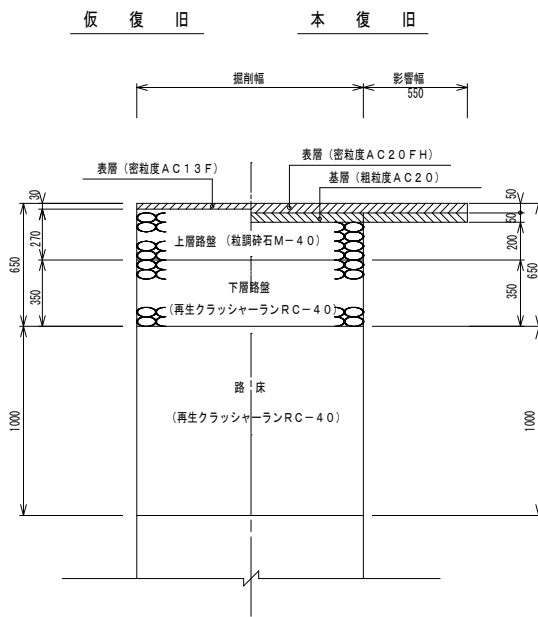


県 道（C 交通）

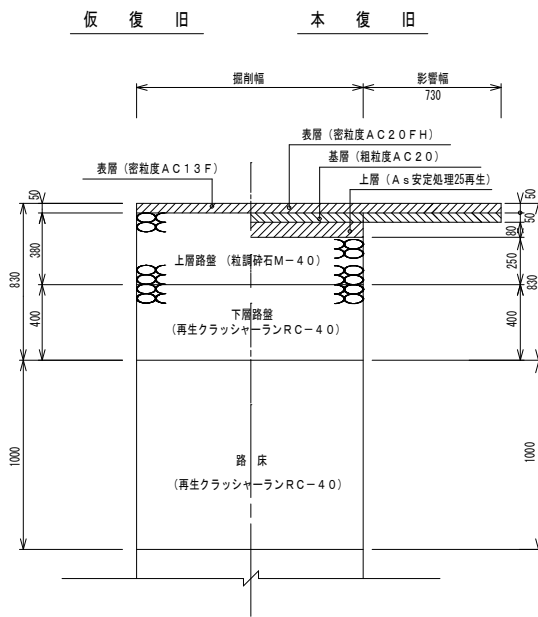


県 道（D 交通）

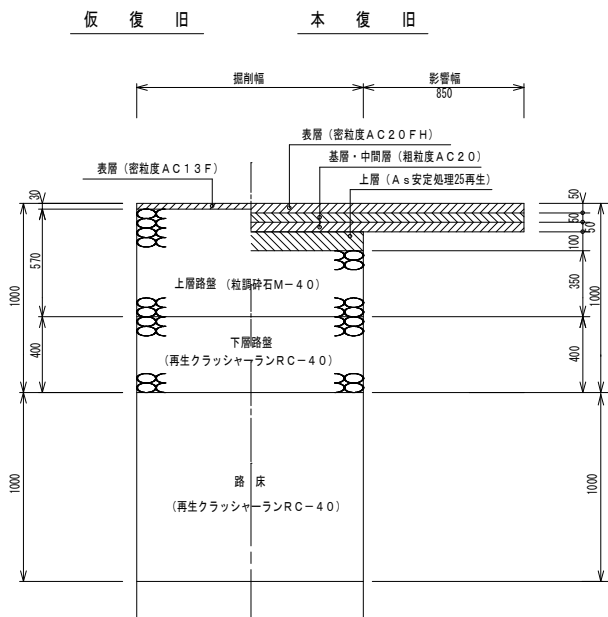


市 道

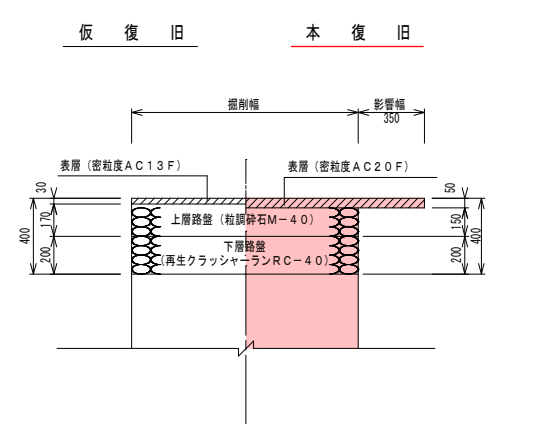


歩 道

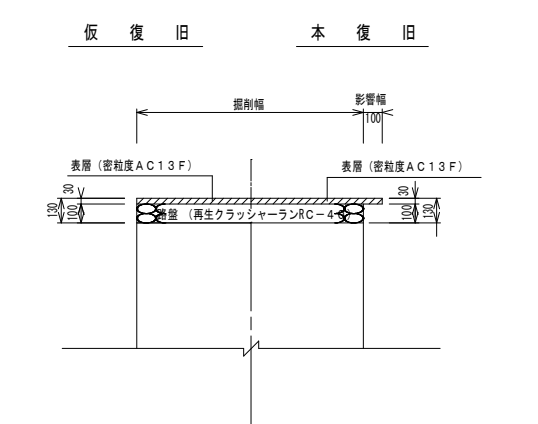


歩道（自動車乗入口）

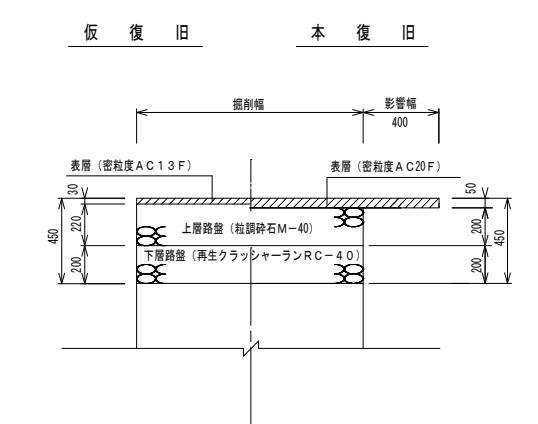


砂 利 道

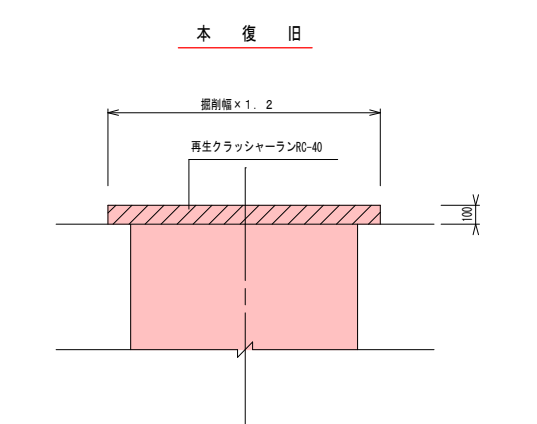

コンクリート舗装

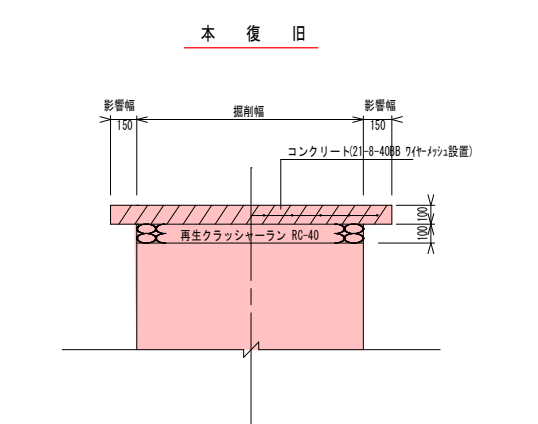

農 道・私 道・駐車場

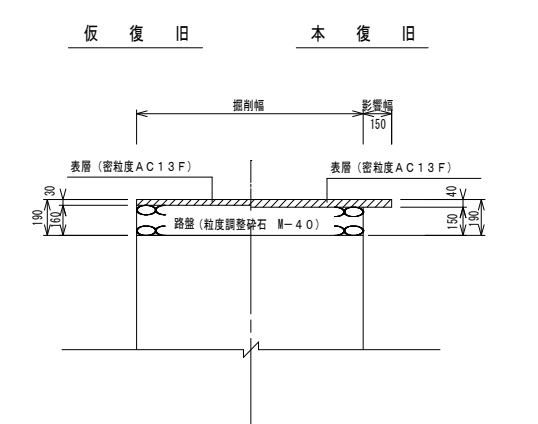

平成 2 7 年 度 魚津市特定環境保全公共下水道事業				
工 事 名				
工事場所		地 内	縮 尺	S=1/20
図 面 名		舗装復旧標準図		
課 長	係 長	設 計	製 図	図 面 番 号
				No ⑥
魚津市上下水道局下水道課				