

位置図


S=1:5000

平面図(1) A1図面 S=1:300
A3図面 S=1:600

福岡市
下水道局
設計番号
図面番号
1/21
工事名
福岡市
地区下水道
計画図(1)
地区下水道
計画図(1)
地区下水道
計画図(1)

(福岡市)

538
2
538
3
539
1
539
2
541
1
541
2

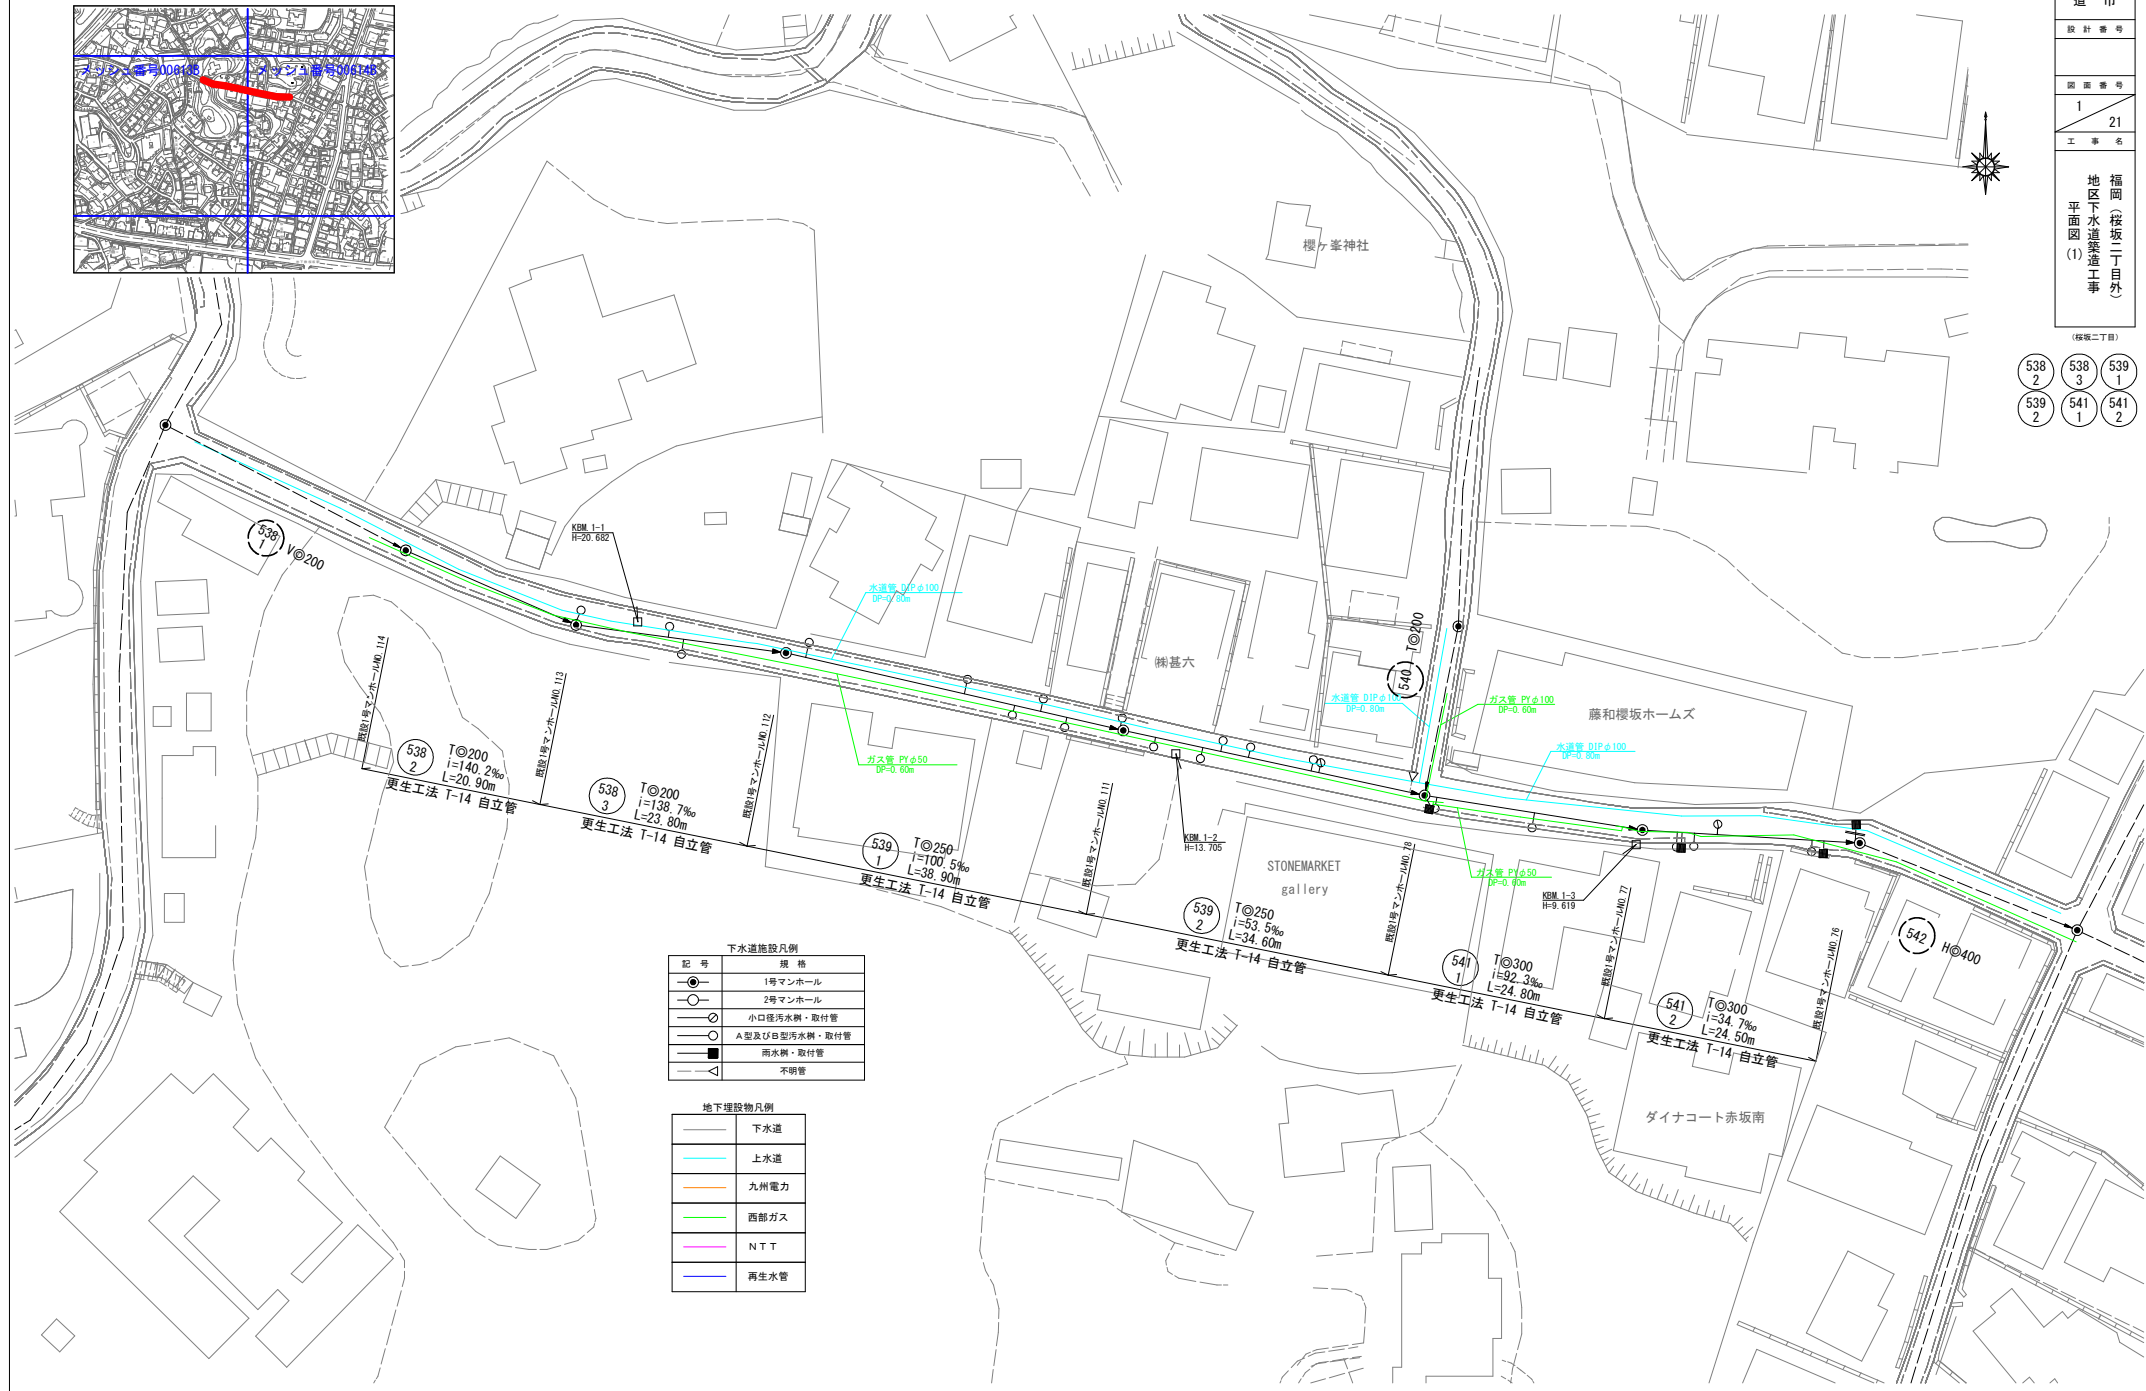

下水道施設凡例	
●	1号マンホール
○	2号マンホール
○	小口径汚水管・取付管
○	A型及びB型汚水管・取付管
■	雨水管・取付管
—	不明管


地下埋設物凡例	
—	下水道
—	上水道
—	九州電力
—	西部ガス
—	N T T
—	再生水管

平 面 図 (2) A1図面 S=1:300
A3図面 S=1:600

A3圖面 S=1:600


位置図

S=1 : 5000

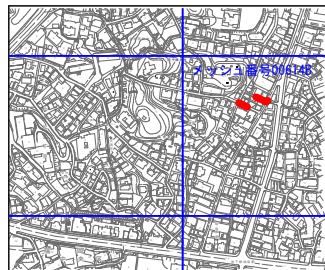


下水道施設凡例	
記 号	規 格
	1号マンホール
	2号マンホール
	小口径汚水樹・取付管
	A型及びB型汚水樹・取付管
	雨水樹・取付管
	不明管

	下水道
	上水道
	九州電力
	西部ガス
	N T T
	再生水管

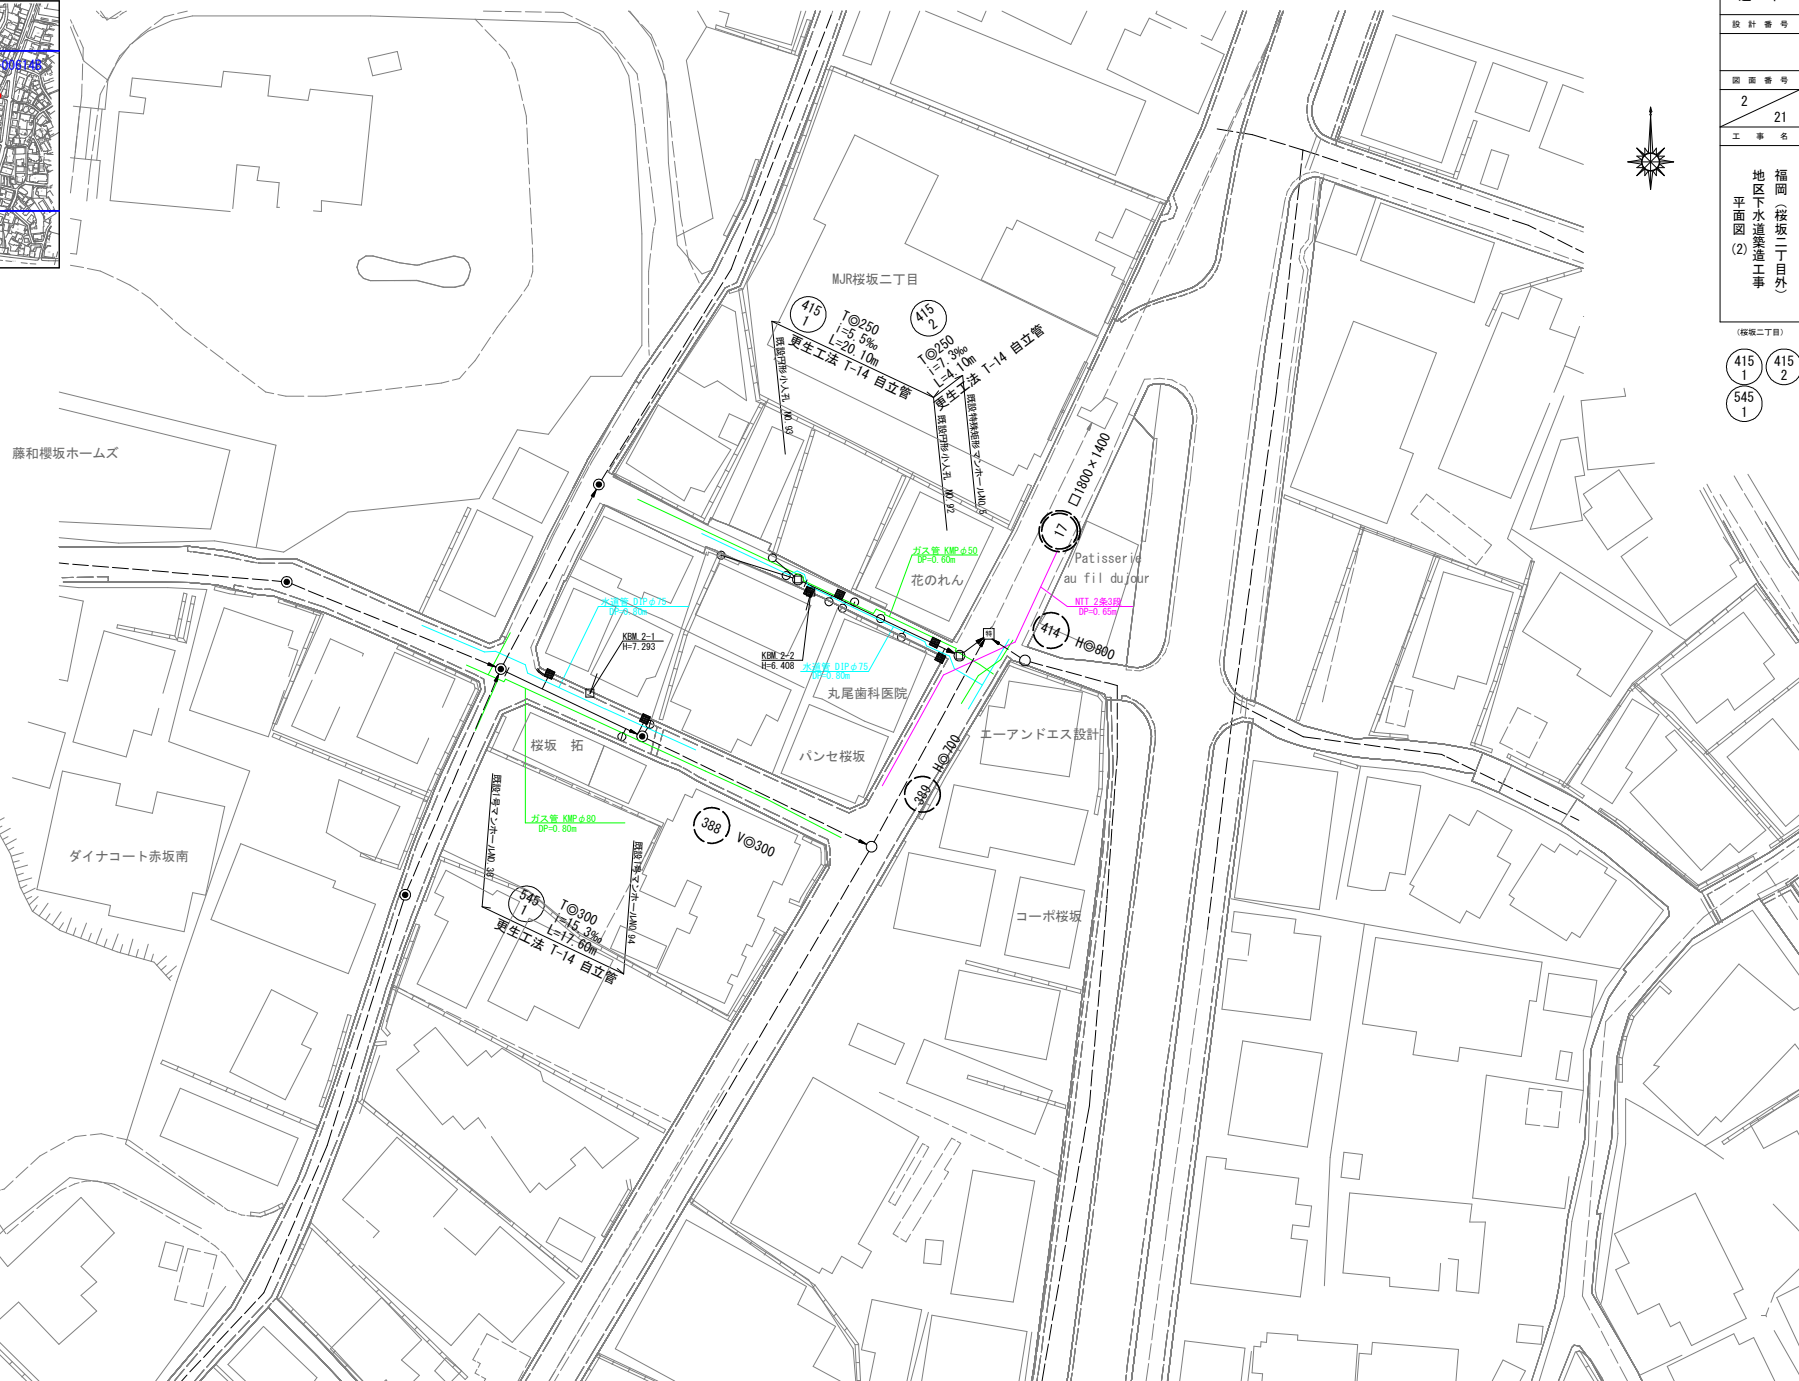

位置図 S=1:5000

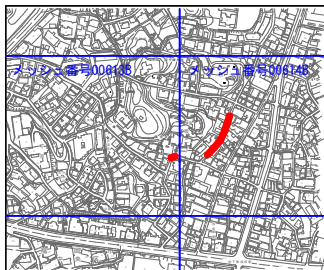

平面図(3) A1図面 S=1:300
A3図面 S=1:600

福岡
下水道
市
設計番号
図面番号
3
21
工事名
福岡(桜坂二丁目)
地区下水道築造工事
平面図(3)

(桜坂二丁目)

375
2
543
1
543
2
544
1
544
2
544
3

下水道施設凡例	
記号	規格
●	1号マンホール
○	2号マンホール
○	小口径汚水側・取付管
○	A型及びB型汚水側・取付管
■	雨水側・取付管
△	不明管

地下埋設物凡例	
—	下水道
—	上水道
—	九州電力
—	西部ガス
—	N T T
—	再生水管



位置図 S=1:5000



平面図 (6) A1図面 S=1:300
A3図面 S=1:600


福岡市
下水道部
設計番号
図面番号
6
21
工事名
福岡市 桜坂二丁目外
地区下水道築造工事
平面図 (6)

(桜坂一丁目)

430
2
441
1

下水道施設凡例	
記号	規格
●	1号マンホール
○	2号マンホール
○	小口径汚水管・取付管
○	A型及びB型汚水管・取付管
■	雨水管・取付管
△	不明管

地下埋設物凡例	
—	下水道
—	上水道
—	九州電力
—	西部ガス
—	N T T
—	再生水管

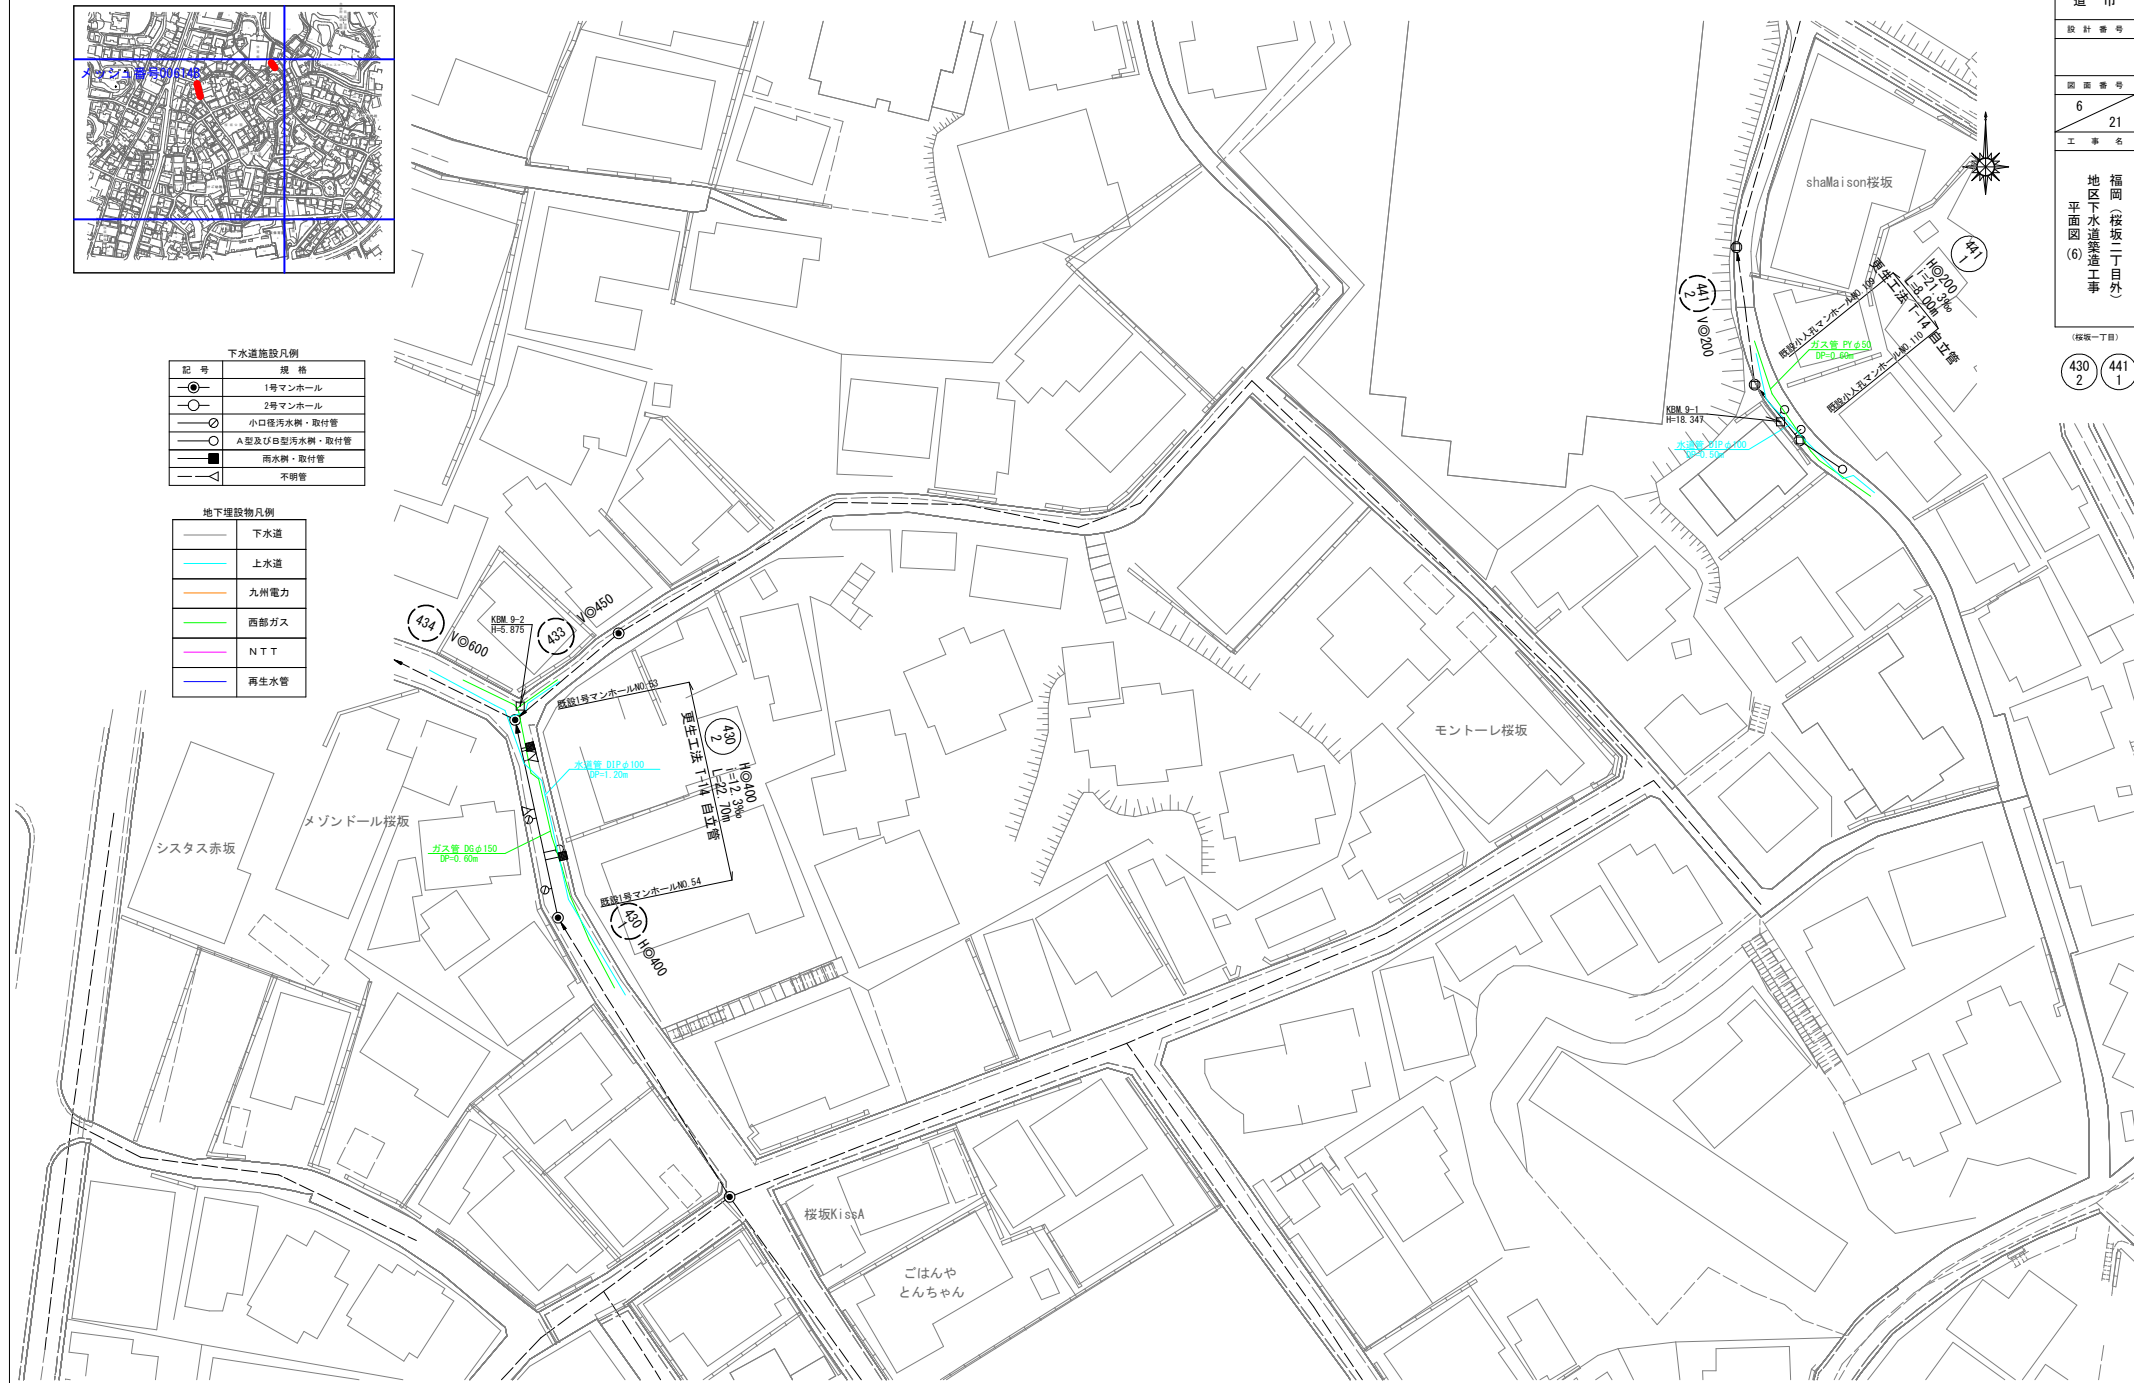

位置図

S=1:5000



平面図(7)

A1図面 S=1:300

A3図面 S=1:600

下水道施設凡例	
記号	規格
●	1号マンホール
○	2号マンホール
○	小口径汚水側・取付管
○	A型及びB型汚水側・取付管
■	雨水側・取付管
△	不明管

地下埋設物凡例	
—	下水道
—	上水道
—	九州電力
—	西部ガス
—	N T T
—	再生水管



福岡
下水道
市

設計番号

図面番号


7 21

工事名


福岡
地区下水道
平面図(7)

(掲載一丁目)

426
3

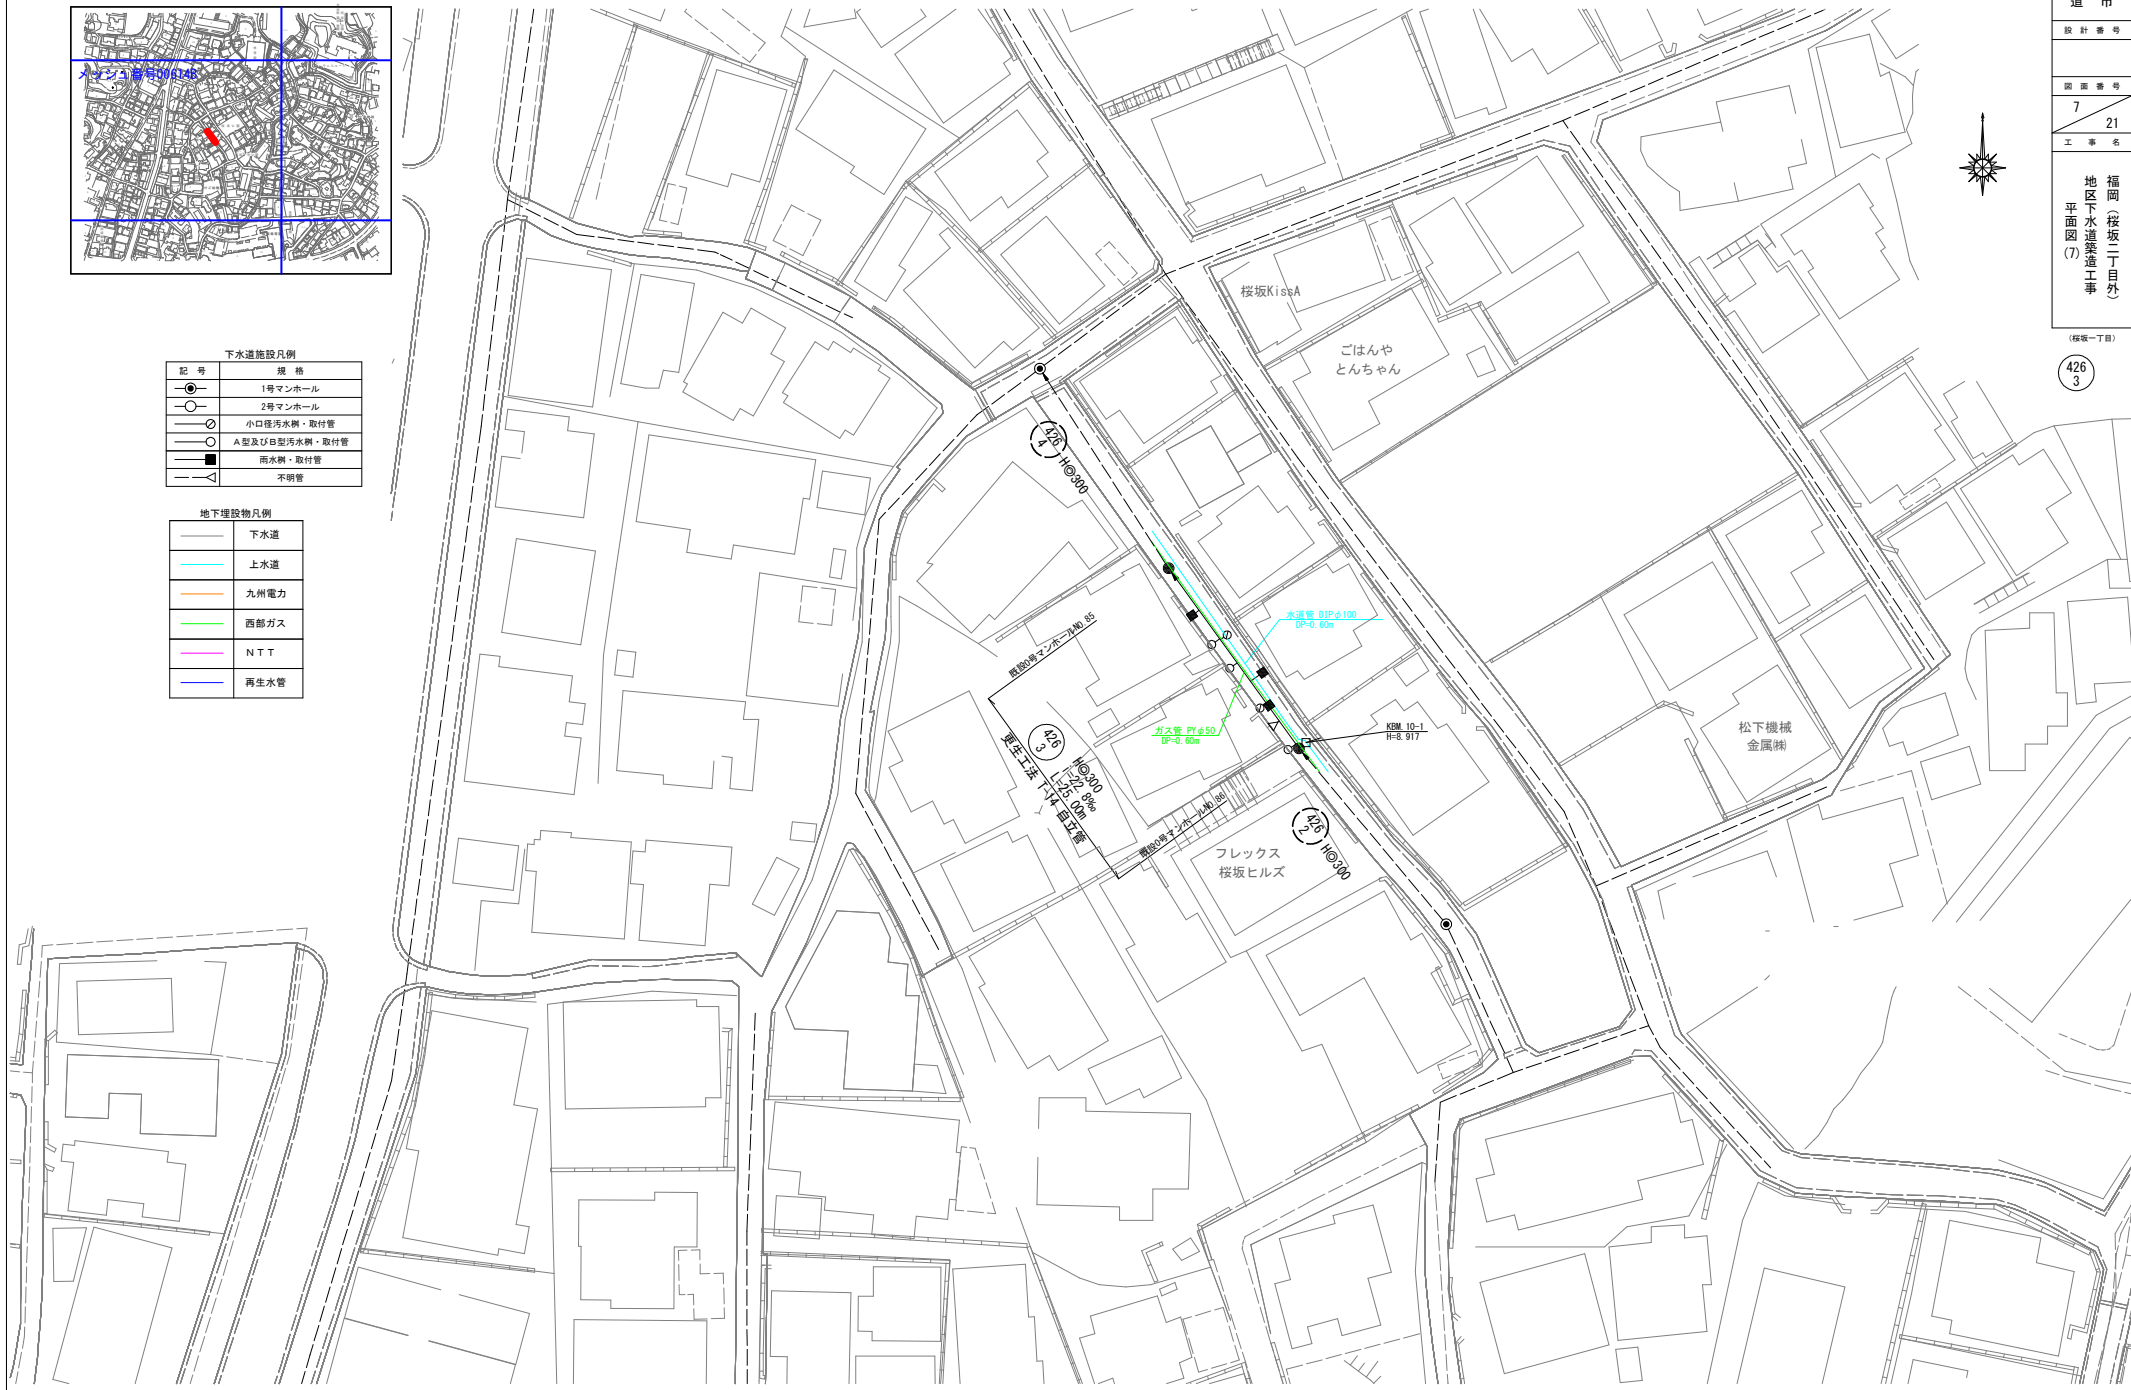


縦断図(1) 縮尺 縦 1:100 横 1:300

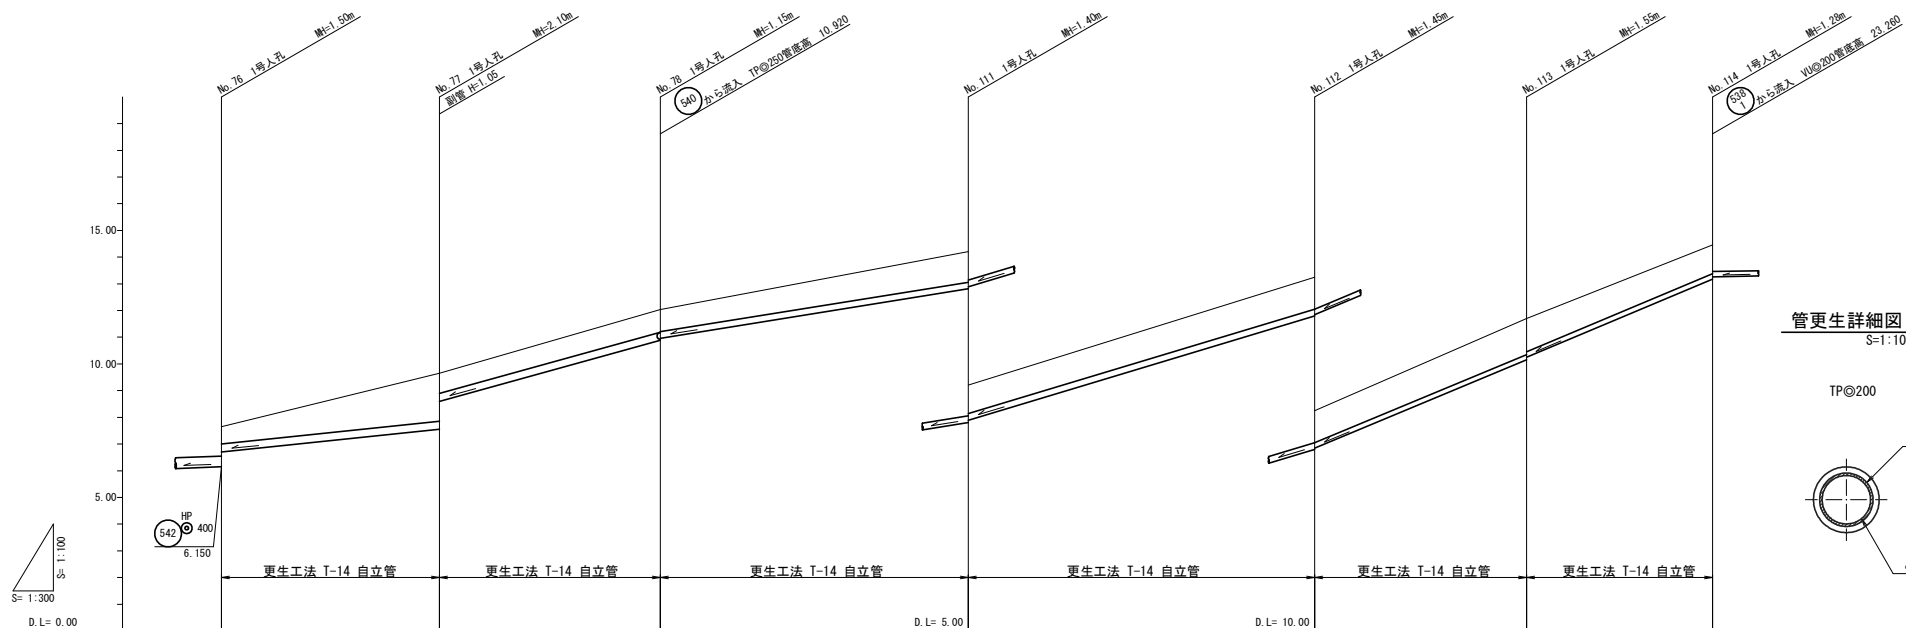


管更生詳細図
S=1:10


TP@200

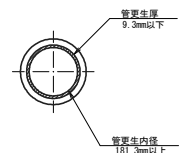

TP@250

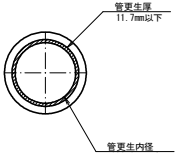

TP@300

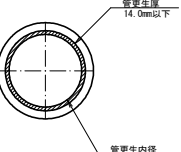

路線番号		542	541	539	538	537	
断面		TP 300	TP 300	TP 250	TP 250	TP 200	TP 200
勾配		34.7‰	92.3‰	53.5‰	100.5‰	138.7‰	140.2‰
延長		24.50	24.80	34.60	38.90	23.80	20.90
地盤高		7.65	9.65	12.04	14.21	18.25	21.70
土被り		0.62	1.77 0.72	0.62 0.80	1.12 1.04	1.17 1.16	1.33 1.23
管底高		6.70	7.55 8.60	10.89 10.80	12.81 12.80	16.80 16.80	20.15 20.20
掘削深							
追加距離		0.00	24.50	49.30	83.90	122.80	146.60
管種		T (1967年)	T (1967年)	T (1967年)	T (1967年)	T (1967年)	T (1967年)
基礎種別							
道路種別		車道アスファルト舗装 (A)	車道アスファルト舗装 (A)	車道アスファルト舗装 (A)	車道アスファルト舗装 (A)	車道アスファルト舗装 (A)	車道アスファルト舗装 (A)
埋戻し工							
土留工							
支保工							
路面覆工							

福岡市
下水道部

設計番号

図面番号

8 21

工事名

福岡(桜坂二丁目)
地区下水道築造工事
縦断図(1)

(縦断二丁目)

541
2 1
539
2 1

管更生厚
9.3mm以下

管更生内径
181.3mm以上


管更生厚
11.7mm以下

管更生内径
226.6mm以上


管更生厚
14.0mm以下

管更生内径
271.0mm以上

縦断図(2) 縮尺 縦尺 1:100 横尺 1:300

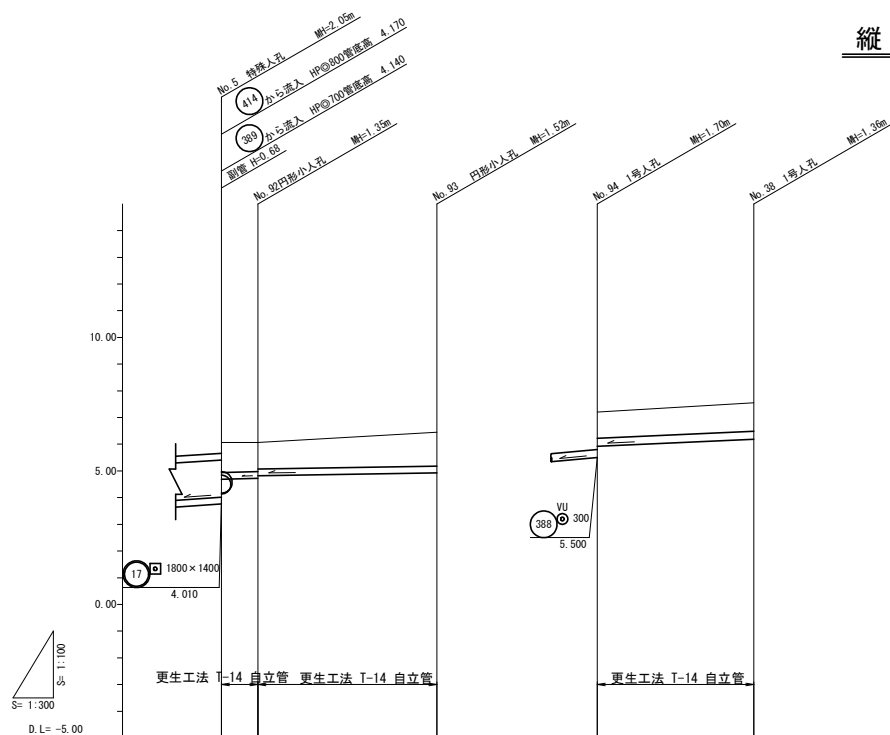


管更生詳細図
S=1:10

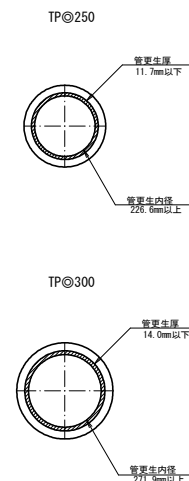


路線番号	415 2	415 1	545 1
断面	TP 250	TP 250	TP 300
勾配	7.3‰	5.5‰	15.3‰
延長	4.10	20.10	17.60
地盤高	6.06 6.07	6.45	7.20 7.55
土被り	1.09 1.07 0.97	1.24	0.95 1.03
管底高	4.90 4.72 4.60	4.90	5.90 6.10
掘削深			
追加距離	0.00 4.10	24.20	0.00 17.60
管種	T (1966年)	T (1966年)	T (1957年)
基礎種別			
道路種別	車道アスファルト舗装 (B)	車道アスファルト舗装 (A)	車道アスファルト舗装 (A)
埋戻し工			
土留工			
支保工			
路面覆工			

縦断図(3) 縮尺 縦 1:100 横 1:300

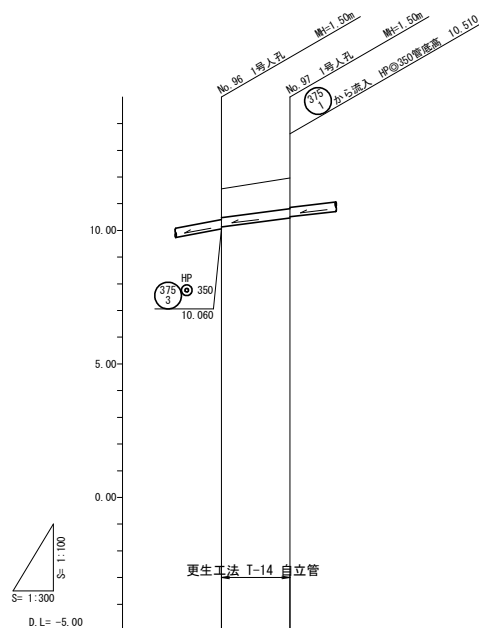


路線番号									
断面	HP ◎ 350								
勾配	42.9‰								
延長	7.70								
地盤高	11.56 11.56	6.94	7.27 7.23	7.70	8.34	8.94	9.06		
土被り	1.05 1.12	0.92	0.97 0.92	1.22 0.87	1.27 0.77	1.07 1.12	1.02		
管底高	10.130 10.460	5.690	5.670 6.040	6.240 6.590	6.740 7.260	7.590 7.540	7.760		
掘削深									
追加距離	0.00 7.70	0.00	27.40	56.70	74.70	93.60	112.40		
管種	T (1965年)	T (1957年)	T (1957年)	T (1957年)	T (1957年)	T (1957年)	T (1957年)		
基礎種別									
道路種別	車道アスファルト舗装 (A)	車道アスファルト舗装 (A)	車道アスファルト舗装 (A)	車道アスファルト舗装 (A)	車道アスファルト舗装 (A)	車道アスファルト舗装 (A)	車道アスファルト舗装 (A)		
埋戻し工									
土留工									
支保工									
路面覆工									


管更生詳細図
S=1:10

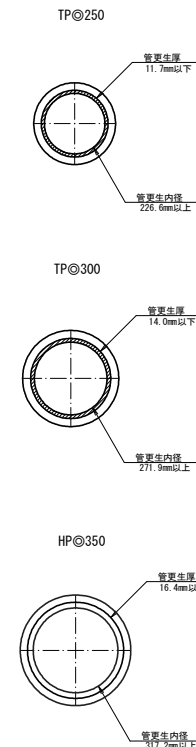

縦断図(4) 縮尺 縦尺 1:100 横尺 1:300

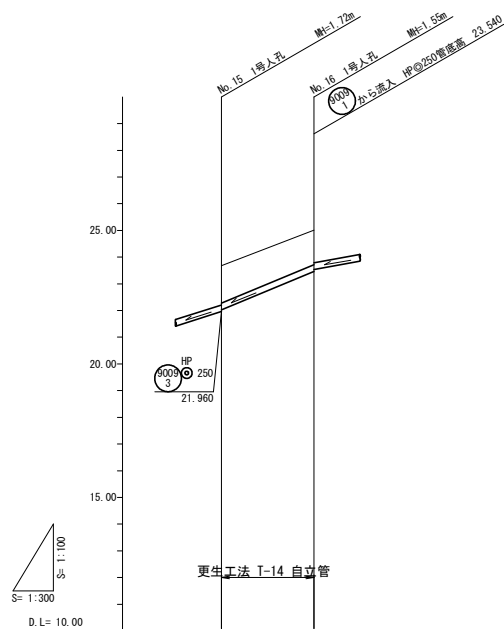


管更生詳細図
S=1:10

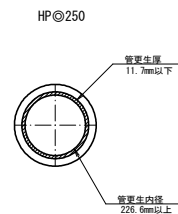


路線番号		②	
断面		HP ② 250	
勾配		137.5‰	
延長		10.40	
地盤高	23.08	25.01	
土被り	1.37	1.27	
管底高	22.00	23.60	
掘削深			
追加距離	0.00	10.40	
管種		H (1971年)	
基礎種別			
道路種別		車道アスファルト舗装 (A)	
埋戻し工			
土留工			
支保工			
路面覆工			

縦断図(5) 縮尺 縦 1:100 横 1:300

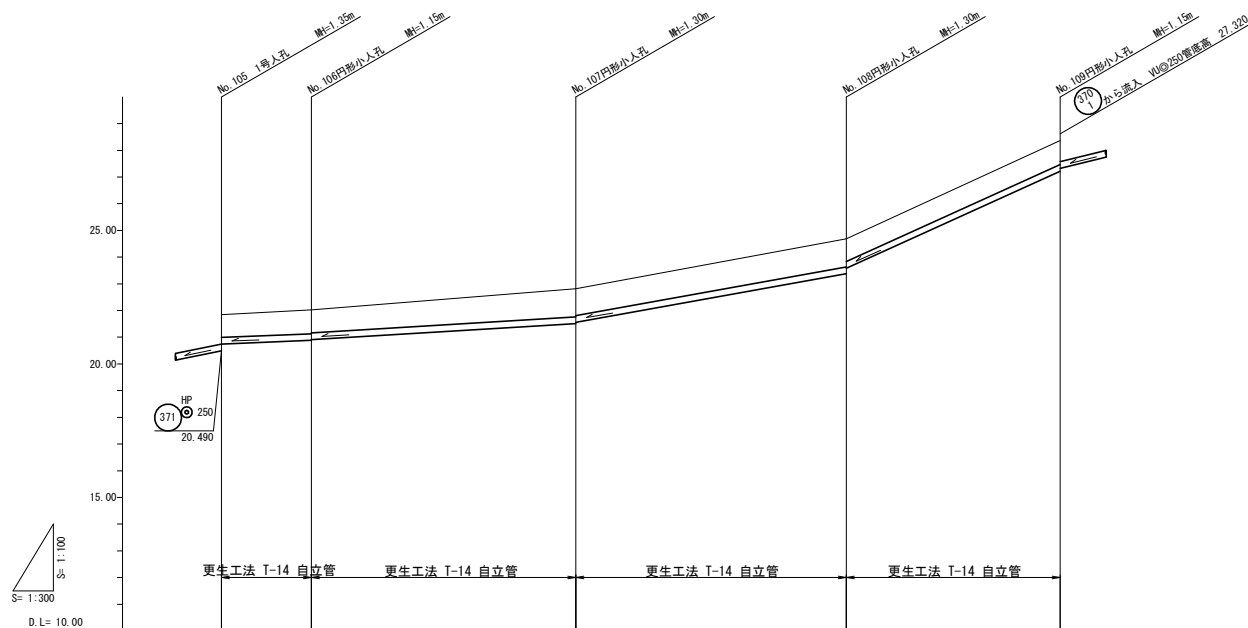



管更生詳細図 S=1:10

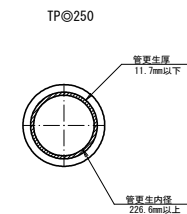

路線番号		370	370	370	370
断面		TP 250	TP 250	TP 250	TP 250
勾配		13.9‰	20.2‰	59.9‰	151.7‰
延長		10.10	29.70	30.40	24.00
地盤高		21.84 22.03	22.81	24.88	28.37
土被り		0.82 0.87 0.84	1.02 0.97	1.02 0.82	0.87
管底高		20.740 20.880 20.910	21.510 21.560	23.380 23.390	27.220
掘削深					
追加距離		0.00 10.10	39.80	70.20	94.20
管種		T (1971年)	T (1971年)	T (1971年)	T (1971年)
基礎種別					
道路種別		車道アスファルト舗装 (A)	車道アスファルト舗装 (A)	車道アスファルト舗装 (A)	車道アスファルト舗装 (A)
埋戻し工					
土留工					
支保工					
路面覆工					

縦断図(6) 縮尺 縦 1:100 横 1:300


管更生詳細図
S=1:10

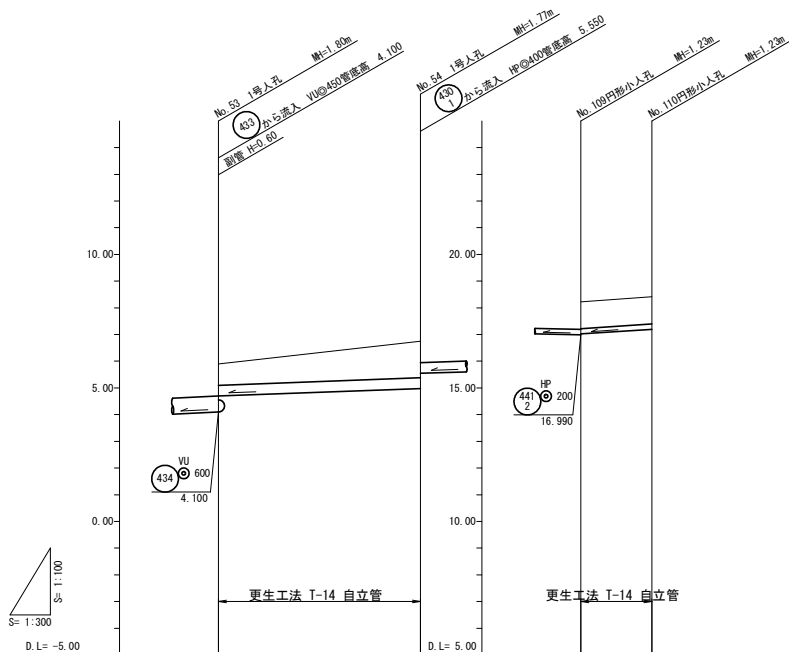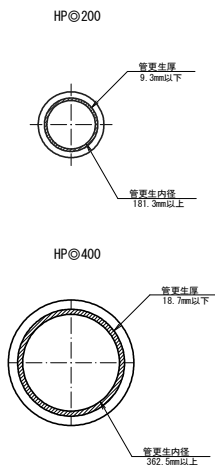


路線番号		430		441	
断面		HP 400		HP 200	
勾配		12.3‰		21.3‰	
延長		22.70		8.00	
地盤高		5.90	6.75	18.22	18.42
土被り		0.77	1.34	0.97	1.00
管底高		4.70	4.80	17.00	17.90
掘削深					
追加距離		0.00	22.70	0.00	8.00

管種		H (1957年)		H (1966年)	
基礎種別					
道路種別		車道アスファルト舗装 (A)		車道アスファルト舗装 (A)	
埋戻し工					
土留工					
支保工					
路面覆工					

縦断図(7) 縮尺 縦 1:100 横 1:300

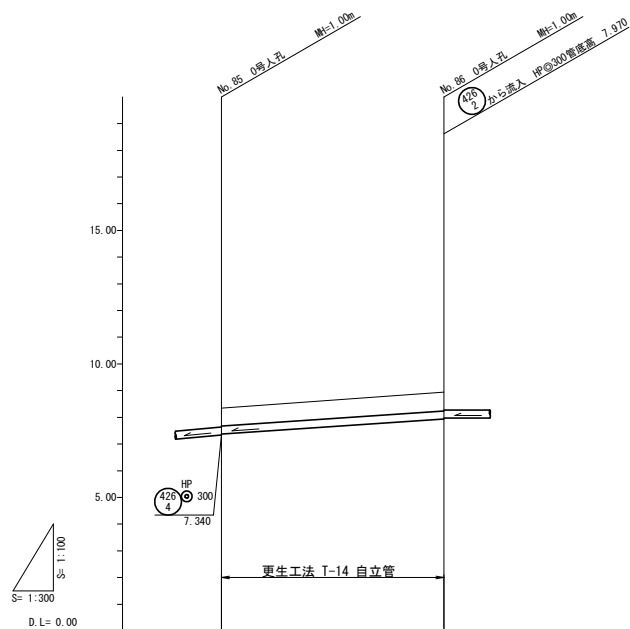

管更生詳細図
S=1:10

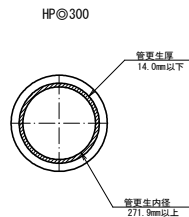

路線番号		05	
断面		HP	
勾配		300	
延長		22.8%	
		25.00	
地盤高	8.34		8.94
土被り	0.64		0.67
管底高	7.370		7.940
掘削深			
追加距離	0.00		25.00
管種		H	
		(1957年)	
基礎種別			
道路種別		車道アスファルト舗装 (A)	
埋戻し工			
土留工			
支保工			
路面覆工			

人孔修繕一覧表

路線番号	人孔番号	蓋・口環	足掛金物	安全梯子	インバート
538-2	No. 114	—	—	1	—
538-3	No. 113	—	2	1	—
539-1	No. 112	—	2	1	—
539-2	No. 111	—	2	—	—
541-1	No. 78	1	2	1	—
541-2	No. 77	1	4	1	—
	No. 76	1	3	1	—

付帯工平面図 (1) A1図面 S=1:300
A3図面 S=1:600

下 福
水 岡
岡 道
道 市
市

設 計 番 号

図 面 番 号

15 21

工 事 名

福岡 桜坂二丁目外
地区下水道築造工事
付帯工平面図 (1)

(桜坂二丁目)

538
2


538
3

539
1

539
2

541
1

541
2

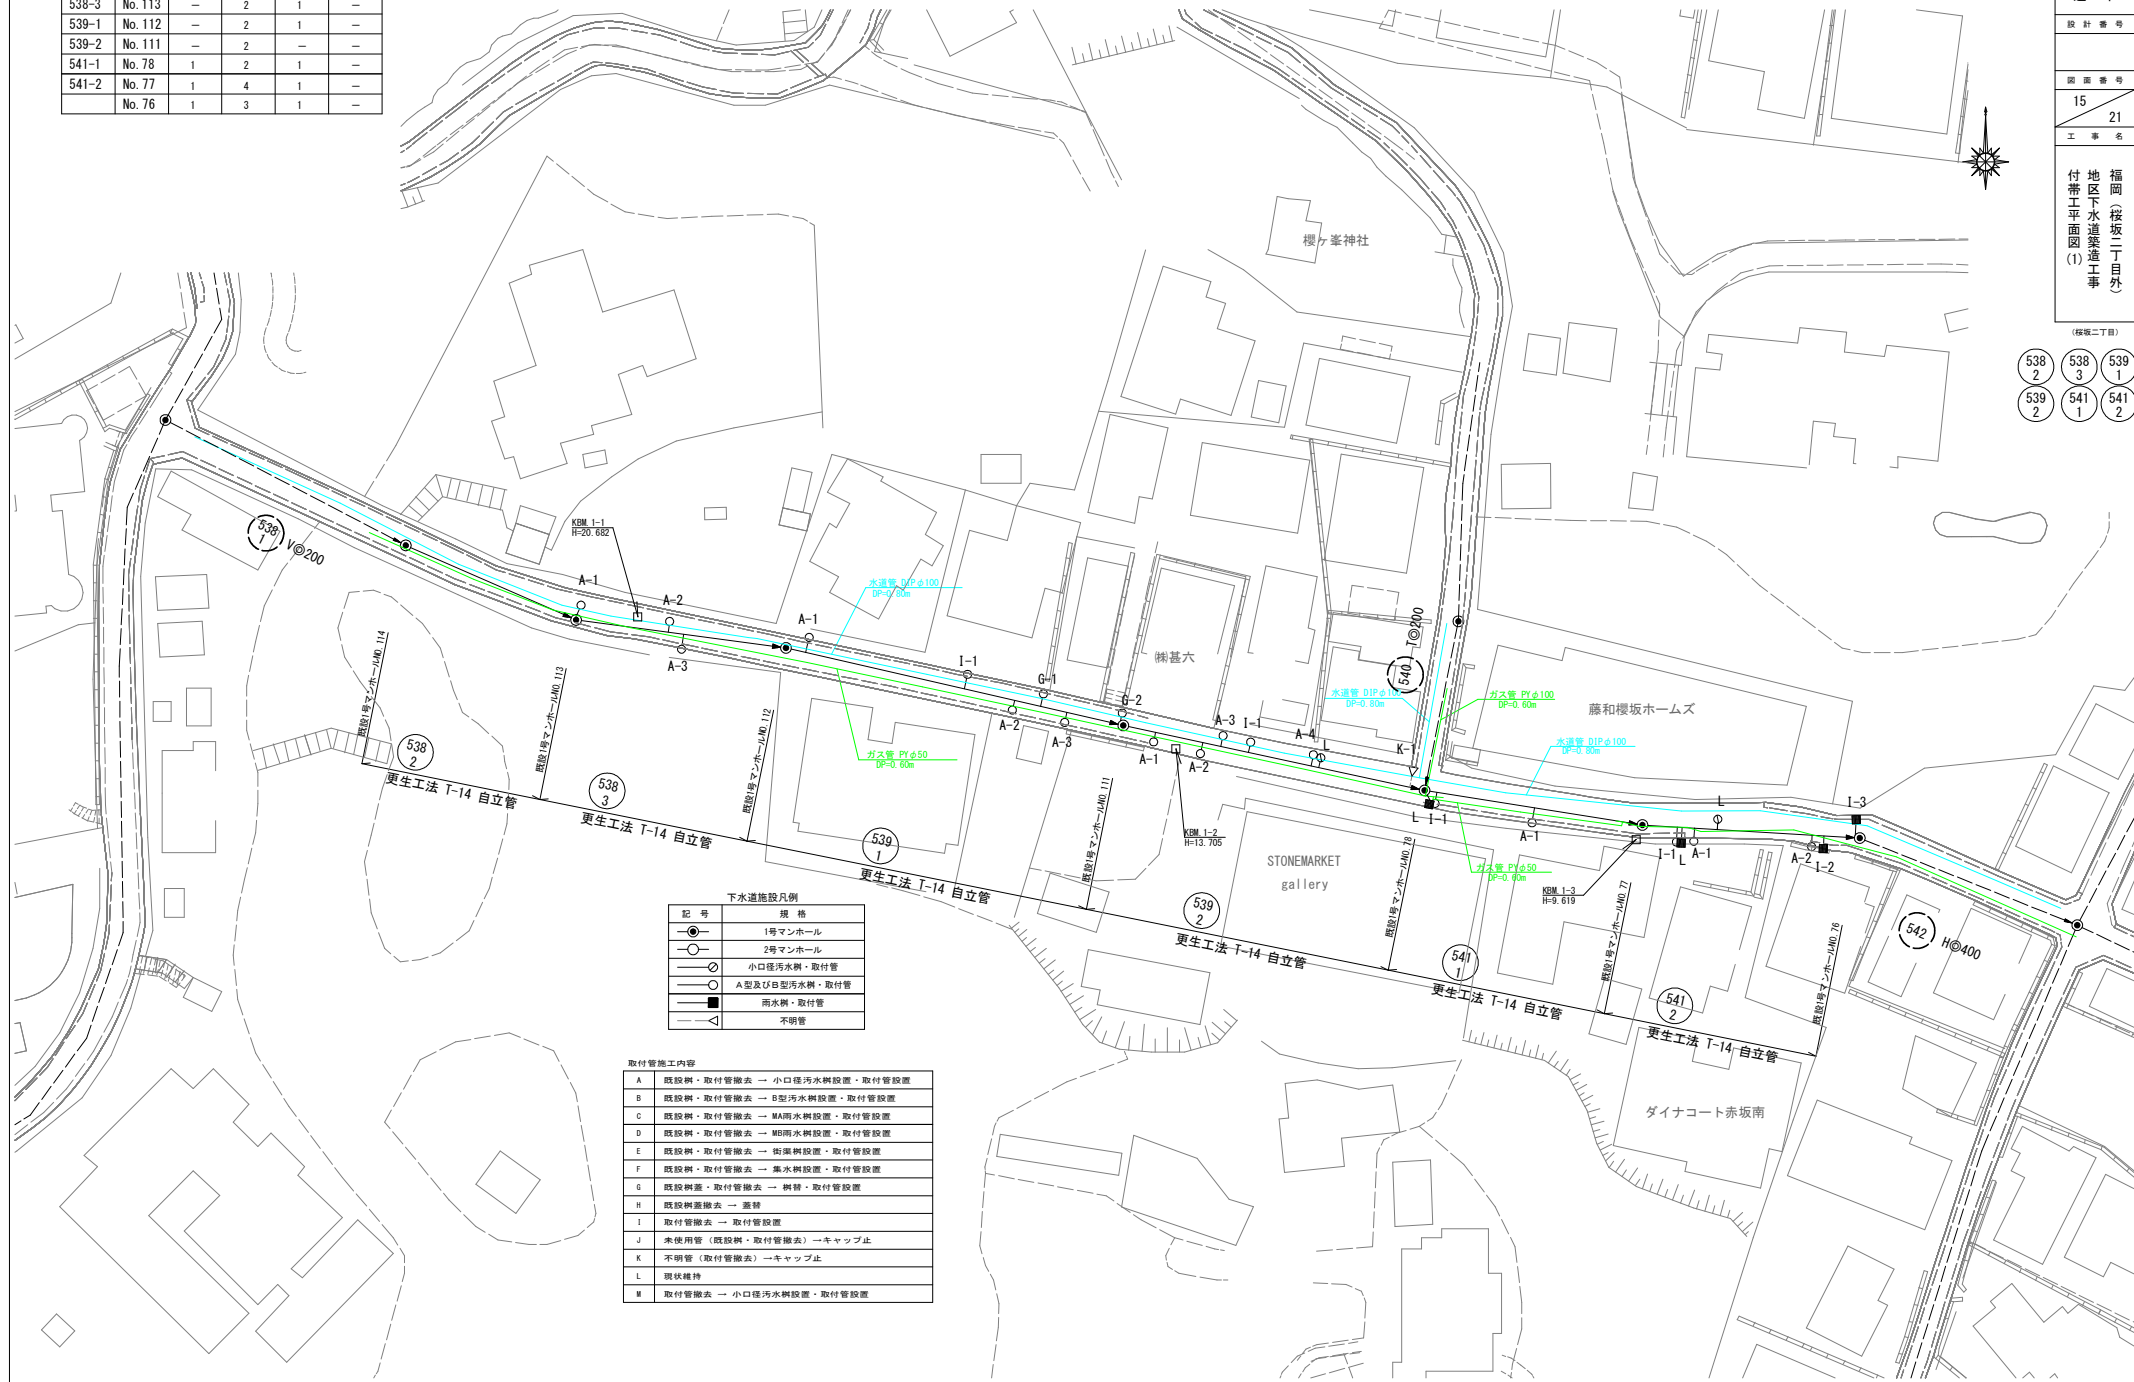

人孔修繕一覧表

路線番号	人孔番号	蓋・口環	足掛金物	安全梯子	インハート
415-1	No. 93	—	—	—	1
415-2	No. 92	—	—	—	—
	No. 5	1	—	1	—
545-1	No. 38	1	2	1	1
	No. 94	—	—	—	—

付帯工平面図 (2) A1図面 S=1:300
A3図面 S=1:600

下 福
水 岡
道 市
設計番号
図面番号
16 / 21
工事名
福岡(桜坂二丁目)
地区下水道築造工事
付帯工平面図(2)

(桜坂二丁目)

415
1
415
2
545
1

下水道施設凡例

記号	規格
●	1号マンホール
○	2号マンホール
○	小口径汚水樹・取付管
○	A型及びB型汚水樹・取付管
■	雨水樹・取付管
△	不明管

取付管施工内容

A	既設樹・取付管撤去 → 小口径汚水樹設置・取付管設置
B	既設樹・取付管撤去 → B型汚水樹設置・取付管設置
C	既設樹・取付管撤去 → MA雨水樹設置・取付管設置
D	既設樹・取付管撤去 → 細雨水樹設置・取付管設置
E	既設樹・取付管撤去 → 街渠樹設置・取付管設置
F	既設樹・取付管撤去 → 集水樹設置・取付管設置
G	既設樹撤去 → 樹撤去・取付管設置
H	既設樹撤去 → 蓋撤去
I	取付管撤去 → 取付管設置
J	未使用管(既設樹・取付管撤去) → キャップ止
K	不明管(取付管撤去) → キャップ止
L	現状維持
M	取付管撤去 → 小口径汚水樹設置・取付管設置

藤和桜坂ホームズ

ダイナコート赤坂南

MJR桜坂二丁目

更生工法 T-14 自立管

更生工法 T-14 自立管

口 1800×1400

Patisserie au fil du jour

丸尾歯科医院

パンセ桜坂

エーアンドエス設計

コーポ桜坂

桜坂 拓

ガス管 Kφ280

D=0.50m

ガス管 Kφ280

D=0.50m

人孔修繕一覧表

路線番号	人孔番号	蓋・口環	足掛金物	安全梯子	インバート
375-2	No. 97	—	—	—	—
	No. 96	—	—	—	—
543-1	No. 43	—	—	—	—
543-2	No. 42	—	2	1	1
544-1	No. 41	—	—	—	—
544-2	No. 40	—	2	—	1
	No. 39	—	2	—	1

※No. 38 [544-3] は [545-1] に計上

付帯工平面図 (3) A1図面 S=1:300
A3図面 S=1:600下 福
水 岡
道 市

設 計 番 号

図 面 番 号

17 21

福 岡
地 区 下 水 道 築 造 工 事
付 帯 工 平 面 図 (3)
(桜坂二丁目)

(桜坂二丁目)

375 2	543 1	543 2
544 1	544 2	544 3

下水道施設凡例	
記 号	規 格
●	1号マンホール
○	2号マンホール
○	小口径汚水側・取付管
○	A型及びB型汚水側・取付管
■	雨水側・取付管
△	不明管

取付管施工内容

A	既設側・取付管撤去 → 小口径汚水側設置・取付管設置
B	既設側・取付管撤去 → B型汚水側設置・取付管設置
C	既設側・取付管撤去 → MA雨水側設置・取付管設置
D	既設側・取付管撤去 → 雨水側設置・取付管設置
E	既設側・取付管撤去 → 街渠側設置・取付管設置
F	既設側・取付管撤去 → 集水側設置・取付管設置
G	既設側・取付管撤去 → 側溝・取付管設置
H	既設側撤去 → 蓋替
I	取付管撤去 → 取付管設置
J	未使用管 (既設側・取付管撤去) → キャップ止
K	不明管 (取付管撤去) → キャップ止
L	現状維持
M	取付管撤去 → 小口径汚水側設置・取付管設置



人孔修繕一覧表

路線番号	人孔番号	蓋・口環	足掛金物	安全梯子	インバート
9009-2	No. 16	—	3	1	—
	No. 15	—	4	1	—

付帯工平面図 (4) A1図面 S=1:300
A3図面 S=1:600

下水道施設凡例

記号	規格
●	1号マンホール
○	2号マンホール
○	小口径汚水樹・取付管
○	A型及びB型汚水樹・取付管
■	雨水樹・取付管
—	不明管

取付管施工内容

A	既設樹・取付管撤去 → 小口径汚水樹設置・取付管設置
B	既設樹・取付管撤去 → B型汚水樹設置・取付管設置
C	既設樹・取付管撤去 → MA雨水樹設置・取付管設置
D	既設樹・取付管撤去 → 細雨水樹設置・取付管設置
E	既設樹・取付管撤去 → 街渠樹設置・取付管設置
F	既設樹・取付管撤去 → 集水樹設置・取付管設置
G	既設樹撤去・取付管撤去 → 樹替・取付管設置
H	既設樹撤去 → 蓋替
I	取付管撤去 → 取付管設置
J	未使用管(既設樹・取付管撤去) → キャップ止
K	不明管(取付管撤去) → キャップ止
L	現状維持
M	取付管撤去 → 小口径汚水樹設置・取付管設置

クリアホームズ
赤坂けやきの杜

天満宮

ヴィラ桜坂

KBM 4-1
H=24.411
コアマンション
赤坂けやき水流量 DIP 420
D=1.20mガス配 P1450
D=1.00m

既設1号マンホールNo.15

既設1号マンホールNo.15

9009
2

東生工業 T-14 自立管

人孔修繕一覧表


路線番号	人孔番号	蓋・口環	足掛金物	安全梯子	インバート
370-2	No. 109	—	—	—	—
370-3	No. 108	1	—	1	—
370-4	No. 107	—	—	—	—
370-5	No. 106	1	—	1	—
	No. 105	—	—	—	—

下水道施設凡例

記号	規格
●	1号マンホール
○	2号マンホール
○	小口径汚水管・取付管
○	A型及びB型汚水管・取付管
■	雨水管・取付管
—	不明管

取付管施工内容

A	既設管・取付管撤去 → 小口径汚水管設置・取付管設置
B	既設管・取付管撤去 → B型汚水管設置・取付管設置
C	既設管・取付管撤去 → MA雨水管設置・取付管設置
D	既設管・取付管撤去 → 細雨水管設置・取付管設置
E	既設管・取付管撤去 → 樹木管設置・取付管設置
F	既設管・取付管撤去 → 雨水管設置・取付管設置
G	既設管撤去・取付管撤去 → 樹管・取付管設置
H	既設管撤去 → 蓋替
I	取付管撤去 → 取付管設置
J	未使用管（既設管・取付管撤去）→ キャップ止
K	不明管（取付管撤去）→ キャップ止
L	現状維持
M	取付管撤去 → 小口径汚水管設置・取付管設置

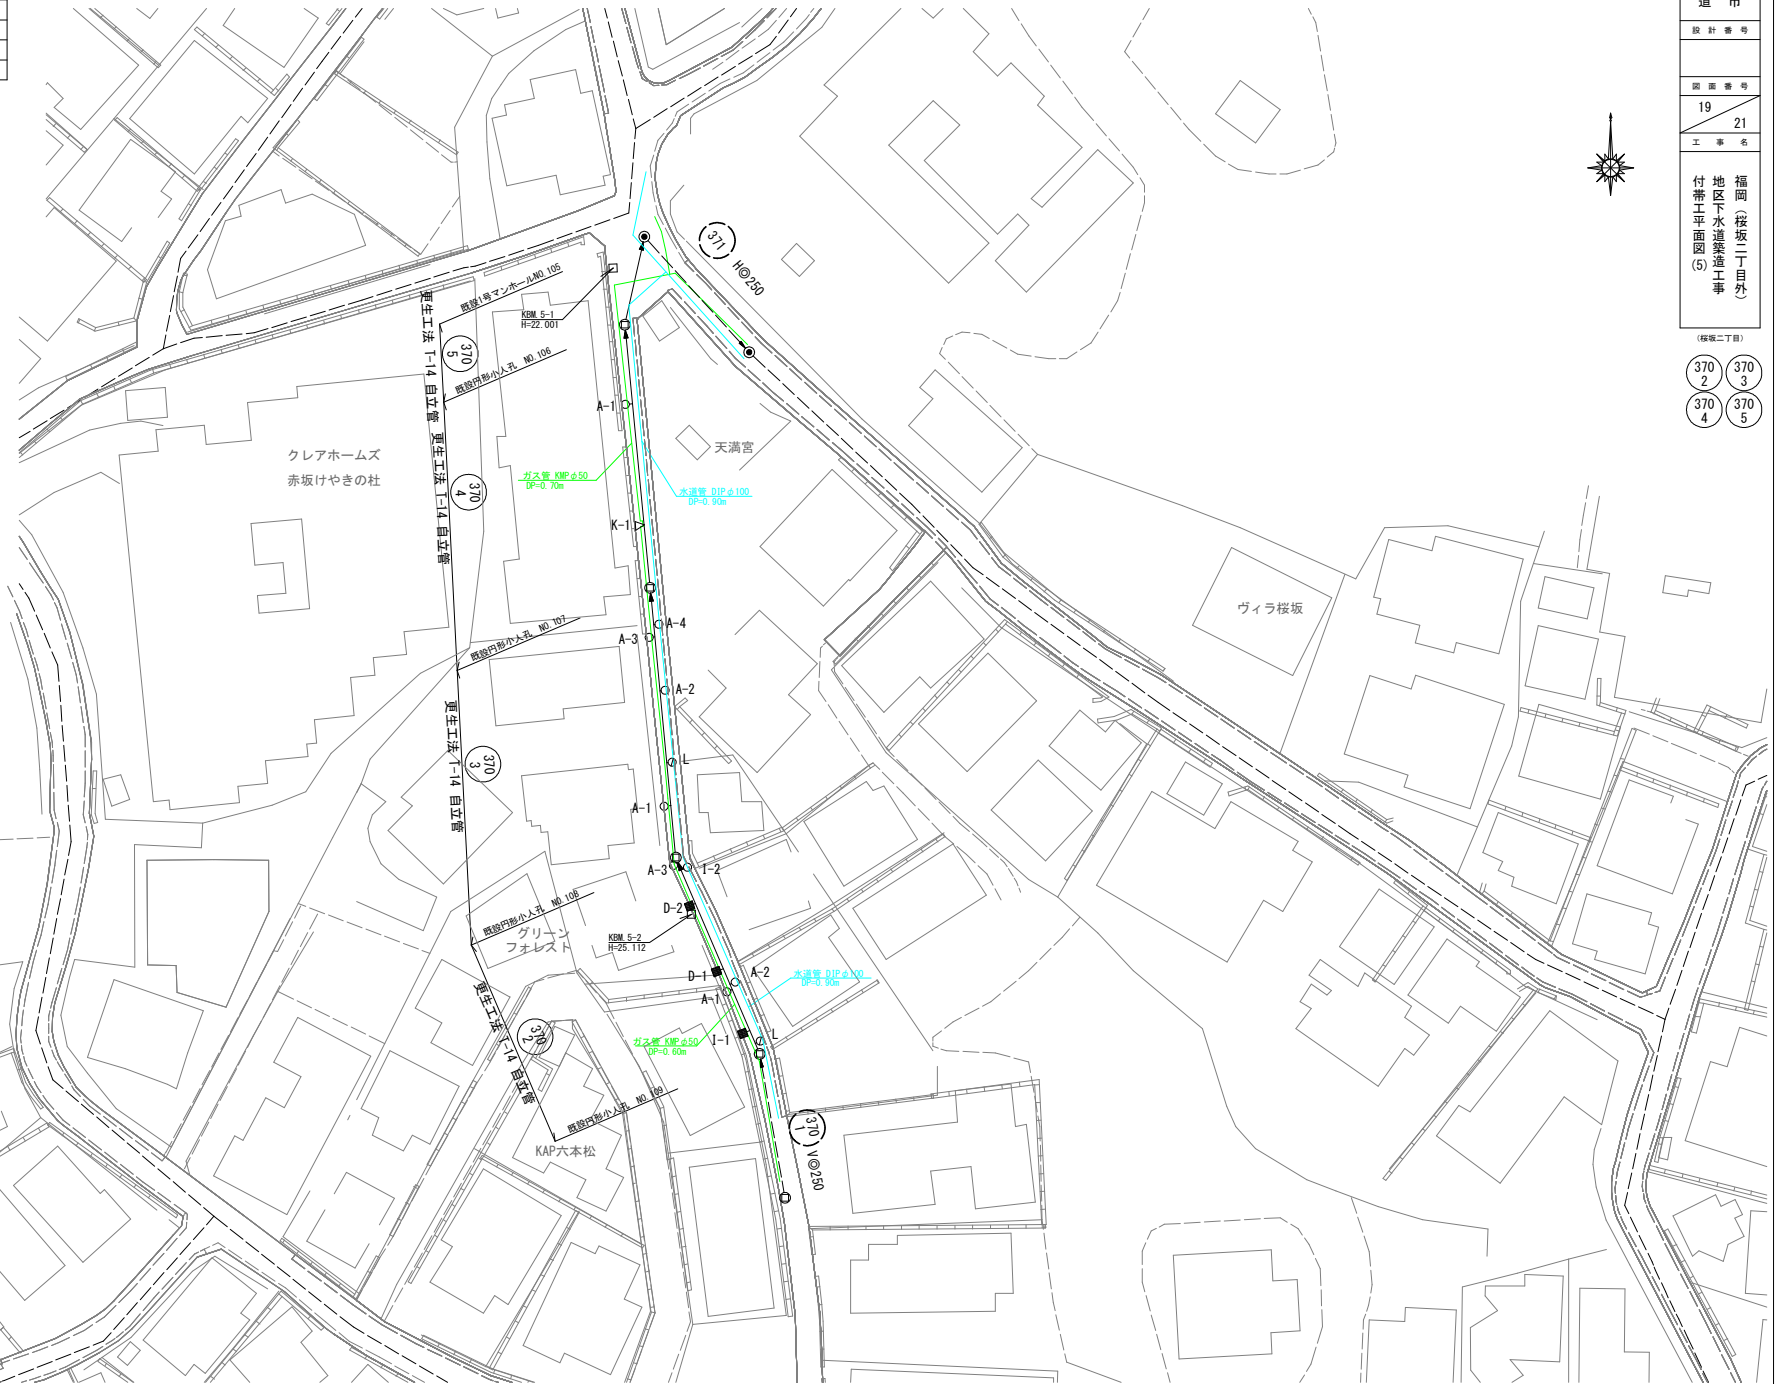付帯工平面図 (5) A1図面 S=1:300
A3図面 S=1:600

人孔修繕一覧表

路線番号	人孔番号	蓋・口環	足掛金物	安全梯子	インバート
430-2	No. 54	—	3	—	1
	No. 53	—	—	—	—
441-1	No. 110	1	—	1	—
	No. 109	1	—	1	—


下水道施設凡例

記号	規格
●	1号マンホール
○	2号マンホール
○	小口径汚水樹・取付管
○	A型及びB型汚水樹・取付管
■	雨水樹・取付管
△	不明管

取付管施工内容

A	既設樹・取付管撤去 → 小口径汚水樹設置・取付管設置
B	既設樹・取付管撤去 → B型汚水樹設置・取付管設置
C	既設樹・取付管撤去 → MA雨水樹設置・取付管設置
D	既設樹・取付管撤去 → 細雨水樹設置・取付管設置
E	既設樹・取付管撤去 → 街渠樹設置・取付管設置
F	既設樹・取付管撤去 → 集水樹設置・取付管設置
G	既設樹撤去 → 樹替・取付管設置
H	既設樹撤去 → 蓋替
I	取付管撤去 → 取付管設置
J	未使用管（既設樹・取付管撤去）→ キャップ止
K	不明管（取付管撤去）→ キャップ止
L	現状維持
M	取付管撤去 → 小口径汚水樹設置・取付管設置

付帯工平面図 (6) A1図面 S=1:300
A3図面 S=1:600

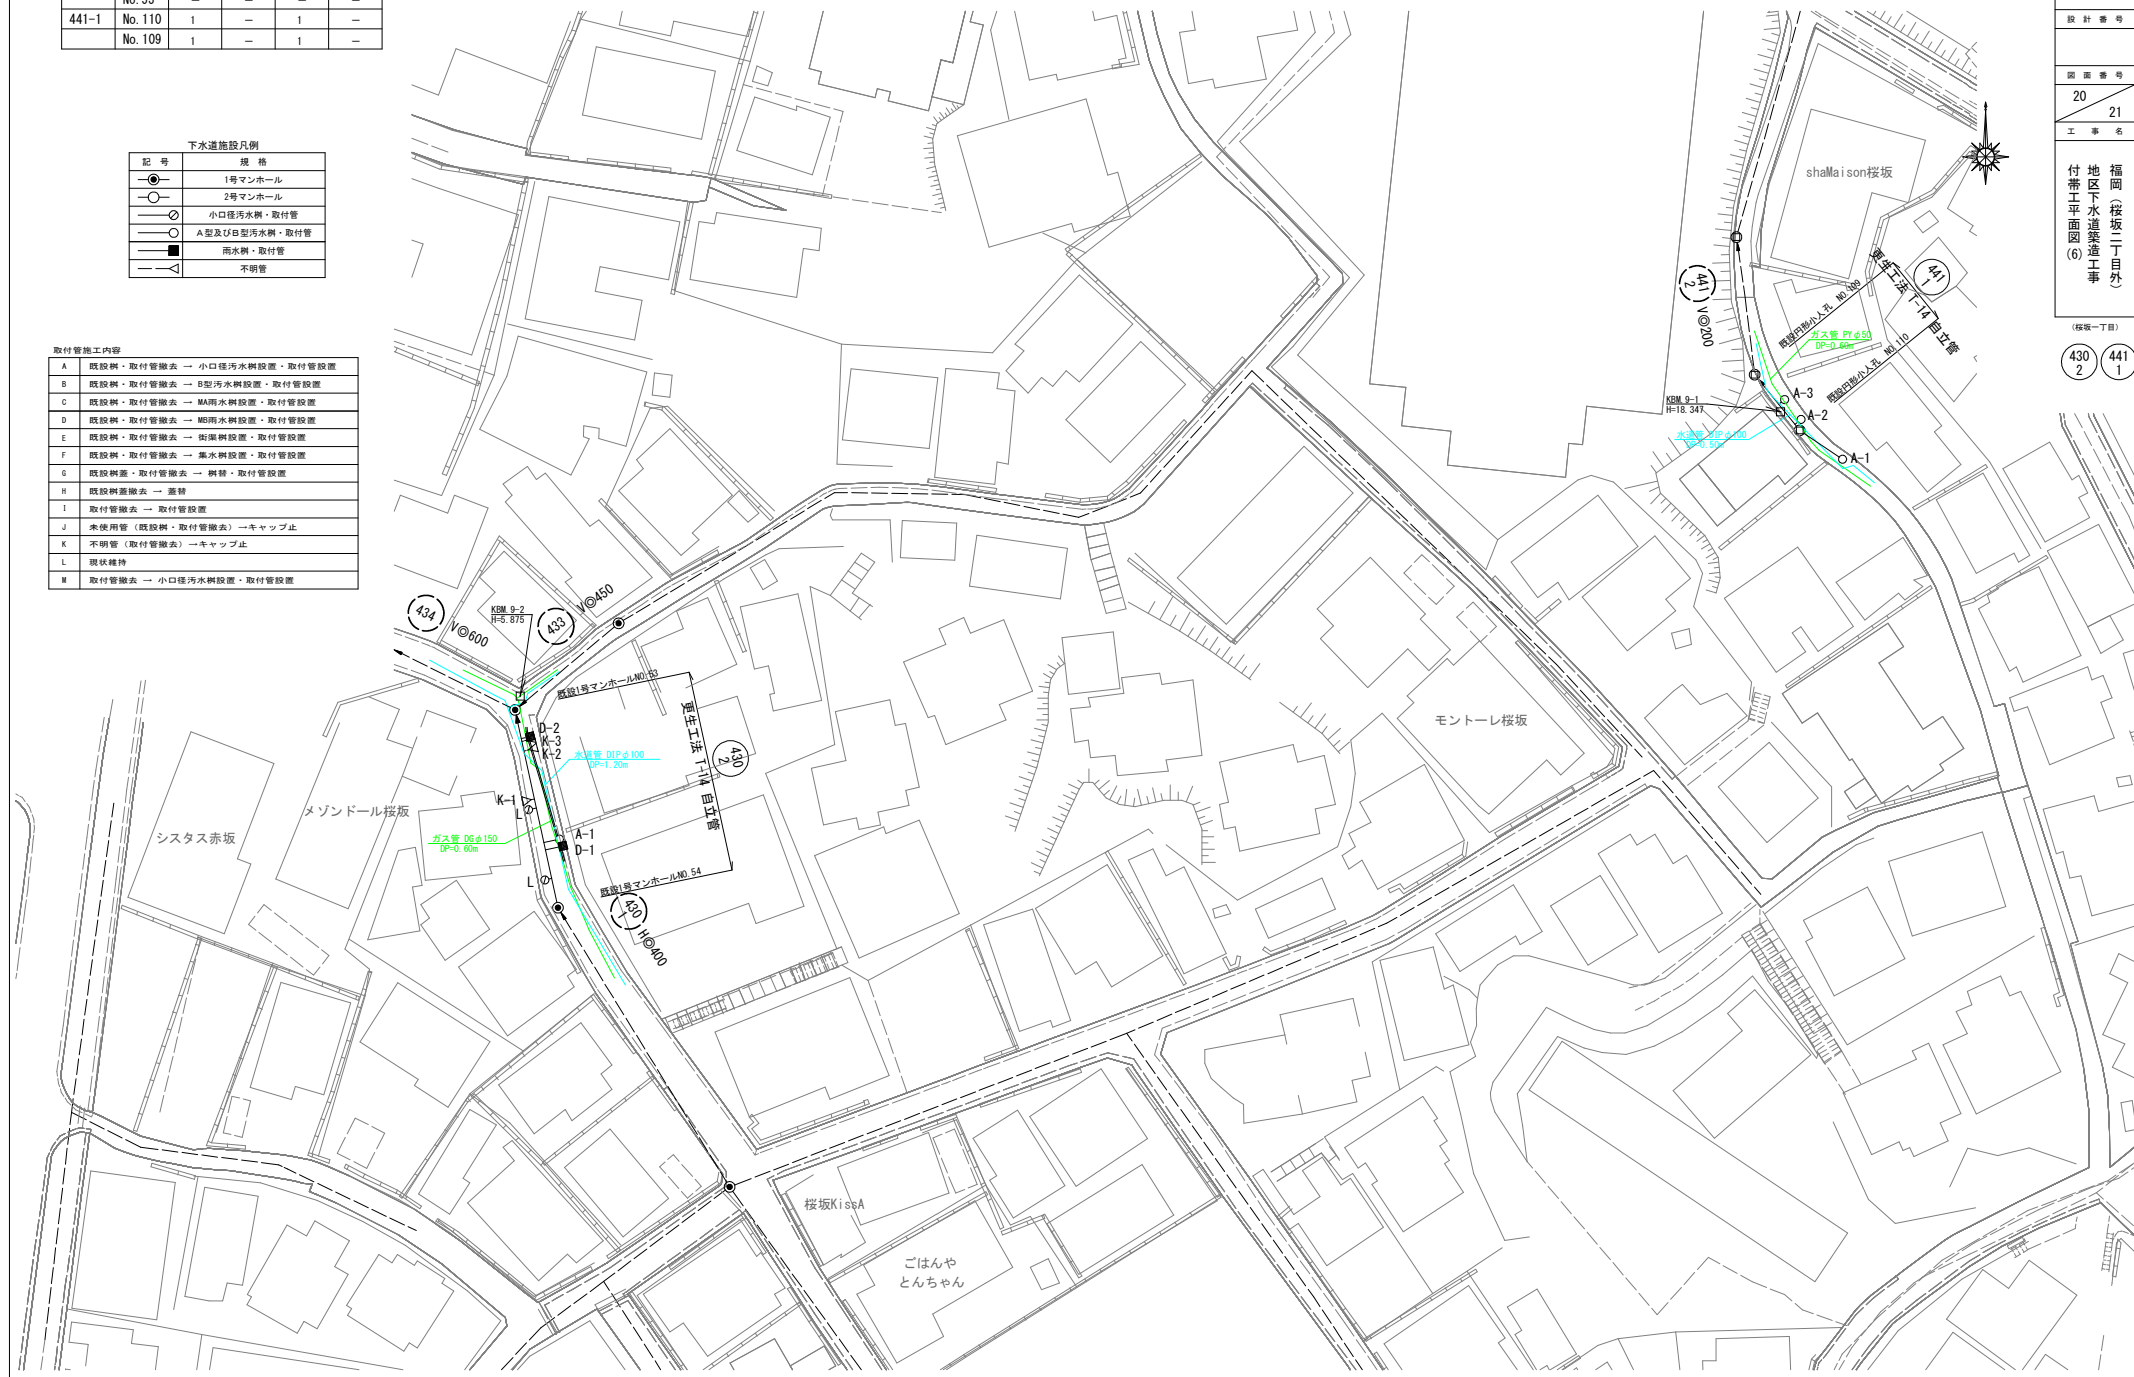

福岡市

設計番号

図面番号
20/21

工事名

福岡市 地区下水道築造工事
付帯工平面図(6)

(縮小一丁目)

430-2 441-1

人孔修繕一覧表

路線番号	人孔番号	蓋・口環	足掛金物	安全梯子	インバート
426-3	No. 86	—	—	1	1
	No. 85	—	—	1	—

付帯工平面図 (7) A1図面 S=1:300
A3図面 S=1:600

下 福
水 岡
道 市

図 計 書 号

図 面 番 号
21 / 21

工 事 名

福岡（桜坂二丁目外）
地区下水道築造工事
付帯工平面図 (7)

(桜坂一丁目)

426
3



記 号	規 格
●	1号マンホール
○	2号マンホール
○	小口径汚水樹、取付管
○	A型及びB型汚水樹、取付管
■	雨水樹、取付管
—	不明管

下水道施設凡例

取付管施工内容

A	既設樹、取付管撤去 → 小口径汚水樹設置、取付管設置
B	既設樹、取付管撤去 → B型汚水樹設置、取付管設置
C	既設樹、取付管撤去 → MA雨水樹設置、取付管設置
D	既設樹、取付管撤去 → MB雨水樹設置、取付管設置
E	既設樹、取付管撤去 → 街渠樹設置、取付管設置
F	既設樹、取付管撤去 → 集水樹設置、取付管設置
G	既設樹撤去 → 新樹、取付管設置
H	既設樹撤去 → 蓋替
I	取付管撤去 → 取付管設置
J	未使用管（既設樹、取付管撤去） → キャップ止
K	不明管（取付管撤去） → キャップ止
L	現状維持
M	取付管撤去 → 小口径汚水樹設置、取付管設置

