

平面図 (1)

A 1 図面 S=1:300
A 3 図面 S=1:600

下 福
水 岡
道 市

設計番号

図面番号


1 6

工 事 名

平尾高宮(大楠一丁目3)
地区下水道築造工事

946
-3
945
-1
945
-2
942
-1

位置図 S=1:10000

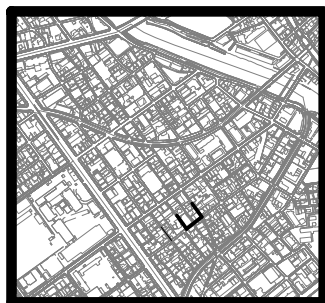


371E




人孔凡例	
凡 例	
5号マンホール	
4号マンホール	
3号マンホール	
2号マンホール	
1号マンホール	
特1号マンホール	
特殊マンホール	
特0号マンホール	
円形小マンホール (内径60cm)	

取付管凡例	
記 号	規 格
	小口径汚水樹・取付管
	A型及びB型汚水樹取付管
	雨水樹・取付管
	雨水樹(円形)・取付管
	不明管

地下埋設物凡例	
記 号	種 類
	汚水(合流)
	雨 水
	上 水
	ガ ス
	電気(配電)
	電気(送電)
	N T T

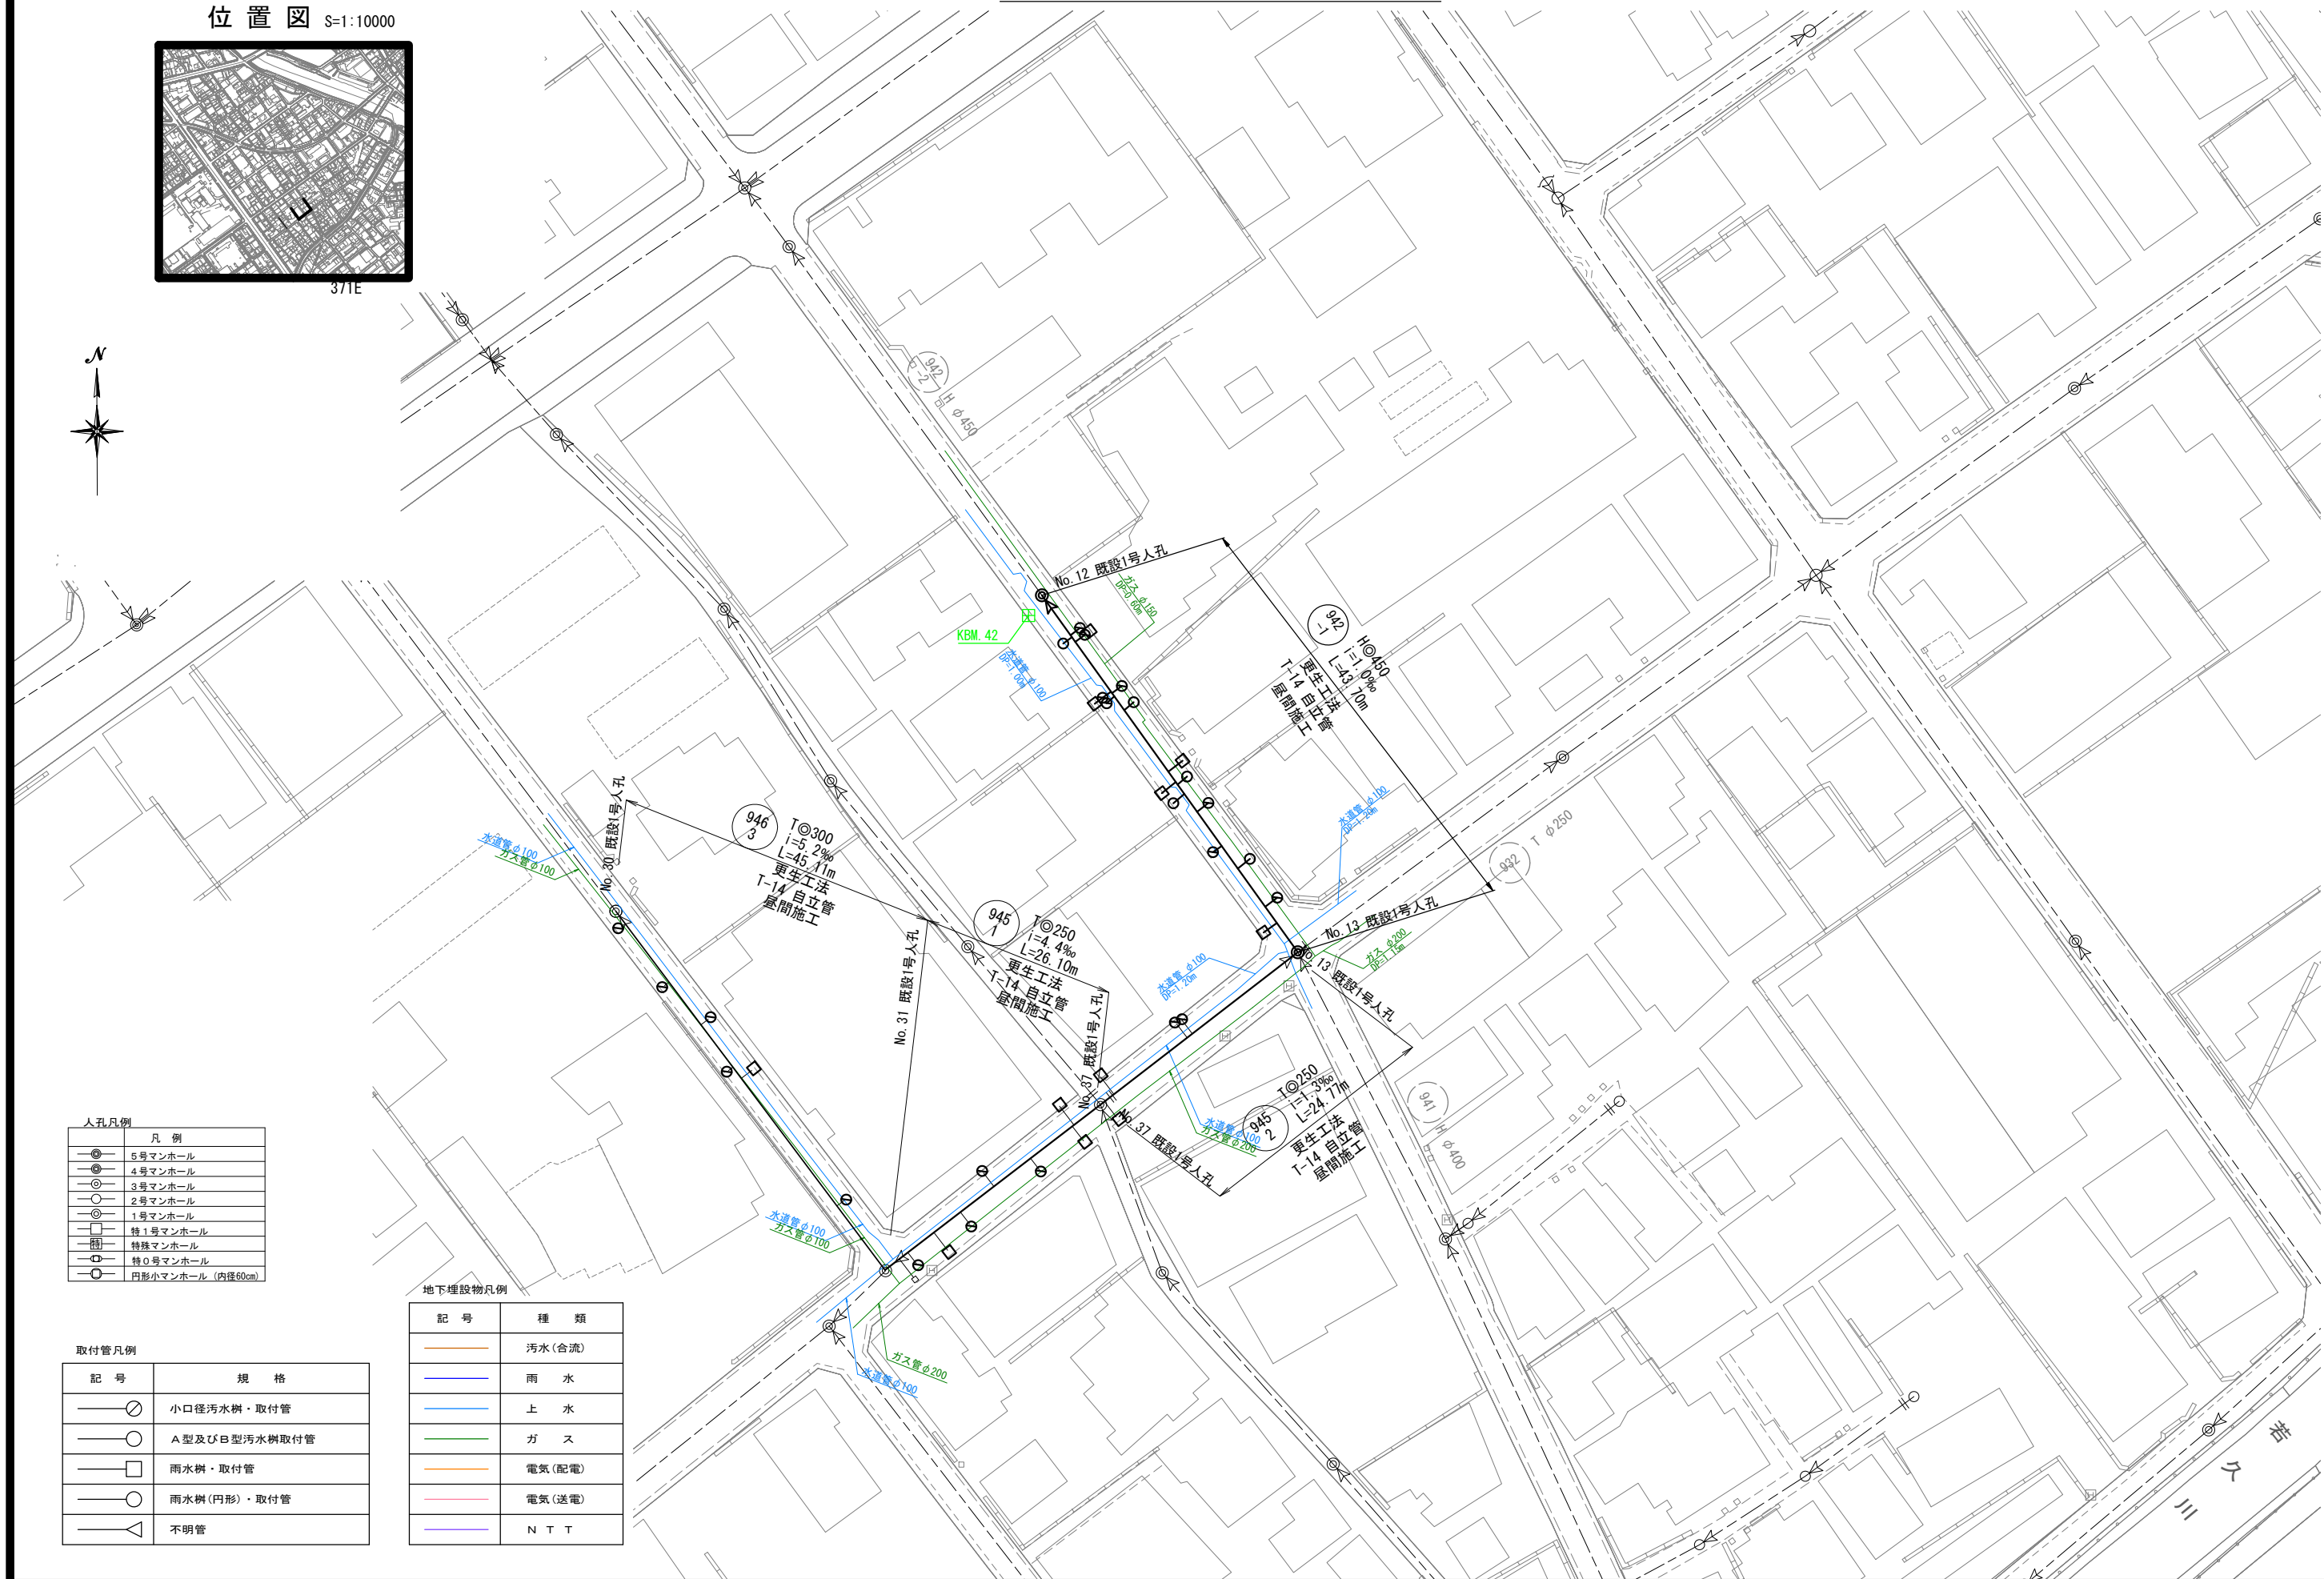

位置図 S=1:10000

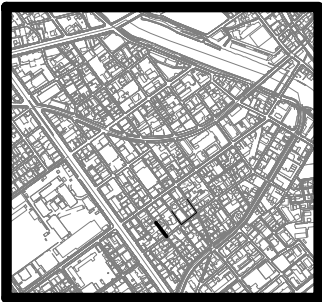

3/1E

平面図 (2)

A 1 図面 S=1:300
A 3 図面 S=1:600

下 福
水 岡
道 市

設計番号

図面番号

2 6

工 事 名

平尾高宮(大楠一丁目3)
地区下水道築造工事

大楠一丁目

956
-1

人孔凡例	
凡 例	
5号マンホール	
4号マンホール	
3号マンホール	
2号マンホール	
1号マンホール	
特1号マンホール	
特殊マンホール	
特0号マンホール	
円形小マンホール (内径60cm)	

取付管凡例	
記 号	規 格
小口径汚水樹・取付管	
A型及びB型汚水樹取付管	
雨水樹・取付管	
雨水樹(円形)・取付管	
不明管	

地下埋設物凡例	
記 号	種 類
汚水(合流)	
雨 水	
上 水	
ガ ス	
電気(配電)	
電気(送電)	
N T T	



縦断図 (1) 縦 S=1:100
横 S=1:300

下福岡水道市

設計番号


図面番号

36


工事名

平尾高宮(大楠一丁目3)地区下水道築造工事

- 946-3
- 945-1
- 945-2
- 942-1

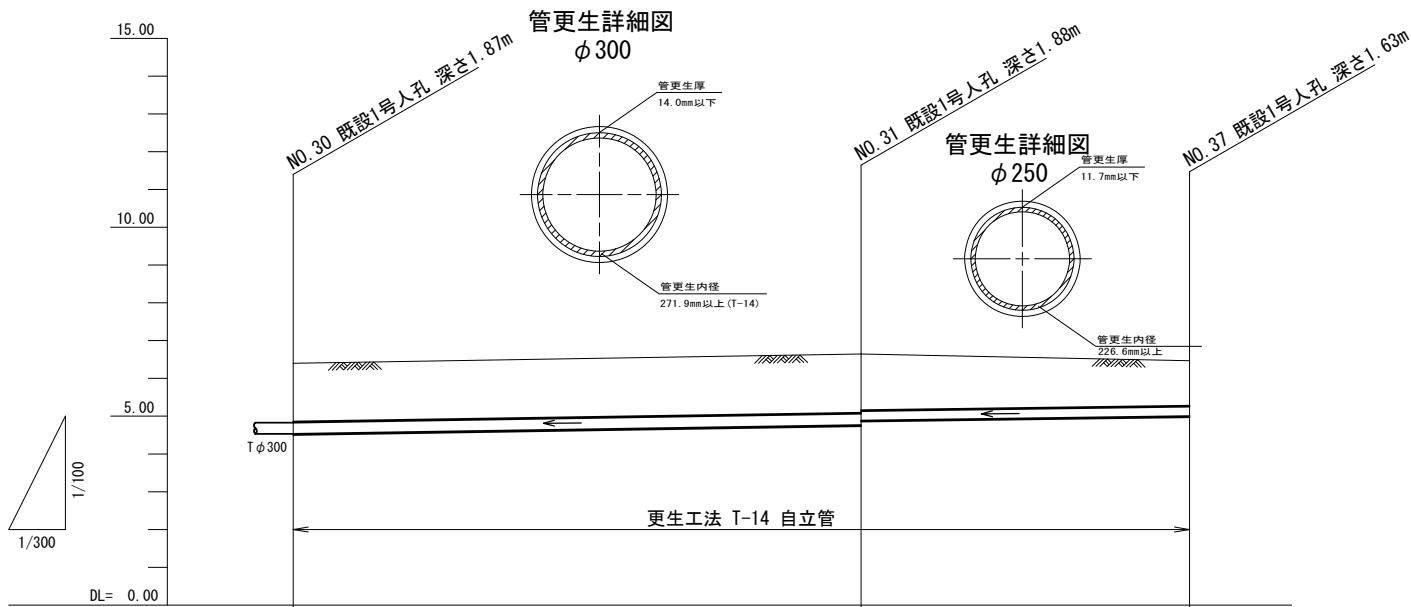

路線番号		946 3	945 1	
既設管径		φ300	φ250	
勾配		i=5.2‰	i=4.4‰	
区間距離		L=45.11m	L=26.10m	
現況地盤高	6.40	6.64	6.47	
土被り	1.54	1.55 1.48	1.19	
管底高	4.530 4.530	4.764 4.884	5.000	
掘削深	2.00	2.01 1.88	1.60	
追加距離	0.00	45.11	71.21	
管種 (施工年月日)		陶管、1973年(昭和48年)施工		
道路種別		車道アスファルト舗装(A)	車道アスファルト舗装(A)	

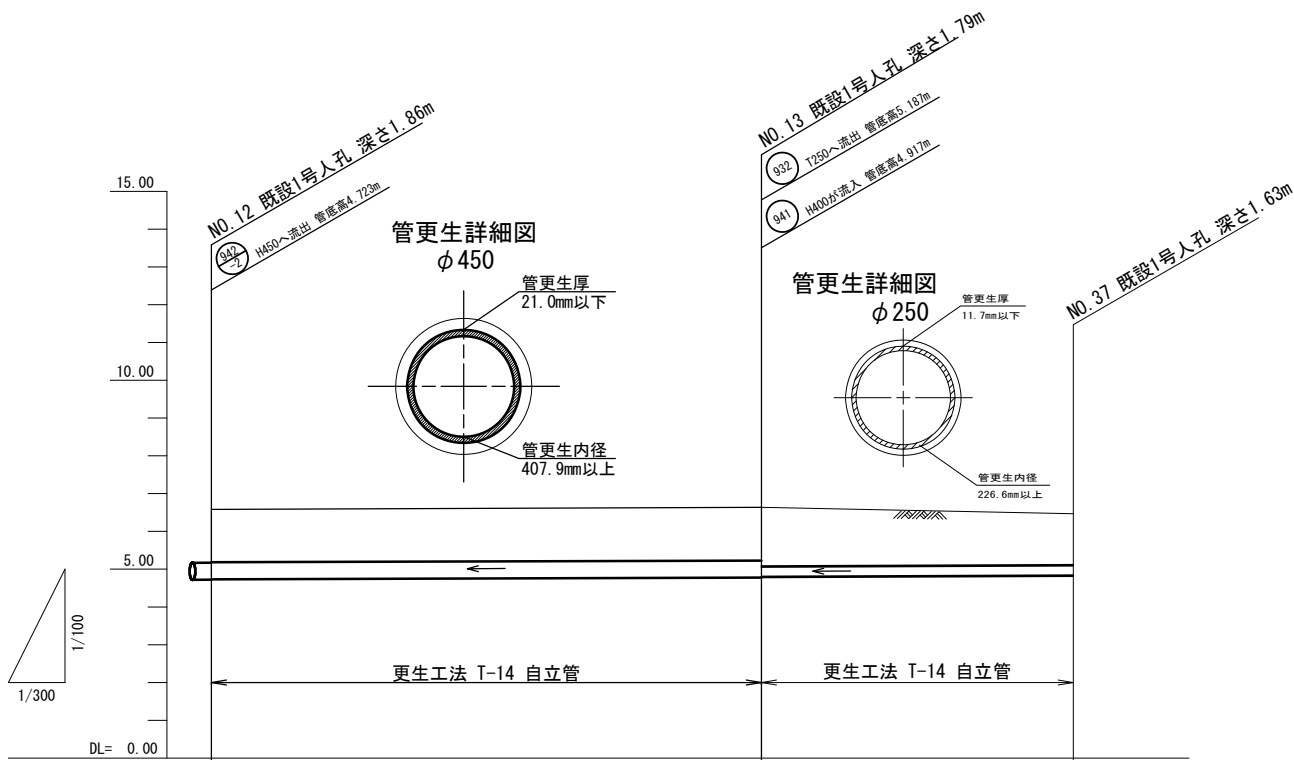

路線番号		942 -1	945 2	
既設管径		Hφ450	φ250	
勾配		i=1.0‰	i=1.3‰	
区間距離		L=43.70m	L=24.77m	
現況地盤高	6.58	6.60	6.47	
土被り	1.36	1.33 1.51	1.35	
管底高	4.723 4.733	4.778 4.808	4.840	
掘削深		1.92	1.76	
追加距離	0.00	43.70	68.47	
管種 (施工年月日)		H (1973年)	陶管、1972年(昭和47年)施工	
道路種別		車道アスファルト舗装(A)	車道アスファルト舗装(A)	

縦断図(2) 縦 S=1:100
横 S=1:300

下福岡水道市

設計番号

図面番号


46

工事名

平尾高宮(大桶一丁目3)地区下水道築造工事

大桶一丁目

956-1

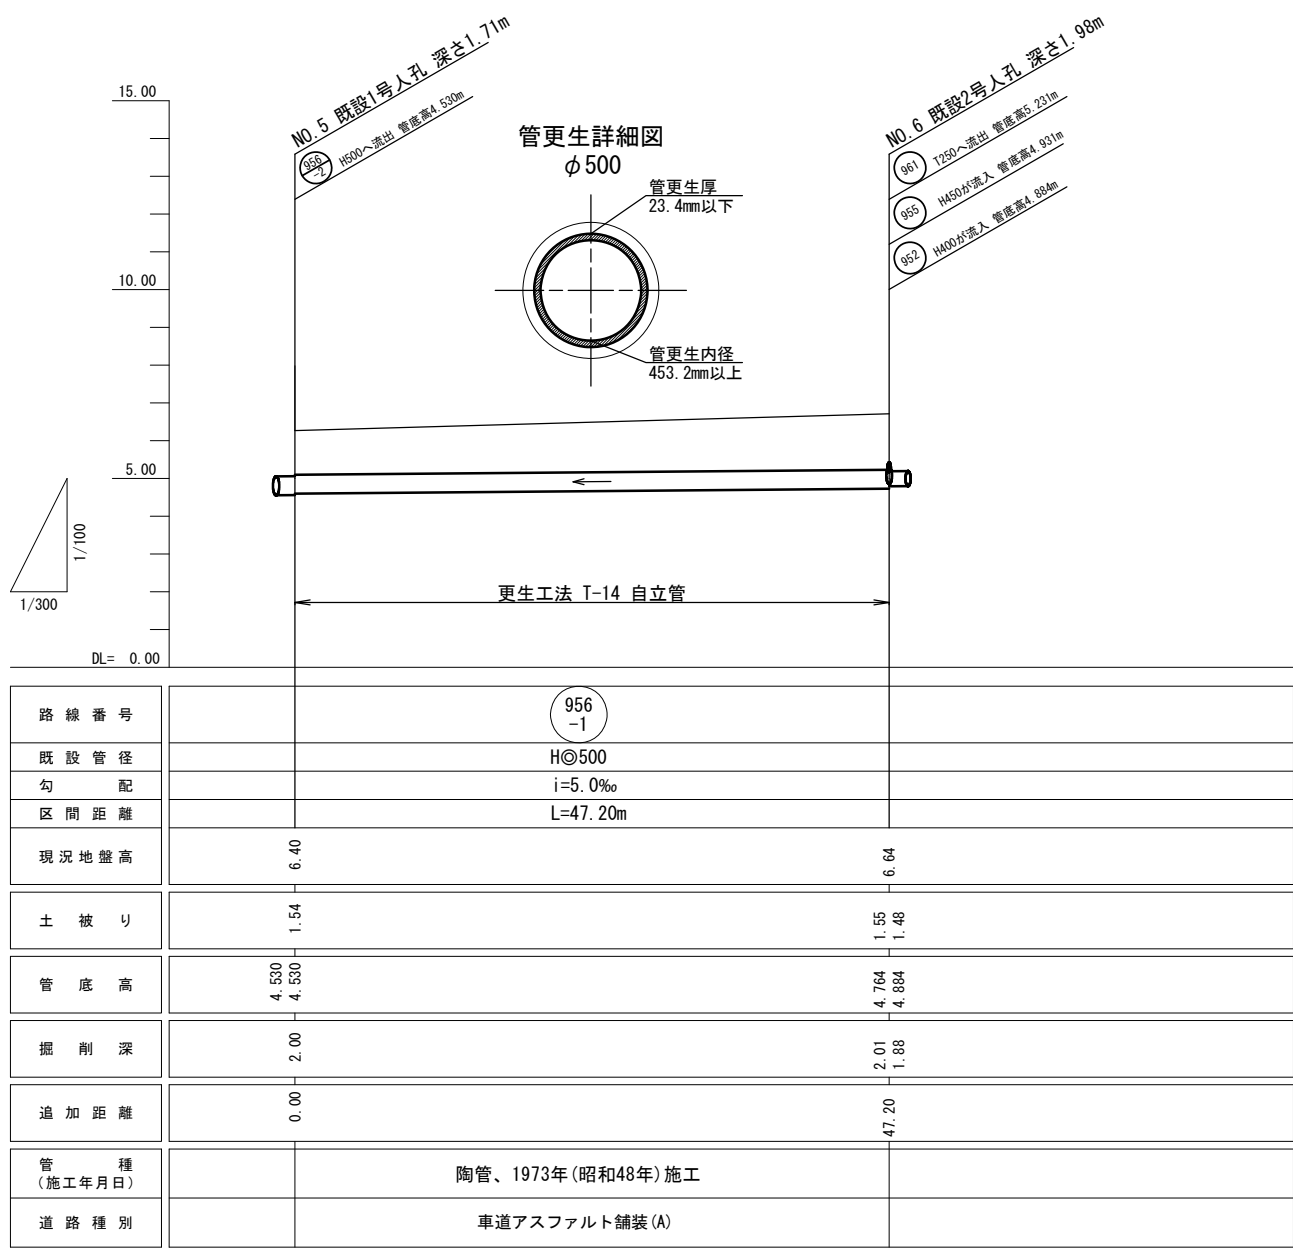

付帯工平面図 (1)

A 1 図面 S=1:300
A 3 図面 S=1:600

下福岡水道市

設計番号

図面番号

56

工事名

平尾高宮(大楠一丁目3)地区下水道築造工事

946-3
945-1
945-2
942-1



人孔凡例	
凡 例	
5号マンホール	
4号マンホール	
3号マンホール	
2号マンホール	
1号マンホール	
特1号マンホール	
特殊マンホール	
特0号マンホール	
円形小マンホール (内径60cm)	

取付管凡例	
記 号	規 格
	小口径汚水樹・取付管
	A型及びB型汚水樹取付管
	雨水樹・取付管
	雨水樹(円形)・取付管
	不明管

地下埋設物凡例	
記 号	種 類
	汚水(合流)
	雨 水
	上 水
	ガ ス
	電気(配電)
	電気(送電)
	N T T


取付管施工内容	
A	既設樹・取付管撤去→小口径汚水樹・取付管設置
B	取付管撤去→取付管設置
C	既設樹・取付管撤去→MA樹・取付管設置
D	既設樹・取付管撤去→MB樹・取付管設置
E	既設樹・取付管撤去→標準雨水樹・取付管設置
F	不明管(取付管)撤去→塩ビキャップ止
G	未使用管(既設樹・取付管)撤去→塩ビキャップ止
H	既設樹撤去→標準雨水樹設置
I	既設樹蓋・取付管撤去→蓋替・取付管設置
J	既設樹蓋撤去→蓋替
K	既設樹・取付管撤去→B型汚水樹・取付管設置
L	現状維持
M	既設樹・取付管撤去

人孔修繕一覧表					
路線番号	人孔番号	蓋・口環	足掛金物	安全梯子	インバート工
946-3	No. 30	-	4	-	-
	No. 31	-	-	-	-
945-1	No. 37	-	-	-	-
	No. 31	同上	同上	同上	同上
945-2	No. 13	-	-	-	-
	No. 37	同上	同上	同上	同上
942-1	No. 12	-	-	-	-
	No. 13	同上	同上	同上	同上

付帯工平面図 (2)

A 1 図面 S=1:300

A 3 図面 S=1:600

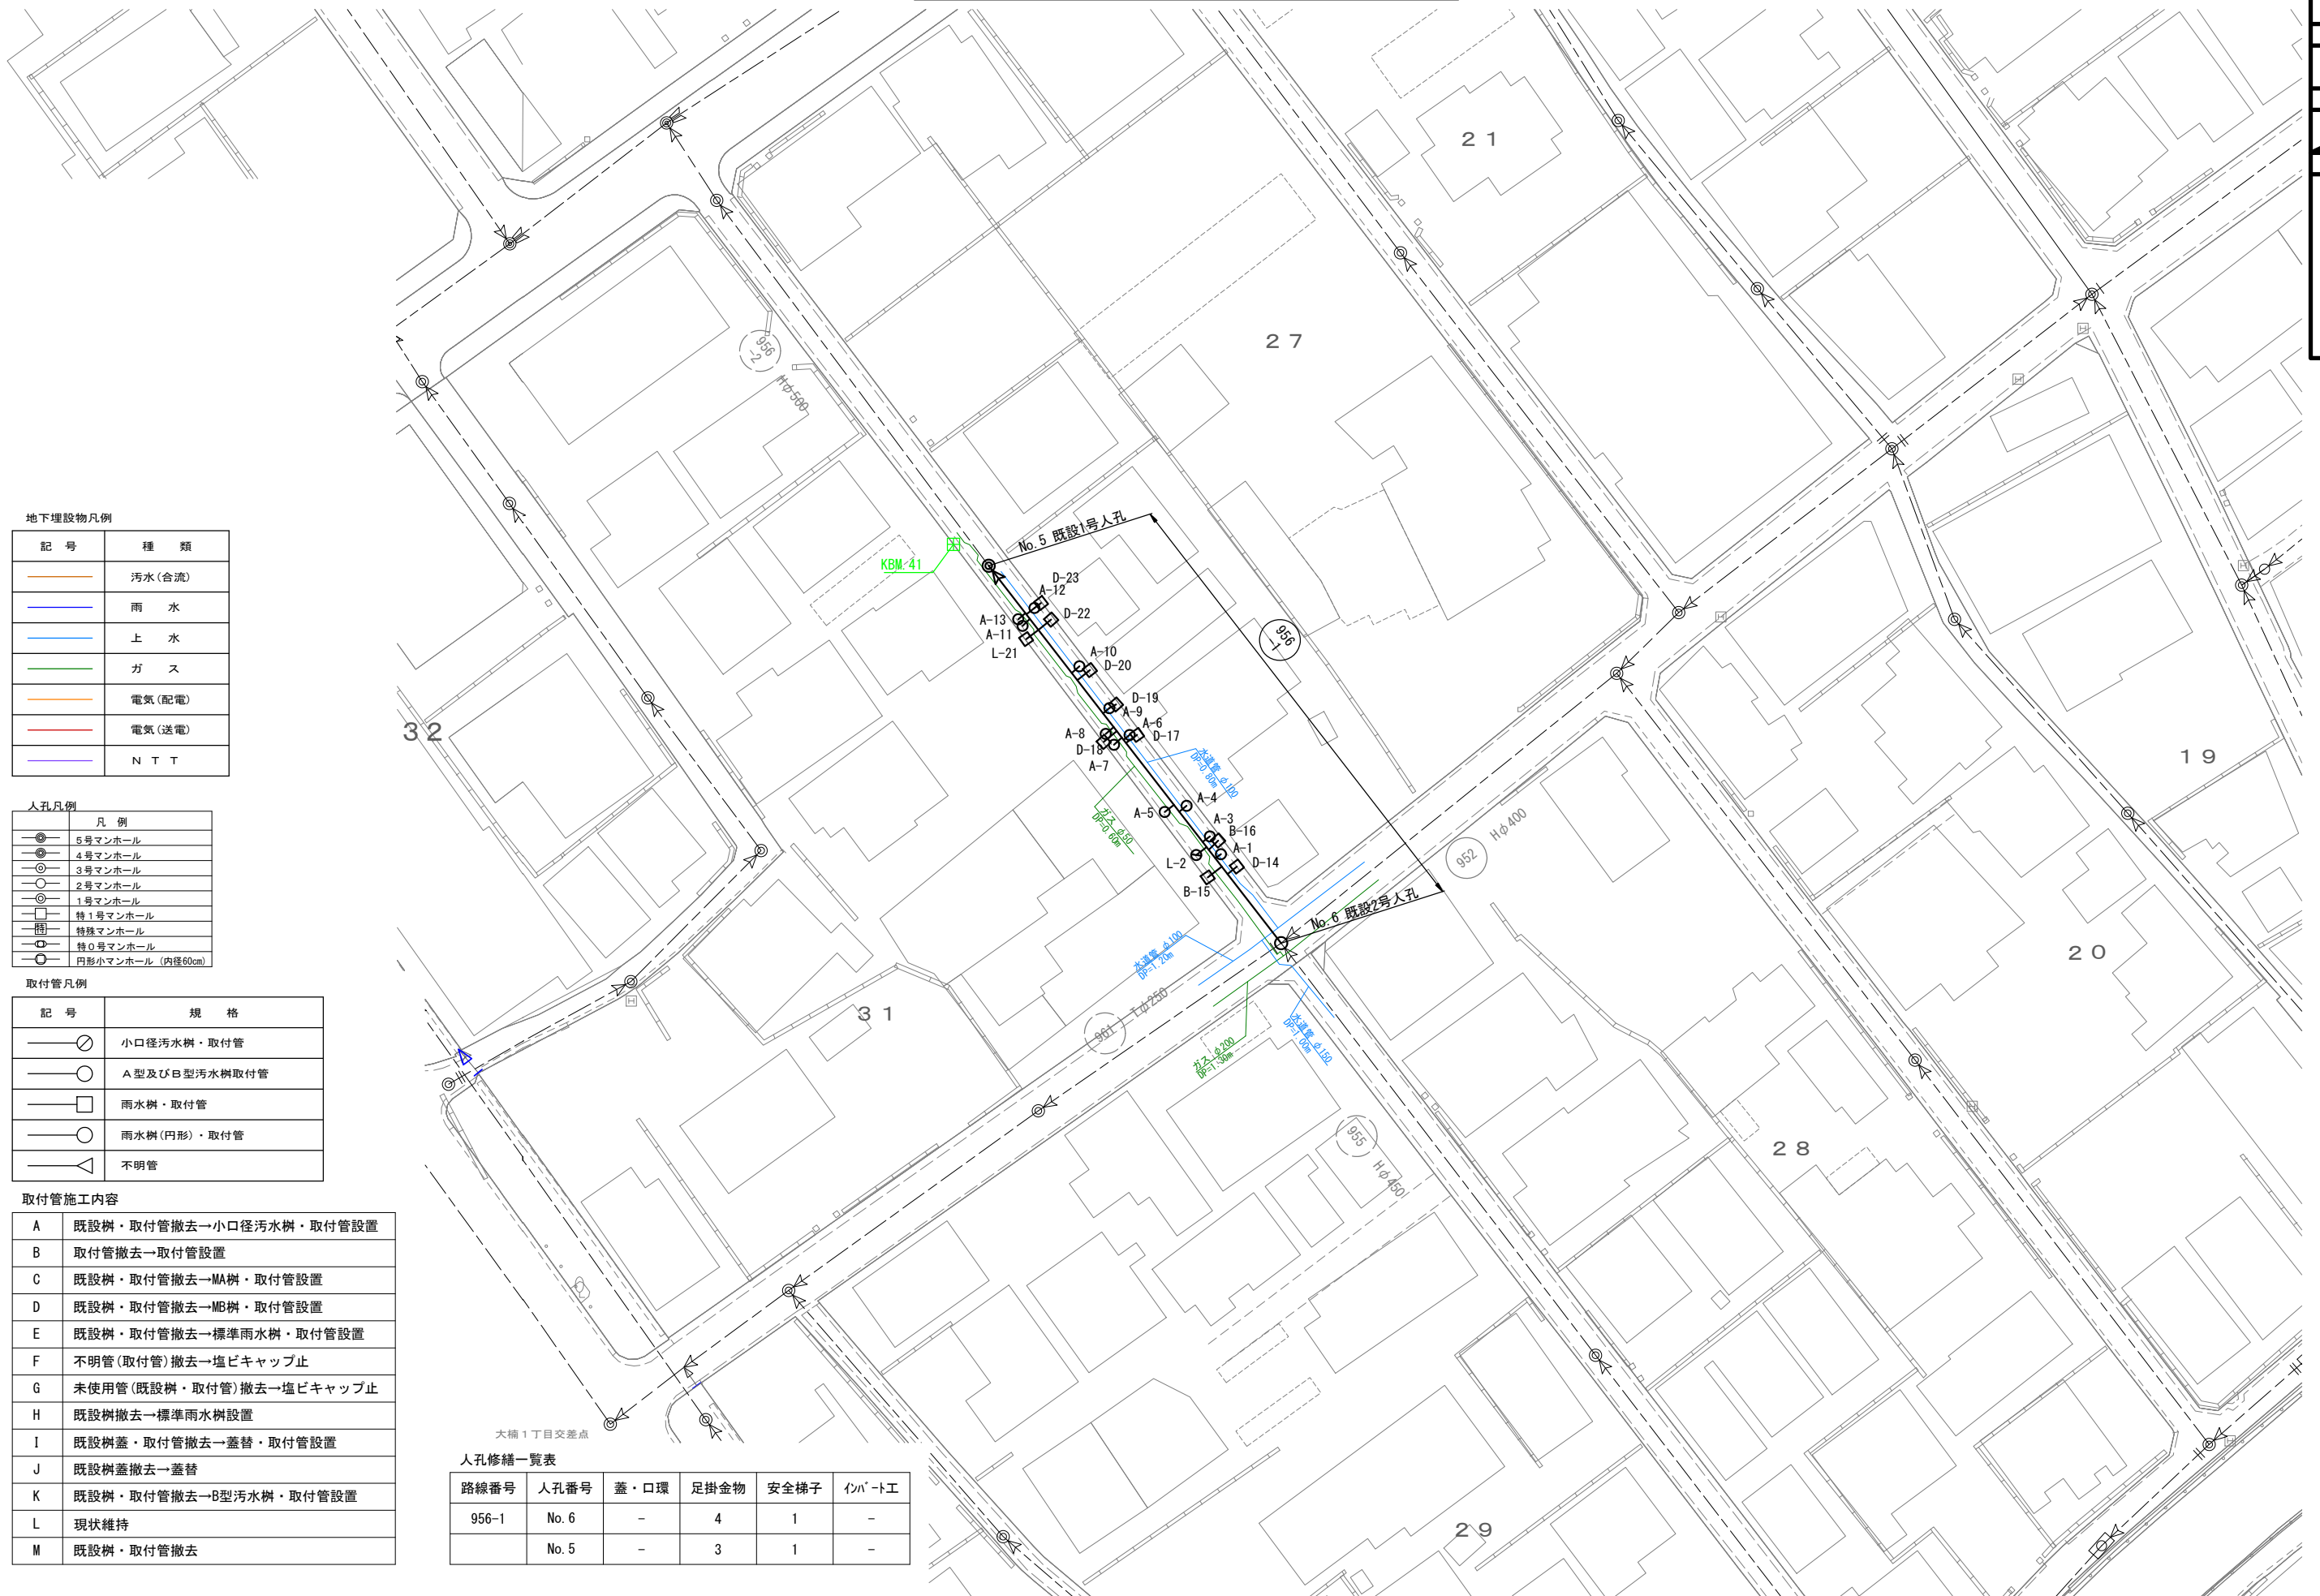

記 号	種 類
	汚水(合流)
	雨 水
	上 水
	ガ ス
	電気(配電)
	電気(送電)
	N T T

人孔凡例	
	凡 例
	5号マンホール
	4号マンホール
	3号マンホール
	2号マンホール
	1号マンホール
	特1号マンホール
	特殊マンホール
	特0号マンホール
	円形小マンホール (内径60cm)

記 号	規 格
	小口径汚水樹・取付管
	A型及びB型汚水樹取付管
	雨水樹・取付管
	雨水樹(円形)・取付管
	不明管

取付管施工内容	
A	既設樹・取付管撤去→小口径汚水樹・取付管設置
B	取付管撤去→取付管設置
C	既設樹・取付管撤去→MA樹・取付管設置
D	既設樹・取付管撤去→MB樹・取付管設置
E	既設樹・取付管撤去→標準雨水樹・取付管設置
F	不明管(取付管)撤去→塩ビキャップ止
G	未使用管(既設樹・取付管)撤去→塩ビキャップ止
H	既設樹撤去→標準雨水樹設置
I	既設樹蓋・取付管撤去→蓋替・取付管設置
J	既設樹蓋撤去→蓋替
K	既設樹・取付管撤去→B型汚水樹・取付管設置
L	現状維持
M	既設樹・取付管撤去

路線番号	人孔番号	蓋・口環	足掛金物	安全梯子	インポート工
956-1	No. 6	-	4	1	-
	No. 5	-	3	1	-