


|                                   |
|-----------------------------------|
| 福岡市                               |
| 下水道                               |
| 設計番号                              |
| 図面番号                              |
| 18                                |
| 工事名                               |
| 那珂 那珂二丁目外 地区<br>下水道工事<br>全体位置図(1) |

全体位置図(1) A1用 : S=1:2500  
A3用 : S=1:5000


那珂工区

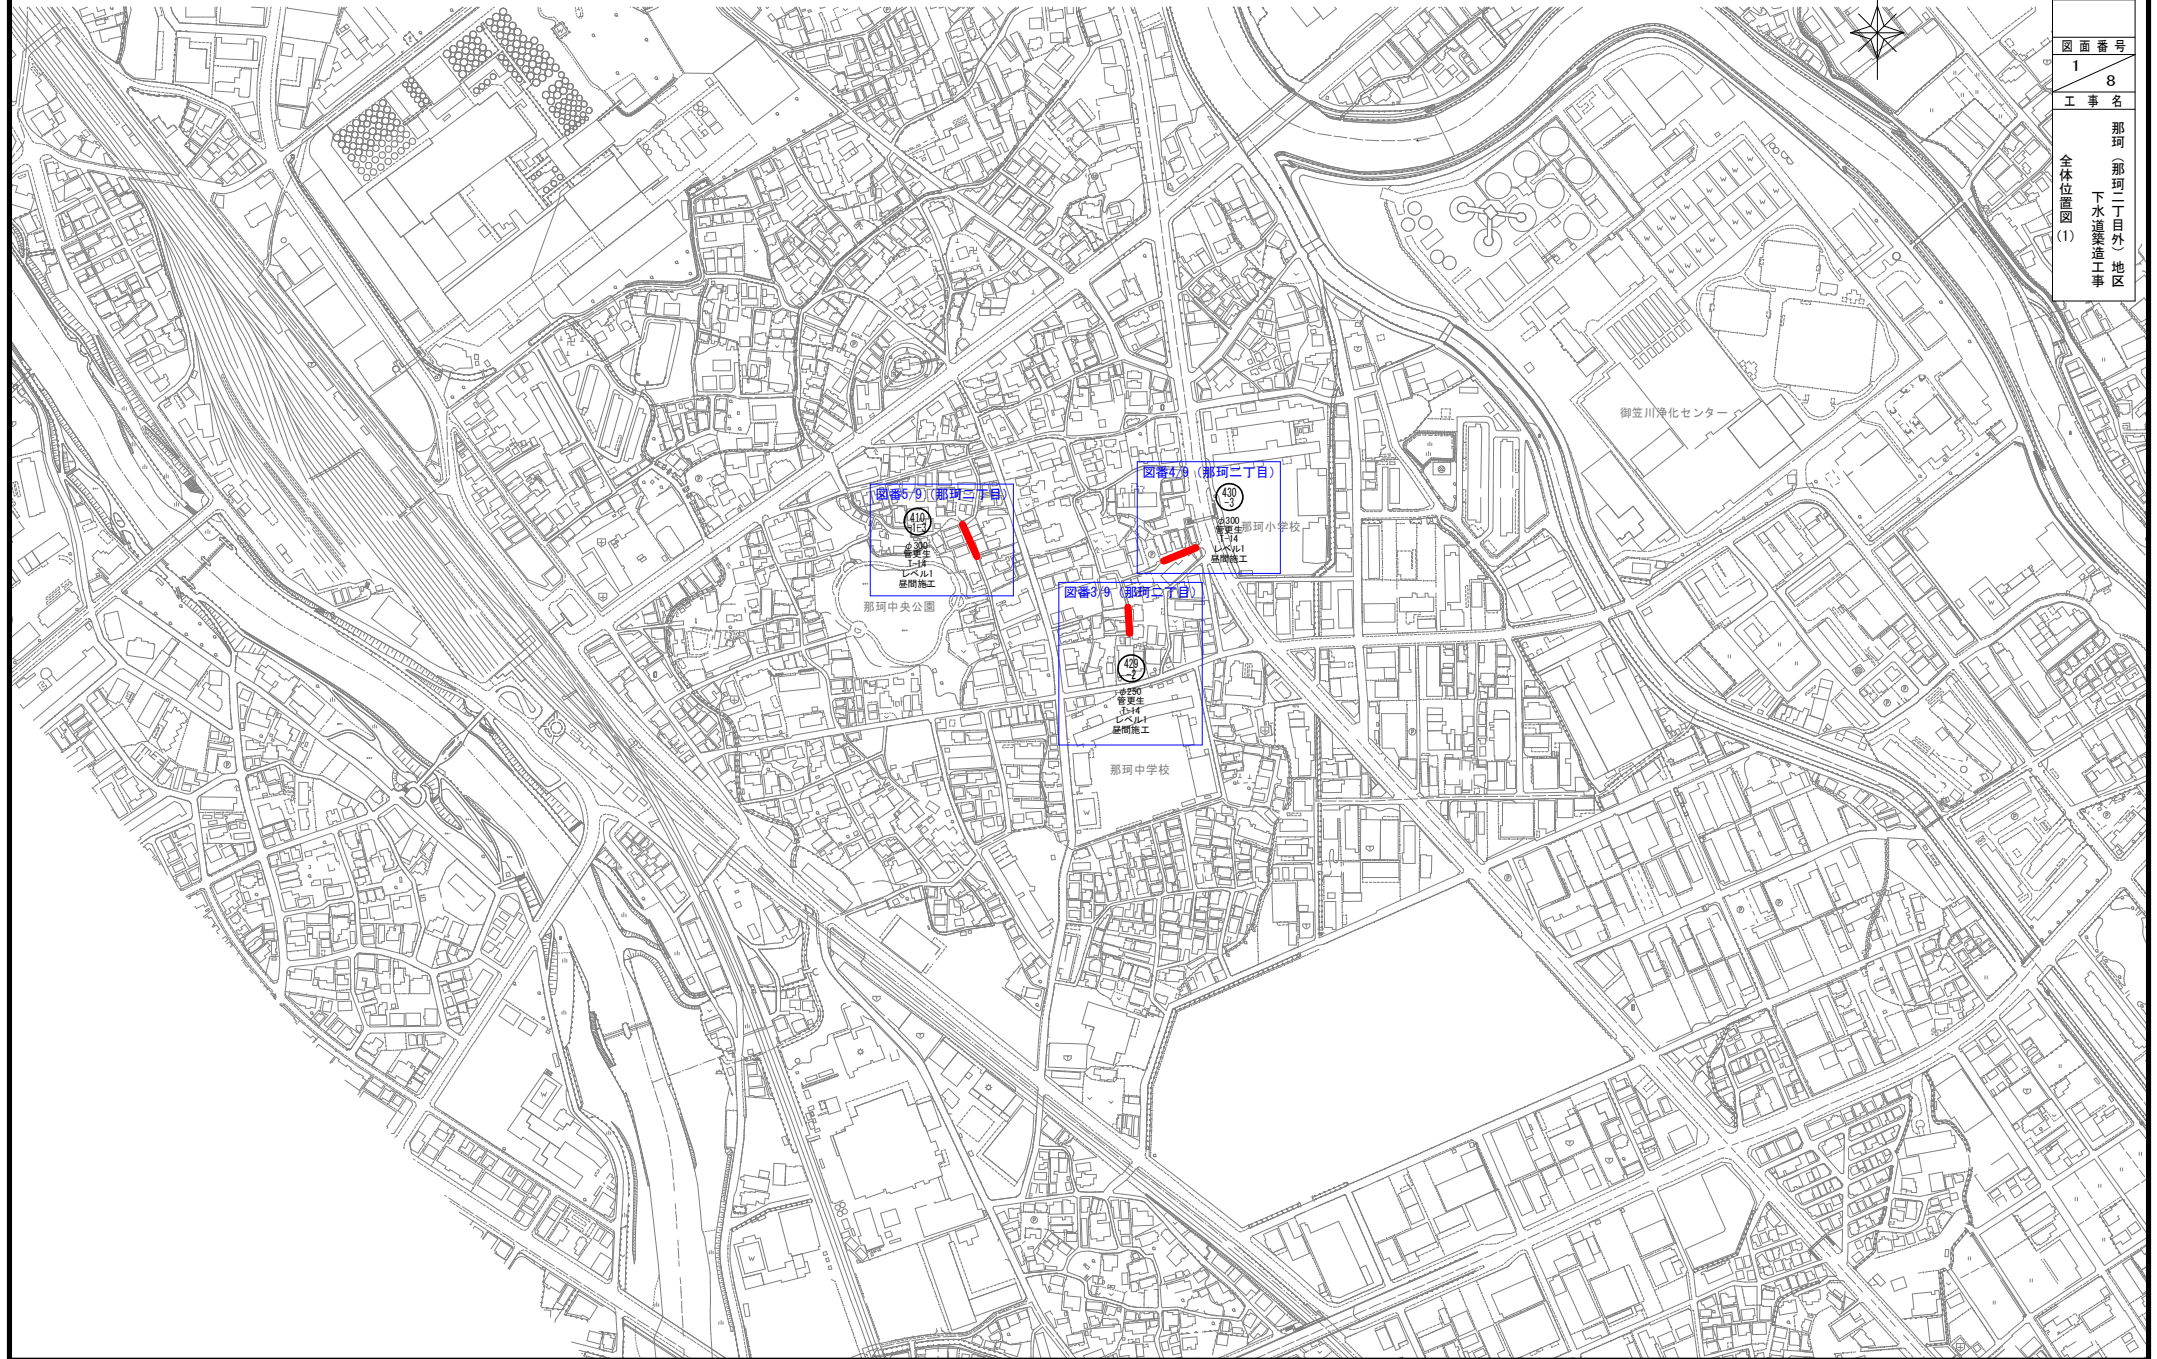

|            |
|------------|
| 福岡市        |
| 下水道        |
| 設計番号       |
| 図面番号       |
| 28         |
| 工事名        |
| 那珂那珂二丁目外地区 |
| 全体位置図(2)   |
| 下水道工事      |

位置図(2) A1用: S=1:2500  
A3用: S=1:5000

板付・諸岡工区

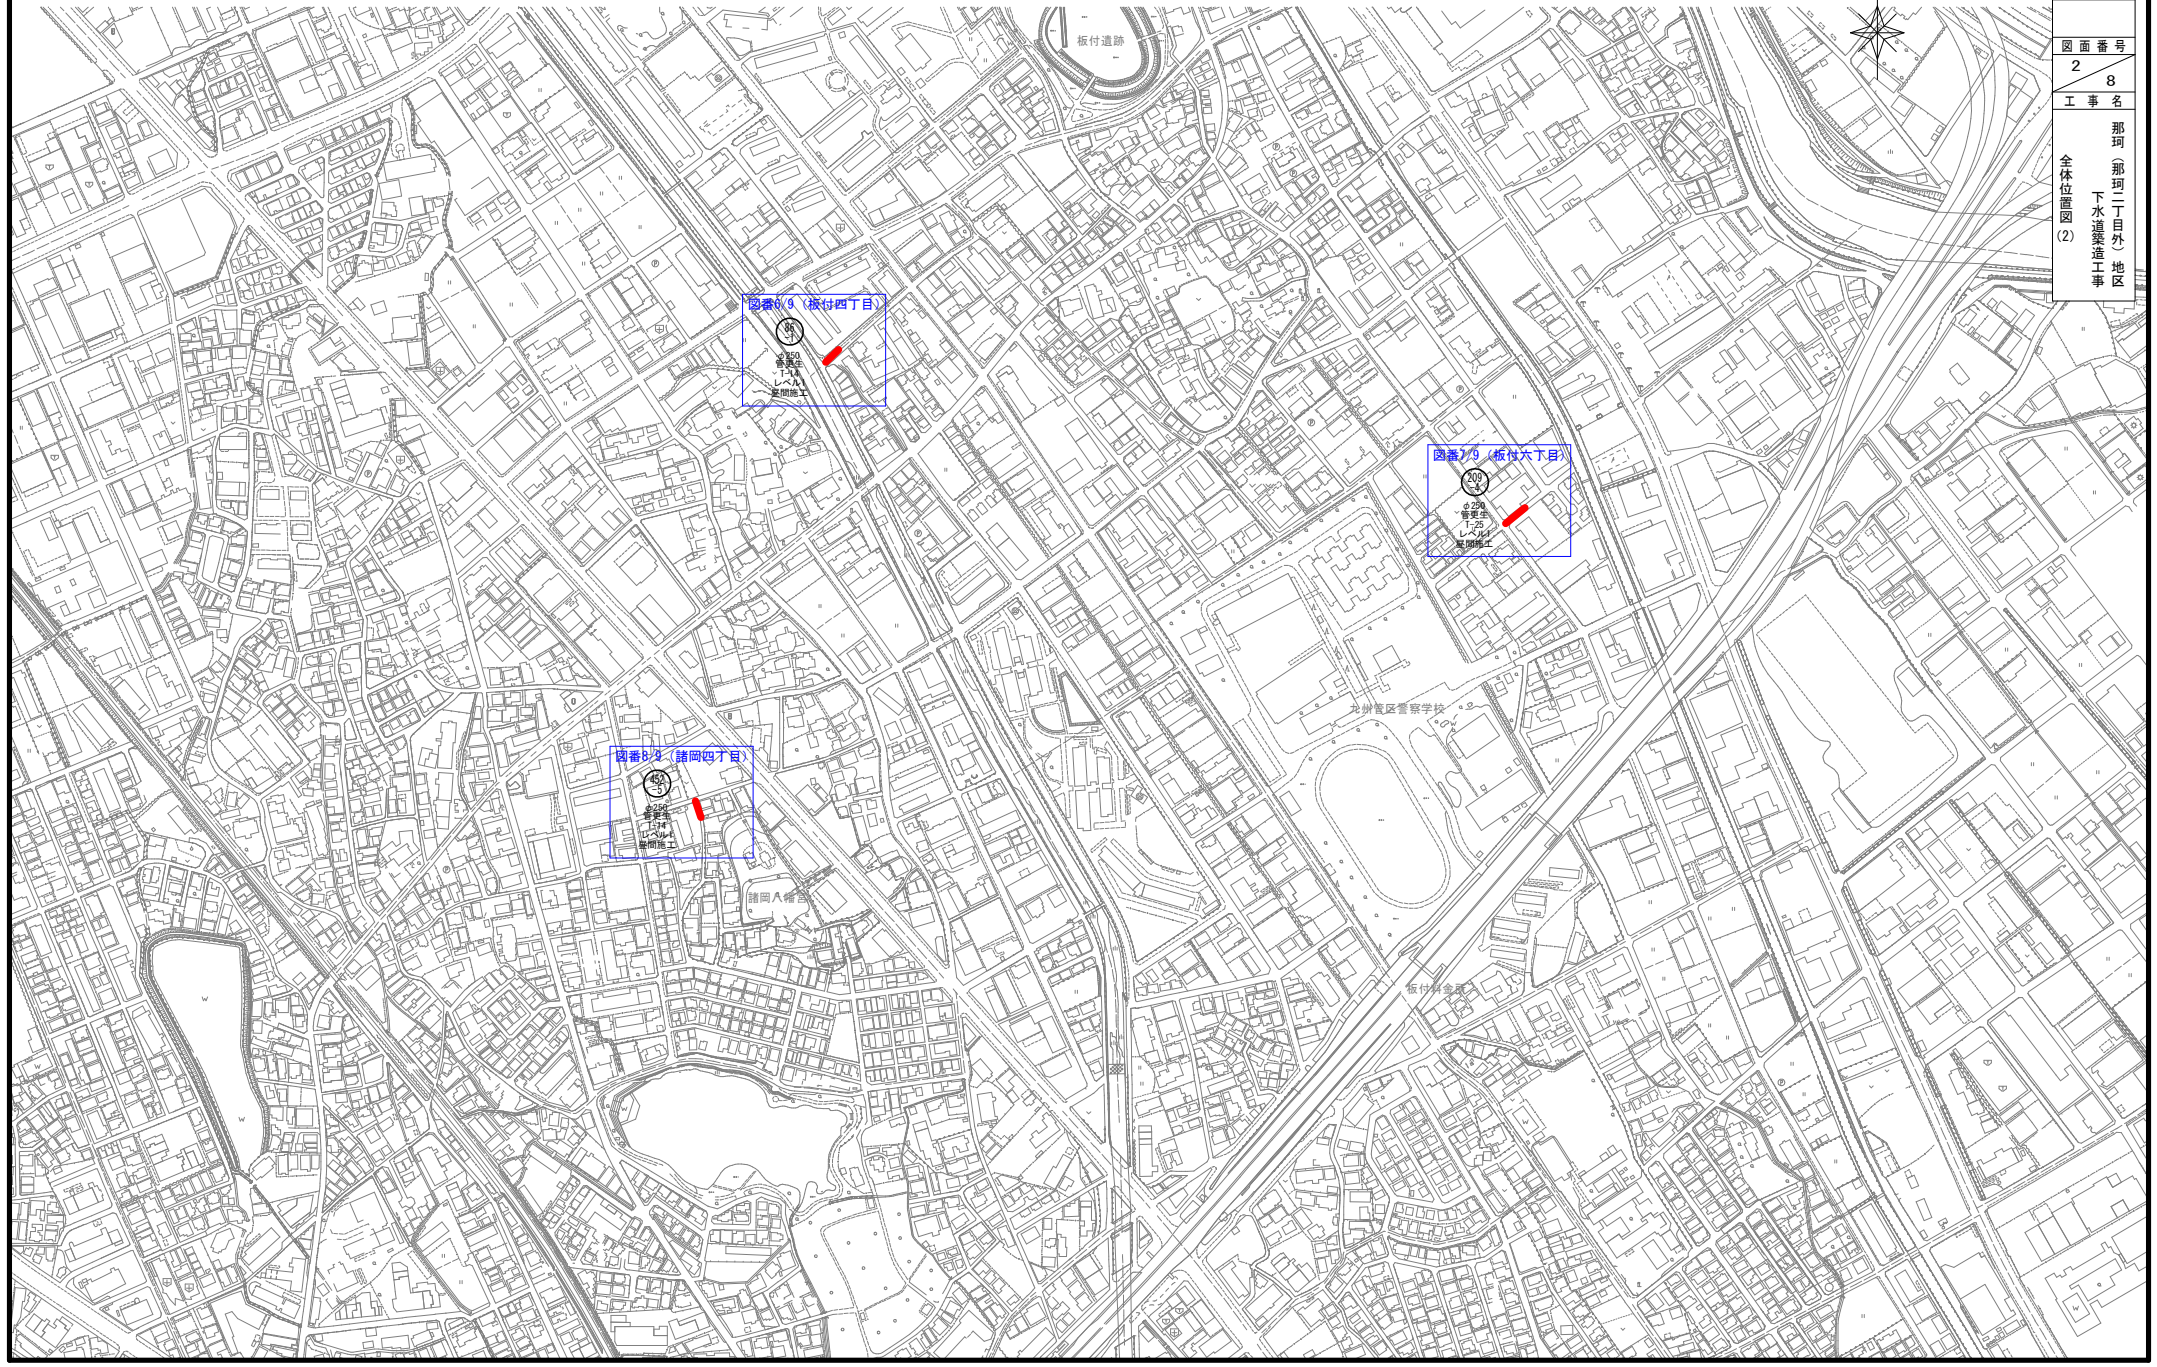

平面・縦断・横断図 (1)




V=1:100  
H=1:300

平面図 S=1:300 (A1)  
S=1:600 (A3)

縦断図 V=1:100 H=1:500 (A1)  
V=1:300 H=1:600 (A3)

横断図 S=1:100 (A1)  
S=1:200 (A3)

福岡市  
下水道  
設計番号  
図面番号  
3/8  
工事名  
那珂(那珂二丁目外)地区  
下水道工事  
平面・縦断・横断図  
(1)  
429-2  
(那珂二丁目)

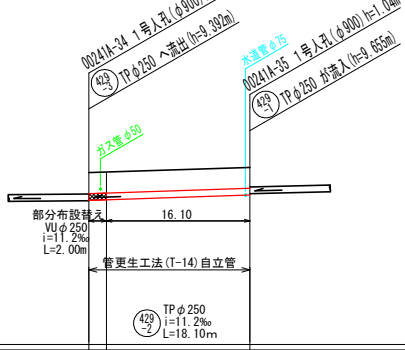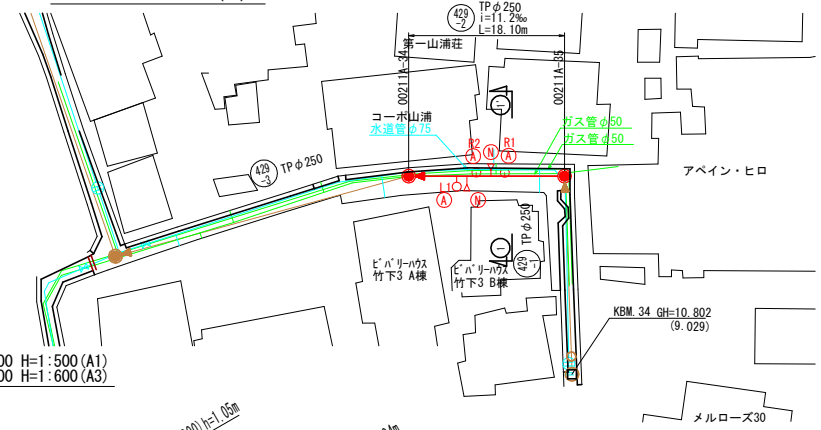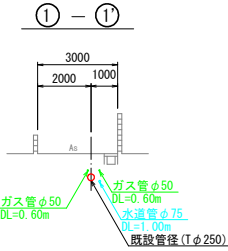

|           |                      |       |       |
|-----------|----------------------|-------|-------|
| 現況地盤高     | 10.44                | 10.46 | 10.64 |
| 土被り       | 0.76                 | 0.76  | 0.76  |
| 管底高       | 9.402                | 9.424 | 9.605 |
| 掘削深       | 1.20                 | 1.20  | 1.20  |
| 単距離       | 0.00                 | 2.00  | 16.10 |
| 追加距離      | 0.00                 | 2.00  | 18.10 |
| 管種        | 更生管                  |       |       |
| 既設管       | TP<br>1971年          |       |       |
| 基礎種別      |                      |       |       |
| 道路種別 (幅員) | 車道舗装 (As-A) (W=3.0m) |       |       |
| 埋戻し       | 再生砂 (A)              |       |       |
| 山留工       | 表掘り                  |       |       |
| 支保工       |                      |       |       |
| 雨水樹       | N=2                  |       |       |
| 汚水樹       | A=3                  |       |       |
| 路面覆工      |                      |       |       |

(更生管断面図)  
管径φ250



汚水・雨水樹布設替え一覧表

| 路線番号  | 樹番号 | 深さ     | 取付管    | 施工内容 |
|-------|-----|--------|--------|------|
| 429-2 | R1  | h=0.70 | L=0.40 | A    |
|       | —   | —      | L=1.00 | N    |
|       | R2  | h=0.68 | L=0.40 | A    |
|       | —   | —      | L=1.00 | N    |
|       | L1  | h=0.79 | L=0.40 | A    |

人孔修繕・取替一覧表

| 人孔番号      | 蓋替 | 荷重   | 足掛金物 | インバート | 転落防止安全梯子 |
|-----------|----|------|------|-------|----------|
| 00241A-35 | 1  | T-14 | —    | —     | 0        |
| 00241A-34 | 1  | T-14 | 1    | —     | 0        |


|         |     |
|---------|-----|
| 凡 例     |     |
| 下水マンホール |     |
| 特0号人孔   | —○— |
| 1号人孔    | ●   |
| 2号人孔    | ○   |
| 3号人孔    | ⊙   |
| 4号人孔    | ⊗   |
| 地下埋設物   |     |
| 設計対象路線  | —   |
| 汚水      | —   |
| 雨水      | —   |
| 再生水     | —   |
| 上水道     | —   |
| N T T   | —   |
| 電力      | —   |
| ガス (低圧) | —   |
| ガス (中圧) | —   |

|     |        |
|-----|--------|
| 凡 例 |        |
| —○  | 小口径汚水樹 |
| —○  | B型汚水樹  |
| —■  | 雨水樹    |
| —△  | 不明管    |


取付管施工内容

|   |                             |
|---|-----------------------------|
| A | 既設樹・取付管撤去 → 小口径汚水樹設置・取付管設置  |
| B | 既設樹・取付管撤去 → B型汚水樹設置・取付管設置   |
| C | 既設樹・取付管撤去 → M A型雨水樹設置・取付管設置 |
| D | 既設樹・取付管撤去 → M B型雨水樹設置・取付管設置 |
| E | 既設樹・取付管撤去 → 街渠樹設置・取付管設置     |
| F | 既設樹・取付管撤去 → 集水樹設置・取付管設置     |
| G | 既設樹蓋・取付管撤去 → 蓋替・取付管設置       |
| H | 既設樹撤去 → 小口径汚水樹設置            |
| I | 既設樹撤去 → B型汚水樹設置             |
| J | 既設樹蓋撤去 → 蓋替                 |
| K | 取付管撤去 → 取付管設置               |
| L | 取付管撤去 → 小口径汚水樹設置・取付管設置      |
| M | 既設樹・取付管撤去 (未使用管) → キャップ止    |
| N | 取付管撤去 (不明管) → キャップ止         |
| O | 現状維持                        |

平面図 A1用 : S=1:300  
A3用 : S=1:600

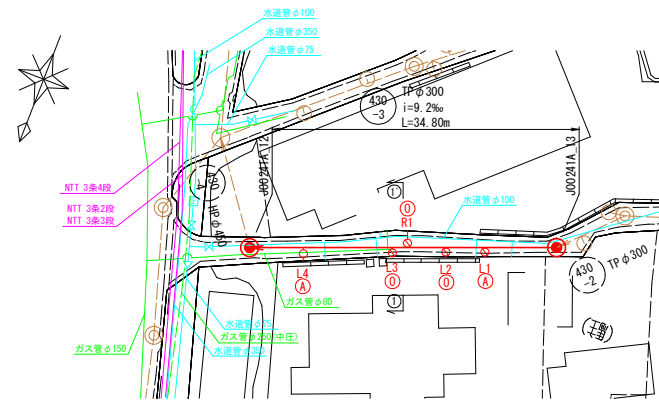



縦断図 A1用: V=1:100  
H=1:300  
A3用: V=1:200  
H=1:600

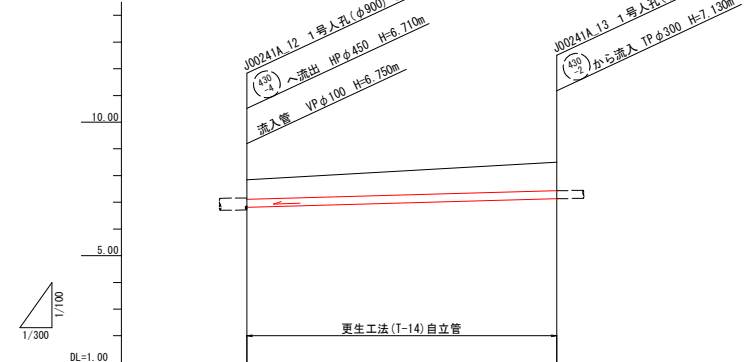

|          |                  |   |                  |
|----------|------------------|---|------------------|
| 路管勾配距離   |                  | <div> <div> <div>430</div> <div>3</div> </div> <div> TP φ300<br/> i=9.2‰<br/> L=34.80m </div> </div> |                  |
| 地盤高      | 7.84             |   | 8.50             |
| 土被り      | 0.70             |   | 1.04             |
| 管底高      | (6.710)<br>6.810 |   | (7.130)<br>7.130 |
| 掘削深      |                  |   |                  |
| 追加距離     | 0.00             |   | 34.80            |
| 新設管種     |                  | 更生管                                                                                                  |                  |
| 既設管種     |                  | TP 1971年度                                                                                            |                  |
| 基礎種別     |                  | —   |                  |
| 道路種別(幅員) |                  | 車道舗装 (As-A)                                                                                          |                  |
| 埋設法      |                  | —   |                  |
| 土留法      |                  | —   |                  |
| 支保工      |                  | —   |                  |
| 路面覆工     |                  | —   |                  |
| 雨水樹      |                  | —   |                  |
| 汚水樹      |                  | A=2.0~3                                                                                              |                  |

### 平面・縦断・横断図 (2)

横断図      A1用 : S=1:50  
                 A3用 : S=1:100

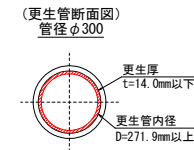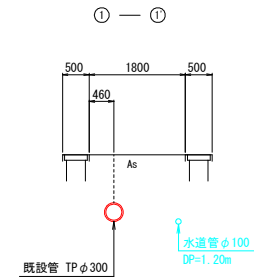

汚水・雨水桝布設替え一覧表

| 路線番号  | 柵番号 | 深さ     | 取付管    | 施工内容 |
|-------|-----|--------|--------|------|
| 430-3 | L1  | h=0.90 | L=1.40 | A    |
|       | L2  | h=0.77 | L=1.30 | 0    |
|       | R1  | h=0.87 | L=1.60 | 0    |
|       | L3  | h=0.75 | L=1.30 | 0    |
|       | L4  | h=0.84 | L=1.60 | A    |

人孔修繕・取替一覽表

| 人孔番号       | 蓋 替 | 荷 重  | 足掛金物 | インバート | 転落防止<br>安全梯子 |
|------------|-----|------|------|-------|--------------|
| J00241A_12 | 1   | T-14 | 1    | 0     | 0            |
| J00241A_13 | 1   | T-14 | 1    | 0     | 0            |

凡 例

| 下水マンホール   |                                                                                     |
|-----------|-------------------------------------------------------------------------------------|
| 特 1 号人孔   |  |
| 0 号人孔     |  |
| 1 号人孔     |  |
| 2 号人孔     |  |
| φ450      |  |
| 地下埋設物     |                                                                                     |
| 設計対象路線    |  |
| 汚 水       |  |
| 雨 水       |  |
| 再生水       |  |
| 上水道       |  |
| N T T     |  |
| 電 力       |  |
| ガス(低圧)    |  |
| ガス(中圧)    |  |
| 共同溝 (通信系) |  |


取付管凡例

|                                                                                       |                    |
|---------------------------------------------------------------------------------------|--------------------|
|  | 污水树 (小口径)          |
|  | 污水树 ( $\phi 450$ ) |
|  | 雨水树                |
|  | 不明管                |


| 取付管施工内容 |         |
|---------|---------|
| 1       | 取付管の取付け |
| 2       | 取付管の取付け |
| 3       | 取付管の取付け |
|   |                            |
|---|----------------------------|
| A | 既設樹、取付管撤去 → 小口径汚水樹設置、取付管設置 |
| B | 既設樹、取付管撤去 → B型汚水樹設置、取付管設置  |
| C | 既設樹、取付管撤去 → MA型雨水樹設置、取付管設置 |
| D | 既設樹、取付管撤去 → MB型雨水樹設置、取付管設置 |
| E | 既設樹、取付管撤去 → 街渠樹設置、取付管設置    |
| F | 既設樹、取付管撤去 → 集水樹設置、取付管設置    |
| G | 既設樹蓋、取付管撤去 → 蓋移、取付管設置      |
| H | 既設樹撤去 → 小口径汚水樹設置           |
| I | 既設樹撤去 → B型汚水樹設置            |
| J | 既設樹蓋撤去 → 蓋移                |
| K | 取付管撤去 → 取付管設置              |
| L | 取付管撤去 → 小口径汚水樹設置、取付管設置     |
| M | 既設樹、取付管撤去（未使用管） → キャップ止    |
| N | 取付管撤去（不明管） → キャップ止         |
| O | 現状維持                       |

平面図 A1用: S=1:300  
A3用: S=1:600

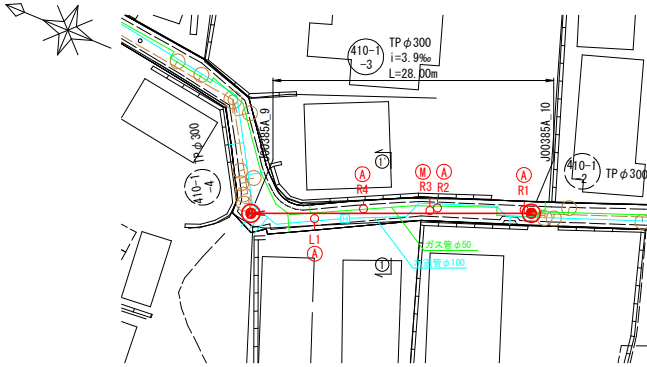


縦断面図 A1用: V=1:100  
H=1:300  
A3用: V=1:200  
H=1:600

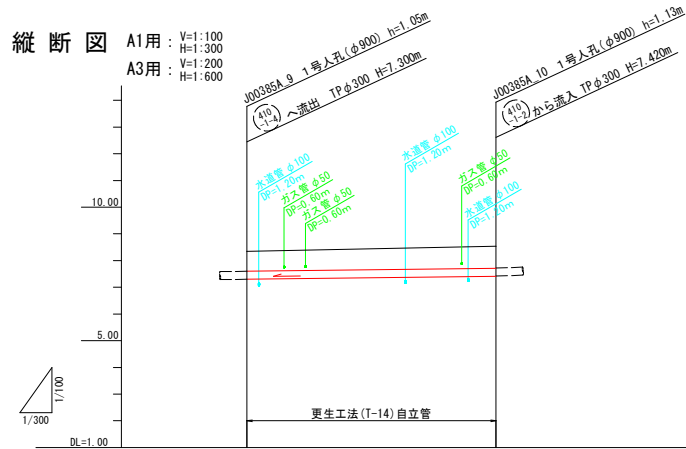


## 平面・縦断・横断図 (3)

横断面図 A1用: S=1:50  
A3用: S=1:100

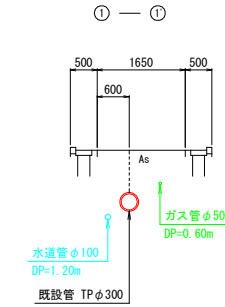

(更生管断面図)  
管径φ300

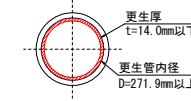

| 凡 例      |   |
|----------|---|
| 下水マンホール  |   |
| 特1号人孔    | □ |
| 0号人孔     | ○ |
| 1号人孔     | ● |
| 2号人孔     | ○ |
| φ450     | ○ |
| 地下埋設物    |   |
| 設計対象路線   | — |
| 汚 水      | — |
| 雨 水      | — |
| 再生水      | — |
| 上水道      | — |
| N T T    | — |
| 電 力      | — |
| ガス(低圧)   | — |
| ガス(中圧)   | — |
| 共同溝(通信系) | — |

取付管凡例

|     |           |
|-----|-----------|
| —○— | 汚水樹(小口径)  |
| —○— | 汚水樹(φ450) |
| —■— | 雨水樹       |
| —△— | 不明管       |

汚水・雨水樹布設替え一覧表

| 路線番号    | 樹番号 | 深さ     | 取付管    | 施工内容 |
|---------|-----|--------|--------|------|
| 410-1-3 | R1  | h=0.87 | L=1.30 | A    |
|         | R2  | h=0.83 | L=1.80 | A    |
|         | R3  | h=1.13 | L=1.90 | M    |
|         | R4  | h=0.83 | L=1.45 | A    |
|         | L1  | h=0.80 | L=1.60 | A    |


人孔修繕・取替一覧表

| 人孔番号       | 蓋 替 | 荷 重  | 足掛金物 | インバート | 転落防止安全梯子 |
|------------|-----|------|------|-------|----------|
| J00385A_9  | 1   | T-14 | 3    | 0     | 0        |
| J00385A_10 | 1   | T-14 | 3    | 0     | 0        |


取付管施工内容

|   |                             |
|---|-----------------------------|
| A | 既設樹・取付管撤去 → 小口径汚水樹設置・取付管設置  |
| B | 既設樹・取付管撤去 → B型汚水樹設置・取付管設置   |
| C | 既設樹・取付管撤去 → M A型雨水樹設置・取付管設置 |
| D | 既設樹・取付管撤去 → M B型雨水樹設置・取付管設置 |
| E | 既設樹・取付管撤去 → 街渠樹設置・取付管設置     |
| F | 既設樹・取付管撤去 → 集水樹設置・取付管設置     |
| G | 既設樹撤去 → 蓋替・取付管設置            |
| H | 既設樹撤去 → 小口径汚水樹設置            |
| I | 既設樹撤去 → B型汚水樹設置             |
| J | 既設樹撤去 → 蓋替                  |
| K | 取付管撤去 → 取付管設置               |
| L | 取付管撤去 → 小口径汚水樹設置・取付管設置      |
| M | 既設樹・取付管撤去(未使用管) → キャップ止     |
| N | 取付管撤去(不明管) → キャップ止          |
| O | 現状維持                        |

平面図 A1用: S=1:300  
A3用: S=1:600

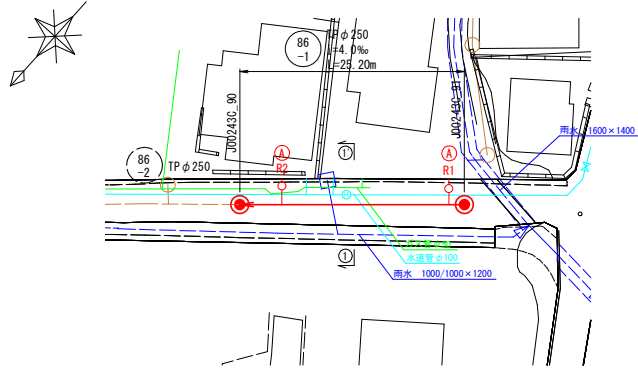


縦断面図 A1用: V=1:100  
H=1:300  
A3用: V=1:200  
H=1:600

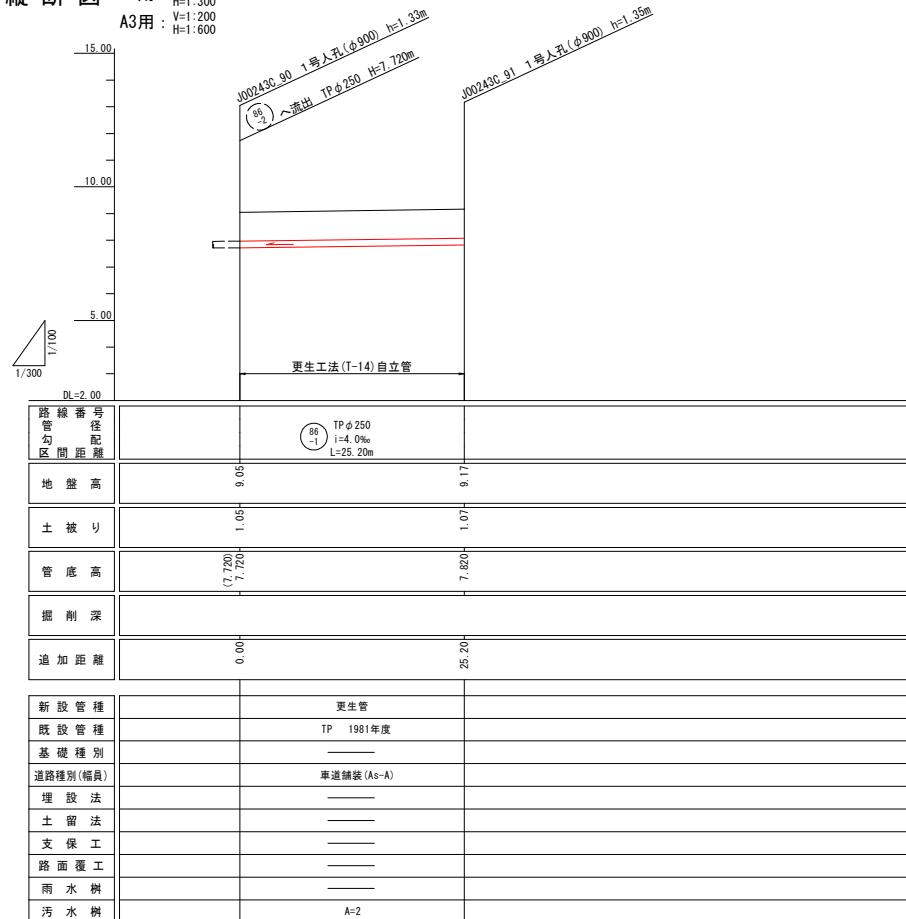


## 平面・縦断・横断図(4)

横断面図 A1用: S=1:50  
A3用: S=1:100

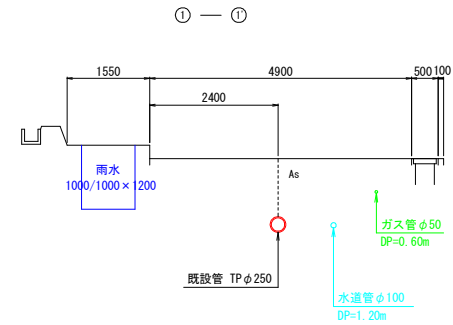

(更生管断面図)  
管径φ250

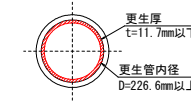

| 凡 例      |   |
|----------|---|
| 下水マンホール  |   |
| 特1号人孔    | □ |
| 0号人孔     | ○ |
| 1号人孔     | ● |
| 2号人孔     | ○ |
| φ450     | ○ |
| 地下埋設物    |   |
| 設計対象路線   | — |
| 汚 水      | — |
| 雨 水      | — |
| 再生水      | — |
| 上水道      | — |
| N T T    | — |
| 電 力      | — |
| ガス(低圧)   | — |
| ガス(中圧)   | — |
| 共同溝(通信系) | — |

取付管凡例

|    |           |
|----|-----------|
| —○ | 汚水樹(小口径)  |
| —○ | 汚水樹(φ450) |
| —■ | 雨水樹       |
| —△ | 不明管       |

汚水・雨水樹布設替え一覧表

| 路線番号 | 樹番号 | 深さ     | 取付管    | 施工内容 |
|------|-----|--------|--------|------|
| 86-1 | R1  | h=1.10 | L=2.80 | A    |
|      | R2  | h=1.06 | L=3.10 | A    |


人孔修繕・取替一覧表

| 人孔番号       | 蓋 替 | 荷 重  | 足掛金物 | インバート | 転落防止<br>安全梯子 |
|------------|-----|------|------|-------|--------------|
| J00243C_90 | 1   | T-14 | 3    | 0     | 0            |
| J00243C_91 | 1   | T-14 | 3    | 1     | 0            |


取付管施工内容

|   |                            |
|---|----------------------------|
| A | 既設樹・取付管撤去 → 小口径汚水樹設置・取付管設置 |
| B | 既設樹・取付管撤去 → B型汚水樹設置・取付管設置  |
| C | 既設樹・取付管撤去 → MA型雨水樹設置・取付管設置 |
| D | 既設樹・取付管撤去 → MB型雨水樹設置・取付管設置 |
| E | 既設樹・取付管撤去 → 街渠樹設置・取付管設置    |
| F | 既設樹・取付管撤去 → 集水樹設置・取付管設置    |
| G | 既設樹撤去 → 蓋替・取付管設置           |
| H | 既設樹撤去 → 小口径汚水樹設置           |
| I | 既設樹撤去 → B型汚水樹設置            |
| J | 既設樹撤去 → 蓋替                 |
| K | 取付管撤去 → 取付管設置              |
| L | 取付管撤去 → 小口径汚水樹設置・取付管設置     |
| M | 既設樹・取付管撤去(未使用管) → キャップ止    |
| N | 取付管撤去(不明管) → キャップ止         |
| O | 現状維持                       |

平面図 A1用: S=1:300  
A3用: S=1:600

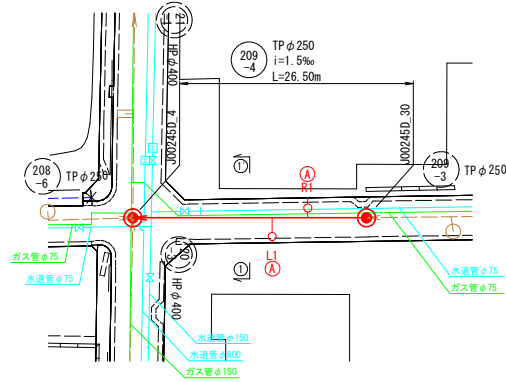


縦断面図 A1用: V=1:100  
H=1:300  
A3用: V=1:200  
H=1:600

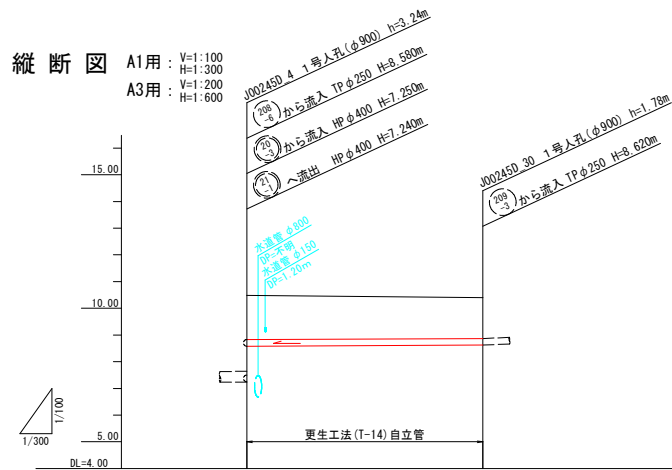


## 平面・縦断・横断図 (5)

横断図

A1用: S=1:50  
A3用: S=1:100

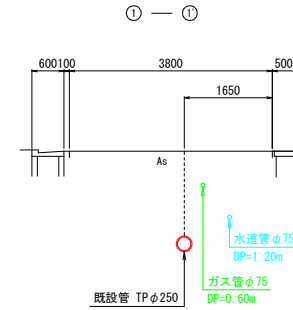

(更生管断面図)  
管径φ250

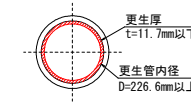

凡 例

| 下水マンホール  |   |
|----------|---|
| 特1号人孔    | □ |
| 0号人孔     | ○ |
| 1号人孔     | ● |
| 2号人孔     | ○ |
| φ450     | ○ |
| 地下埋設物    |   |
| 設計対象路線   | — |
| 汚 水      | — |
| 雨 水      | — |
| 再生水      | — |
| 上水道      | — |
| N T T    | — |
| 電 力      | — |
| ガス(低圧)   | — |
| ガス(中圧)   | — |
| 共同溝(通信系) | — |

取付管凡例

|     |            |
|-----|------------|
| —○— | 汚水樹 (小口径)  |
| —○— | 汚水樹 (φ450) |
| —■— | 雨水樹        |
| —△— | 不明管        |

汚水・雨水樹布設替え一覧表

| 路線番号  | 樹番号 | 深さ     | 取付管    | 施工内容 |
|-------|-----|--------|--------|------|
| 209-4 | R1  | h=1.05 | L=2.00 | A    |
|       | L1  | h=1.05 | L=3.00 | A    |

人孔修繕・取替一覧表

| 人孔番号       | 蓋 替 | 荷 重  | 足掛金物 | インバート | 転落防止安全梯子 |
|------------|-----|------|------|-------|----------|
| J002450_4  | 1   | T-14 | 7    | 0     | 1        |
| J002450_30 | 1   | T-14 | 0    | 0     | 0        |


取付管施工内容

|   |                             |
|---|-----------------------------|
| A | 既設樹・取付管撤去 → 小口径汚水樹設置・取付管設置  |
| B | 既設樹・取付管撤去 → B型汚水樹設置・取付管設置   |
| C | 既設樹・取付管撤去 → M A型雨水樹設置・取付管設置 |
| D | 既設樹・取付管撤去 → M B型雨水樹設置・取付管設置 |
| E | 既設樹・取付管撤去 → 街渠樹設置・取付管設置     |
| F | 既設樹・取付管撤去 → 集水樹設置・取付管設置     |
| G | 既設樹撤去 → 蓋替・取付管設置            |
| H | 既設樹撤去 → 小口径汚水樹設置            |
| I | 既設樹撤去 → B型汚水樹設置             |
| J | 既設樹撤去 → 蓋替                  |
| K | 取付管撤去 → 取付管設置               |
| L | 取付管撤去 → 小口径汚水樹設置・取付管設置      |
| M | 既設樹・取付管撤去 (未使用管) → キャップ止    |
| N | 取付管撤去 (不明管) → キャップ止         |
| O | 現状維持                        |


|                |
|----------------|
| 福岡市            |
| 下水道            |
| 設計番号           |
| 図面番号           |
| 7 / 8          |
| 工事名            |
| 那珂 (那珂二丁目外) 地区 |
| 平面・縦断・横断図 (5)  |
| 下水道築造工事        |

209-4  
(板付六丁目)

平面図 A1用: S=1:300  
A3用: S=1:600

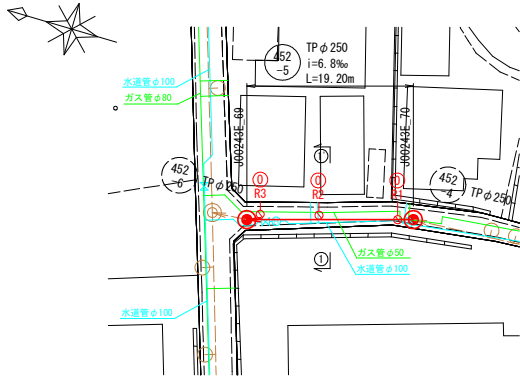


縦断面図 A1用: V=1:100  
A3用: V=1:200  
H=1:300  
H=1:600

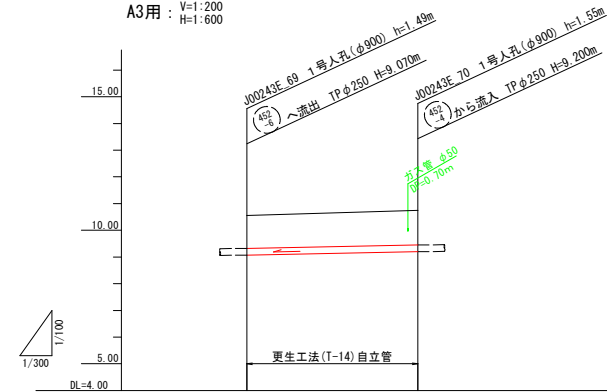


## 平面・縦断・横断図 (6)

横断図 A1用: S=1:50  
A3用: S=1:100

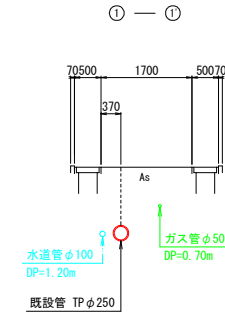

(更生管断面図)  
管径φ250

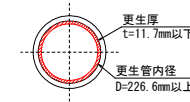

凡 例

| 下水マンホール  |       |
|----------|-------|
| 特1号人孔    | —[□]— |
| 0号人孔     | —(○)— |
| 1号人孔     | —(●)— |
| 2号人孔     | —(○)— |
| φ450     | —(○)— |
| 地下埋設物    |       |
| 設計対象路線   | —[—]— |
| 汚 水      | —[—]— |
| 雨 水      | —[—]— |
| 再生水      | —[—]— |
| 上水道      | —[—]— |
| N T T    | —[—]— |
| 電 力      | —[—]— |
| ガス(低圧)   | —[—]— |
| ガス(中圧)   | —[—]— |
| 共同溝(通信系) | —[—]— |

取付管凡例

|     |            |
|-----|------------|
| —○— | 汚水樹 (小口径)  |
| —○— | 汚水樹 (φ450) |
| —■— | 雨水樹        |
| —△— | 不明管        |

汚水・雨水樹布設替え一覧表

| 路線番号  | 樹番号 | 深さ     | 取付管    | 施工内容 |
|-------|-----|--------|--------|------|
| 452-5 | R1  | h=1.05 | L=1.20 | 0    |
|       | R2  | h=1.01 | L=1.40 | 0    |
|       | R3  | h=1.05 | L=1.60 | 0    |

取付管施工内容

|   |                             |
|---|-----------------------------|
| A | 既設樹・取付管撤去 → 小口径汚水樹設置・取付管設置  |
| B | 既設樹・取付管撤去 → B型汚水樹設置・取付管設置   |
| C | 既設樹・取付管撤去 → M A型雨水樹設置・取付管設置 |
| D | 既設樹・取付管撤去 → M B型雨水樹設置・取付管設置 |
| E | 既設樹・取付管撤去 → 街渠樹設置・取付管設置     |
| F | 既設樹・取付管撤去 → 集水樹設置・取付管設置     |
| G | 既設樹撤去 → 蓋替・取付管設置            |
| H | 既設樹撤去 → 小口径汚水樹設置            |
| I | 既設樹撤去 → B型汚水樹設置             |
| J | 既設樹撤去 → 蓋替                  |
| K | 取付管撤去 → 取付管設置               |
| L | 取付管撤去 → 小口径汚水樹設置・取付管設置      |
| M | 既設樹・取付管撤去 (未使用管) → キャップ止    |
| N | 取付管撤去 (不明管) → キャップ止         |
| O | 現状維持                        |

人孔修繕・取替一覧表

| 人孔番号       | 蓋 替 | 荷 重  | 足掛金物 | インバート | 転落防止安全梯子 |
|------------|-----|------|------|-------|----------|
| J00243E_69 | 1   | T-14 | 0    | 1     | 0        |
| J00243E_70 | 1   | T-14 | 0    | 1     | 0        |