

千歳川大橋(下り線) P15-P18 プレキャスト壁高欄詳細図(28)



S=1:25

[中分側 R-48-M0-SP]

(P16-P17径間 製作数 : 1)

断面図


1 - 1

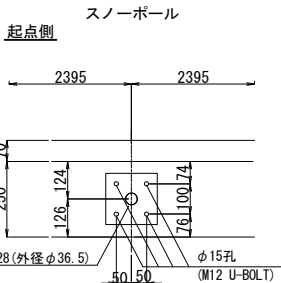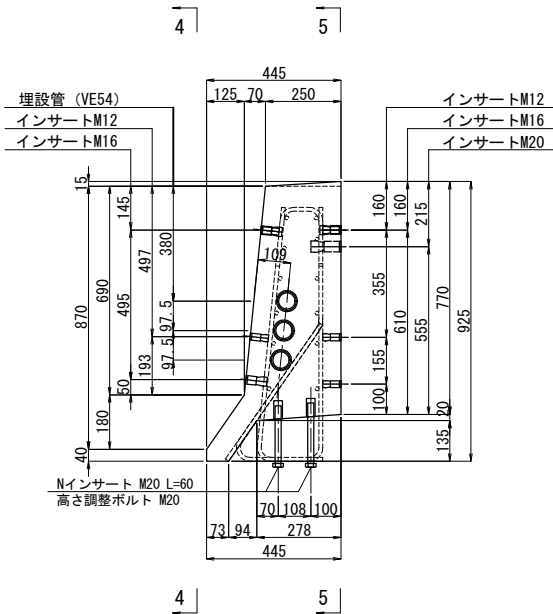

起点側


インサート配置側面図

4 - 4

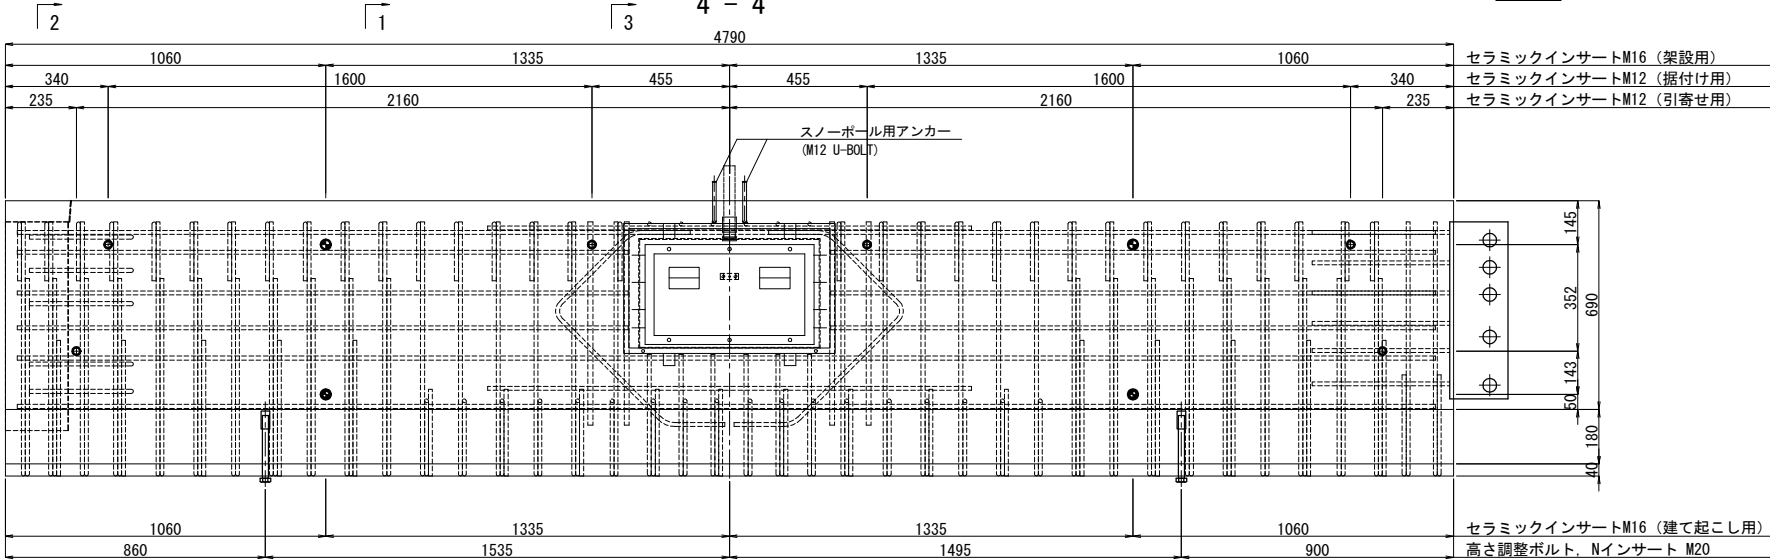


終点側


2 - 2

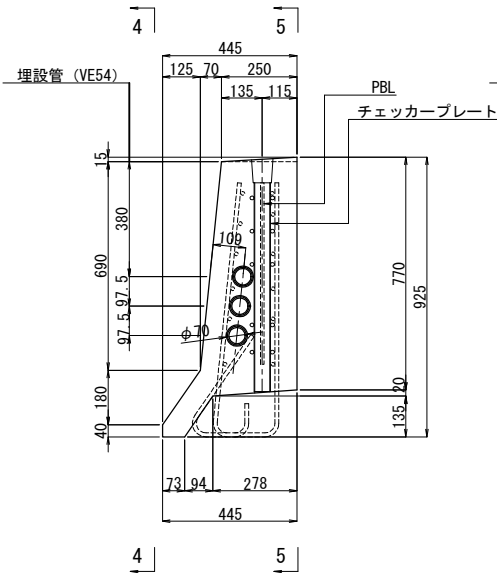

3 - 3

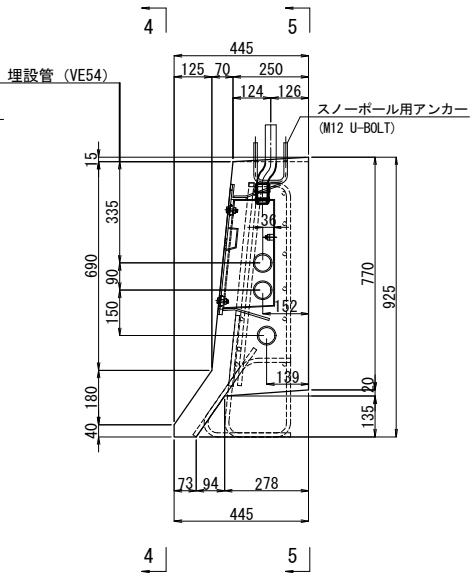

5 - 5

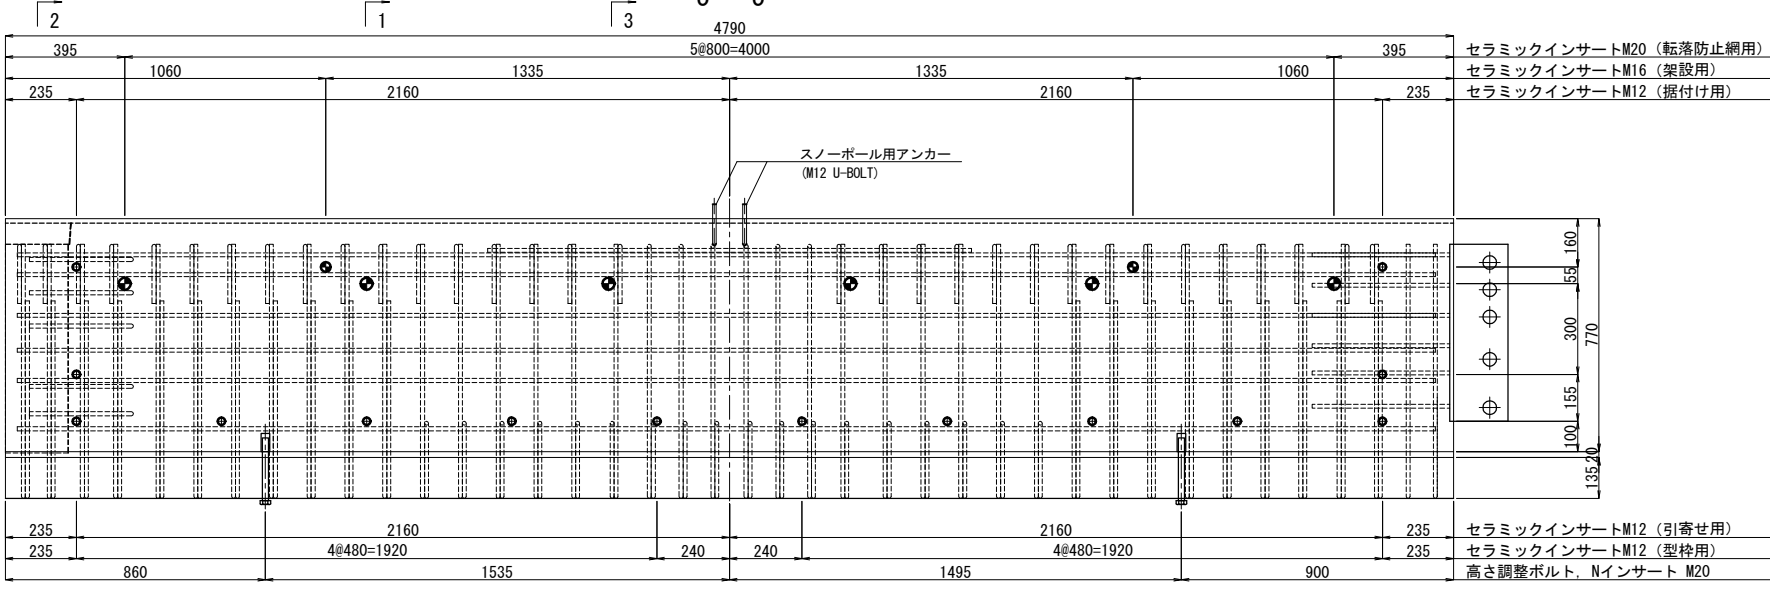


鉄筋表(1ブロック当り)

鉄筋番号	材質	長さ (mm)	本数 (本)	単位重量 (kg/m)	1本当り質量 (kg)	質量 (kg)	備考
H1	D13	1840	34	0.995	1.831	62	EP塗装
H2	D13	490	32	0.995	0.488	16	EP塗装
H3	D13	1010	20	0.995	1.005	20	EP塗装
H4	D13	620	2	0.995	0.617	1	EP塗装
H5	D13	550	10	0.995	0.547	5	EP塗装
H6	D13	350	9	0.995	0.348	3	EP塗装
H7	D13	4690	9	0.995	4.667	42	
H8	D13	2000	6	0.995	1.990	12	
H9	D13	1510	6	0.995	1.502	9	EP塗装
H10	D13	700	18	0.995	0.697	13	EP塗装
H11	D16	680	4	1.56	1.061	4	EP塗装
H12	D13	1600	2	0.995	1.592	3	
H13	D13	1270	2	0.995	1.264	3	
合 計						193	kg
鉄筋質量集計 (SD345)							
				普通鉄筋	塗装鉄筋		
				D16	0 kg	4 kg	4 kg
				D13	60 kg	129 kg	189 kg
合計				60 kg	133 kg	193 kg	

起点側

埋設管配置側面図

4 - 4

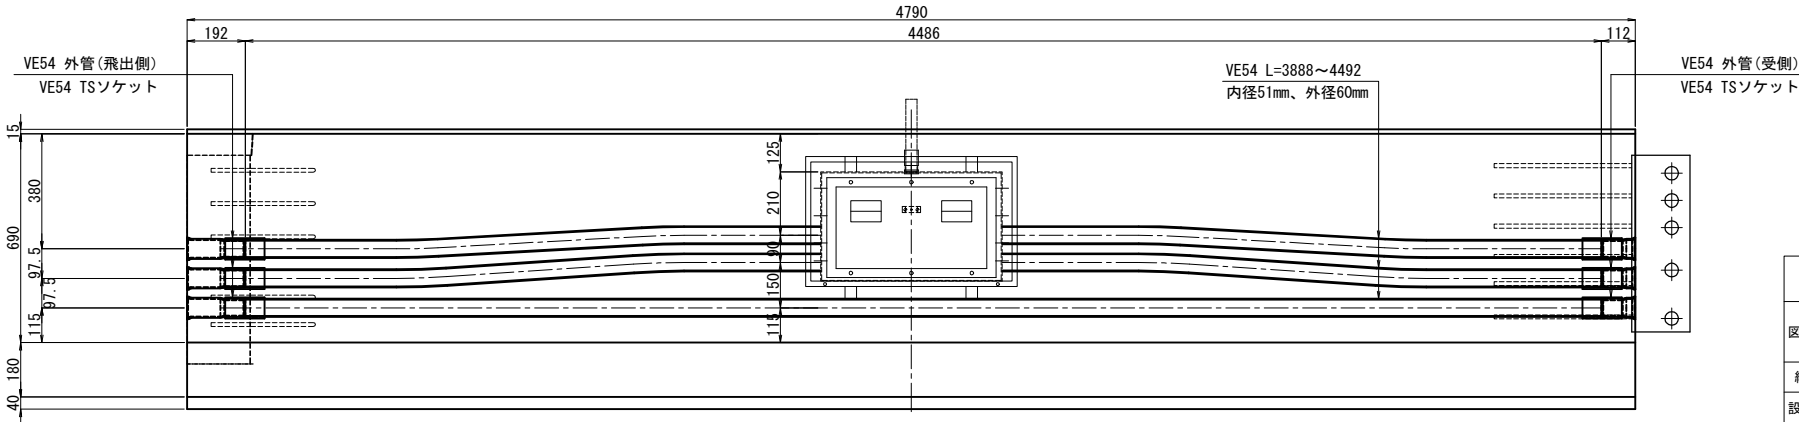

終点側




道央自動車道 千歳川大橋(下り線) 床版取替工事			
図面の種類	千歳川大橋(下り線) P15-P18 プレキャスト壁高欄詳細図(28)		
縮 尺	図 示	図面番号	/
設計会社名	戸田建設株式会社		
施工会社名	戸田建設株式会社		
事務所名	東日本高速道路株式会社 北海道支社 札幌管理事務所		

S=1 : 25

(P15-P16径間 製作数 : 1)



※ インサートおよび埋設管などの詳細位置は、壁高欄詳細図(30)を参照のこと。

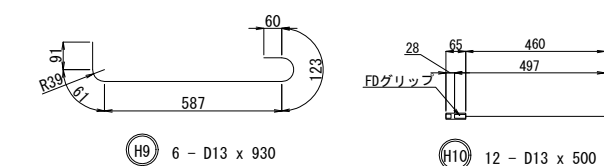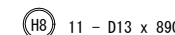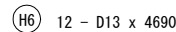

鉄筋番号	材質	長さ (mm)	本数 (本)	単位重量 (kg/m)	1本当り質量 (kg)	質量 (kg)	備考
H1	D13	1840	34	0.995	1.831	62	EP塗装
H2	D13	490	34	0.995	0.488	17	EP塗装
H3	D13	1010	29	0.995	1.005	29	EP塗装
H4	D13	550	14	0.995	0.547	8	EP塗装
H5	D13	350	5	0.995	0.348	2	EP塗装
H6	D13	4690	12	0.995	4.667	56	
H7	D13	1640	6	0.995	1.632	10	EP塗装
H8	D13	890	11	0.995	0.886	10	EP塗装
H9	D13	930	6	0.995	0.925	6	EP塗装
H10	D13	500	12	0.995	0.498	6	EP塗装
合 計						206	kg
鉄筋質量集計 (SD345)							
				普通鉄筋	塗装鉄筋		
D13				56 kg	150 kg	206 kg	
合計				56 kg	150 kg	206 kg	
機械式継手 D13						12	組

道失自動車道 千歳川大橋(下り線) 床版取替工事			
図面の種類	千歳川大橋(下り線) P15-P18 プレキャスト壁高欄詳細図(29)		
縮 尺	図 示	図面番号	/
設計会社名	戸田建設株式会社		
施工会社名	戸田建設株式会社		
事務所名	東日本高速道路株式会社 北海道支社 札幌管理事務所		

千歳川大橋(下り線) P15-P18 プレキャスト壁高欄詳細図(30)


S=1:25

[中分側 R-48-J0-PB]

(P15-P16径間 製作数 : 1)


断面図

1 - 1

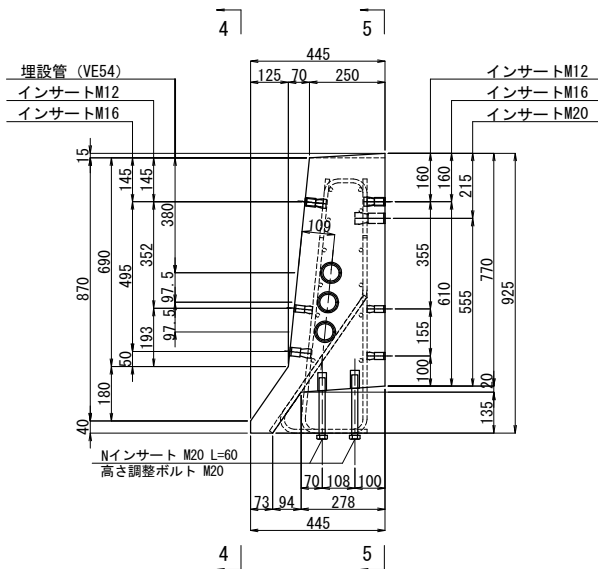


断面図

2 - 2

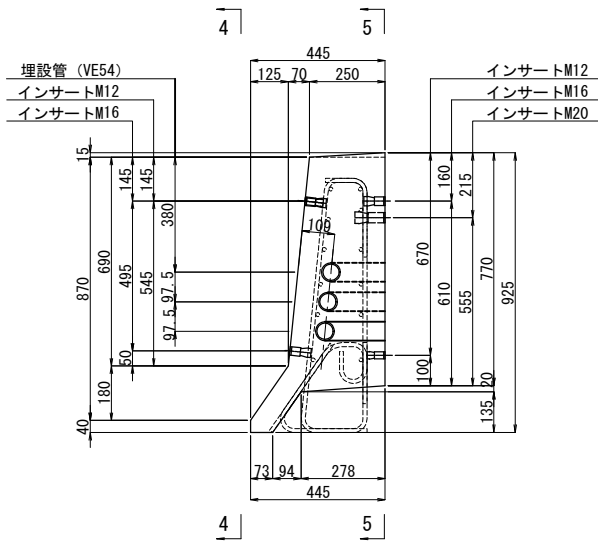


断面図

3 - 3

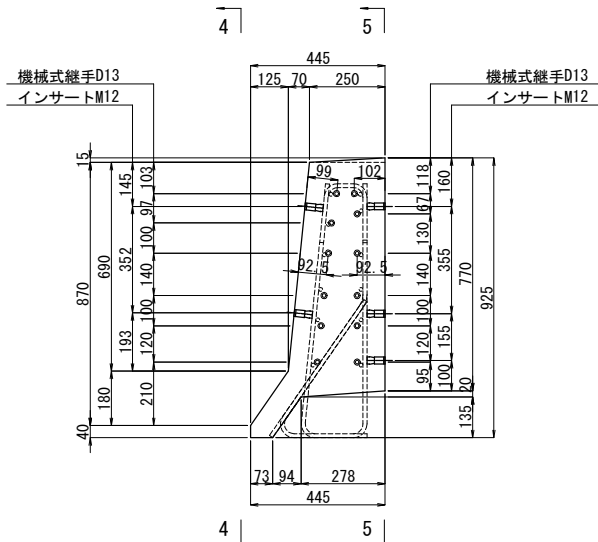


インサート配置側面図

4 - 4

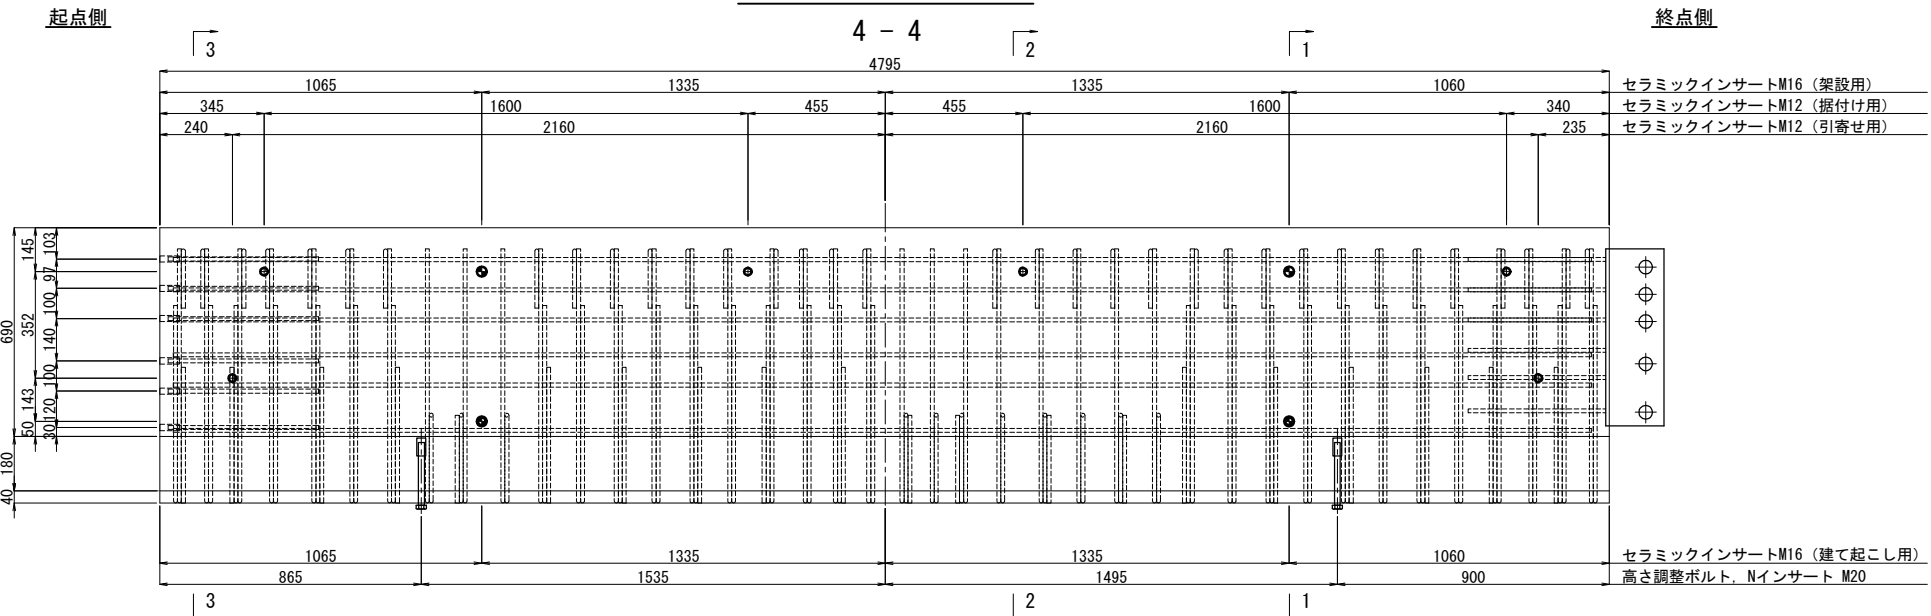


5 - 5

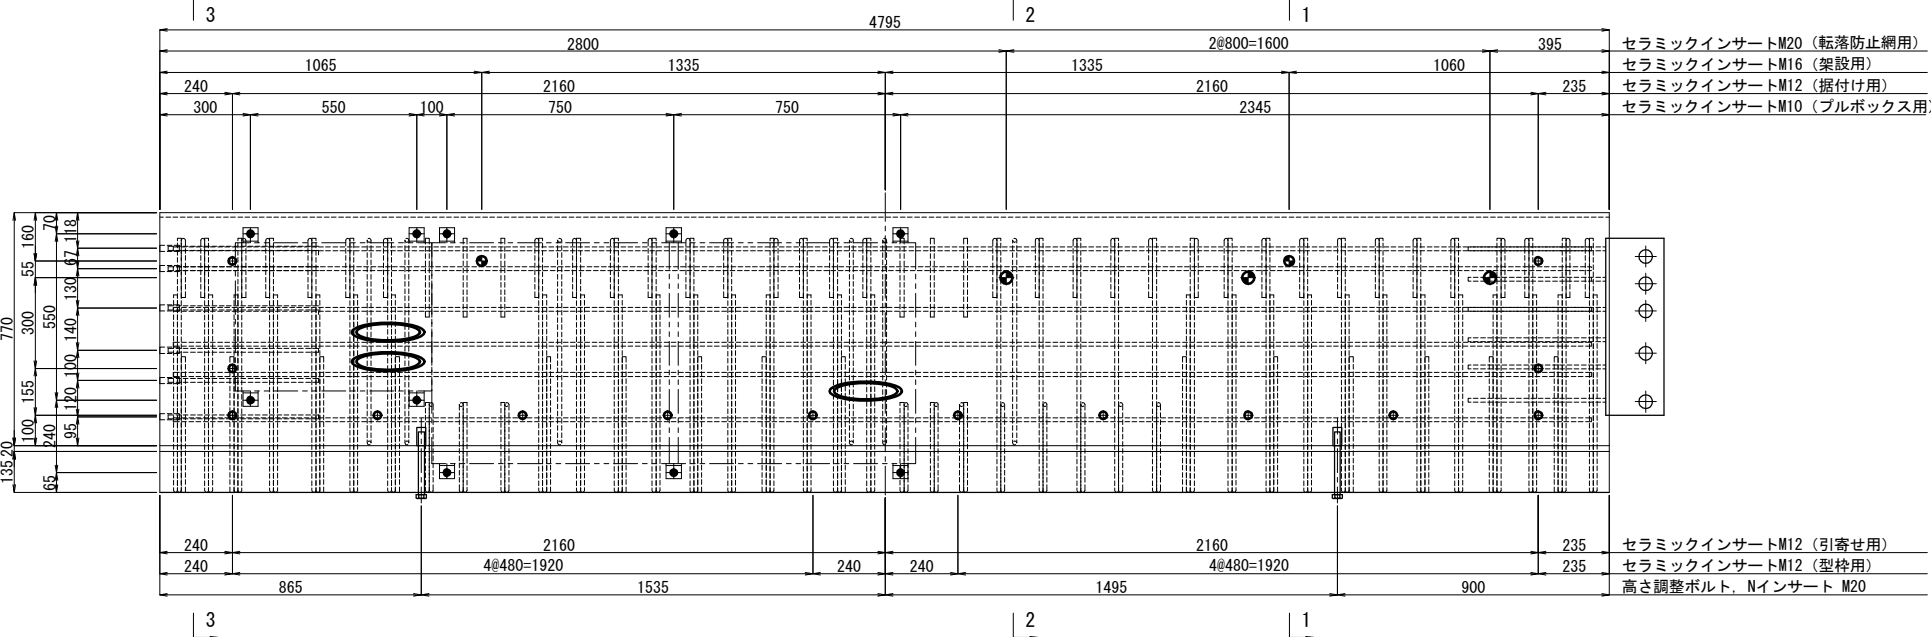

埋設管配置側面図

5 - 5

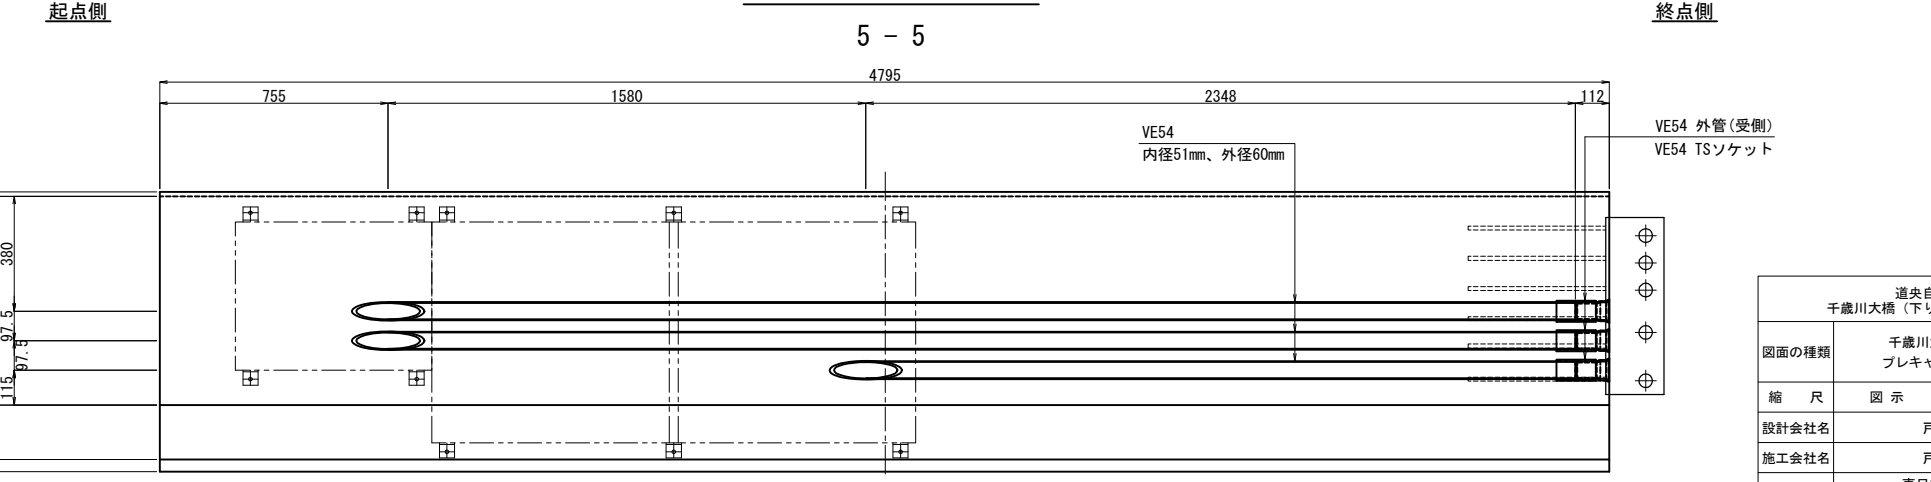

道央自動車道 千歳川大橋(下り線) 床版取替工事			
図面の種類	千歳川大橋(下り線) P15-P18 プレキャスト壁高欄詳細図(30)		
縮 尺	図 示	図面番号	/
設計会社名	戸田建設株式会社		
施工会社名	戸田建設株式会社		
事務所名	東日本高速道路株式会社 北海道支社 札幌管理事務所		

S=1:25

道央自動車道 千歳川大橋（下り線）床版取替工事			
図面の種類	千歳川大橋（下り線）P15-P18 フレキャスト壁高欄詳細図(31)		
縮 尺	図 示	図面番号	/
設計会社名	戸田建設株式会社		
施工会社名	戸田建設株式会社		
事務所名	東日本高速道路株式会社 北海道支社 札幌管理事務所		

千歳川大橋(下り線) P15-P18 プレキャスト壁高欄詳細図(32)


S=1:25

[中分側 R-E1-MJ-PB]


(P17-P18径間 製作数 : 1)

断面図


1 - 1

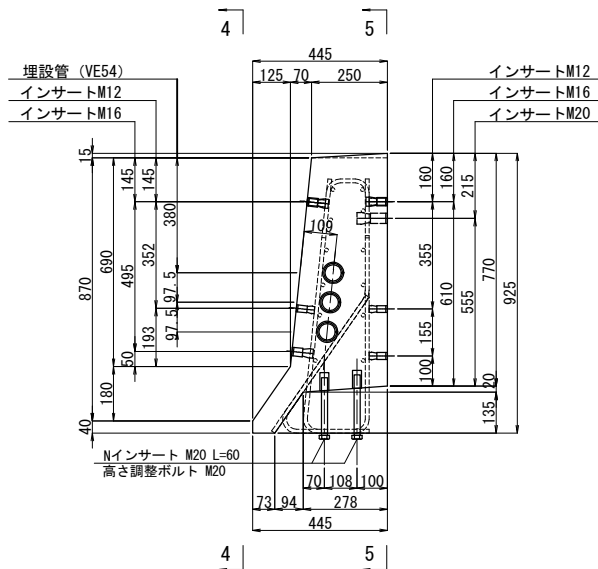

2 - 2

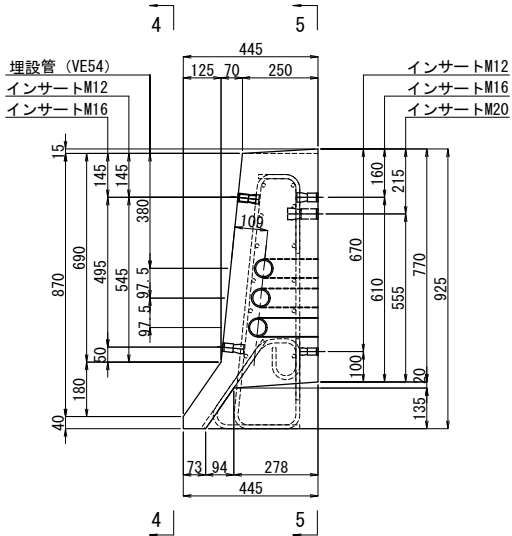


3 - 3

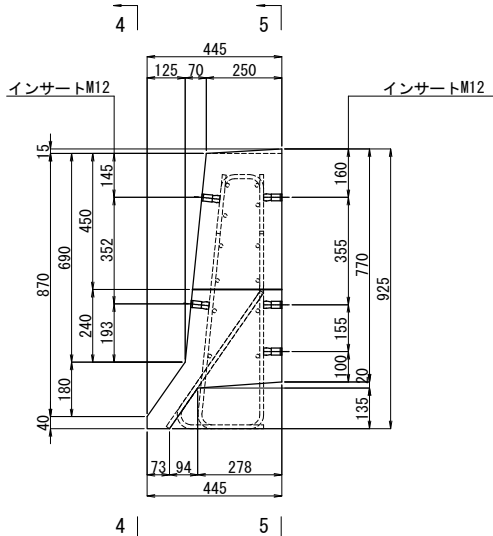


インサート配置側面図

4 - 4

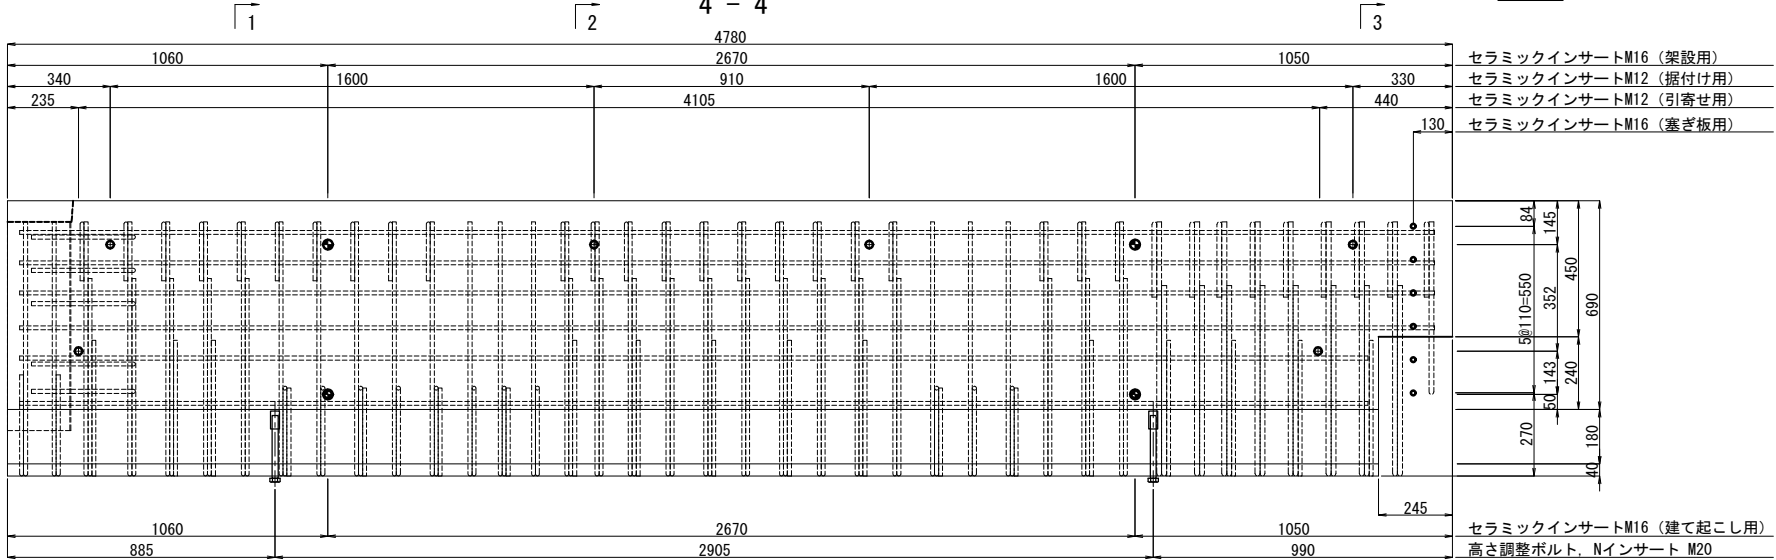

5 - 5

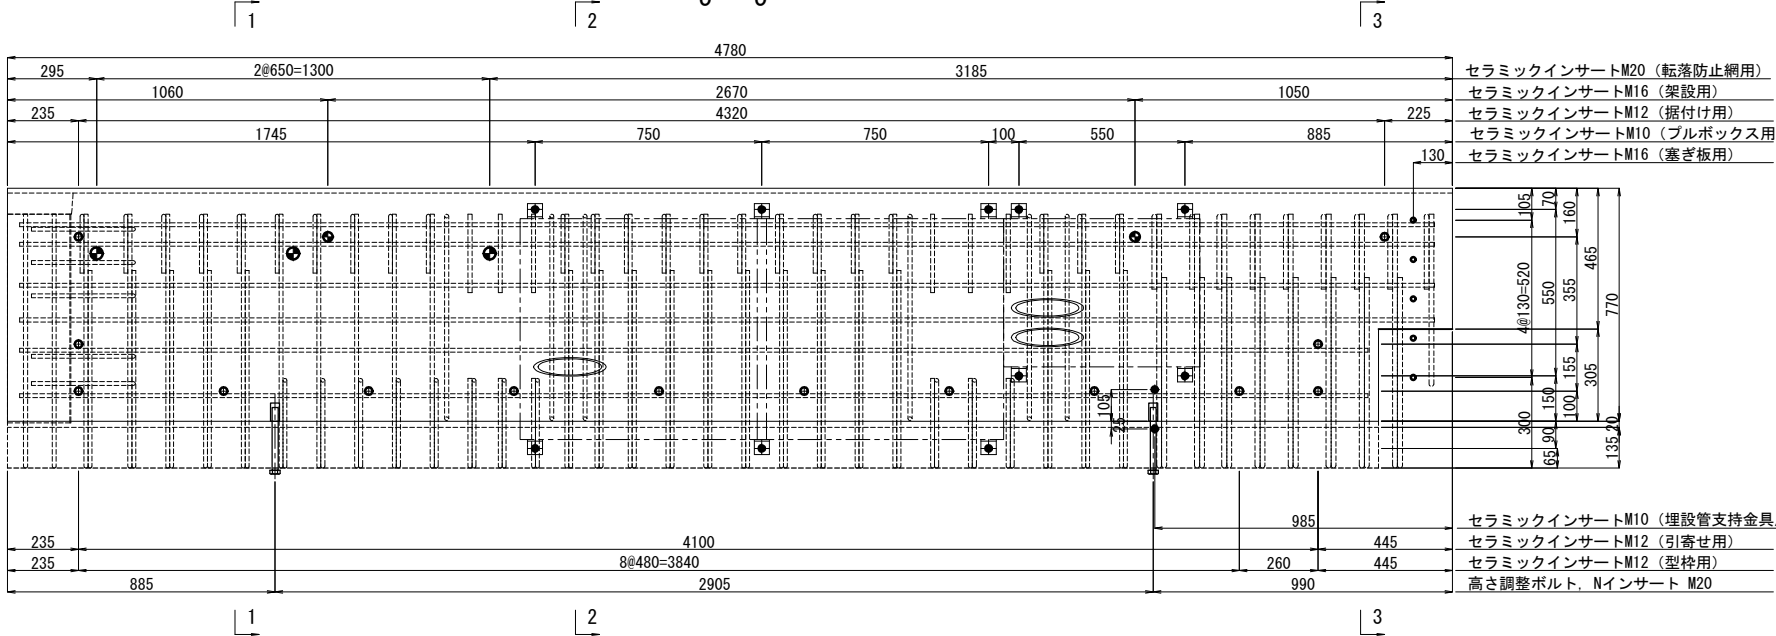


鉄筋表(1ブロック当り)

鉄筋番号	材質	長さ (mm)	本数 (本)	単位重量 (kg/m)	1本当り質量 (kg)	質量 (kg)	備考
H1	D13	1840	25	0.995	1.831	46	EP塗装
H2	D13	490	23	0.995	0.488	11	EP塗装
H3	D13	1010	18	0.995	1.005	18	EP塗装
H4	D13	620	2	0.995	0.617	1	EP塗装
H5	D16	1840	8	1.56	2.870	23	EP塗装
H6	D16	570	9	1.56	0.889	8	EP塗装
H7	D16	990	8	1.56	1.544	12	EP塗装
H8	D13	550	13	0.995	0.547	7	EP塗装
H9	D13	350	6	0.995	0.348	2	EP塗装
H10	D13	4570	12	0.995	4.547	55	
H11	D13	1640	6	0.995	1.632	10	EP塗装
H12	D13	890	11	0.995	0.886	10	EP塗装
H13	D13	930	6	0.995	0.925	6	EP塗装
H14	D16	1300	1	1.56	2.028	2	EP塗装
合 計						211	kg
鉄筋質量集計(SD345)				普通鉄筋	塗装鉄筋		
				D16	0 kg	45 kg	45 kg
				D13	55 kg	111 kg	166 kg
				合計	55 kg	156 kg	211 kg

埋設管配置側面図

5 - 5

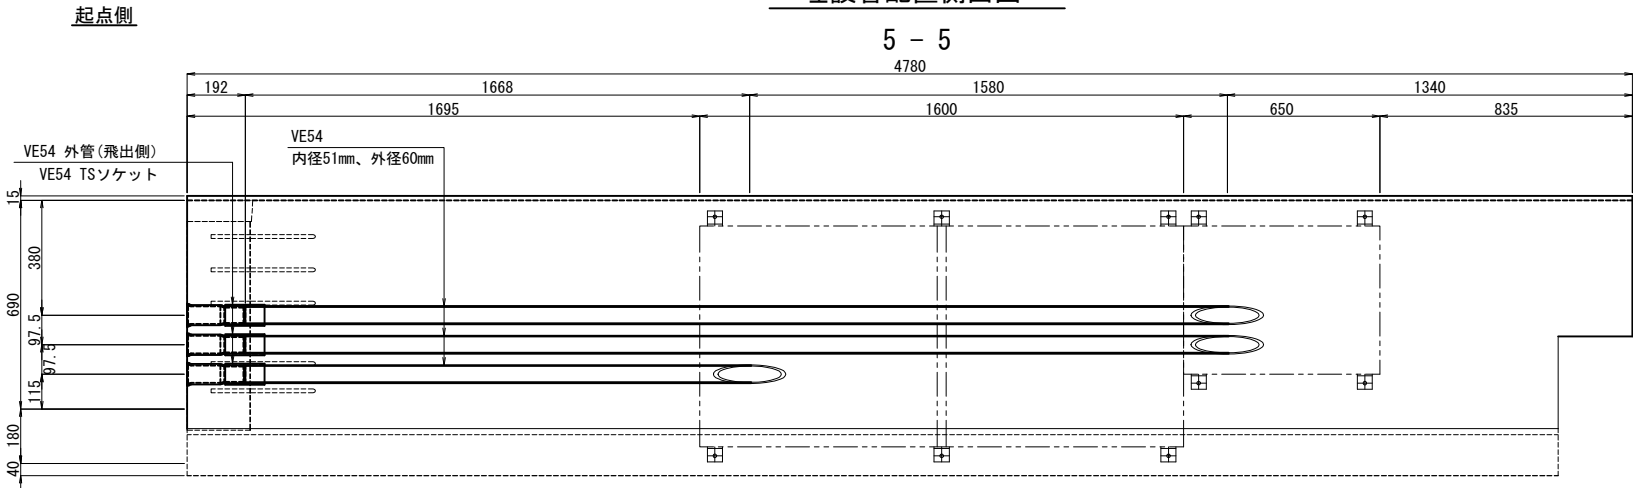


道央自動車道 千歳川大橋(下り線) 床版取替工事			
図面の種類	千歳川大橋(下り線) P15-P18 プレキャスト壁高欄詳細図(32)		
縮 尺	図 示	図面番号	/
設計会社名	戸田建設株式会社		
施工会社名	戸田建設株式会社		
事務所名	東日本高速道路株式会社 北海道支社 札幌管理事務所		




千歳川大橋(下り線) P18-P24 プレキャスト壁高欄詳細図(1)

S=1:25

断面図
1 - 1

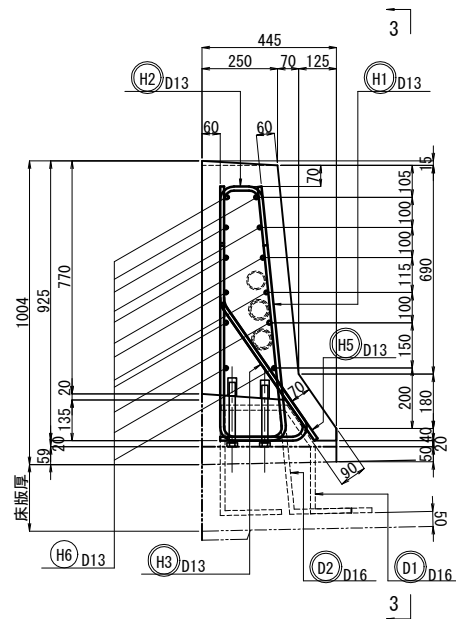


断面図
2 - 2

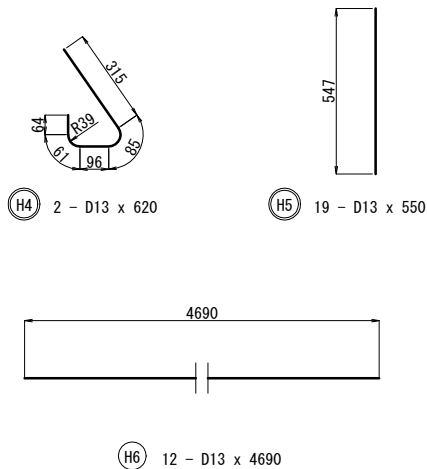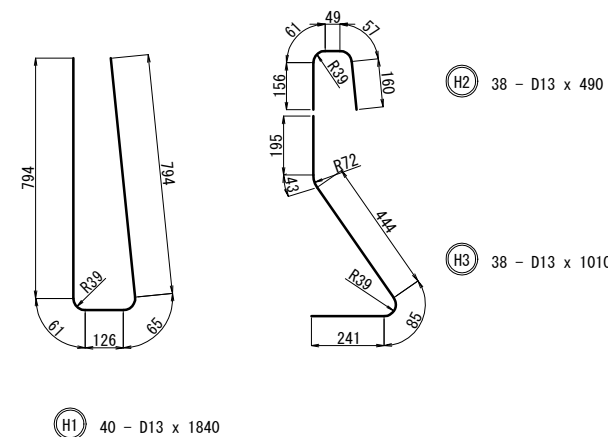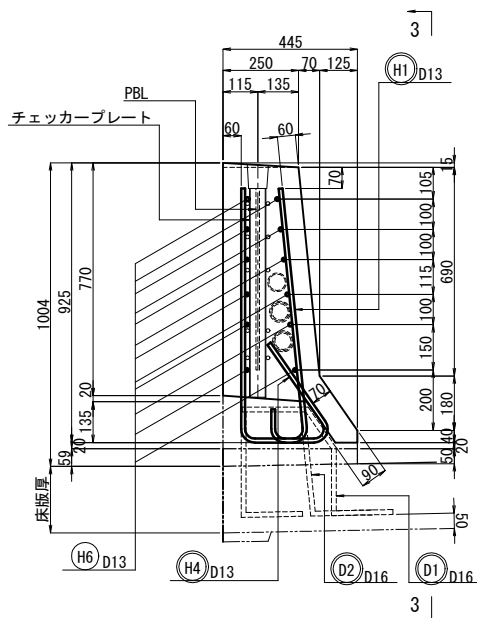


[路肩側 L-48-0M]

(P18-P19径間 製作数 : 3) (P19-P20径間 製作数 : 2)
(P20-P21径間 製作数 : 4) (P21-P22径間 製作数 : 3)
(P22-P23径間 製作数 : 3) (P23-P24径間 製作数 : 3)

側面図
3 - 3

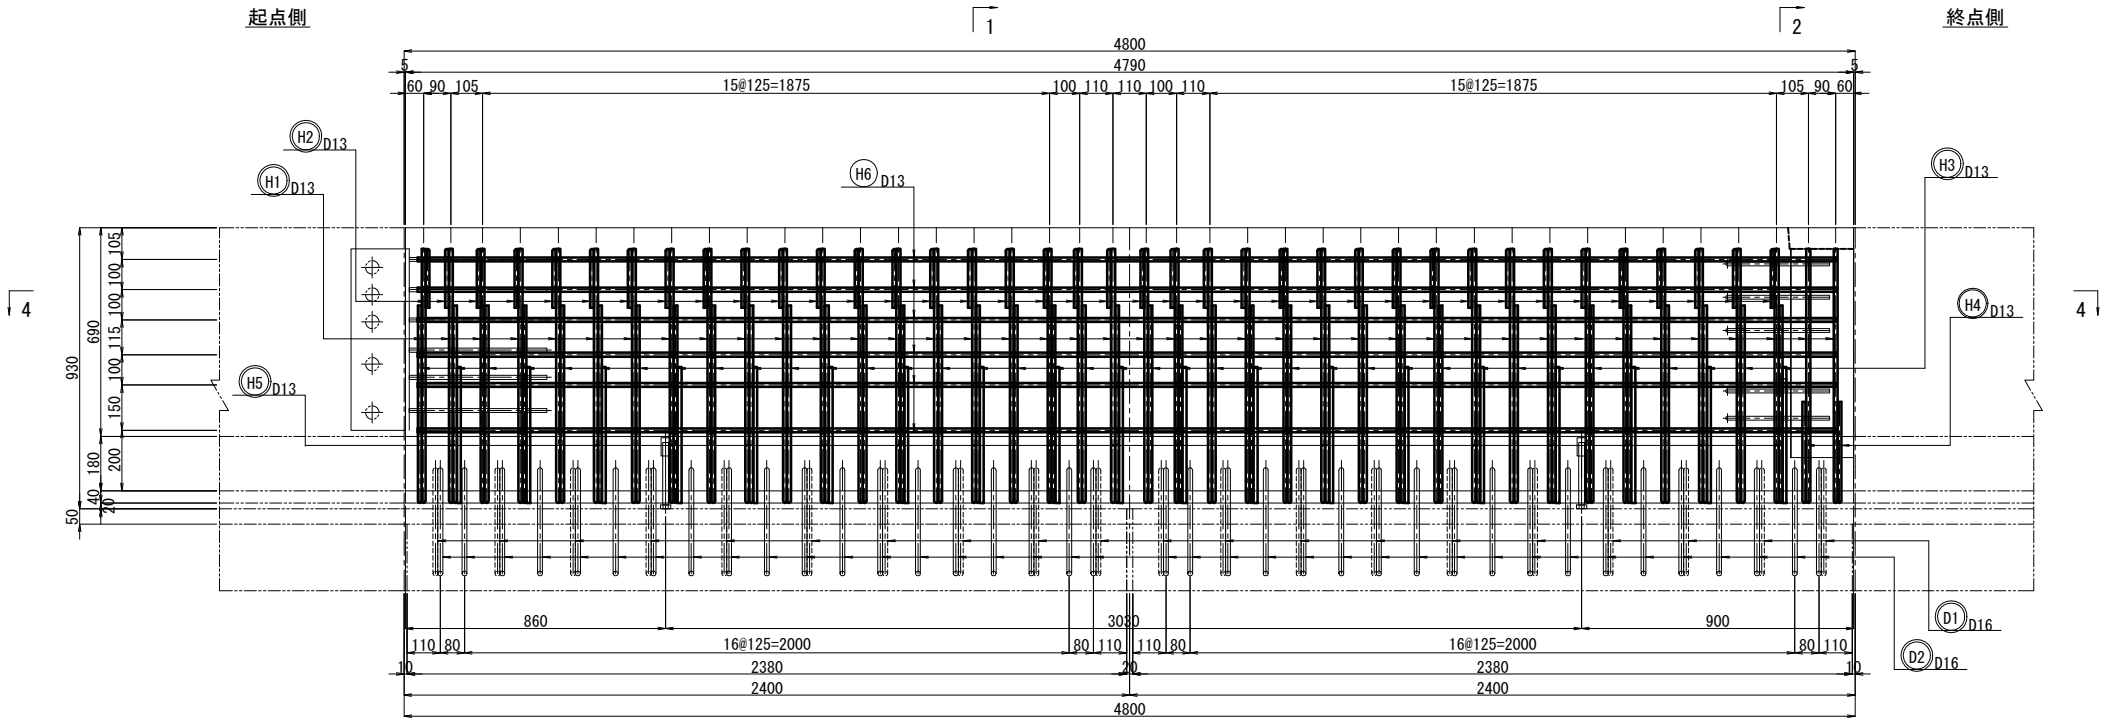

平面図
4 - 4

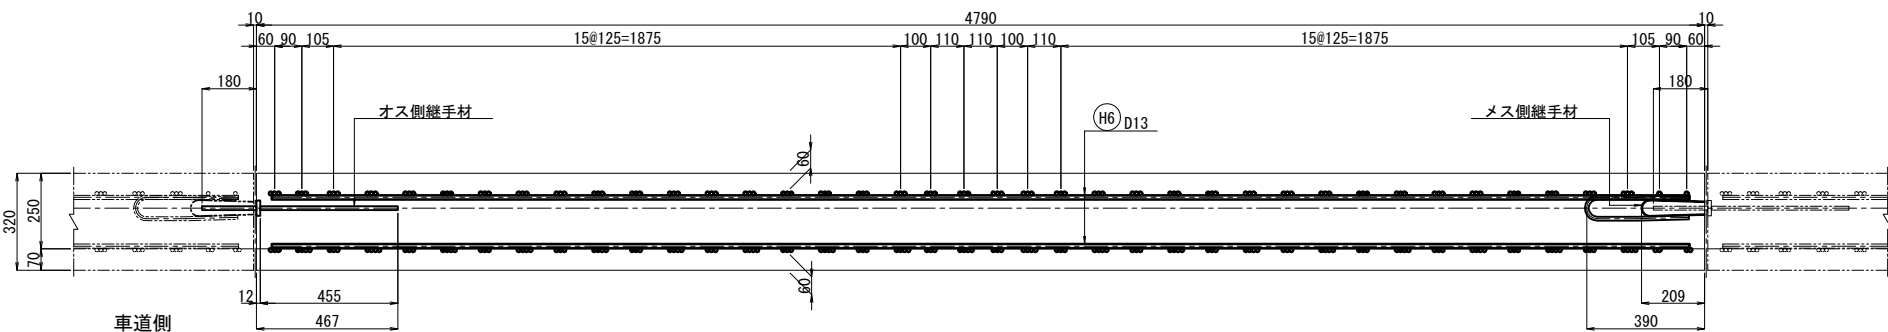

※ 鉄筋記号の○は塗装鉄筋を示す。
※ インサートおよび埋設管などの詳細位置は、壁高欄詳細図(2)を参照のこと。

鉄筋表(1ブロック当り)							
鉄筋番号	材質	長さ (mm)	本数 (本)	単位重量 (kg/m)	1本当り質量 (kg)	質量 (kg)	備考
H1	D13	1840	40	0.995	1.831	73	EP塗装
H2	D13	490	38	0.995	0.488	19	EP塗装
H3	D13	1010	38	0.995	1.005	38	EP塗装
H4	D13	620	2	0.995	0.627	1	EP塗装
H5	D13	550	19	0.995	0.547	10	EP塗装
H6	D13	4690	12	0.995	4.667	56	
合 計						197	kg
鉄筋質量集計(SD345)							
				普通鉄筋	塗装鉄筋		
				D13	56 kg	141 kg	197 kg
				合計	56 kg	141 kg	197 kg

道央自動車道 千歳川大橋(下り線)床版取替工事			
図面の種類	千歳川大橋(下り線) P18-P24 プレキャスト壁高欄詳細図(1)		
縮 尺	図 示	図面番号	/
設計会社名	戸田建設株式会社		
施工会社名	戸田建設株式会社		
事務所名	東日本高速道路株式会社 北海道支社 札幌管理事務所		


千歳川大橋(下り線) P18-P24 プレキャスト壁高欄詳細図(2)

S=1:25


[路肩側 L-48-0M]

(P18-P19径間 製作数 : 3) (P19-P20径間 製作数 : 2)
(P20-P21径間 製作数 : 4) (P21-P22径間 製作数 : 3)
(P22-P23径間 製作数 : 3) (P23-P24径間 製作数 : 3)


断面図
1 - 1

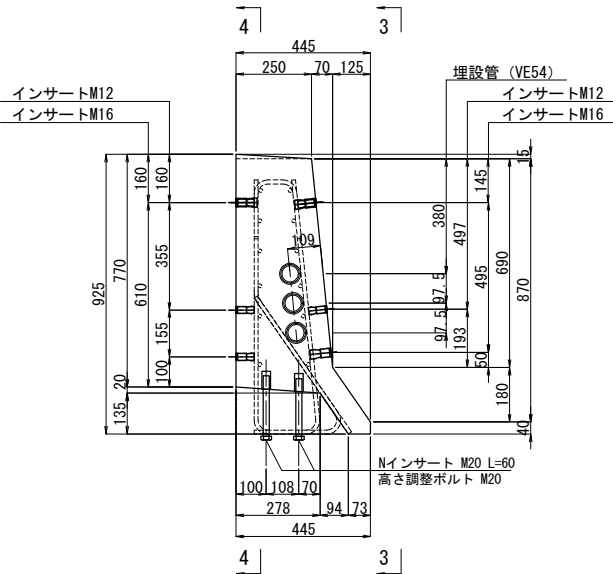


2 - 2

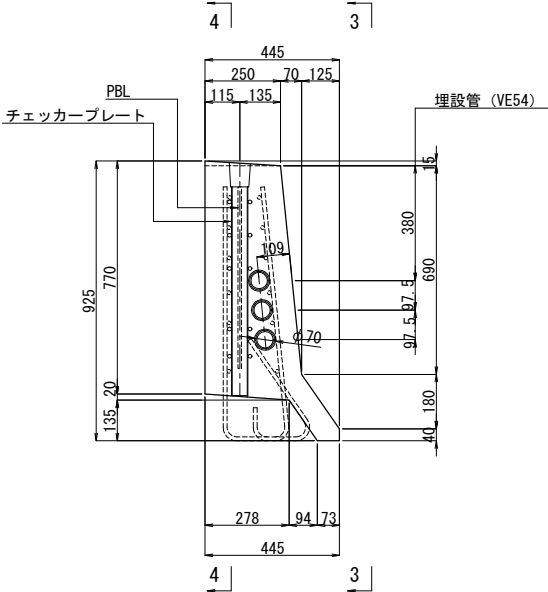

インサート配置側面図

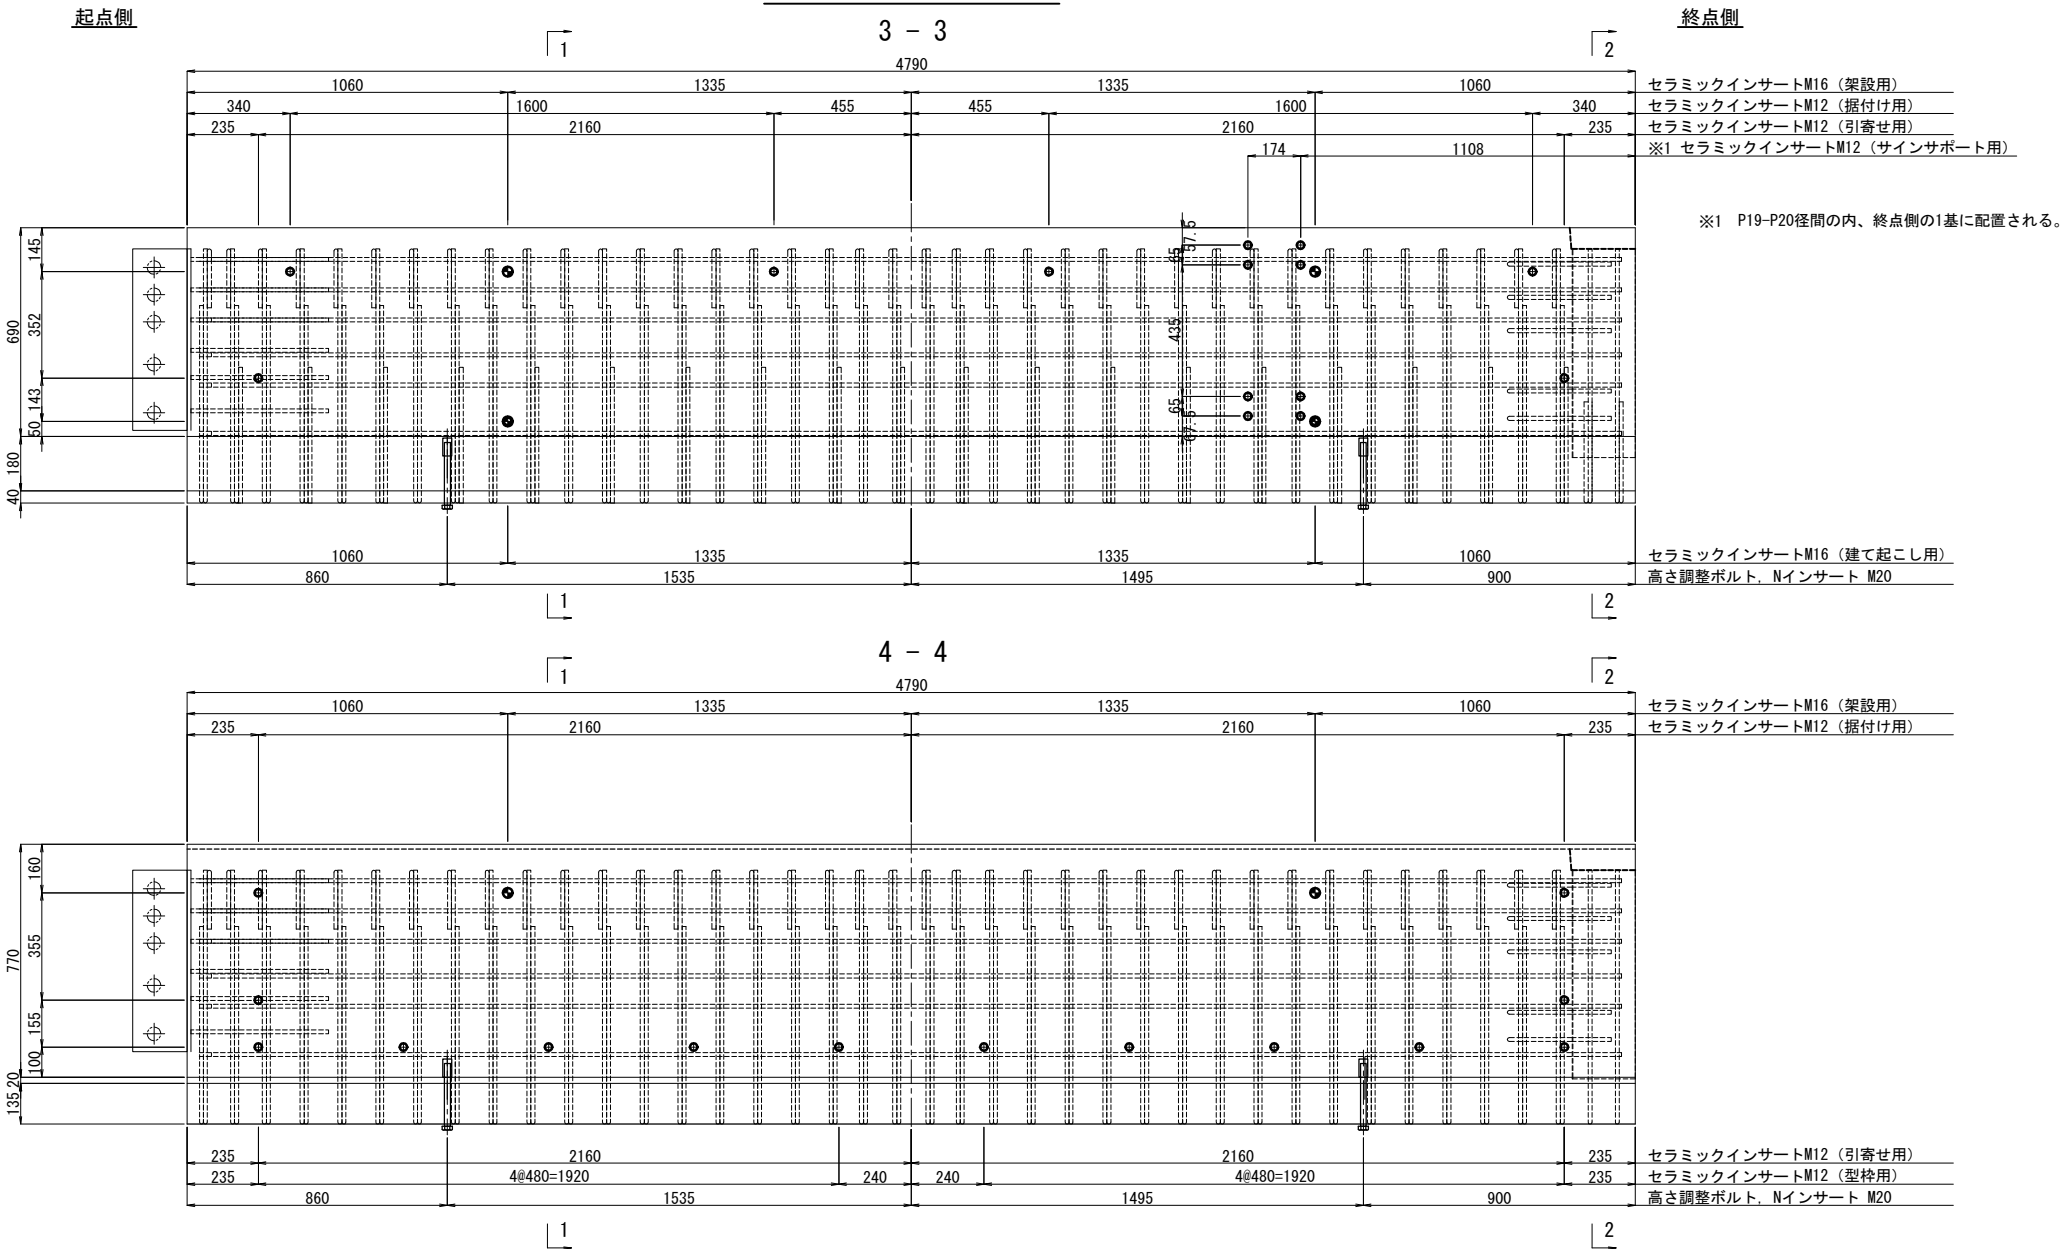


埋設管配置側面図

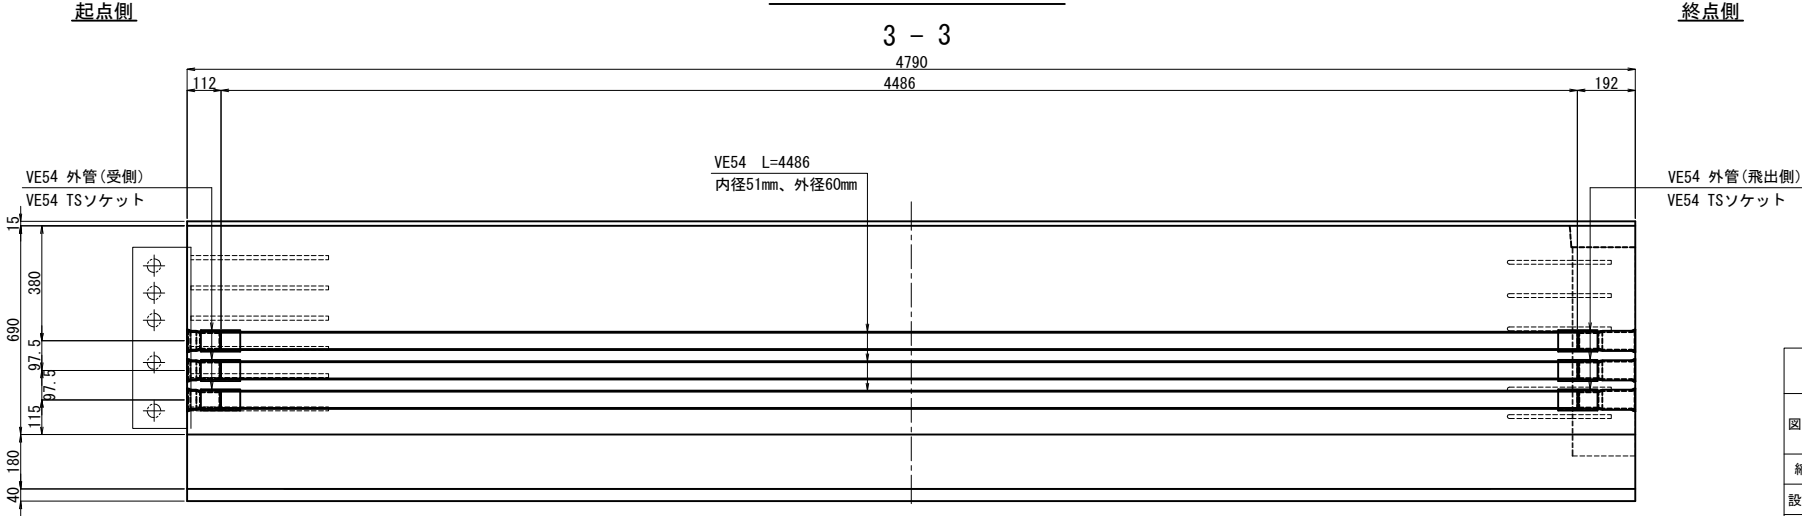

道央自動車道 千歳川大橋(下り線)床版取替工事			
図面の種類	千歳川大橋(下り線) P18-P24 プレキャスト壁高欄詳細図(2)		
縮 尺	図 示	図面番号	/
設計会社名	戸田建設株式会社		
施工会社名	戸田建設株式会社		
事務所名	東日本高速道路株式会社 北海道支社 札幌管理事務所		

S=1 : 25

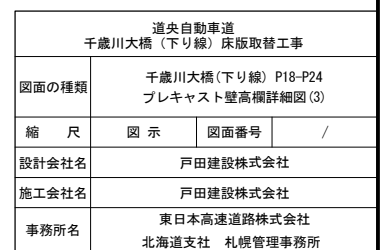


千歳川大橋(下り線) P18-P24 プレキャスト壁高欄詳細図(4)

S=1:25


[路肩側 L-24-0M]

(P19-P20径間 製作数 : 1) (P20-P21径間 製作数 : 1)
(P21-P22径間 製作数 : 1) (P22-P23径間 製作数 : 1)
(P23-P24径間 製作数 : 1)


断面図
1 - 1

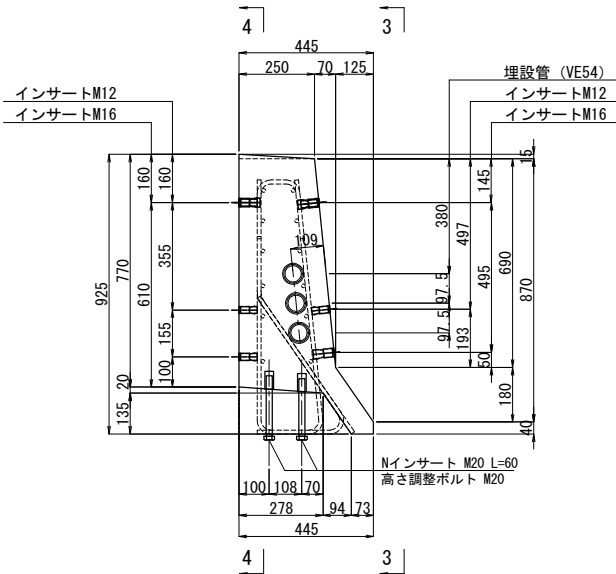


2 - 2

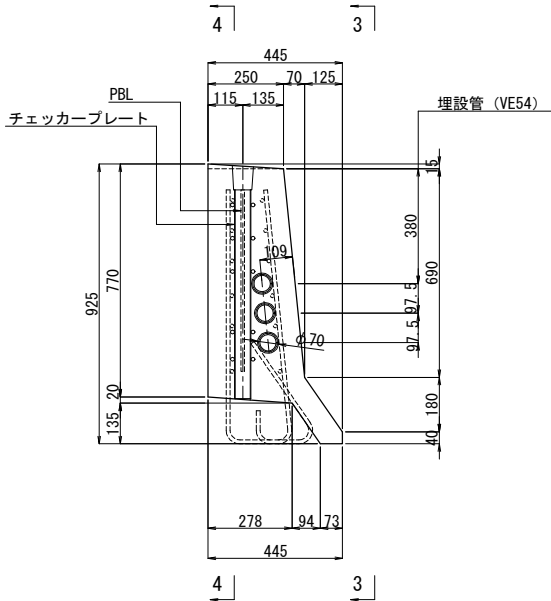


インサート配置側面図

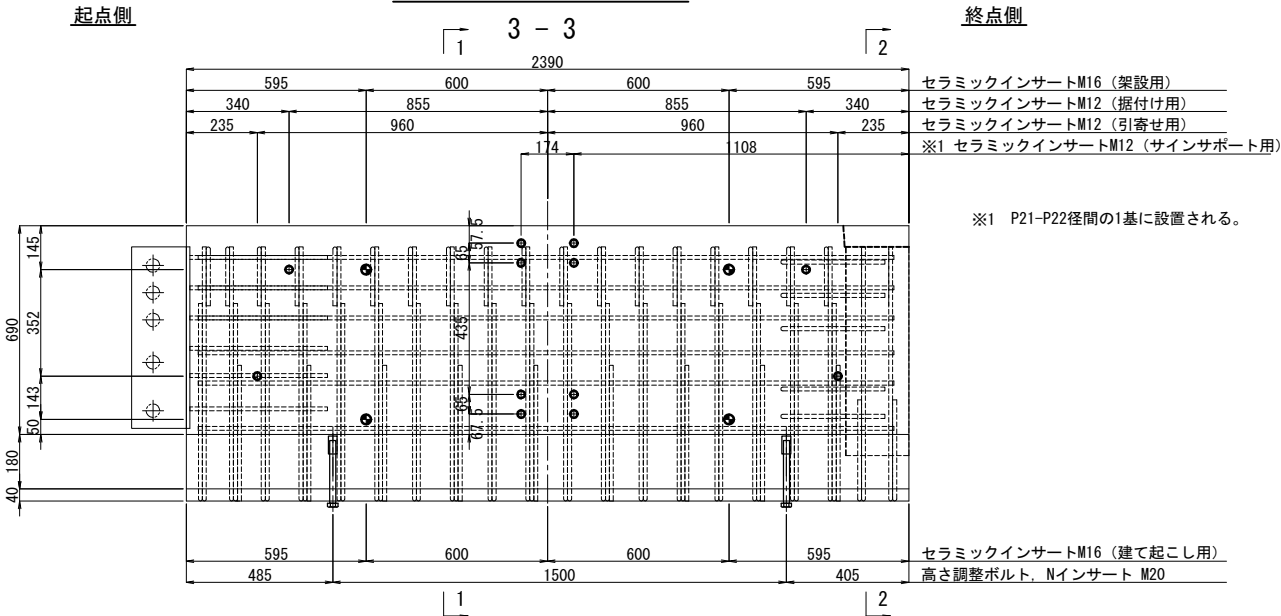

4 - 4

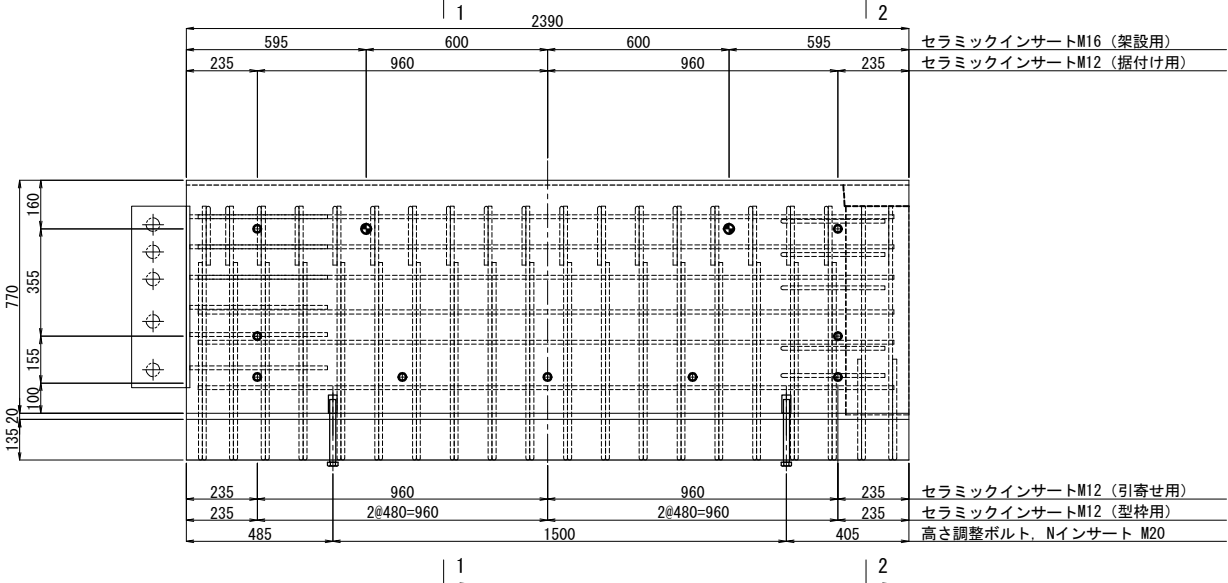

埋設管配置側面図

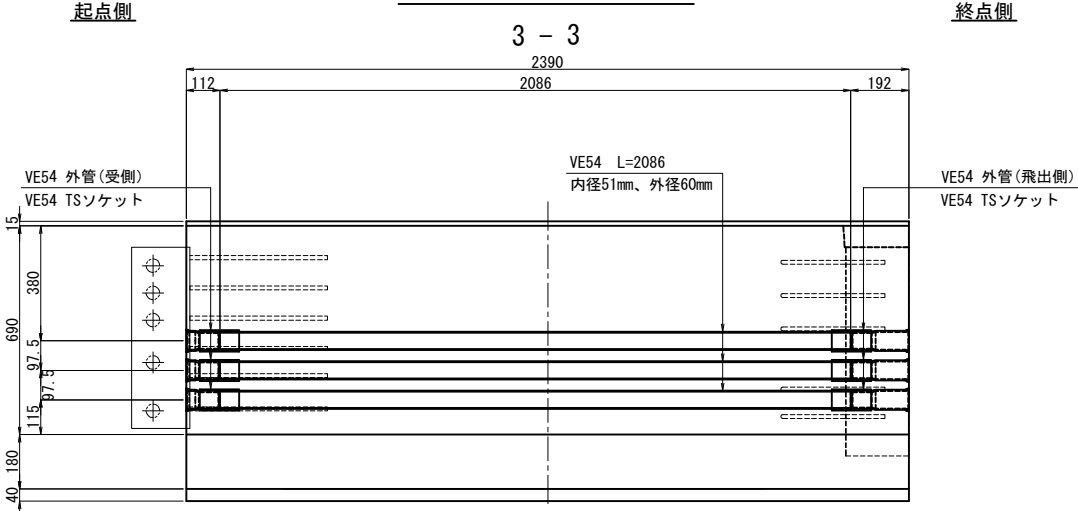

道央自動車道 千歳川大橋(下り線)床版取替工事			
図面の種類	千歳川大橋(下り線) P18-P24 プレキャスト壁高欄詳細図(4)		
縮 尺	図 示	図面番号	/
設計会社名	戸田建設株式会社		
施工会社名	戸田建設株式会社		
事務所名	東日本高速道路株式会社 北海道支社 札幌管理事務所		

千歳川大橋(下り線) P18-P24 プレキャスト壁高欄詳細図(5)


S=1:25

[路肩側 L-30-0M]

(P18-P19径間 製作数 : 1)




断面図

1 - 1

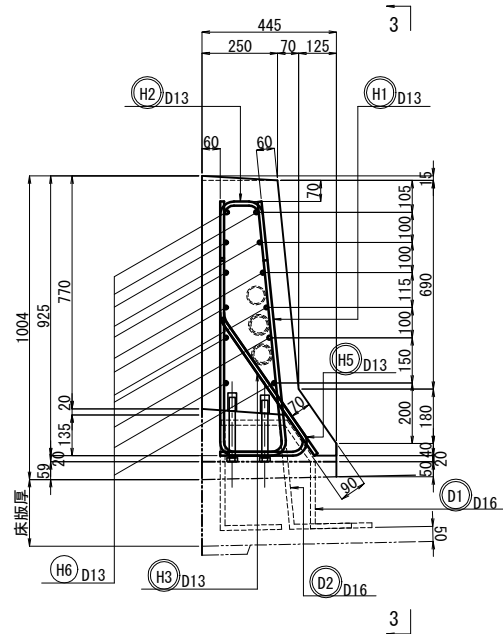


断面図

2 - 2

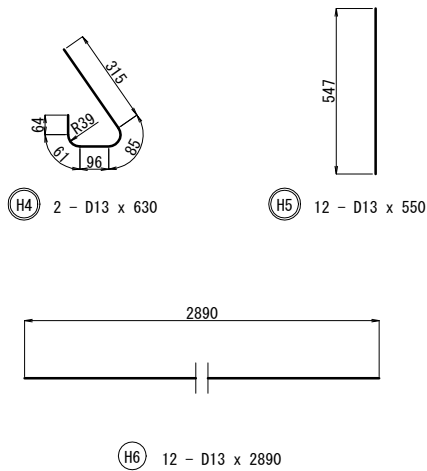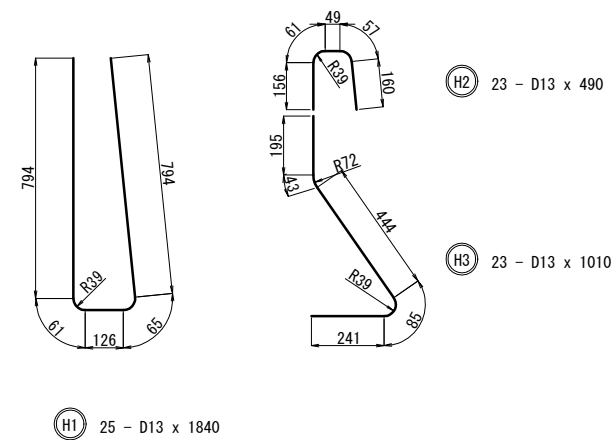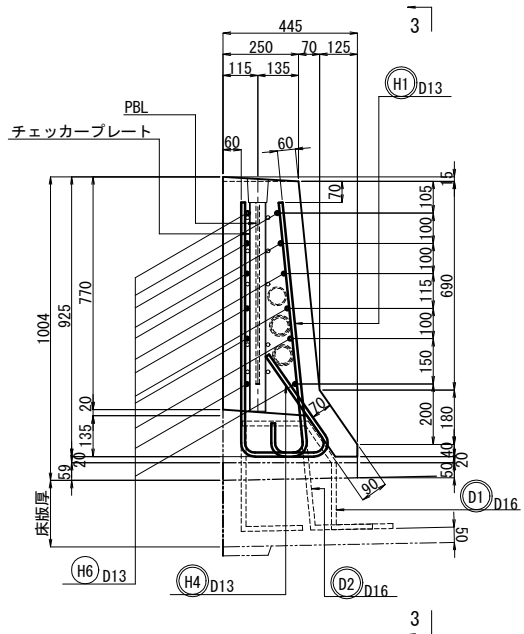


側面図

3 - 3

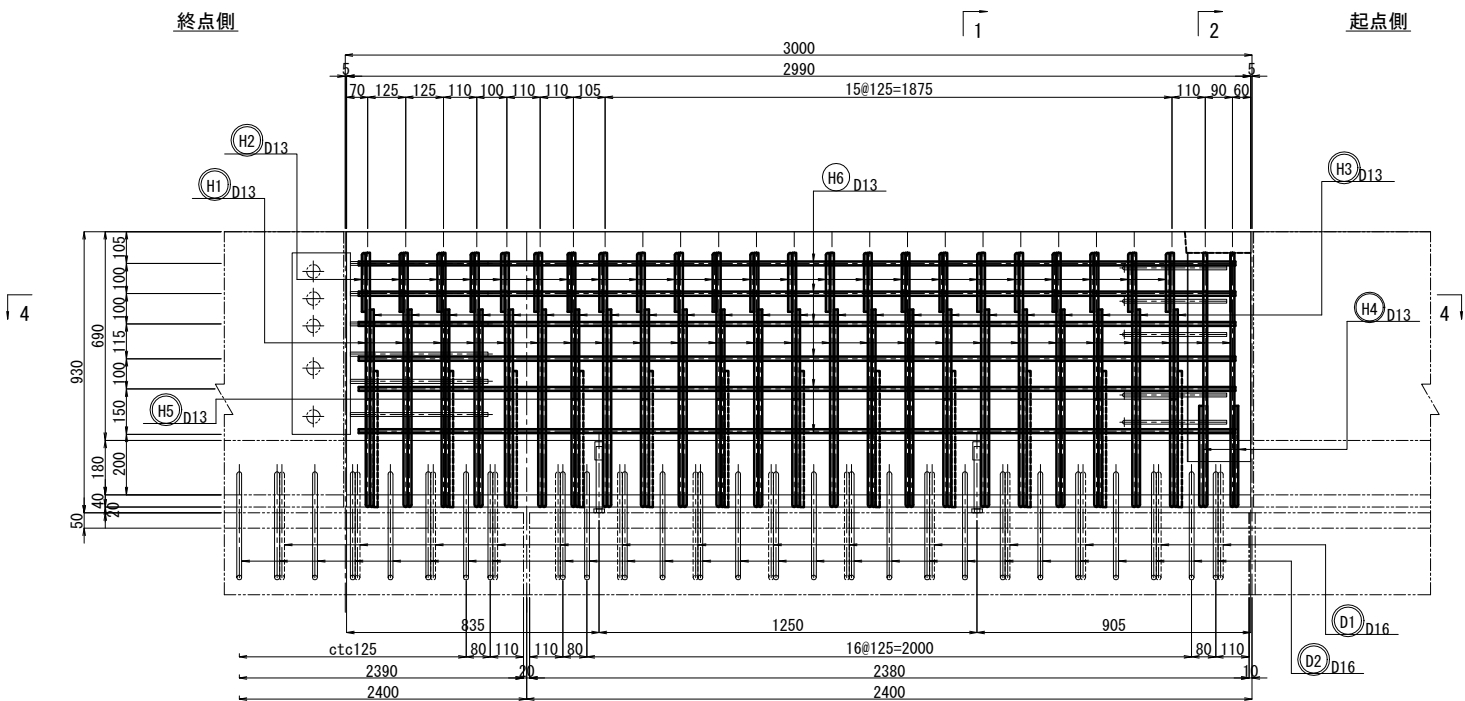

平面図

4 - 4

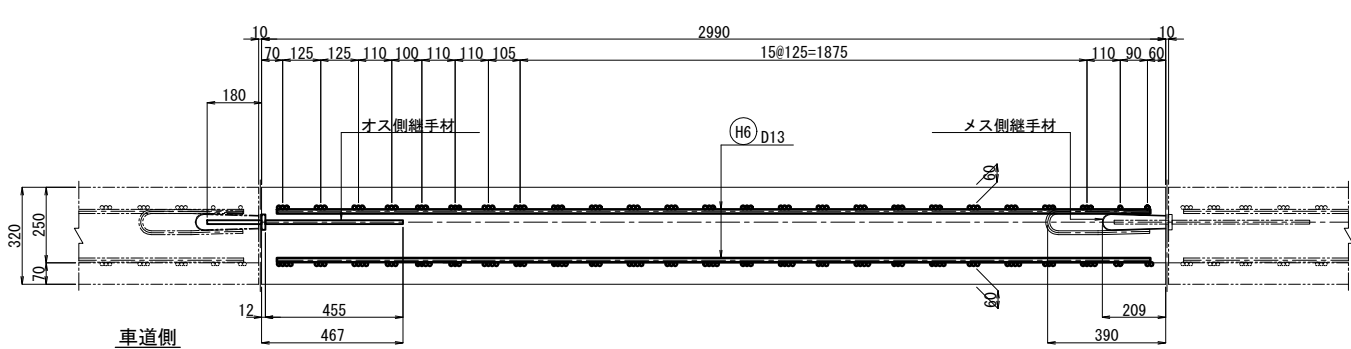

※ 鉄筋記号の○は塗装鉄筋を示す。
※ インサートおよび埋設管などの詳細位置は、壁高欄詳細図(6)を参照のこと。

鉄筋表(1ブロック当り)							
鉄筋番号	材質	長さ (mm)	本数 (本)	単位重量 (kg/m)	1本当り質量 (kg)	質量 (kg)	備考
H1	D13	1840	25	0.995	1.831	46	EP塗装
H2	D13	490	23	0.995	0.488	11	EP塗装
H3	D13	1010	23	0.995	1.005	23	EP塗装
H4	D13	620	2	0.995	0.617	1	EP塗装
H5	D13	550	12	0.995	0.547	7	EP塗装
H6	D13	2890	12	0.995	2.876	35	
合 計						123	kg
鉄筋質量集計(SD345)							
				普通鉄筋	塗装鉄筋		
				D13	35 kg	88 kg	123 kg
				合計	35 kg	88 kg	123 kg

道央自動車道 千歳川大橋(下り線)床版取替工事			
図面の種類	千歳川大橋(下り線) P18-P24 プレキャスト壁高欄詳細図(5)		
縮 尺	図 示	図面番号	/
設計会社名	戸田建設株式会社		
施工会社名	戸田建設株式会社		
事務所名	東日本高速道路株式会社 北海道支社 札幌管理事務所		

千歳川大橋(下り線) P18-P24 プレキャスト壁高欄詳細図(6)


S=1:25

[路肩側 L-30-0M]


(P18-P19径間 製作数 : 1)

断面図

1 - 1

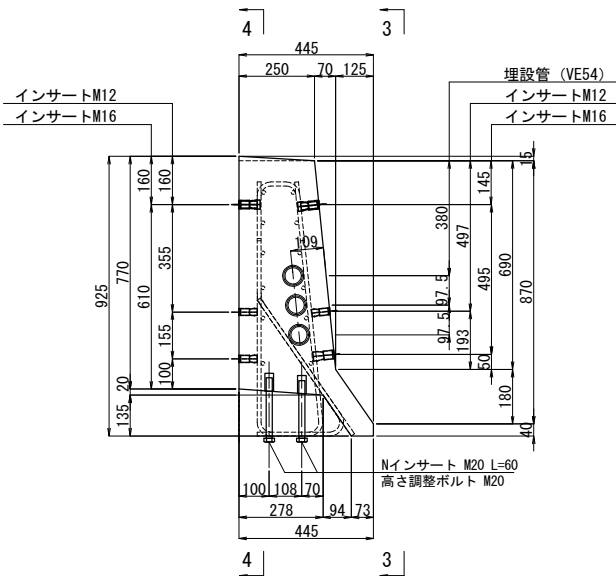


2 - 2

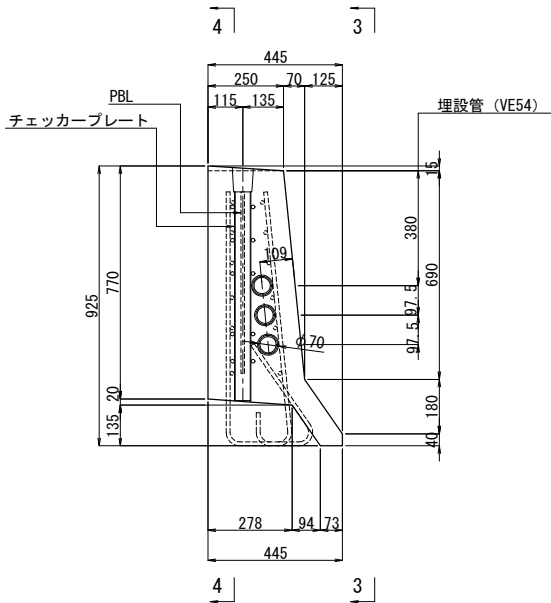


インサート配置側面図

3 - 3

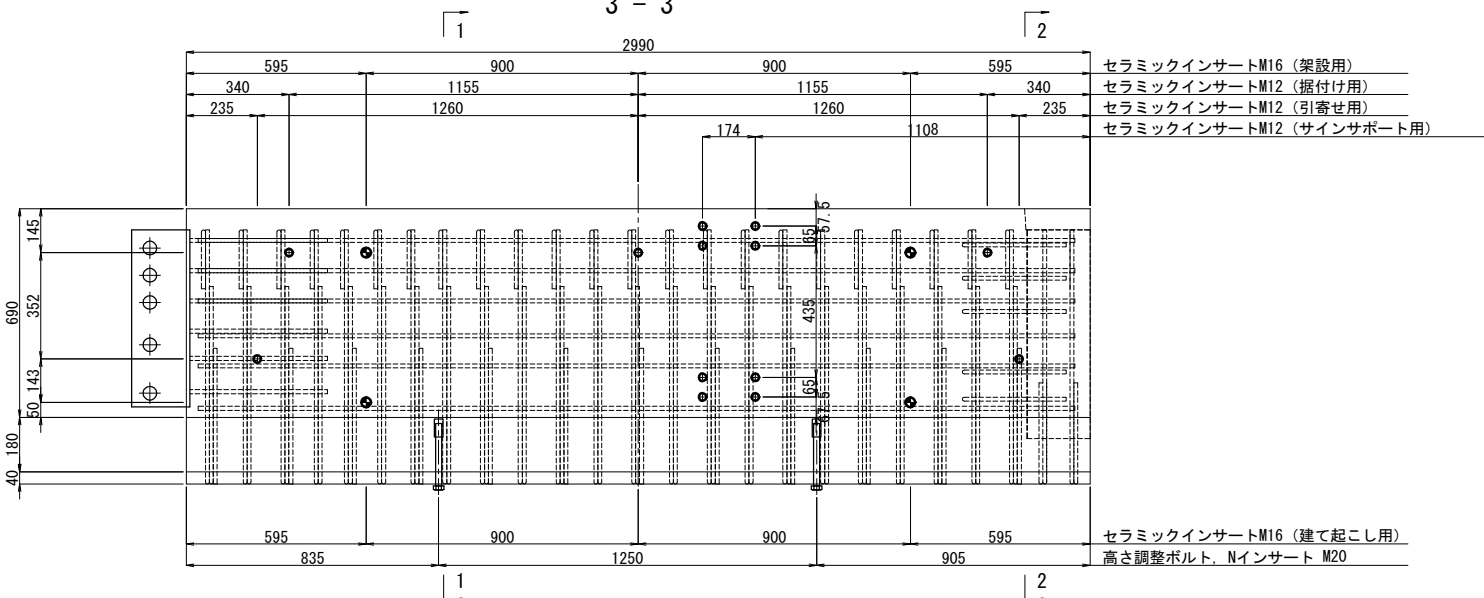


4 - 4

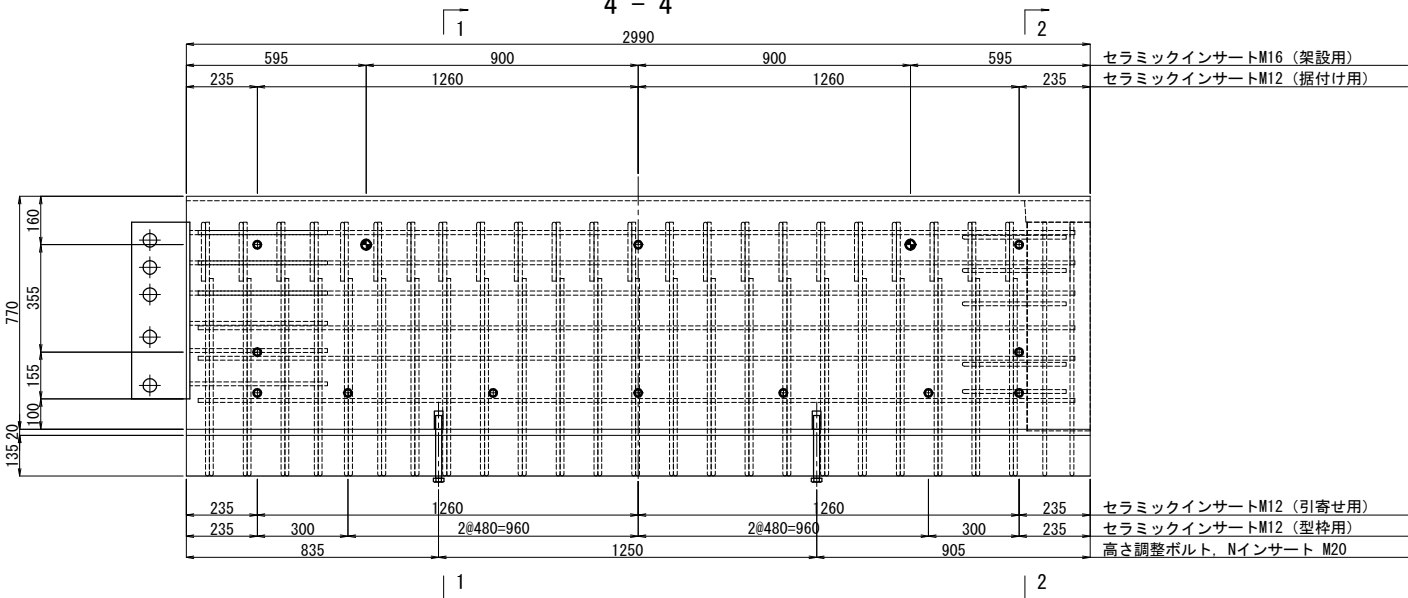

埋設管配置側面図

3 - 3

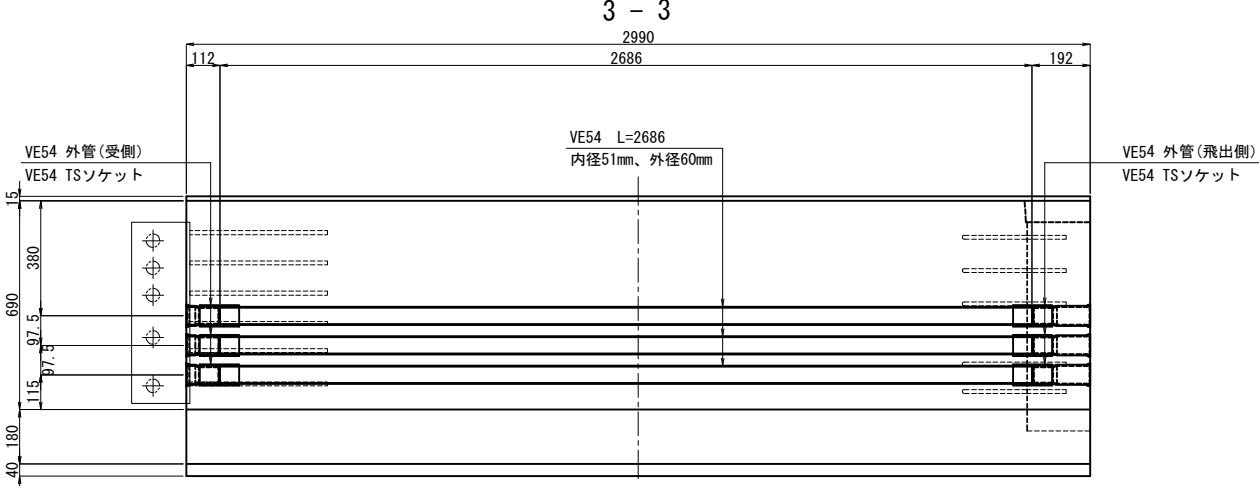

道央自動車道 千歳川大橋(下り線) 床版取替工事			
図面の種類	千歳川大橋(下り線) P18-P24 プレキャスト壁高欄詳細図(6)		
縮 尺	図 示	図面番号	/
設計会社名	戸田建設株式会社		
施工会社名	戸田建設株式会社		
事務所名	東日本高速道路株式会社 北海道支社 札幌管理事務所		

S=1 : 25



通央自動車道 千歳川大橋（下り線）床版取替工事			
図面の種類	千歳川大橋（下り線）P18-P24 プレキャスト壁高欄詳細図 (8)		
縮 尺	図 示	図面番号	/
設計会社名	戸田建設株式会社		
施工会社名	戸田建設株式会社		
事務所名	東日本高速道路株式会社 北海道支社 札幌管理事務所		

千歳川大橋(下り線) P18-P24 プレキャスト壁高欄詳細図(9)





S=1:25

[路肩側 L-48-FM]

(P19-P20径間 製作数 : 1) (P20-P21径間 製作数 : 1)
(P21-P22径間 製作数 : 1) (P22-P23径間 製作数 : 1)
(P23-P24径間 製作数 : 1)


側面図

4 - 4


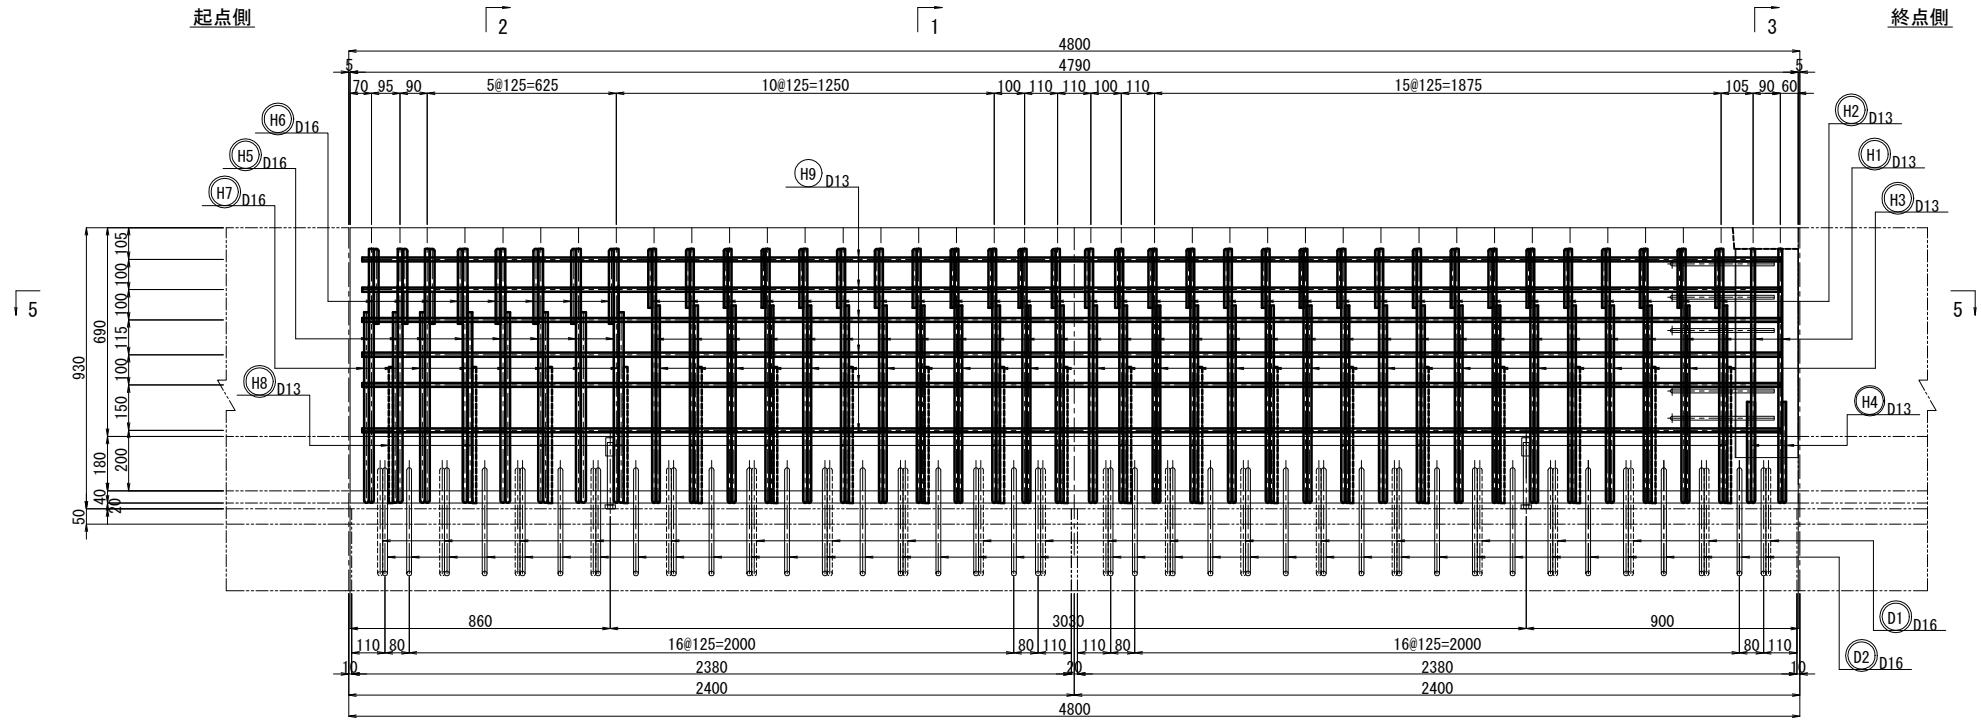
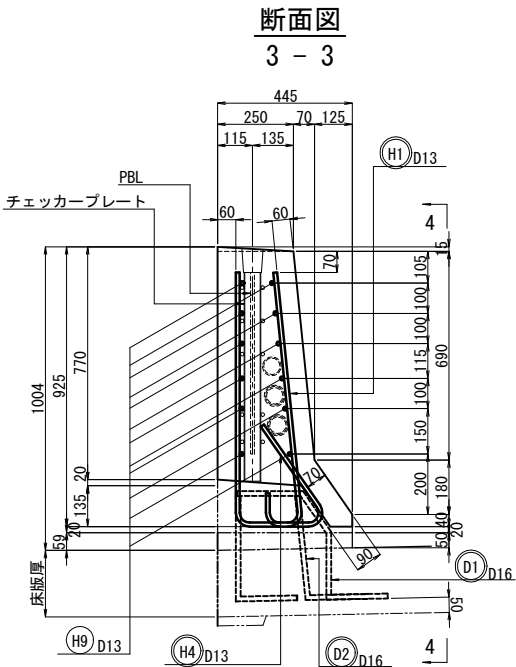
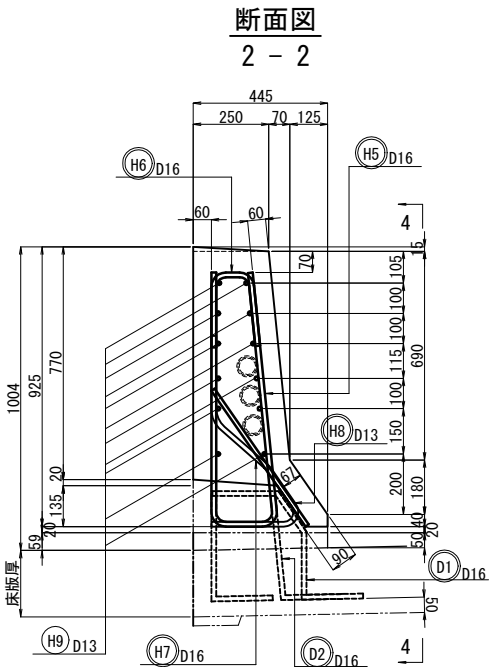
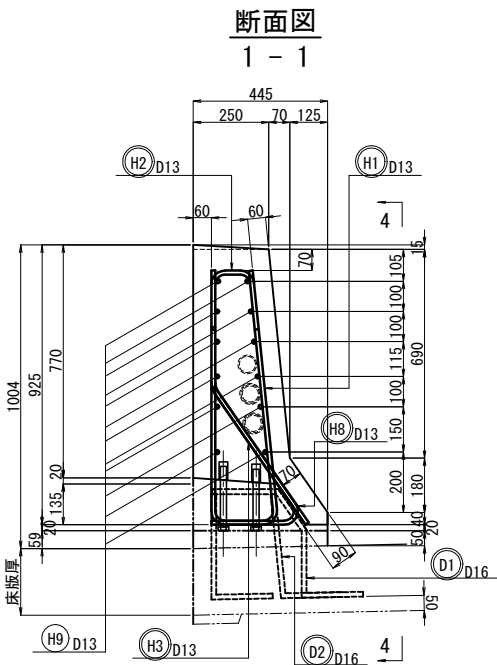


平面図

5 - 5

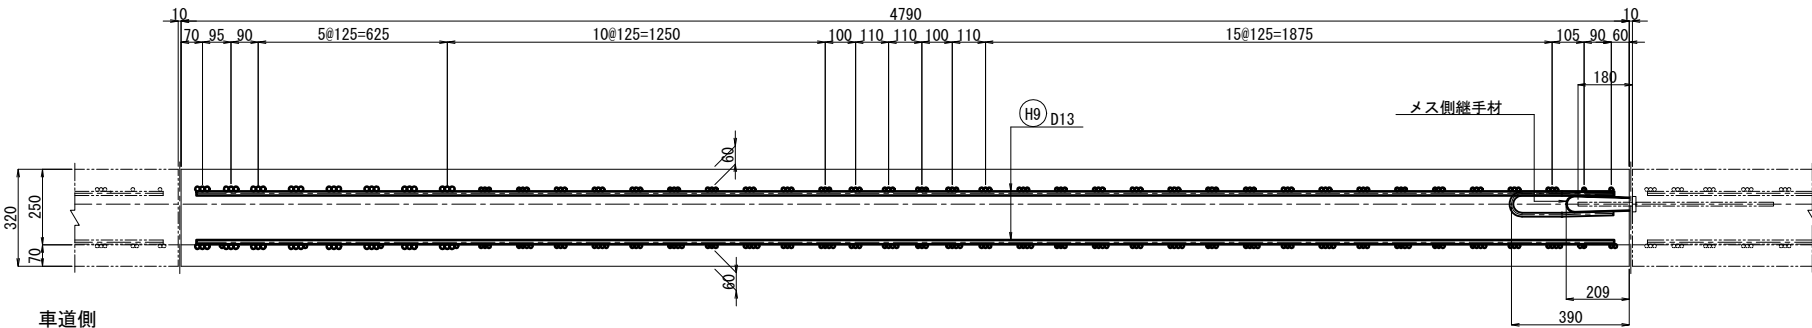

※ 鉄筋記号の  は塗装鉄筋を示す。
※ インサートおよび埋設管などの詳細位置は、壁高欄詳細図(10)を参照のこと。

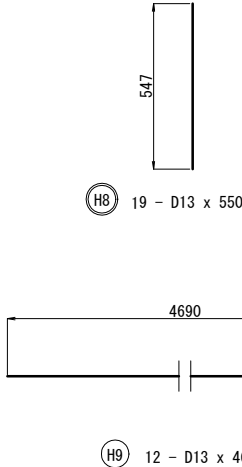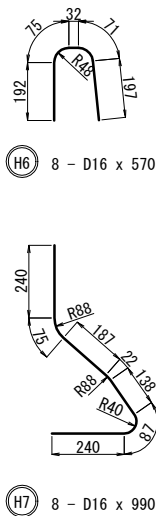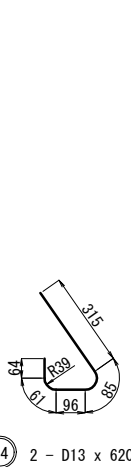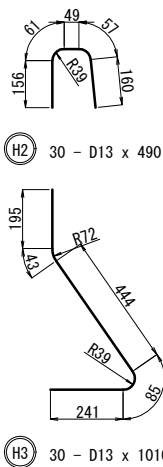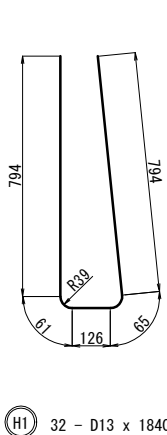

鉄筋表(1ブロック当り)							
鉄筋番号	材質	長さ (mm)	本数 (本)	単位重量 (kg/m)	1本当り質量 (kg)	質 量 (kg)	備考
H1	D13	1840	32	0.995	1.831	59	EP塗装
H2	D13	490	30	0.995	0.488	15	EP塗装
H3	D13	1010	30	0.995	1.005	30	EP塗装
H4	D13	620	2	0.995	0.617	1	EP塗装
H5	D16	1840	8	1.56	2.870	23	EP塗装
H6	D16	570	8	1.56	0.889	7	EP塗装
H7	D16	990	8	1.56	1.544	12	EP塗装
H8	D13	550	19	0.995	0.547	10	EP塗装
H9	D13	4690	12	0.995	4.667	56	
合 計						213	kg
鉄筋質量集計(SD345)							
				普通鉄筋		塗装鉄筋	
				D16	0 kg	42 kg	42 kg
				D13	56 kg	115 kg	171 kg
				合計	56 kg	157 kg	213 kg


道央自動車道 千歳川大橋(下り線)床版取替工事			
図面の種類	千歳川大橋(下り線) P18-P24 プレキャスト壁高欄詳細図(9)		
縮 尺	図 示	図面番号	/
設計会社名	戸田建設株式会社		
施工会社名	戸田建設株式会社		
事務所名	東日本高速道路株式会社 北海道支社 札幌管理事務所		

千歳川大橋(下り線) P18-P24 プレキャスト壁高欄詳細図(10)


S=1:25




断面図
1 - 1

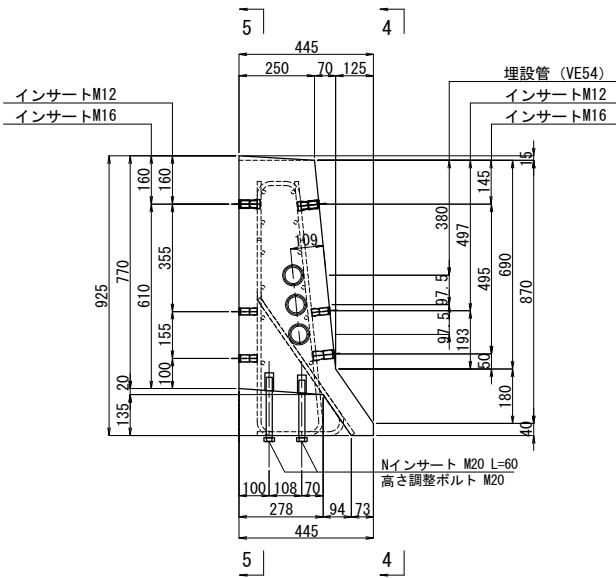

2 - 2

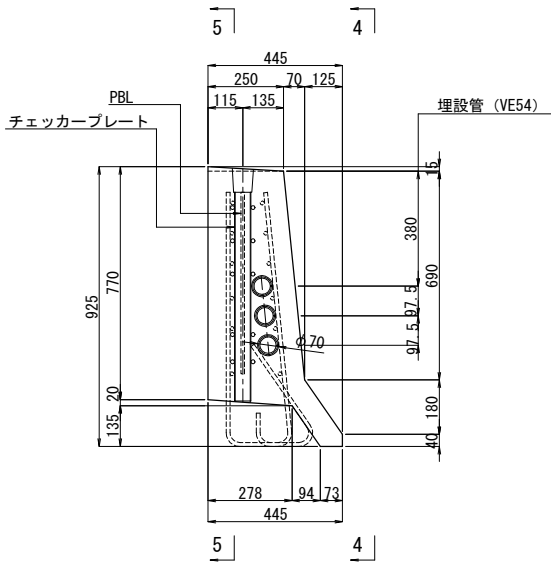


3 - 3

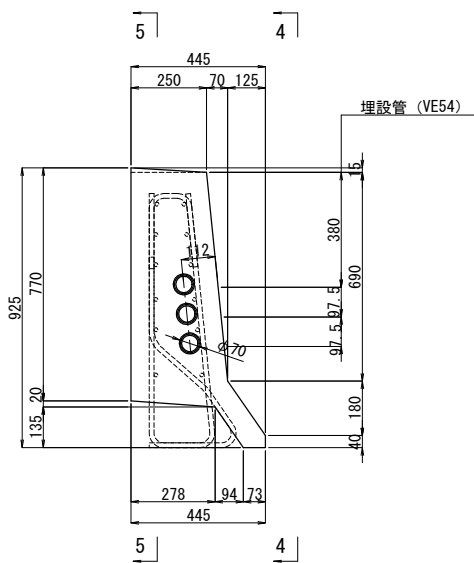


[路肩側 L-48-FM]

(P19-P20径間 製作数 : 1) (P20-P21径間 製作数 : 1)
(P21-P22径間 製作数 : 1) (P22-P23径間 製作数 : 1)
(P23-P24径間 製作数 : 1)

インサート配置側面図

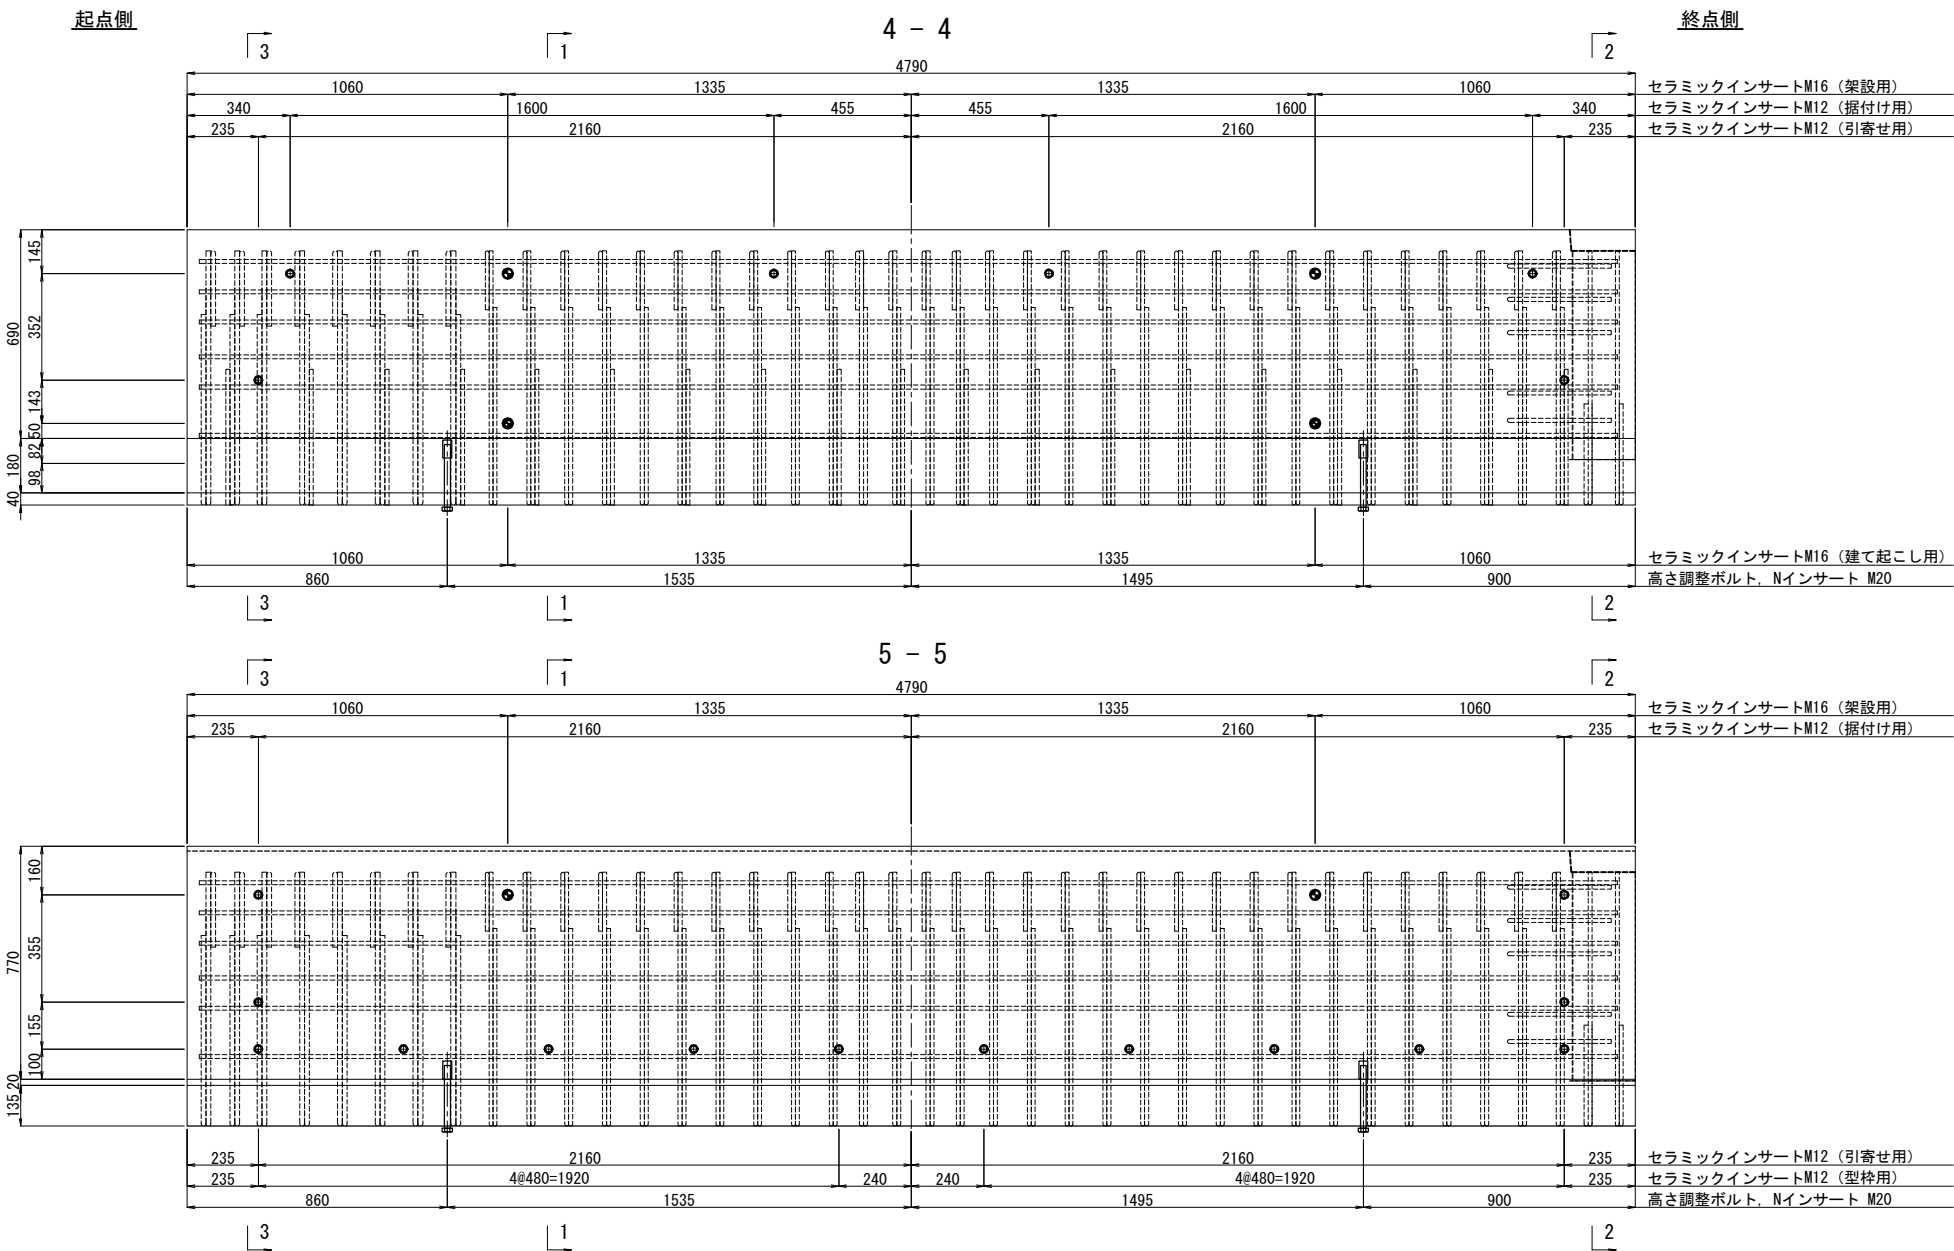

埋設管配置側面図

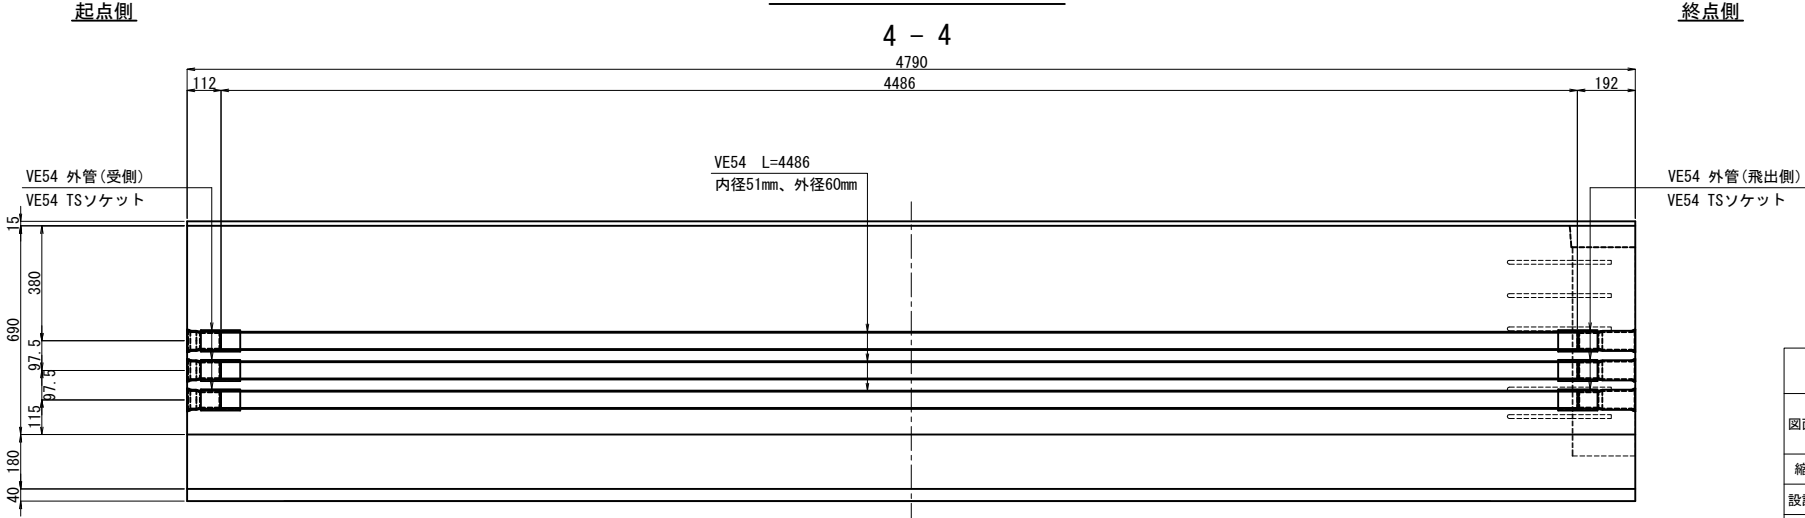


道央自動車道 千歳川大橋(下り線) 床版取替工事			
図面の種類	千歳川大橋(下り線) P18-P24 プレキャスト壁高欄詳細図(10)		
縮 尺	図 示	図面番号	/
設計会社名	戸田建設株式会社		
施工会社名	戸田建設株式会社		
事務所名	東日本高速道路株式会社 北海道支社 札幌管理事務所		

[路肩側 L-24-FF]

(P21上 製作数 : 1)


断面図

1 - 1

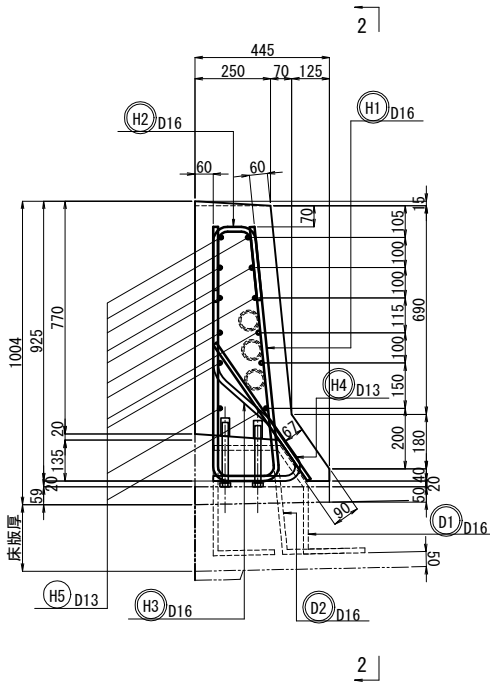


側面図

2 - 2

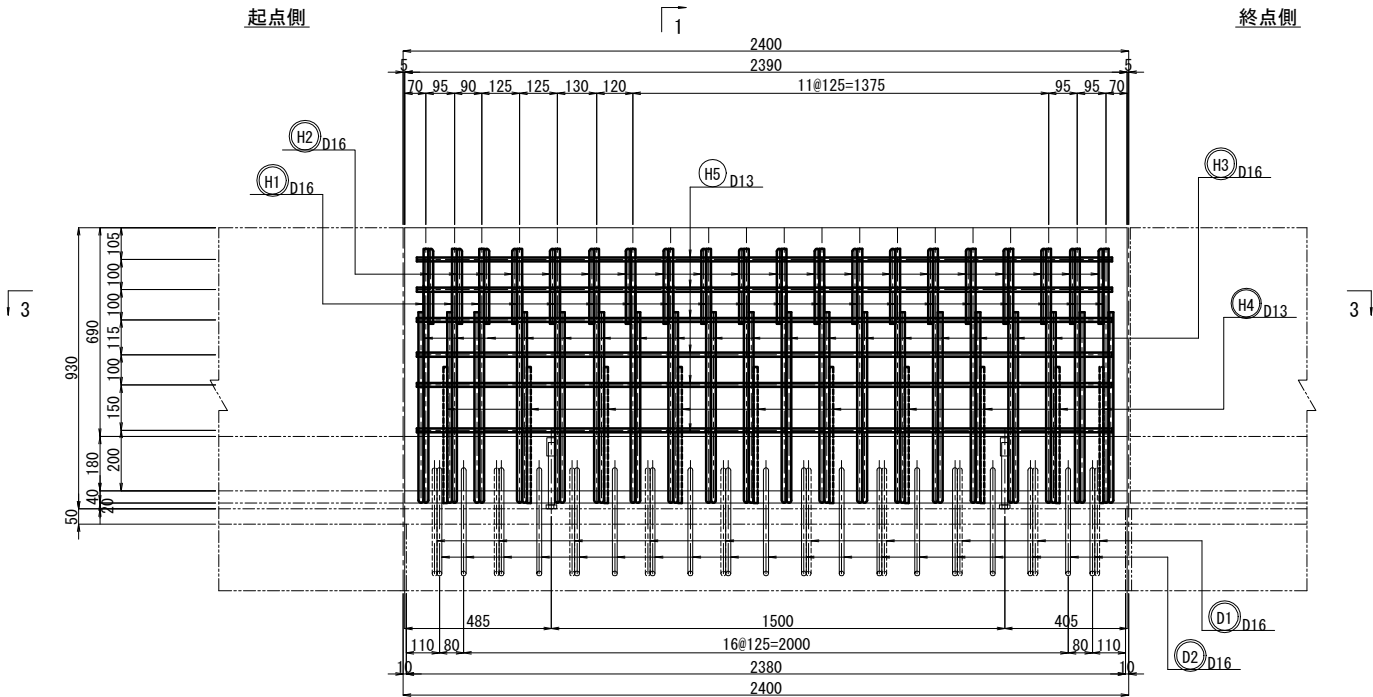


平面図


3 - 3

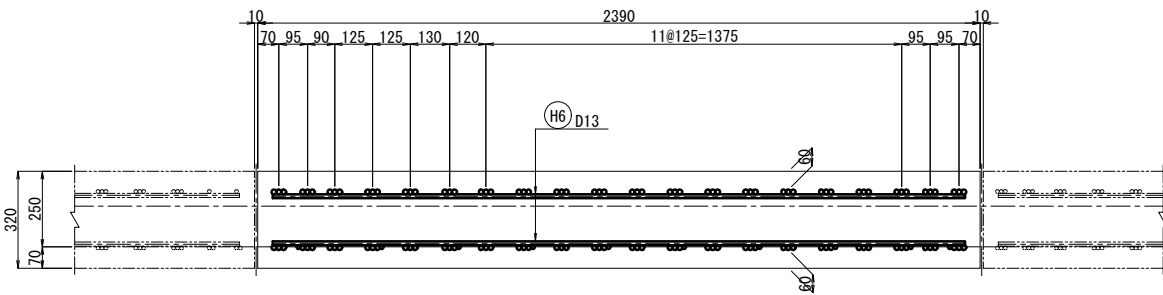


車道側

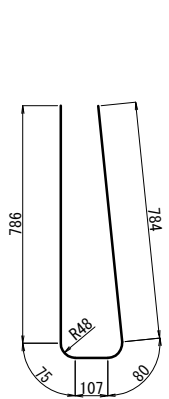


H1 20 - D16 x 1840

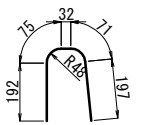


H2 20 - D16 x 570

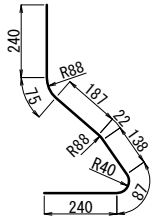

H3 20 - D16 x 990

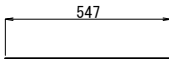

H4 10 - D13 x 550

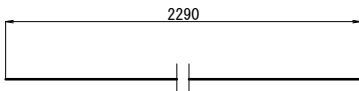

H5 12 - D13 x 2290

鉄筋表(1ブロック当り)

鉄筋番号	材質	長さ (mm)	本数 (本)	単位重量 (kg/m)	1本当り質量 (kg)	質量 (kg)	備考
H1	D16	1840	20	1.56	2.870	57	EP塗装
H2	D16	570	20	1.56	0.889	18	EP塗装
H3	D16	990	20	1.56	1.544	31	EP塗装
H4	D13	550	10	0.995	0.547	5	EP塗装
H5	D13	2290	12	0.995	2.279	27	
合 計						138	kg
鉄筋質量集計 (SD345)							
				普通鉄筋	塗装鉄筋		
				D16	0 kg	106 kg	106 kg
				D13	27 kg	5 kg	32 kg
				合計	27 kg	111 kg	138 kg


※ 鉄筋記号の○は塗装鉄筋を示す。

※ インサートおよび埋設管などの詳細位置は、壁高欄詳細図(12)を参照のこと。



道央自動車道 千歳川大橋(下り線)床版取替工事			
図面の種類	千歳川大橋(下り線) P18-P24 プレキャスト壁高欄詳細図(11)		
縮 尺	図 示	図面番号	/
設計会社名	戸田建設株式会社		
施工会社名	戸田建設株式会社		
事務所名	東日本高速道路株式会社 北海道支社 札幌管理事務所		

S=1:25


(P21上 製作数 : 1)

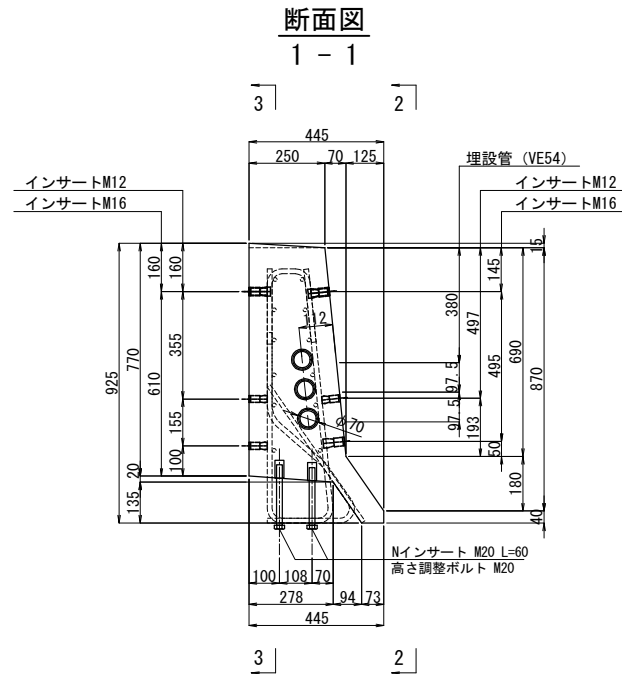

終点側

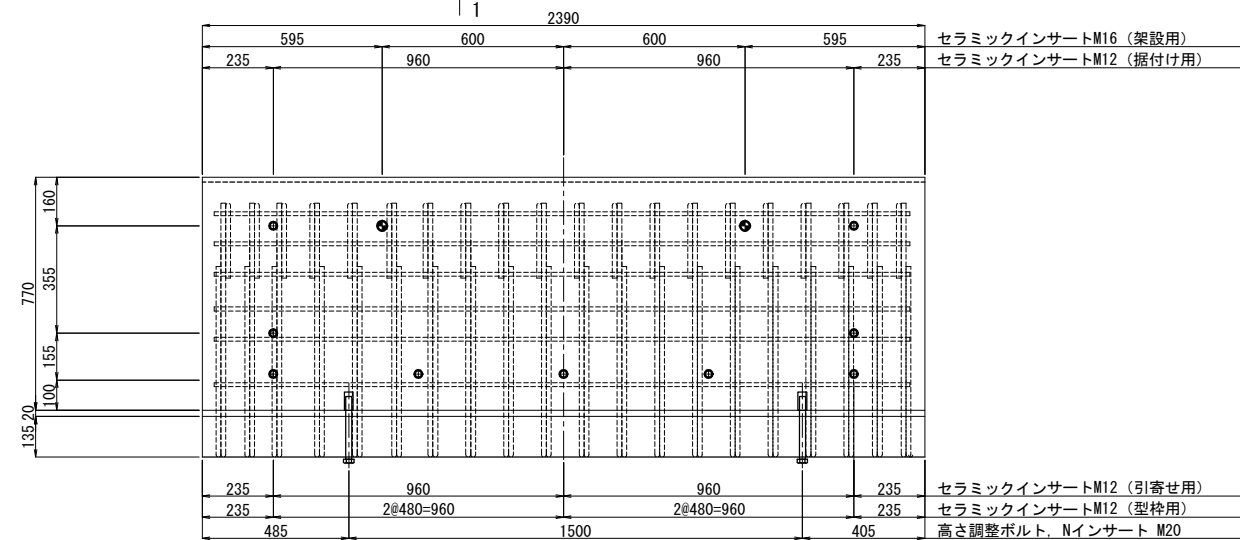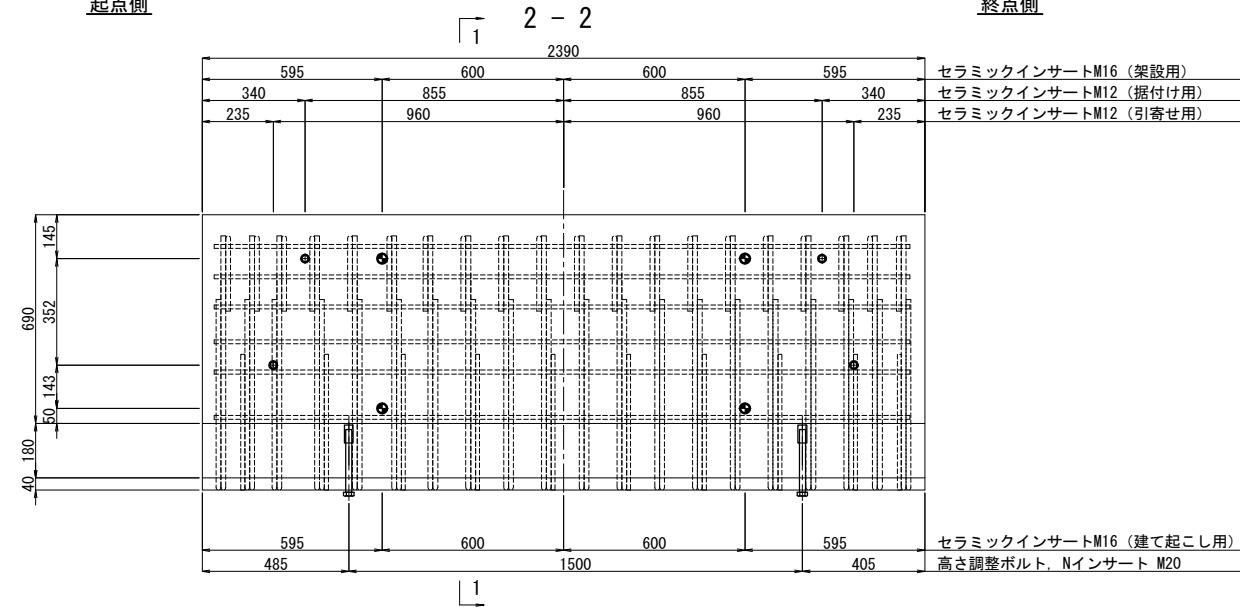

終点側

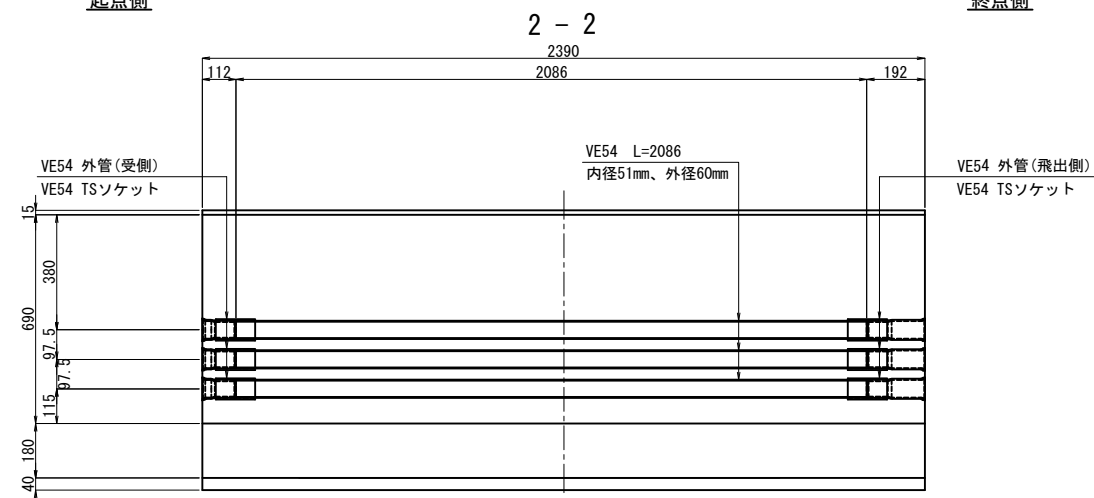


道央自動車道 千歳川大橋（下り線）床版取替工事			
図面の種類	千歳川大橋（下り線）P18～P24 プレキャスト壁高欄詳細図(12)		
縮 尺	図 示	図面番号	/
設計会社名	戸田建設株式会社		
施工会社名	戸田建設株式会社		
事務所名	東日本高速道路株式会社 北海道支社 札幌管理事務所		


千歳川大橋(下り線) P18-P24 プレキャスト壁高欄詳細図(13)

S=1:25


断面図
1 - 1

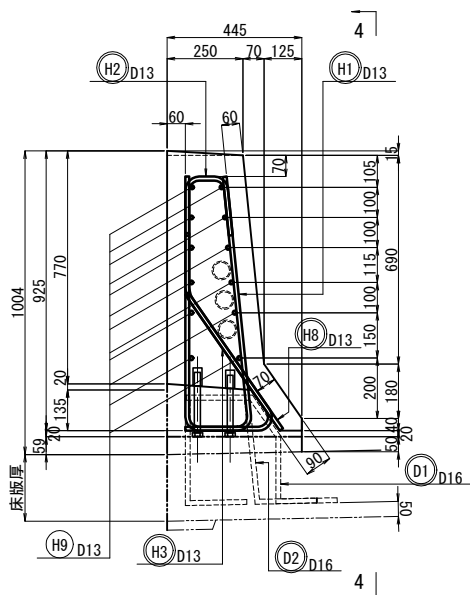

断面図
2 - 2

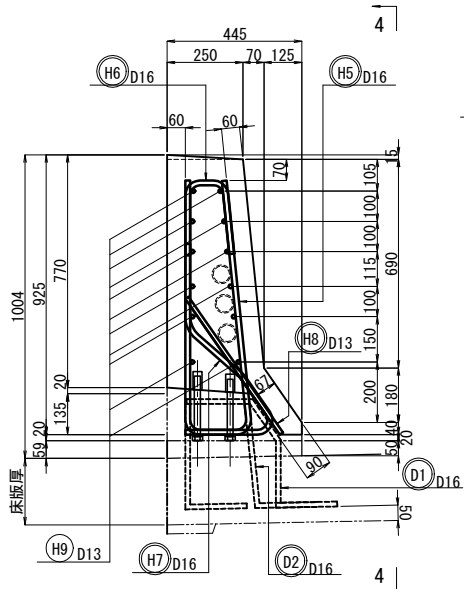


断面図
3 - 3

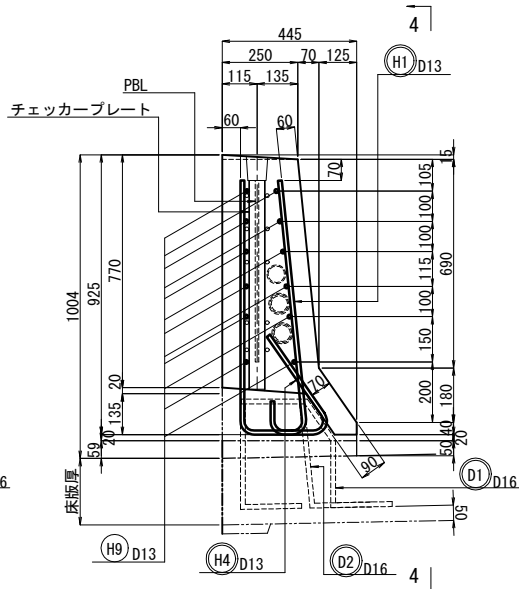


[路肩側 L-E3-0M]
(P23-P24径間 製作数 : 1)








側面図
4 - 4

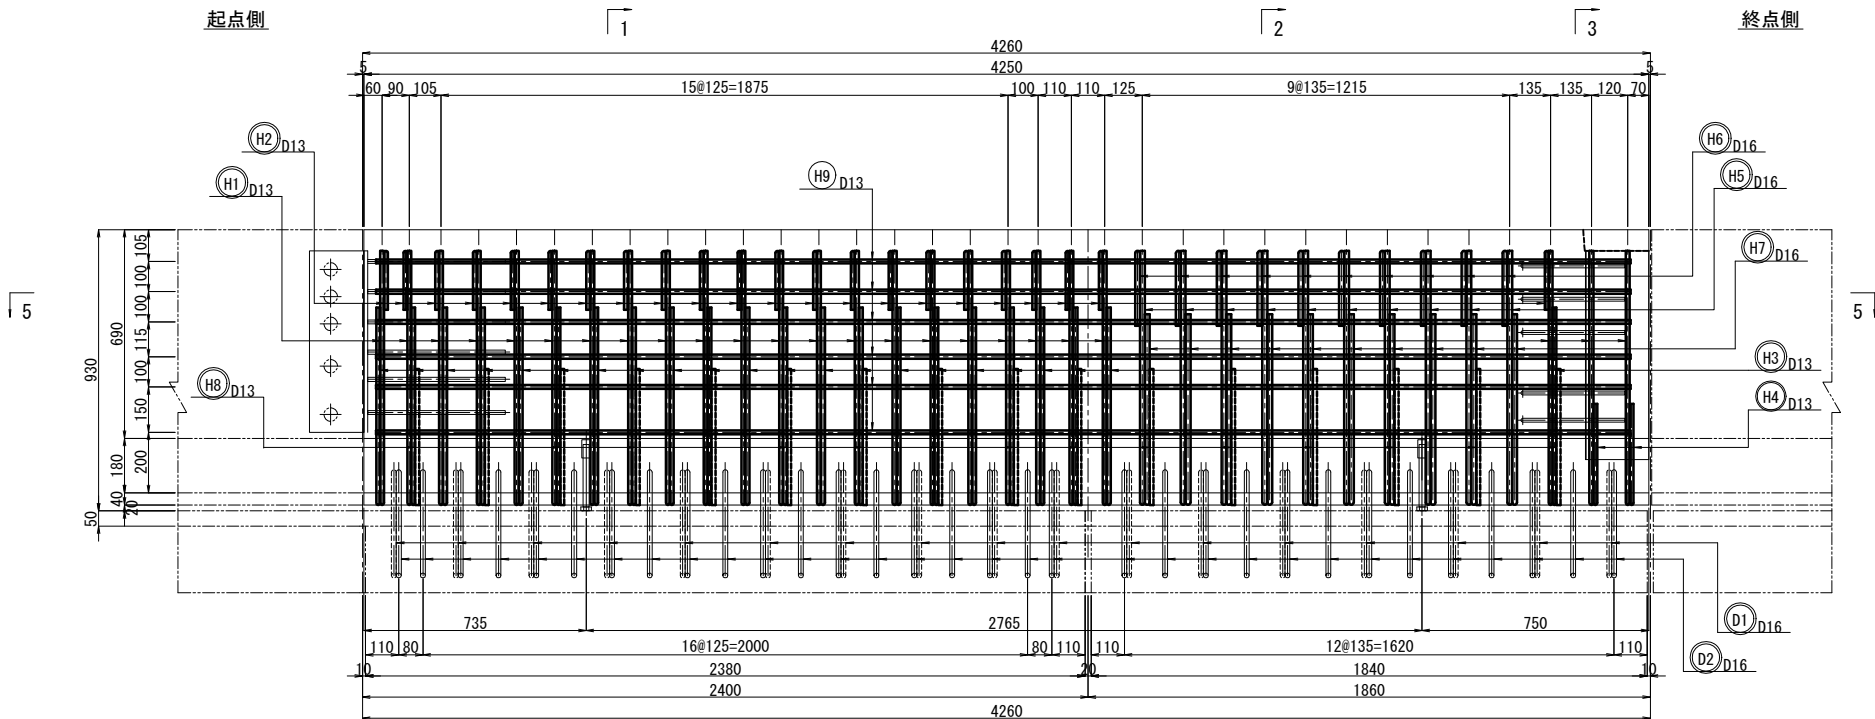

平面図
5 - 5

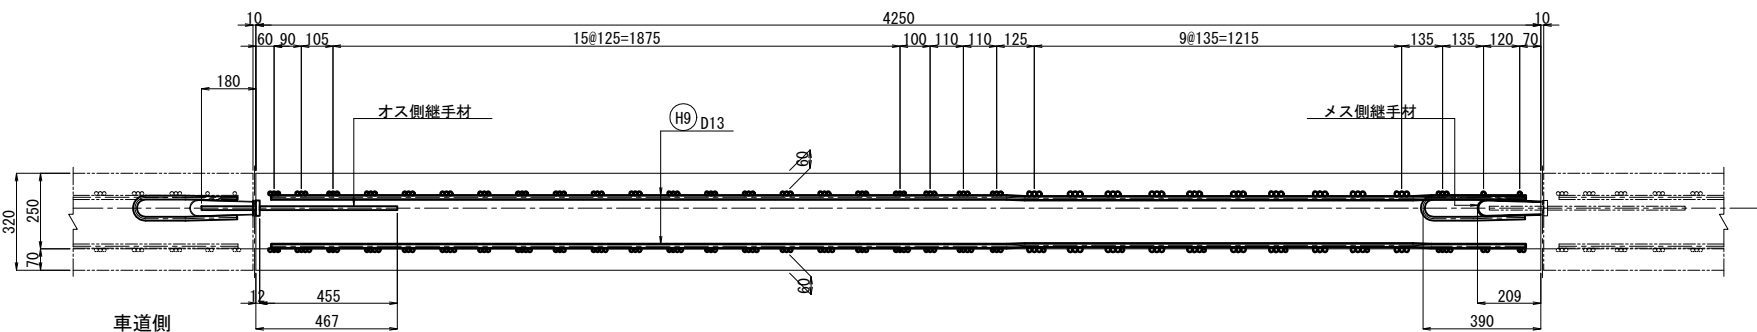

※ 鉄筋記号の○は塗装鉄筋を示す。
※ インサートおよび埋設管などの詳細位置は、壁高欄詳細図(14)を参照のこと。

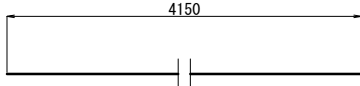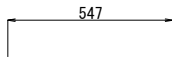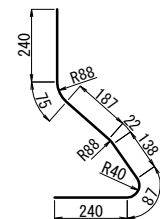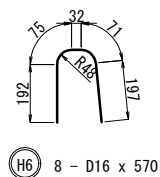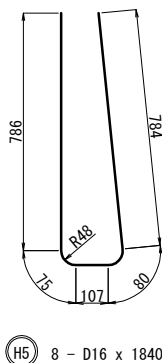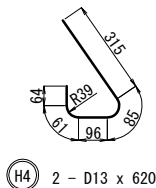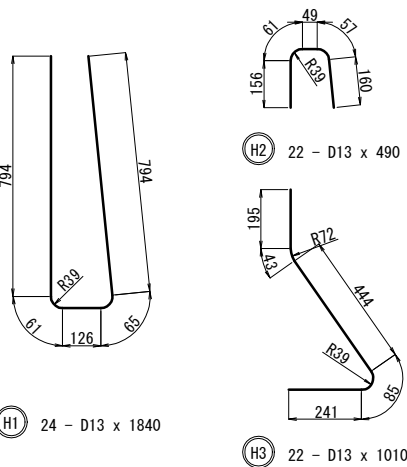

鉄筋表(1ブロック当り)						
鉄筋番号	材質	長さ (mm)	本数 (本)	単位重量 (kg/m)	1本当り質量 (kg)	質量 (kg)
H1	D13	1840	24	0.995	1.831	44
H2	D13	490	22	0.995	0.488	11
H3	D13	1010	22	0.995	1.005	22
H4	D13	620	2	0.995	0.627	1
H5	D16	1840	10	1.56	2.870	29
H6	D16	570	10	1.56	0.889	9
H7	D16	990	10	1.56	1.544	15
H8	D13	550	16	0.995	0.547	9
H9	D13	4150	12	0.995	4.129	50
合 計						190 kg
鉄筋質量集計(SD345)						
		普通鉄筋		塗装鉄筋		
D16		0 kg		53 kg		53 kg
D13		50 kg		87 kg		137 kg
合計		50 kg		140 kg		190 kg

道央自動車道 千歳川大橋(下り線) 床版取替工事			
図面の種類	千歳川大橋(下り線) P18-P24 プレキャスト壁高欄詳細図(13)		
縮 尺	図 示	図面番号	/
設計会社名	戸田建設株式会社		
施工会社名	戸田建設株式会社		
事務所名	東日本高速道路株式会社 北海道支社 札幌管理事務所		

千歳川大橋(下り線) P18-P24 プレキャスト壁高欄詳細図(14)


S=1:25

[路肩側 L-E3-0M]


(P23-P24径間 製作数 : 1)

断面図


1 - 1

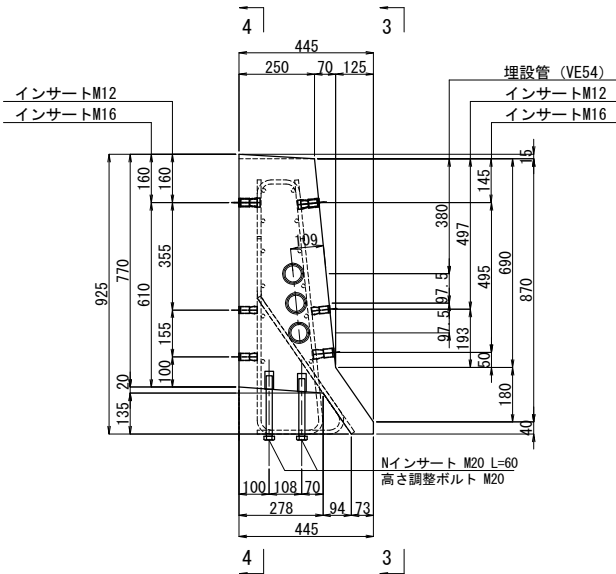


2 - 2

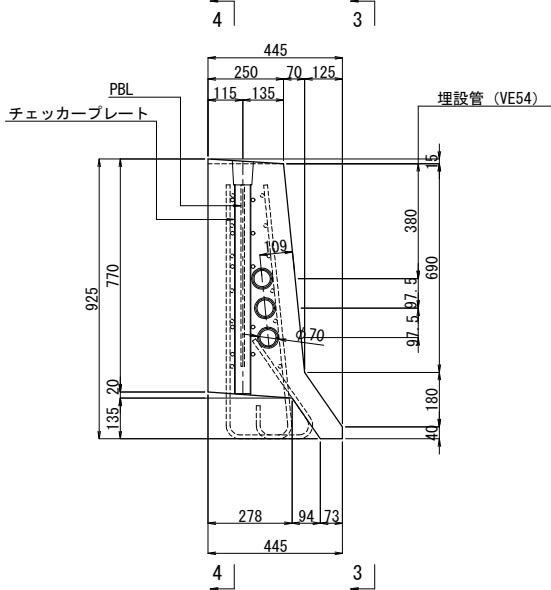

インサート配置側面図

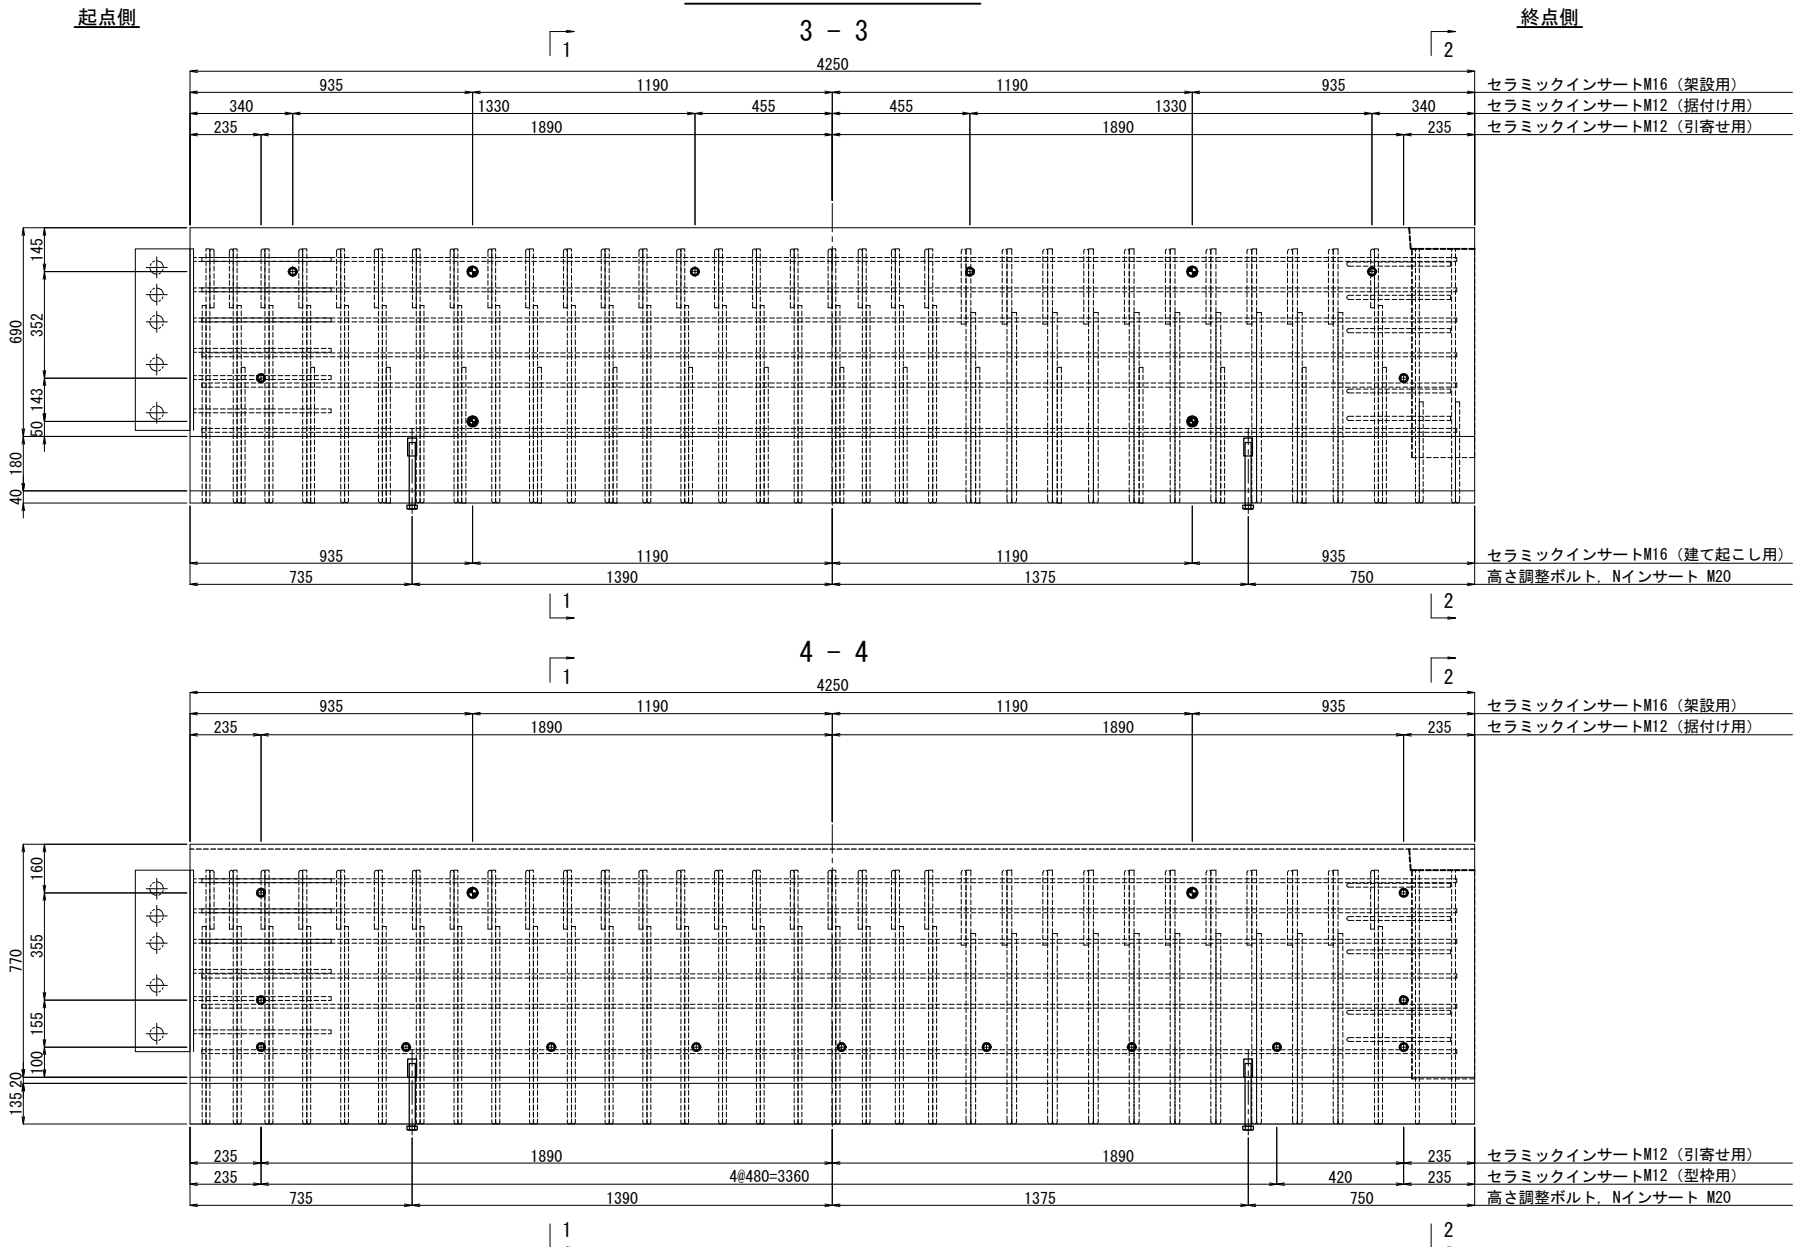

埋設管配置側面図

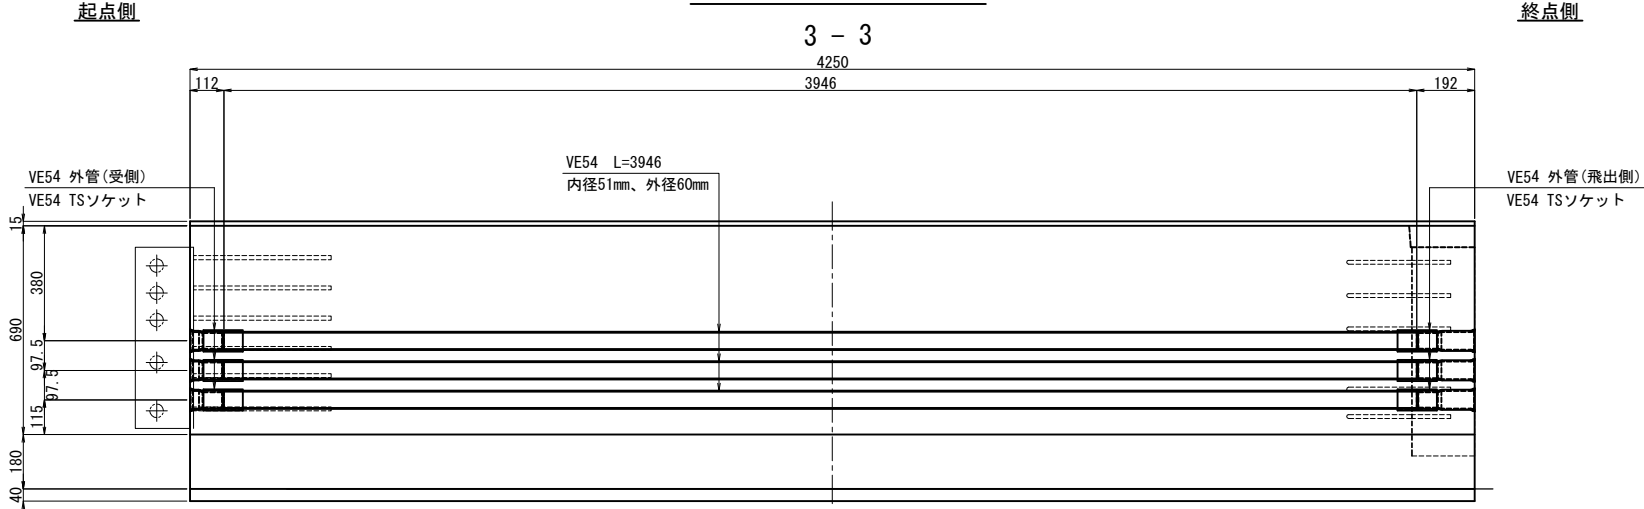


道央自動車道 千歳川大橋(下り線) 床版取替工事			
図面の種類	千歳川大橋(下り線) P18-P24 プレキャスト壁高欄詳細図(14)		
縮 尺	図 示	図面番号	/
設計会社名	戸田建設株式会社		
施工会社名	戸田建設株式会社		
事務所名	東日本高速道路株式会社 北海道支社 札幌管理事務所		


S=1 : 25

(P18-P19径間 製作数 : 1) (P19-P20径間 製作数 : 1)
(P21-P22径間 製作数 : 1)

1 - 1

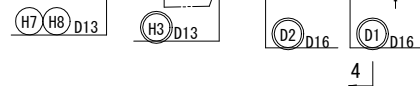


2 - 2

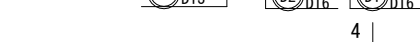


3 - 3





4 - 4

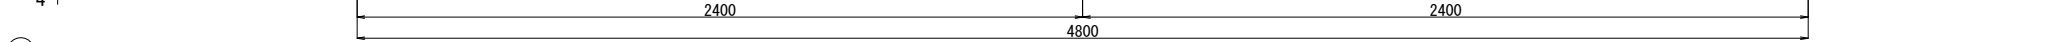

5 - 5

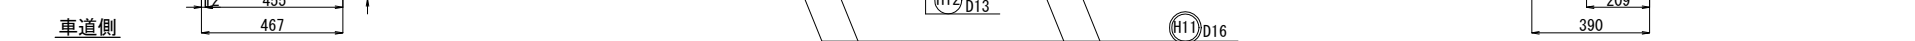

※ インサートおよび埋設管などの詳細位置は、壁高欄詳細図(16)を参照のこと。

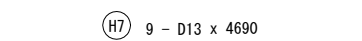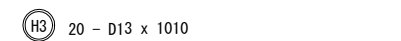

道央自動車道 千歳川大橋（下り線）床版取替工事			
図面の種類	千歳川大橋（下り線）P18-P24 プレキャスト壁高欄詳細図(15)		
縮 尺	図 示	図面番号	/
設計会社名	戸田建設株式会社		
施工会社名	戸田建設株式会社		
事務所名	東日本高速道路株式会社 北海道支社 札幌管理事務所		

千歳川大橋(下り線) P18-P24 プレキャスト壁高欄詳細図(16)

S=1:25


[路肩側 L-48-0M-SP]

(P18-P19径間 製作数 : 1) (P19-P20径間 製作数 : 1)
(P21-P22径間 製作数 : 1)

※スノーボール用アンカーの埋込深さについては共通詳細図(9)を参照のこと。
※視線誘導標本体用のアンカーは、製作時には設置しないことに留意する。

断面図


1 - 1

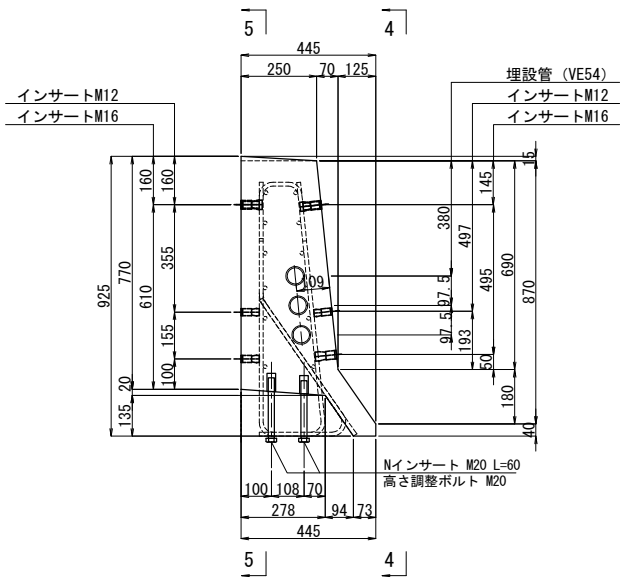

視線誘導標および落下防止装置


起点側

起点側

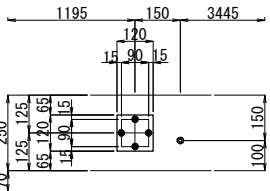

スノーボール


起点側

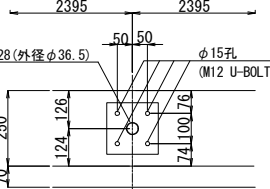

インサート配置側面図

4 - 4

終点側

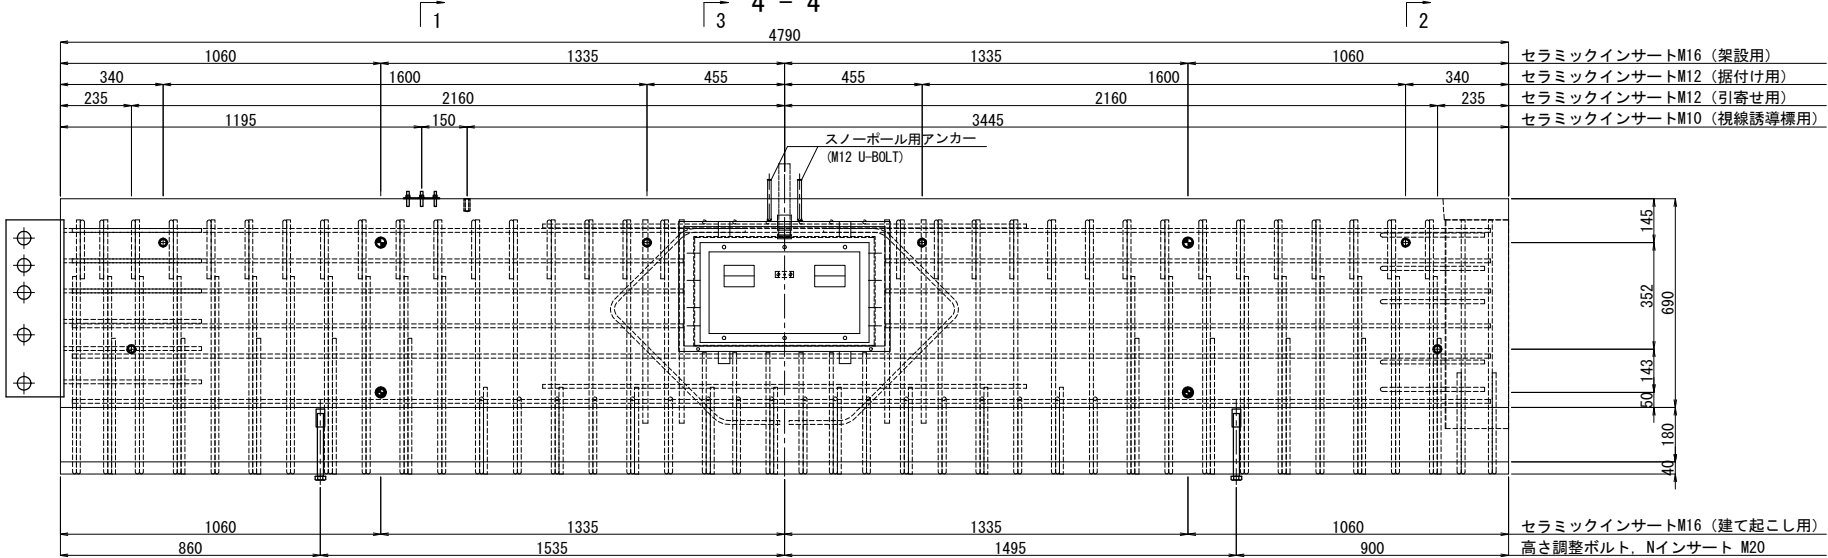

1

3

2

1

3

2

2 - 2

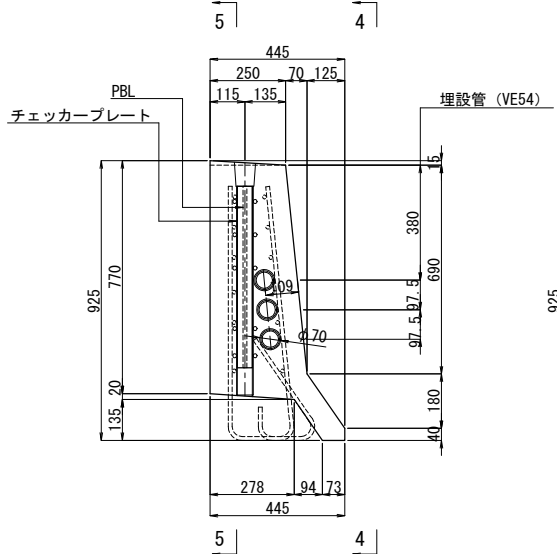

3 - 3

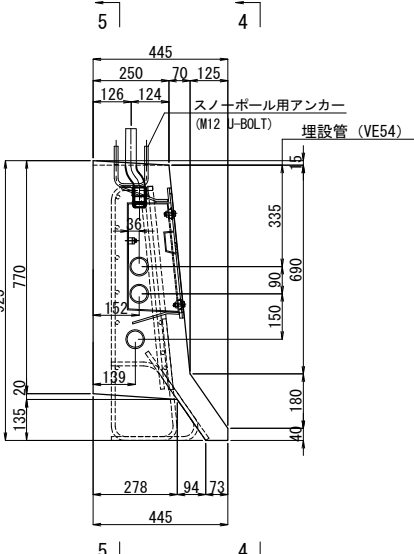


埋設管配置側面図

4 - 4

終点側

起点側

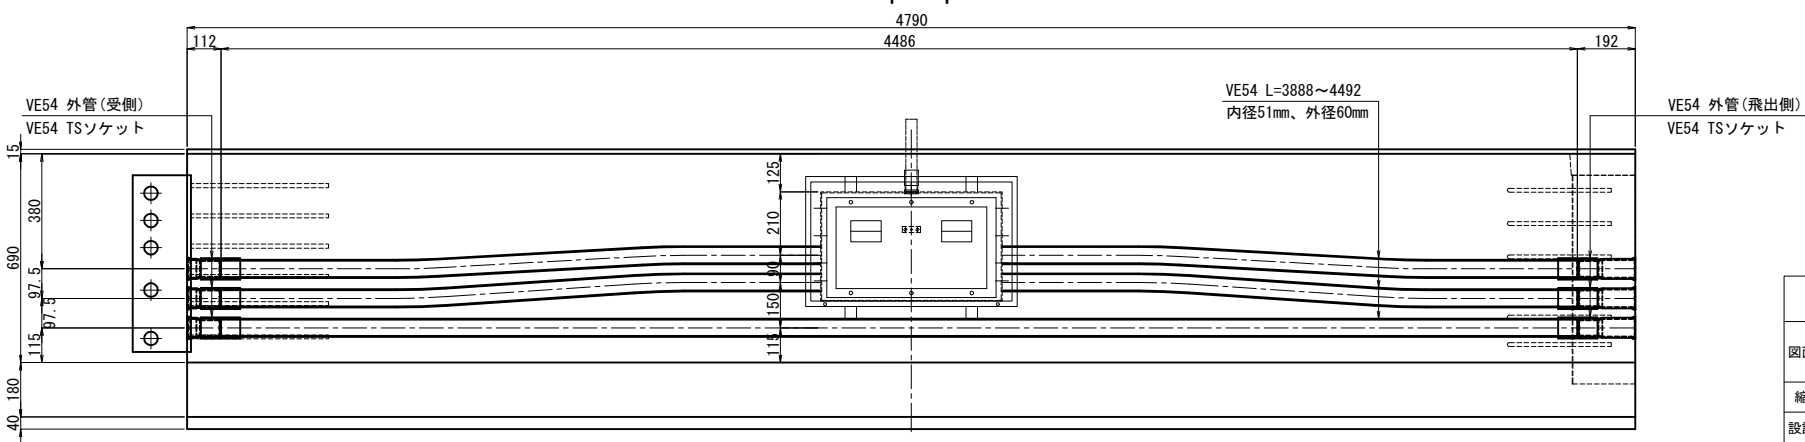

鉄筋表(1ブロック当り)

鉄筋番号	材質	長さ (mm)	本数 (本)	単位重量 (kg/m)	1本当り質量 (kg)	質量 (kg)	備考
H1	D13	1840	34	0.995	1.831	62	EP塗装
H2	D13	490	32	0.995	0.488	16	EP塗装
H3	D13	1010	20	0.995	1.005	20	EP塗装
H4	D13	620	2	0.995	0.617	1	EP塗装
H5	D13	550	10	0.995	0.547	5	EP塗装
H6	D13	350	9	0.995	0.348	3	EP塗装
H7	D13	4690	9	0.995	4.667	42	
H8	D13	2000	6	0.995	1.990	12	
H9	D13	1510	6	0.995	1.502	9	EP塗装
H10	D13	700	18	0.995	0.697	13	EP塗装
H11	D16	680	4	1.56	1.061	4	EP塗装
H12	D13	1600	2	0.995	1.592	3	
H13	D13	1270	2	0.995	1.264	3	
合 計						193	kg
鉄筋質量集計(SD345)							
				普通鉄筋	塗装鉄筋		
				D16	0 kg	4 kg	4 kg
				D13	60 kg	129 kg	189 kg
合計				60 kg	133 kg	193 kg	

道央自動車道 千歳川大橋(下り線)床版取替工事			
図面の種類	千歳川大橋(下り線) P18-P24 プレキャスト壁高欄詳細図(16)		
縮 尺	図 示	図面番号	/
設計会社名	戸田建設株式会社		
施工会社名	戸田建設株式会社		
事務所名	東日本高速道路株式会社 北海道支社 札幌管理事務所		

千歳川大橋(下り線) P18-P24 プレキャスト壁高欄詳細図(18)


S=1:25

[路肩側 L-48-0F-SP]


(P22-P23径間 製作数 : 1)

断面図

1 - 1

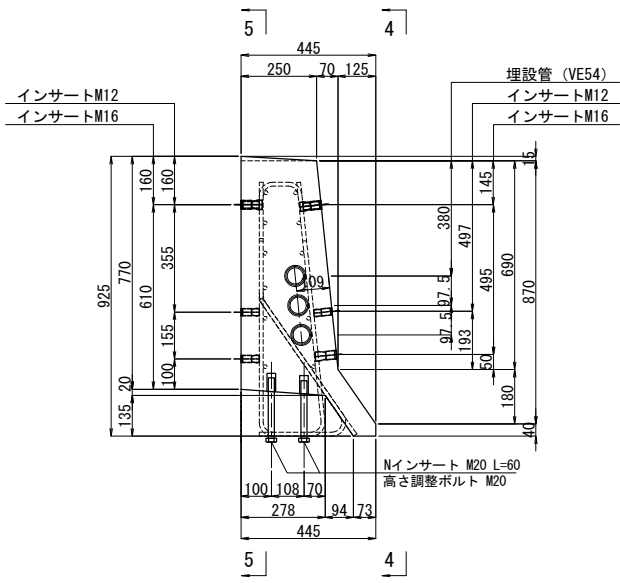


2 - 2

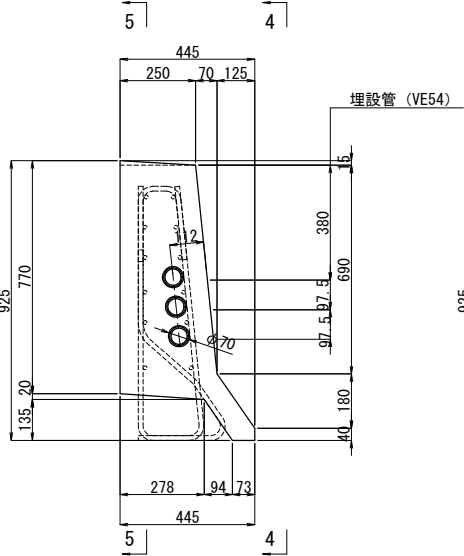

視線誘導標および落下防止装置


起点側

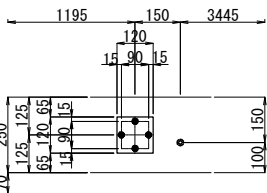


起点側

スノーボール

起点側

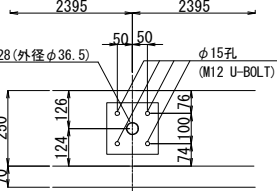


3 - 3

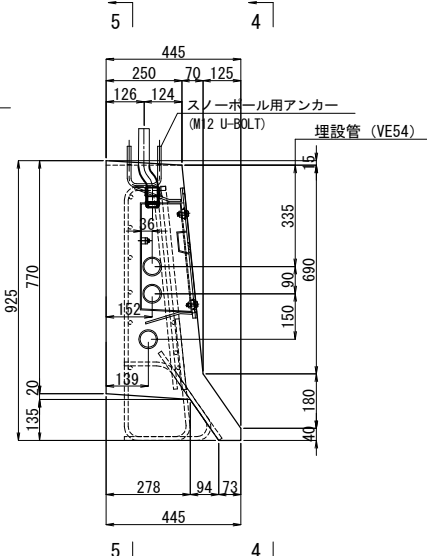

インサート配置側面図

4 - 4

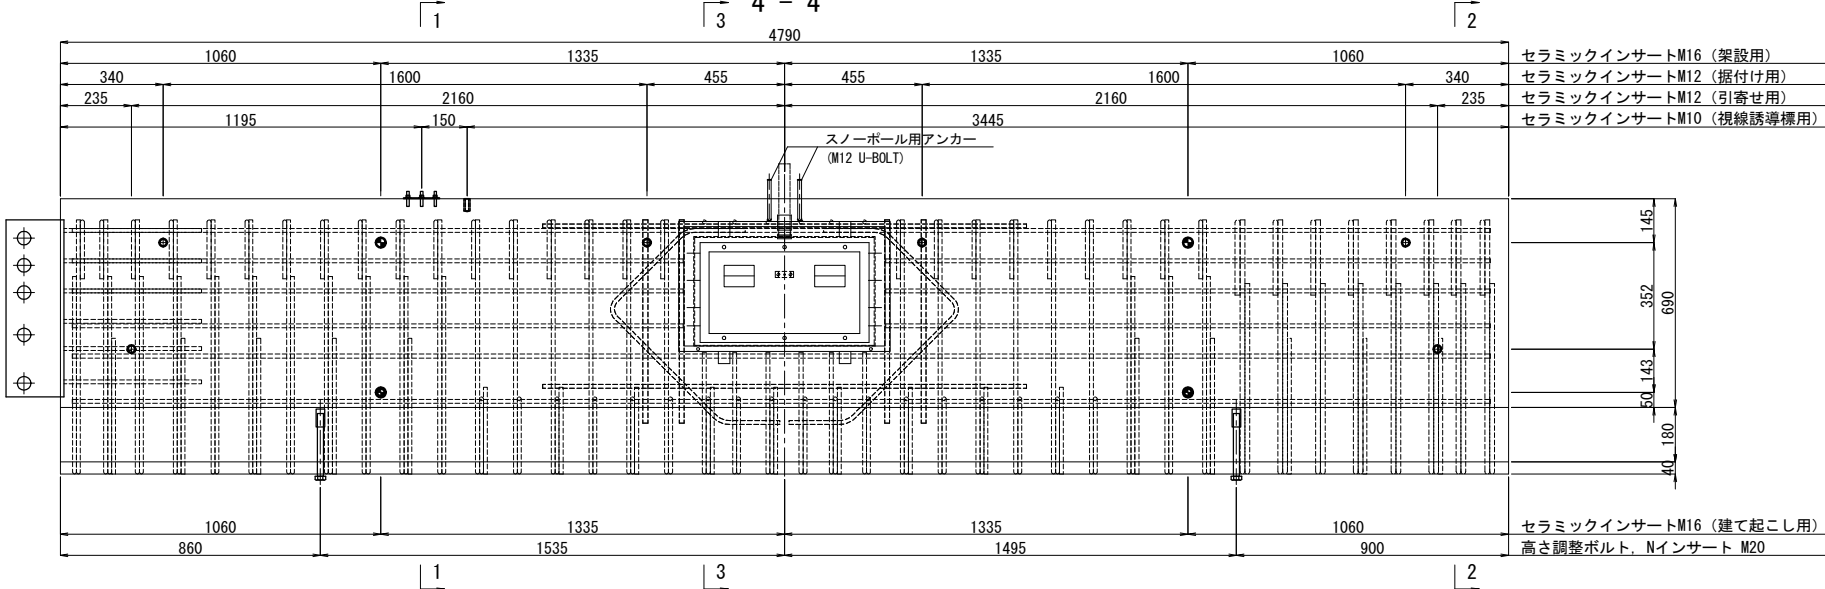

1

3

2

1

3

2

鉄筋表 (1ブロック当り)

鉄筋番号	材質	長さ (mm)	本数 (本)	単位重量 (kg/m)	1本当り質量 (kg)	質量 (kg)	備考
H1	D13	1840	26	0.995	1.831	48	EP塗装
H2	D13	490	26	0.995	0.488	13	EP塗装
H3	D13	1010	14	0.995	1.005	14	EP塗装
H4	D16	1840	8	1.56	2.870	23	EP塗装
H5	D16	570	8	1.56	0.889	7	EP塗装
H6	D16	990	8	1.56	1.544	12	EP塗装
H7	D13	550	10	0.995	0.547	5	EP塗装
H8	D13	350	9	0.995	0.348	3	EP塗装
H9	D13	4690	9	0.995	4.667	42	
H10	D13	2000	6	0.995	1.990	12	
H11	D13	1510	6	0.995	1.502	9	EP塗装
H12	D13	700	18	0.995	0.697	13	EP塗装
H13	D16	680	4	1.56	1.061	4	EP塗装
H14	D13	1600	2	0.995	1.592	3	
H15	D13	1270	2	0.995	1.264	3	
合 計						211 kg	
鉄筋質量集計 (SD345)							
				普通鉄筋	塗装鉄筋		
				D16	0 kg	46 kg	46 kg
				D13	60 kg	105 kg	165 kg
合計				60 kg	151 kg	211 kg	

埋設管配置側面図

4 - 4

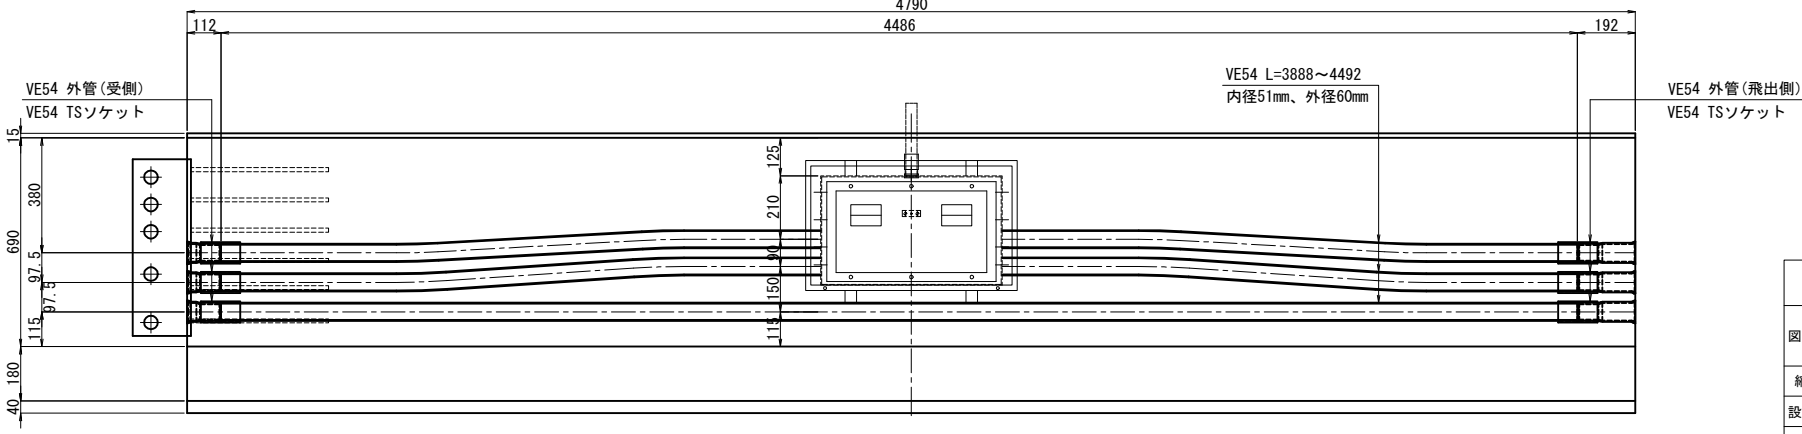

※スノーボール用アンカーの埋込深さについては共通詳細図(9)を参照のこと。
※視線誘導標本体用のアンカーは、製作時には設置しないことに留意する。

終点側

セラミックインサートM16 (架設用)
セラミックインサートM12 (据付け用)
セラミックインサートM10 (視線誘導標用)

セラミックインサートM16 (建て起こし用)
高さ調整ボルト、Nインサート M20


セラミックインサートM16 (架設用)
セラミックインサートM12 (据付け用)

セラミックインサートM12 (引寄せ用)
セラミックインサートM12 (型枠用)
高さ調整ボルト、Nインサート M20


道央自動車道 千歳川大橋(下り線) 床版取替工事			
図面の種類	千歳川大橋(下り線) P18-P24 プレキャスト壁高欄詳細図(18)		
縮 尺	図 示	図面番号	/
設計会社名	戸田建設株式会社		
施工会社名	戸田建設株式会社		
事務所名	東日本高速道路株式会社 北海道支社 札幌管理事務所		

S=1 : 25








断面図
1 - 1

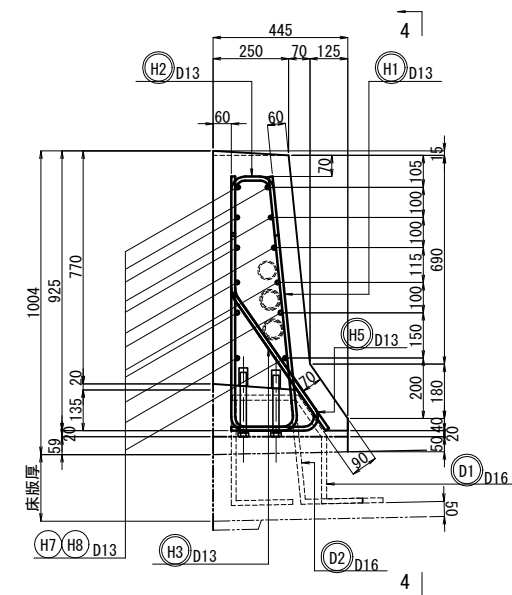

断面図
2 - 2

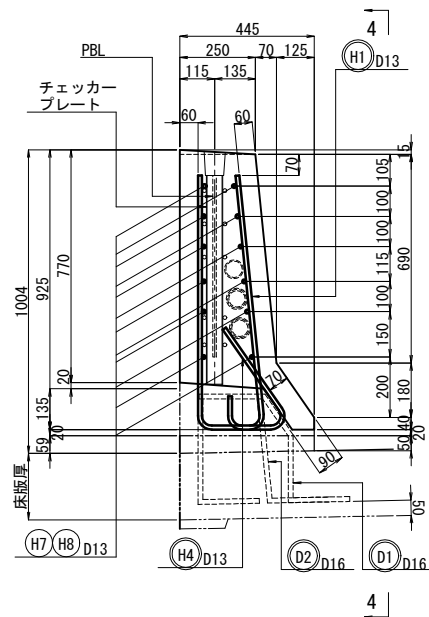


断面図
3 - 3

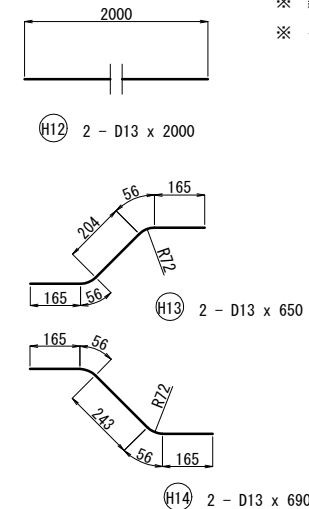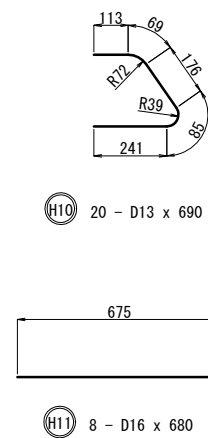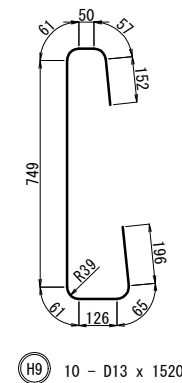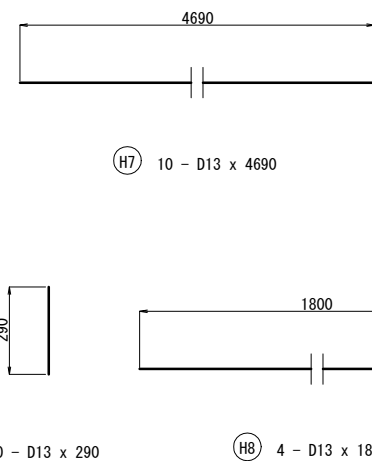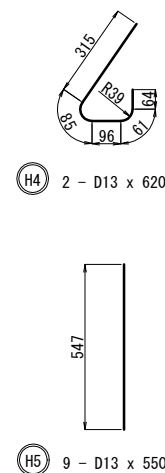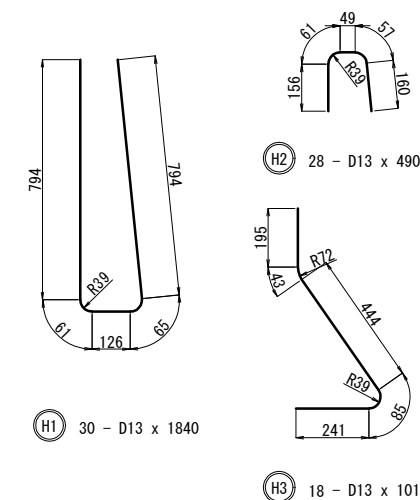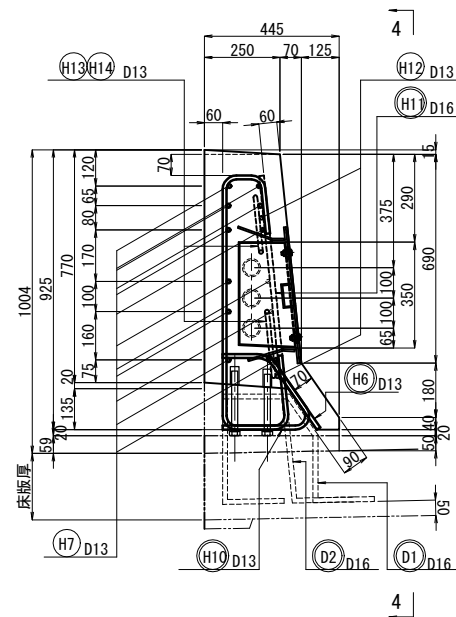


※ 鉄筋記号の  は塗装鉄筋を示す。

※ インサートおよび埋設管などの詳細位置は、壁高欄詳細図(20)を参照のこと。

側面図
4 - 4

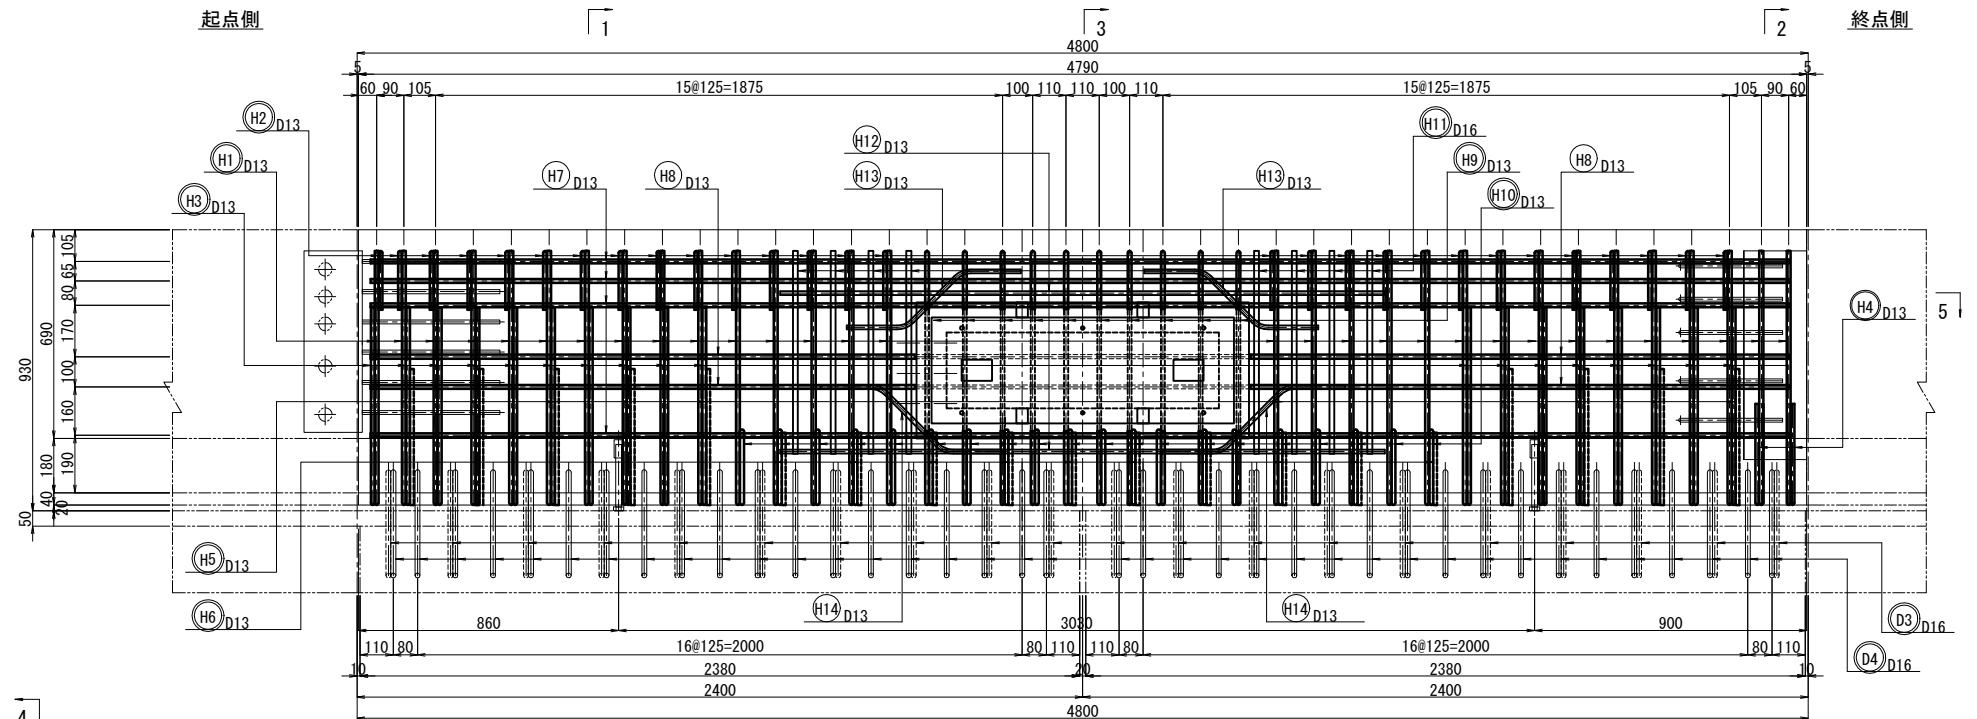

平面图
5 - 5

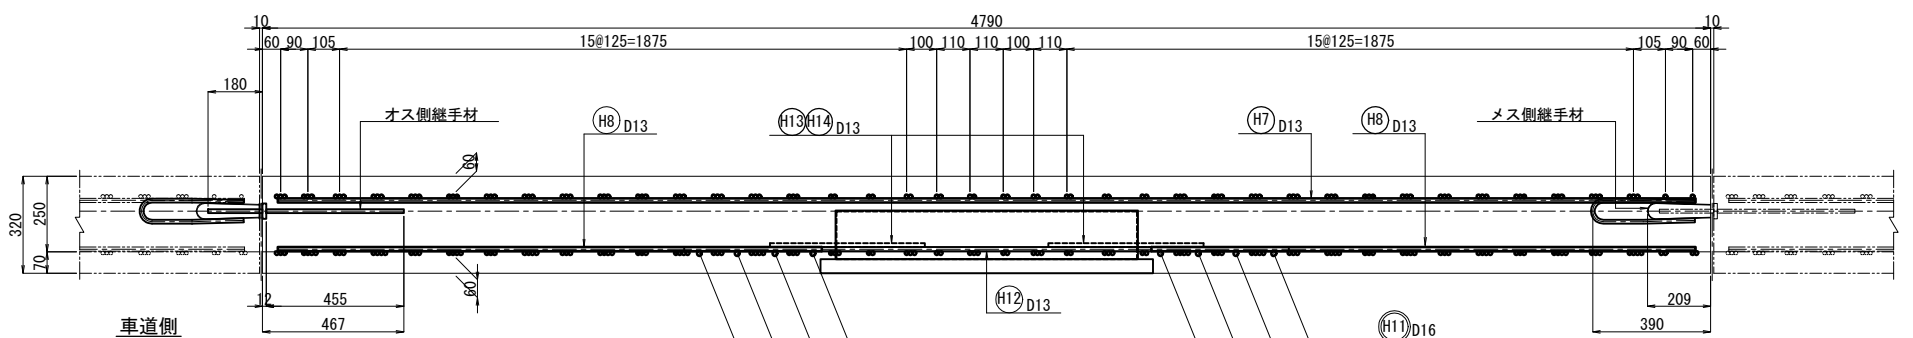


道央自動車道 千歳川大橋（下り線）床版取替工事			
図面の種類	千歳川大橋（下り線）P18-P24 プレキャスト壁高欄詳細図(19)		
縮 尺	図 示	図面番号	/
設計会社名	戸田建設株式会社		
施工会社名	戸田建設株式会社		
事務所名	東日本高速道路株式会社 北海道支社 札幌管理事務所		


S=1 : 25

(P19-P20径間 製作数 : 1) (P22-P23径間 製作数 : 1)


1 - 1

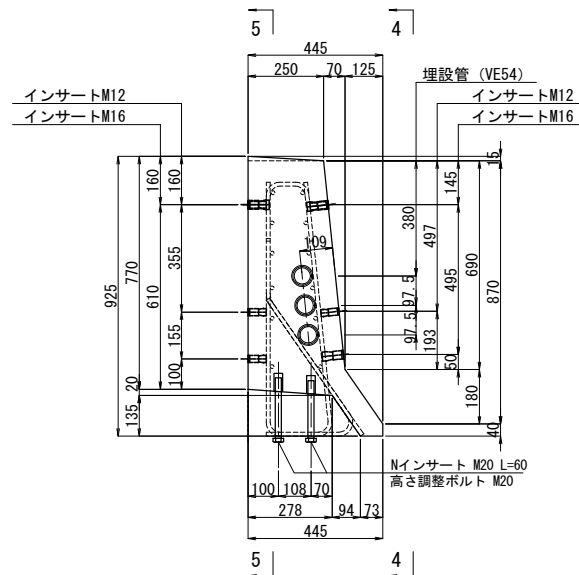


3 - 3

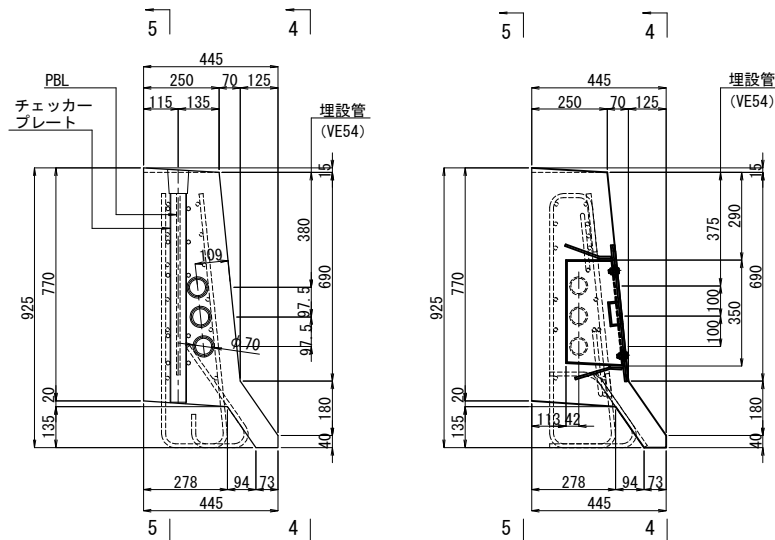


終点側

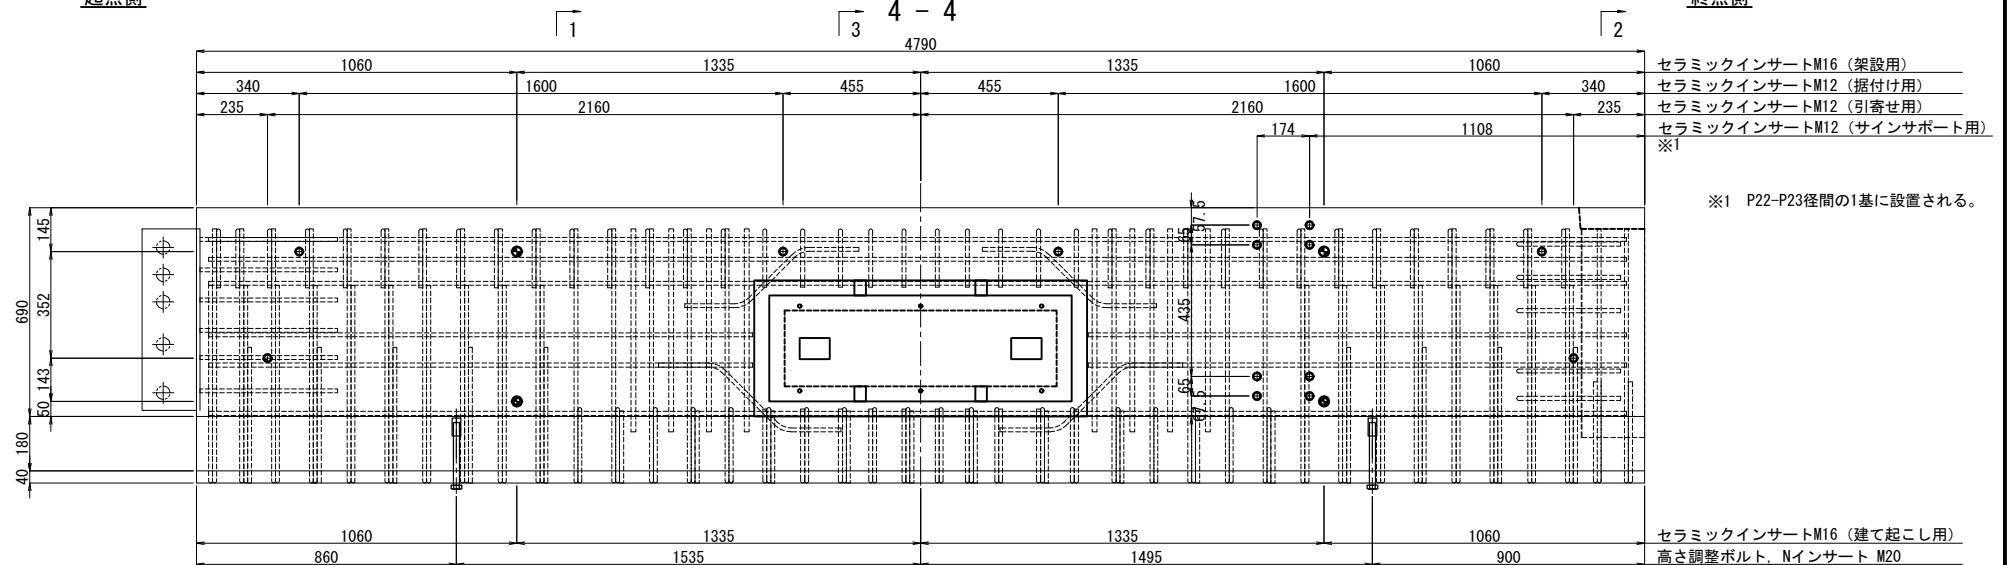

埋設管配置側面図

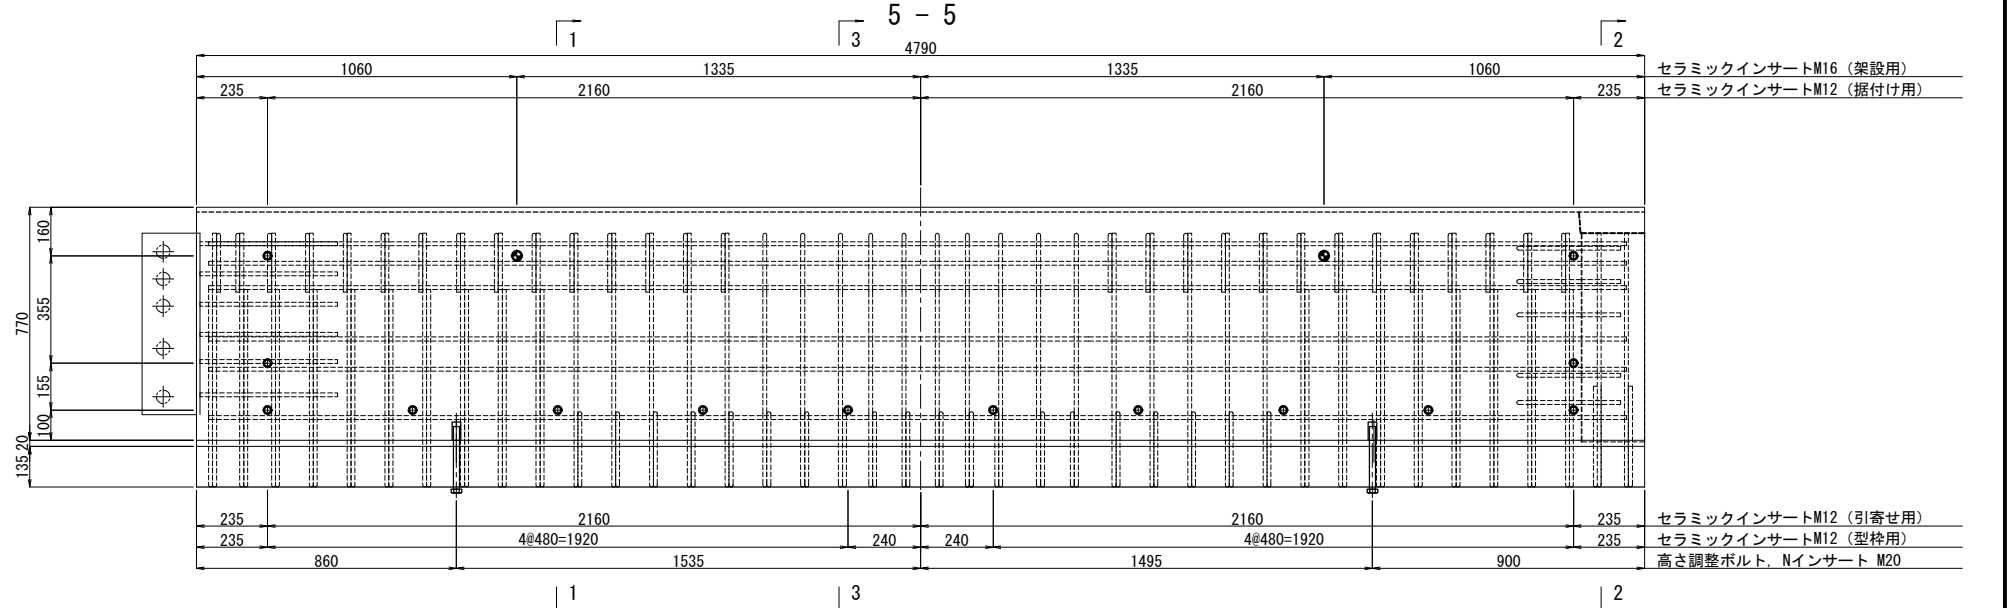

終点側

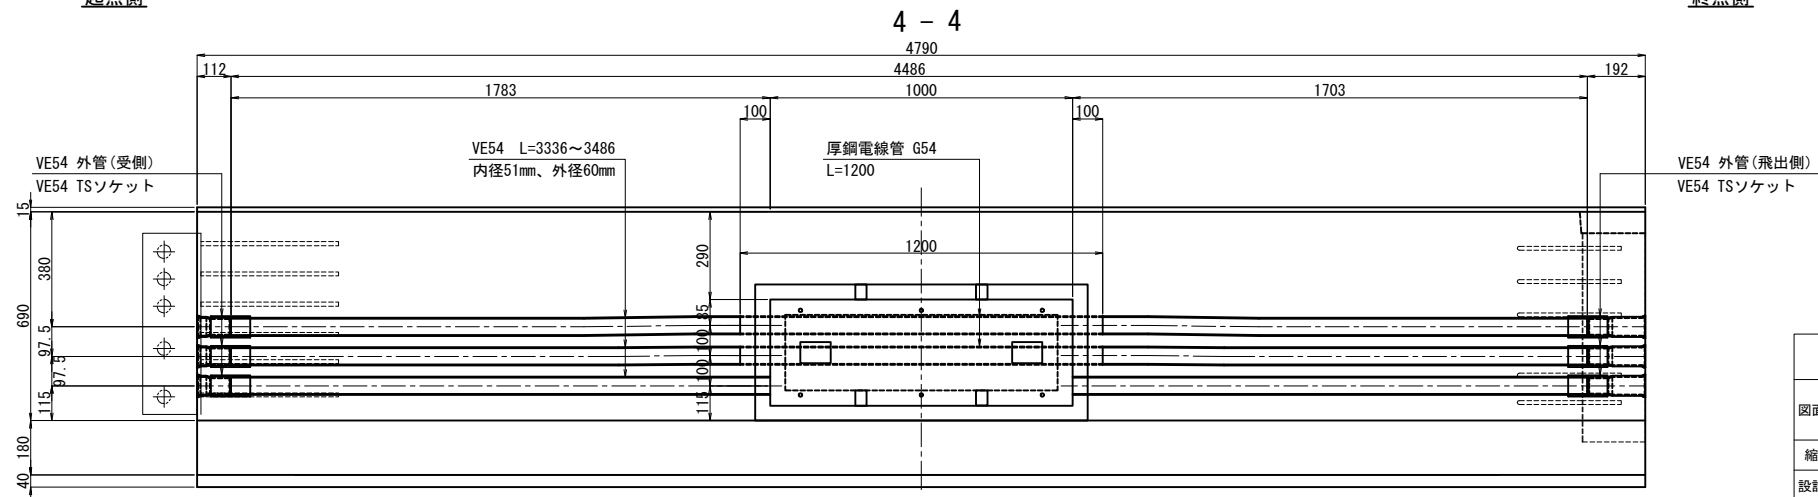


鉄筋番号	材質	長さ (mm)	本数 (本)	単位重量 (kg/m)	1本当たり質量 (kg)	質 量 (kg)	備考
H1	D13	1840	30	0.995	1.831	55	EP塗装
H2	D13	490	28	0.995	0.488	14	EP塗装
H3	D13	1010	18	0.995	1.005	18	EP塗装
H4	D13	630	2	0.995	0.627	1	EP塗装
H5	D13	550	9	0.995	0.547	5	EP塗装
H6	D13	290	10	0.995	0.289	3	EP塗装
H7	D13	4690	10	0.995	4.667	47	
H8	D13	1800	4	0.995	1.791	7	
H9	D13	1520	10	0.995	1.512	15	EP塗装
H10	D13	690	20	0.995	0.687	14	EP塗装
H11	D16	680	8	1.56	1.061	8	EP塗装
H12	D13	2000	2	0.995	1.990	4	
H13	D13	650	2	0.995	0.647	1	
H14	D13	690	2	0.995	0.687	1	
合 計						193	kg
鉄筋質量集計 (SD345)							
				普通鉄筋	塗装鉄筋		
				D16	0 kg	8 kg	8 kg
				D13	60 kg	125 kg	185 kg
				合計	60 kg	133 kg	193 kg

道央自動車道 千歳川大橋（下り線）床版取替工事			
図面の種類	千歳川大橋（下り線）P18-P24 プレキャスト 壁高欄詳細図 (20)		
縮 尺	図 示	図面番号	/
設計会社名	戸田建設株式会社		
施工会社名	戸田建設株式会社		
事務所名	東日本高速道路株式会社 北海道支社 札幌管理事務所		


S=1 : 25

(P18-P19径間 製作数 : 1)

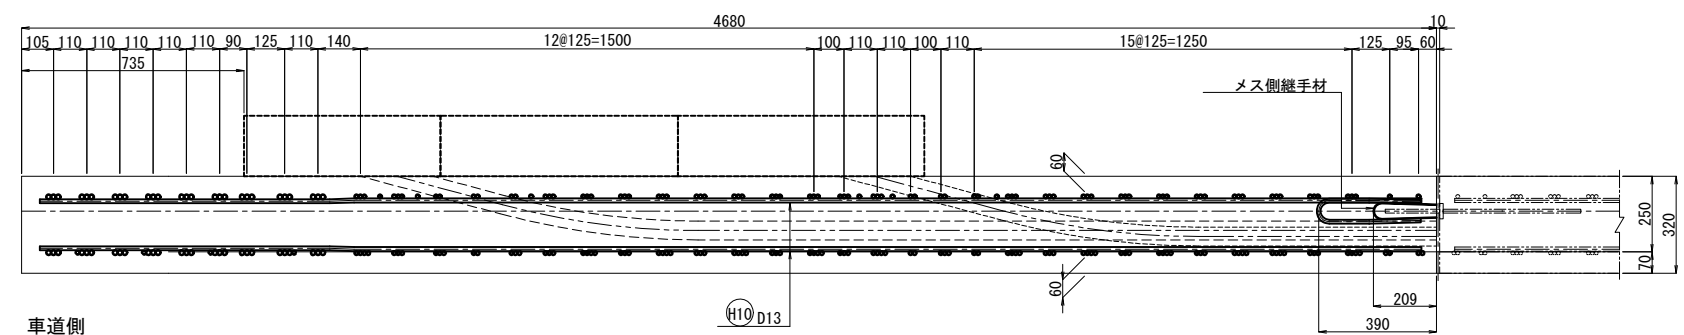

※ 鉄筋記号の  は塗装鉄筋を示す。

※ インサートおよび埋設管などの詳細位置は、壁高欄詳細図(22)を参照のこと。

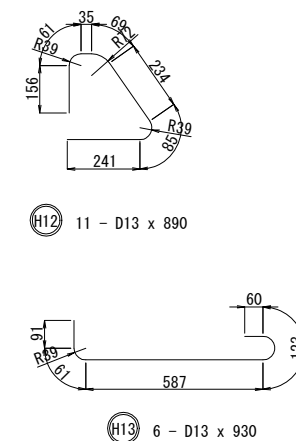

道失自動車道 千歳川大橋（下り線）床版取替工事				
図面の種類	千歳川大橋（下り線）P18-P24 プレキャスト壁高欄詳細図(21)			
縮 尺	図 示	図面番号	/	
設計会社名	戸田建設株式会社			
施工会社名	戸田建設株式会社			
事務所名	東日本高速道路株式会社 北海道支社 札幌管理事務所			

千歳川大橋(下り線) P18-P24 プレキャスト壁高欄詳細図(22)


S=1:25

[路肩側 L-E2-JM-PB]


(P18-P19径間 製作数 : 1)

断面図


1 - 1

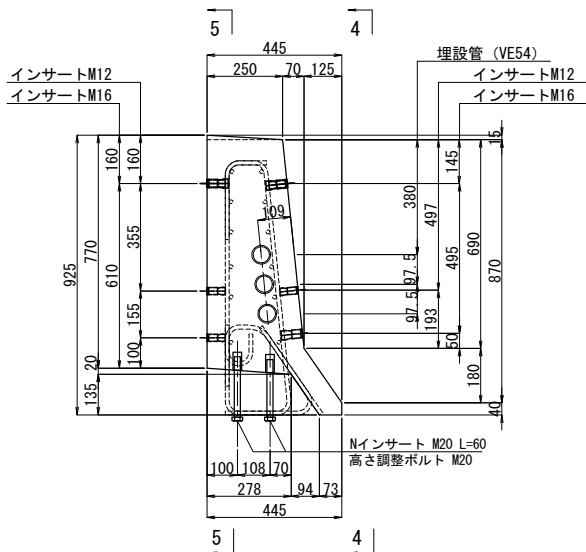

2 - 2

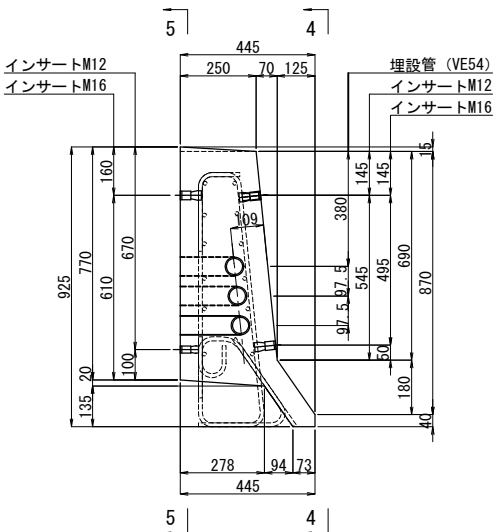

3 - 3

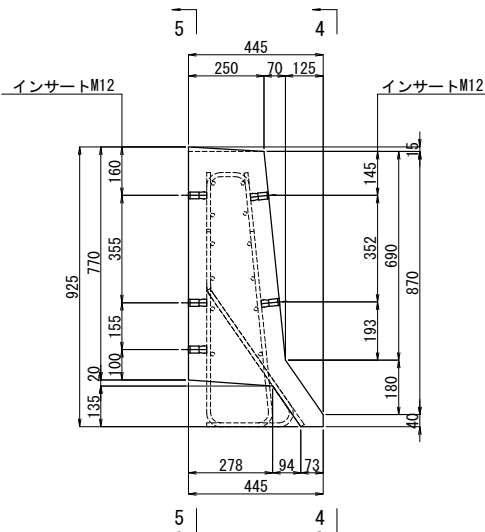


インサート配置側面図


起点側

4 - 4

終点側

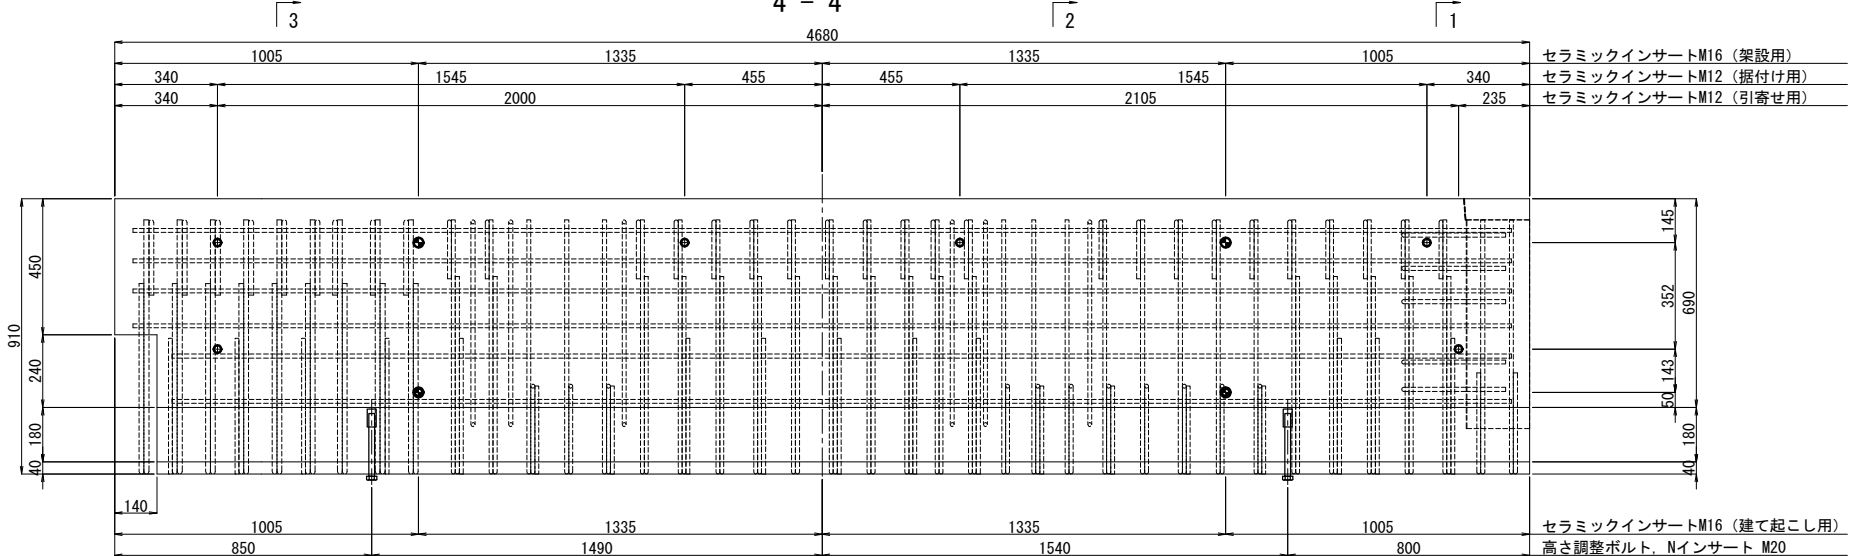

5 - 5

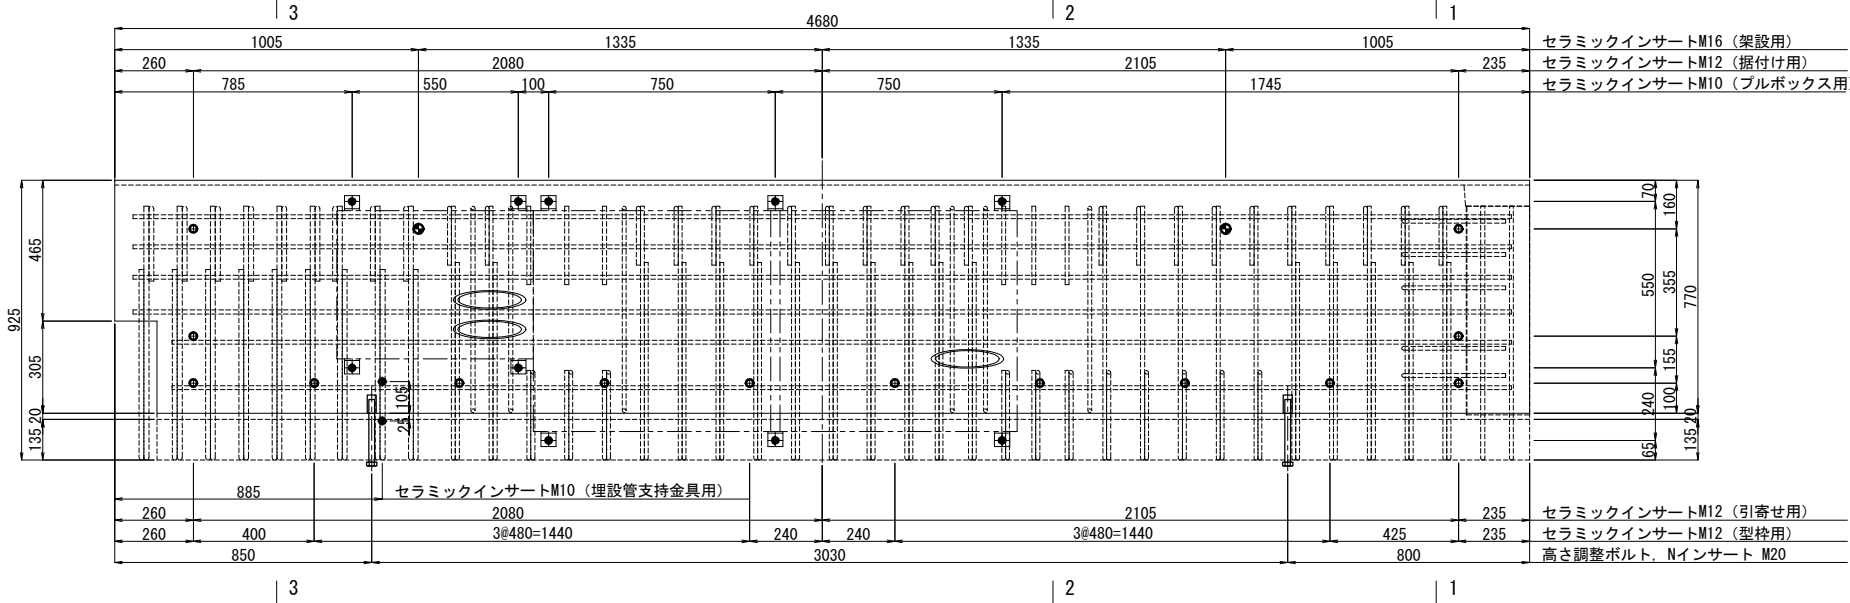


埋設管配置側面図

起点側

5 - 5

終点側

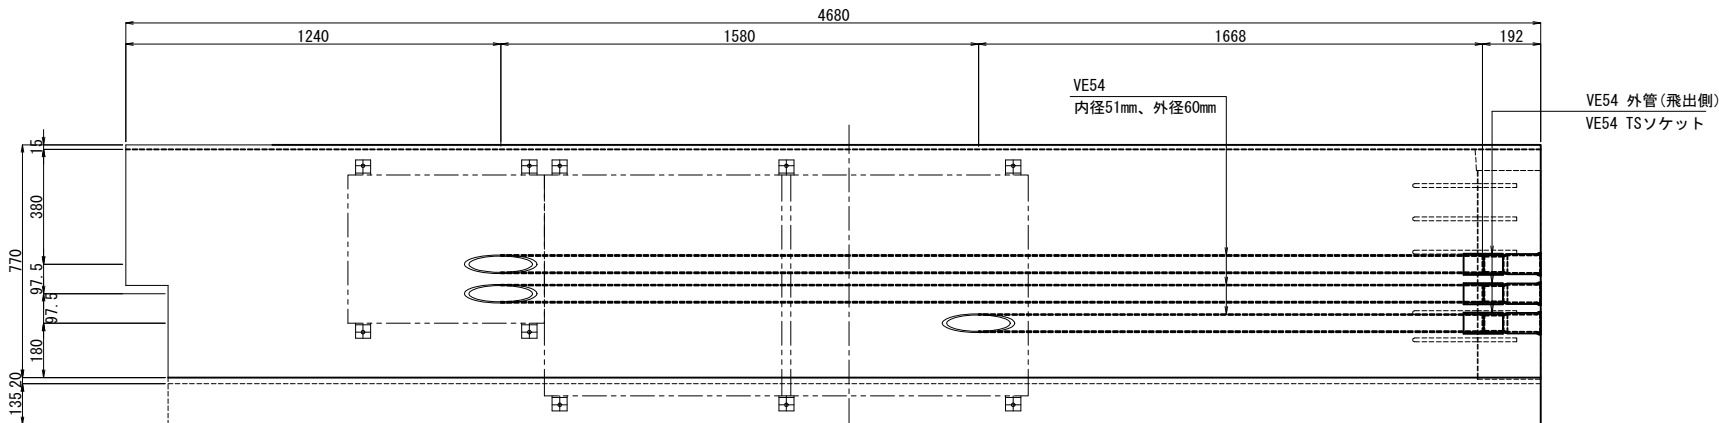


鉄筋表(1ブロック当り)

鉄筋番号	材質	長さ (mm)	本数 (本)	単位重量 (kg/m)	1本当り質量 (kg)	質量 (kg)	備考
H1	D13	1840	24	0.995	1.831	44	EP塗装
H2	D13	490	22	0.995	0.488	11	EP塗装
H3	D13	1010	17	0.995	1.005	17	EP塗装
H4	D13	620	2	0.995	0.617	1	EP塗装
H5	D16	1840	9	1.56	2.870	26	EP塗装
H6	D16	570	9	1.56	0.889	8	EP塗装
H7	D16	990	9	1.56	1.544	14	EP塗装
H8	D13	550	13	0.995	0.547	7	EP塗装
H9	D13	350	6	0.995	0.348	2	EP塗装
H10	D13	4500	12	0.995	4.478	54	
H11	D13	1640	6	0.995	1.632	10	EP塗装
H12	D13	890	11	0.995	0.886	10	EP塗装
H13	D13	930	6	0.995	0.925	6	EP塗装
合 計						210	kg
鉄筋質量集計(SD345)							
				普通鉄筋	塗装鉄筋		
				D16	0 kg	48 kg	48 kg
				D13	54 kg	108 kg	162 kg
				合計	54 kg	156 kg	210 kg



道央自動車道 千歳川大橋(下り線)床版取替工事			
図面の種類	千歳川大橋(下り線) P18-P24 プレキャスト壁高欄詳細図(22)		
縮 尺	図 示	図面番号	/
設計会社名	戸田建設株式会社		
施工会社名	戸田建設株式会社		
事務所名	東日本高速道路株式会社 北海道支社 札幌管理事務所		

S=1:25

終点側



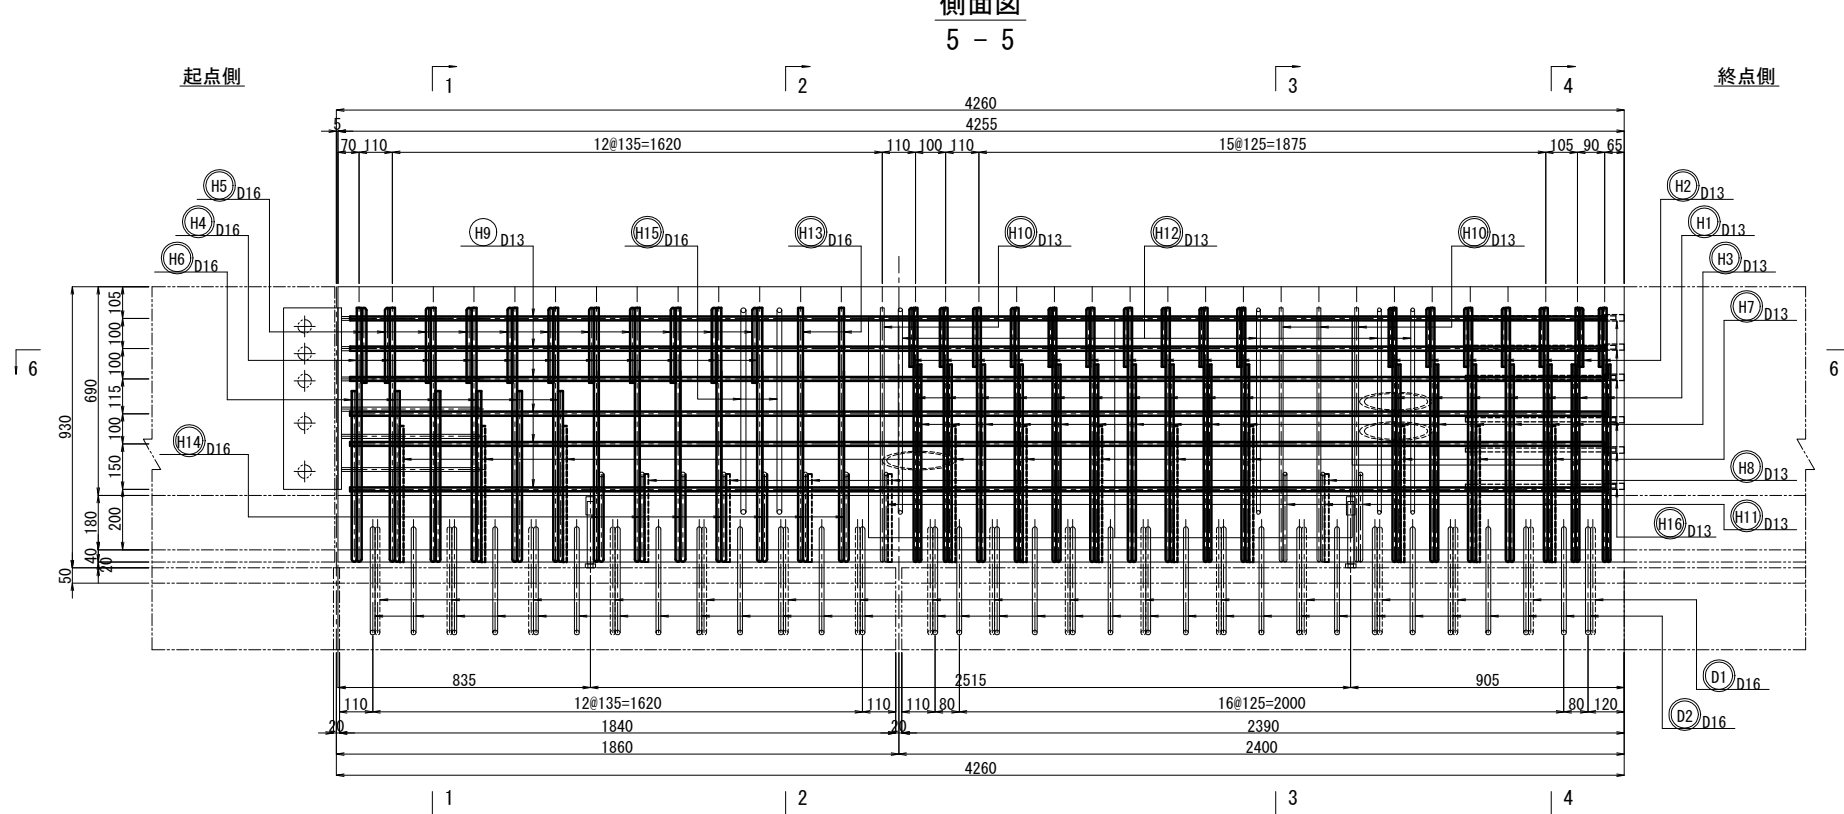


平面図
6 - 6

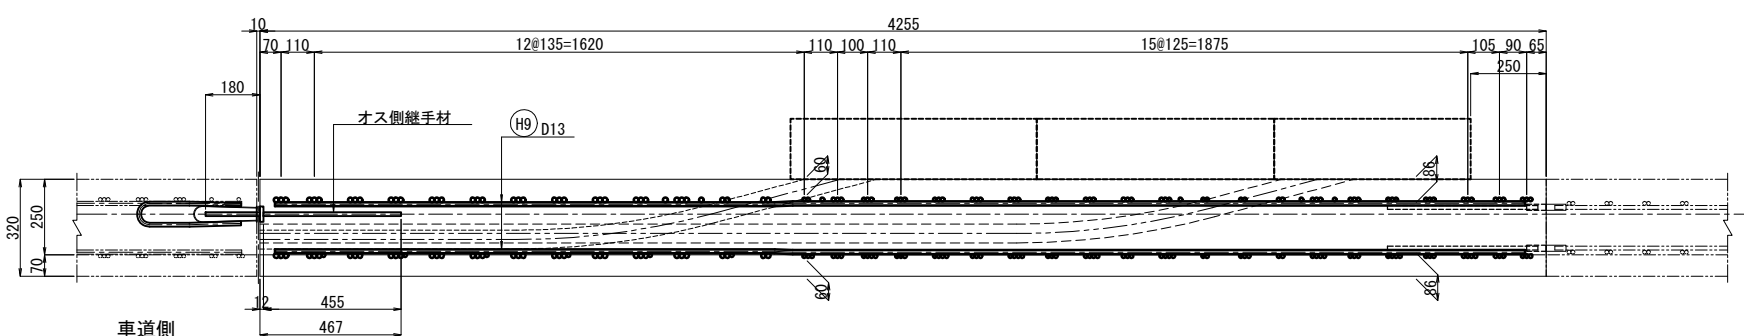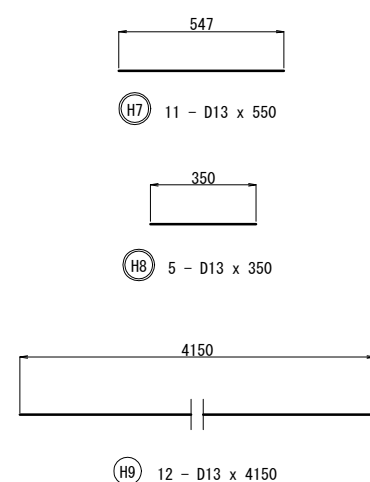

※ 鉄筋記号の は塗装鉄筋を示す。

※ インサートおよび埋設管などの詳細位置は、壁高欄詳細図(24)を参照のこと。

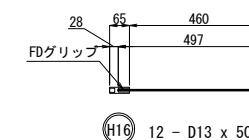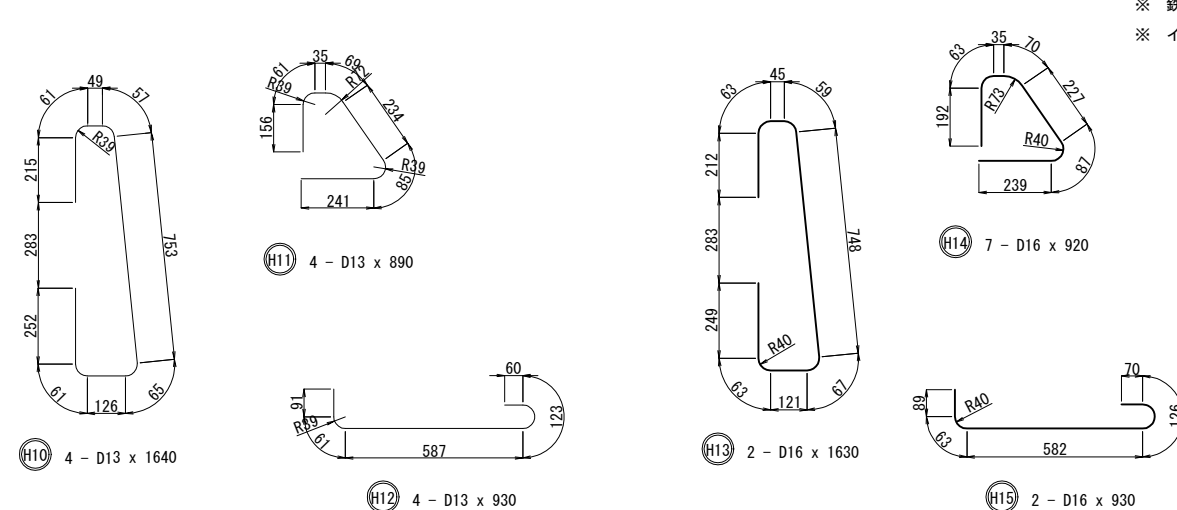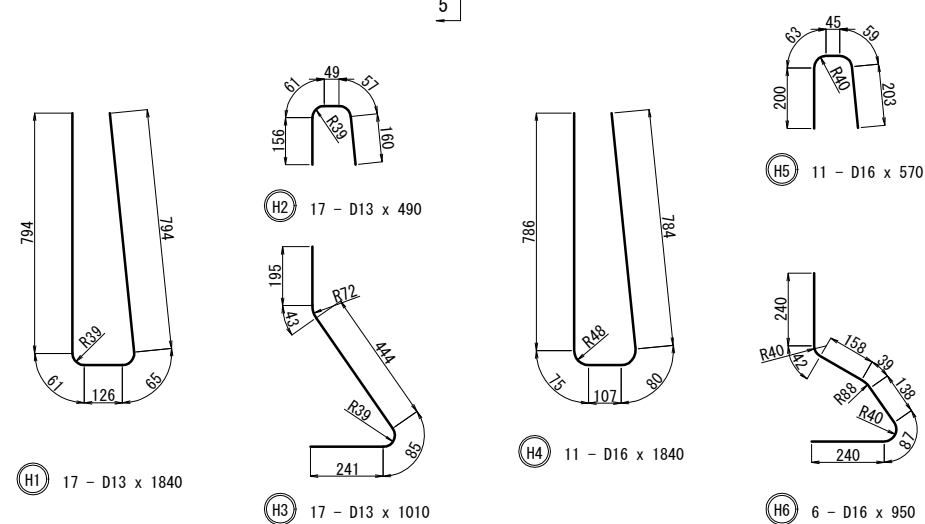

道央自動車道 千歳川大橋（下り線）床版取替工事			
図面の種類	千歳川大橋（下り線）P18～P24 プレキャスト壁高詳細図 (23)		
縮 尺	図 示	図面番号	/
設計会社名	戸田建設株式会社		
施工会社名	戸田建設株式会社		
事務所名	東日本高速道路株式会社 北海道支社 札幌管理事務所		

千歳川大橋(下り線) P18-P24 プレキャスト壁高欄詳細図(24)


S=1:25

[路肩側 L-E3-0J-PB]


(P23-P24径間 製作数 : 1)

断面図


1 - 1

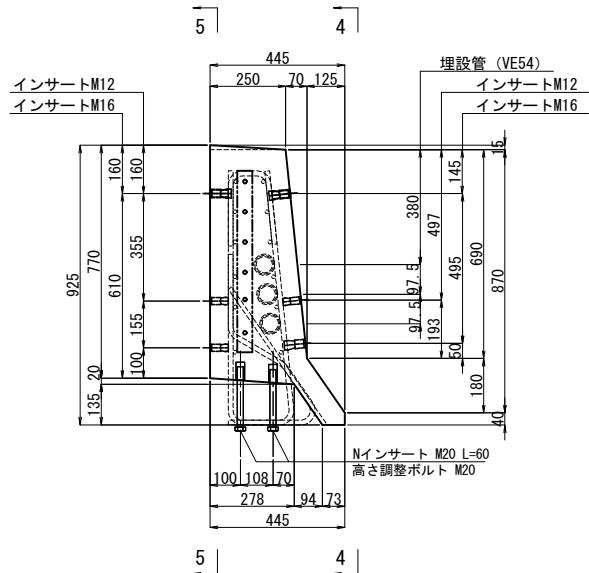

2 - 2

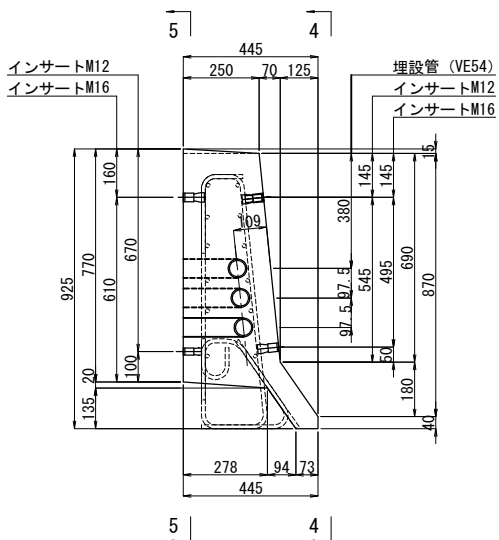

3 - 3

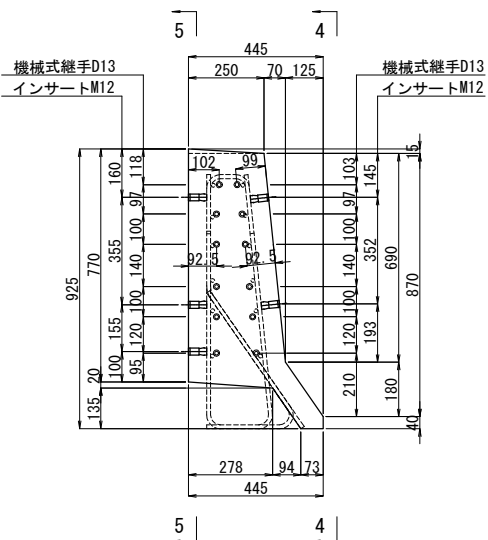

鉄筋表(1ブロック当り)


鉄筋番号	材質	長さ (mm)	本数 (本)	単位重量 (kg/m)	1本当り質量 (kg)	質量 (kg)	備考
H1	D13	1840	17	0.995	1.831	31	EP塗装
H2	D13	490	17	0.995	0.488	8	EP塗装
H3	D13	1010	17	0.995	1.005	17	EP塗装
H4	D16	1840	11	1.56	2.870	32	EP塗装
H5	D16	570	11	1.56	0.889	10	EP塗装
H6	D16	950	6	1.56	1.482	9	EP塗装
H7	D13	550	11	0.995	0.547	6	EP塗装
H8	D13	350	5	0.995	0.348	2	EP塗装
H9	D13	4150	12	0.995	4.129	50	
H10	D13	1640	4	0.995	1.632	7	EP塗装
H11	D13	890	4	0.995	0.886	4	EP塗装
H12	D13	930	4	0.995	0.925	4	EP塗装
H13	D16	1630	2	1.56	2.543	5	EP塗装
H14	D16	920	7	1.56	1.435	10	EP塗装
H15	D16	930	2	1.56	1.451	3	EP塗装
H16	D13	500	12	0.995	0.498	6	EP塗装
合 計						204	kg
鉄筋質量集計 (SD345)							
				普通鉄筋	塗装鉄筋		
				D16	0 kg	69 kg	69 kg
				D13	50 kg	85 kg	135 kg
				合計	50 kg	154 kg	204 kg
				F0グリップ D13		12 組	

インサート配置側面図


起点側

4 - 4

終点側

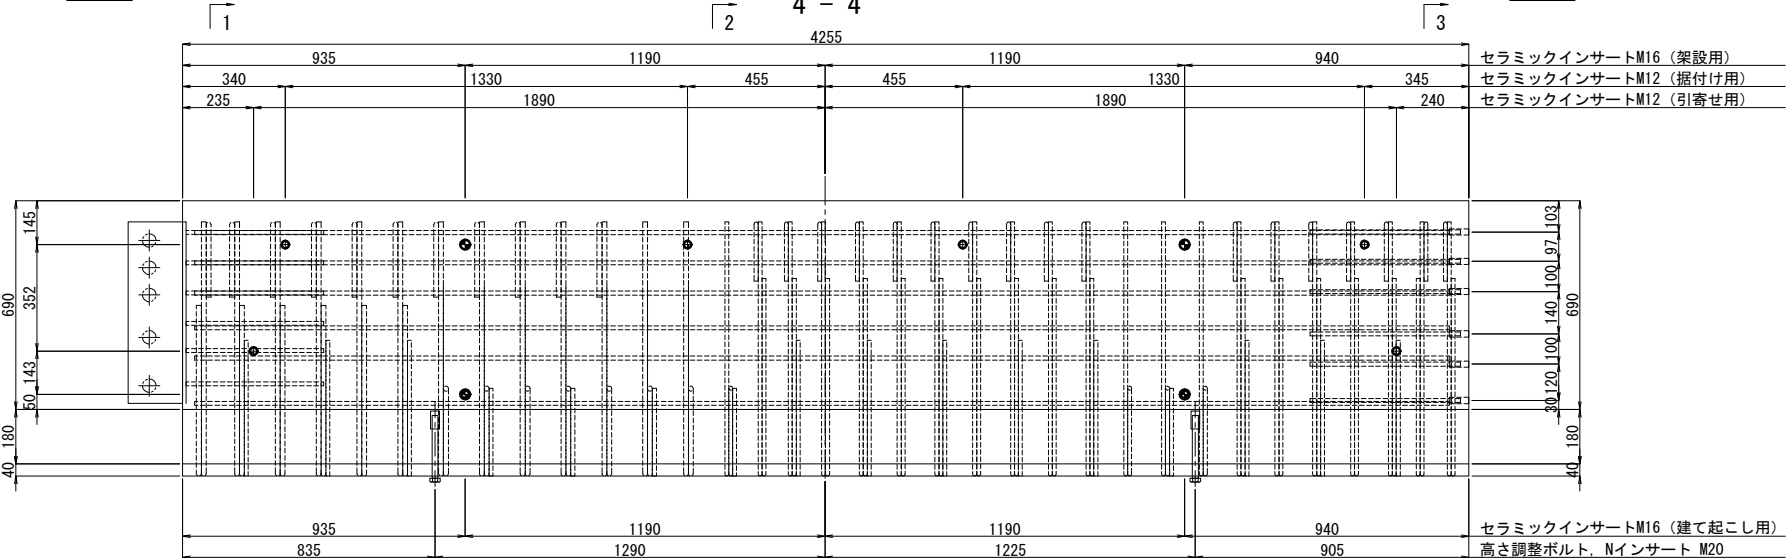

5 - 5

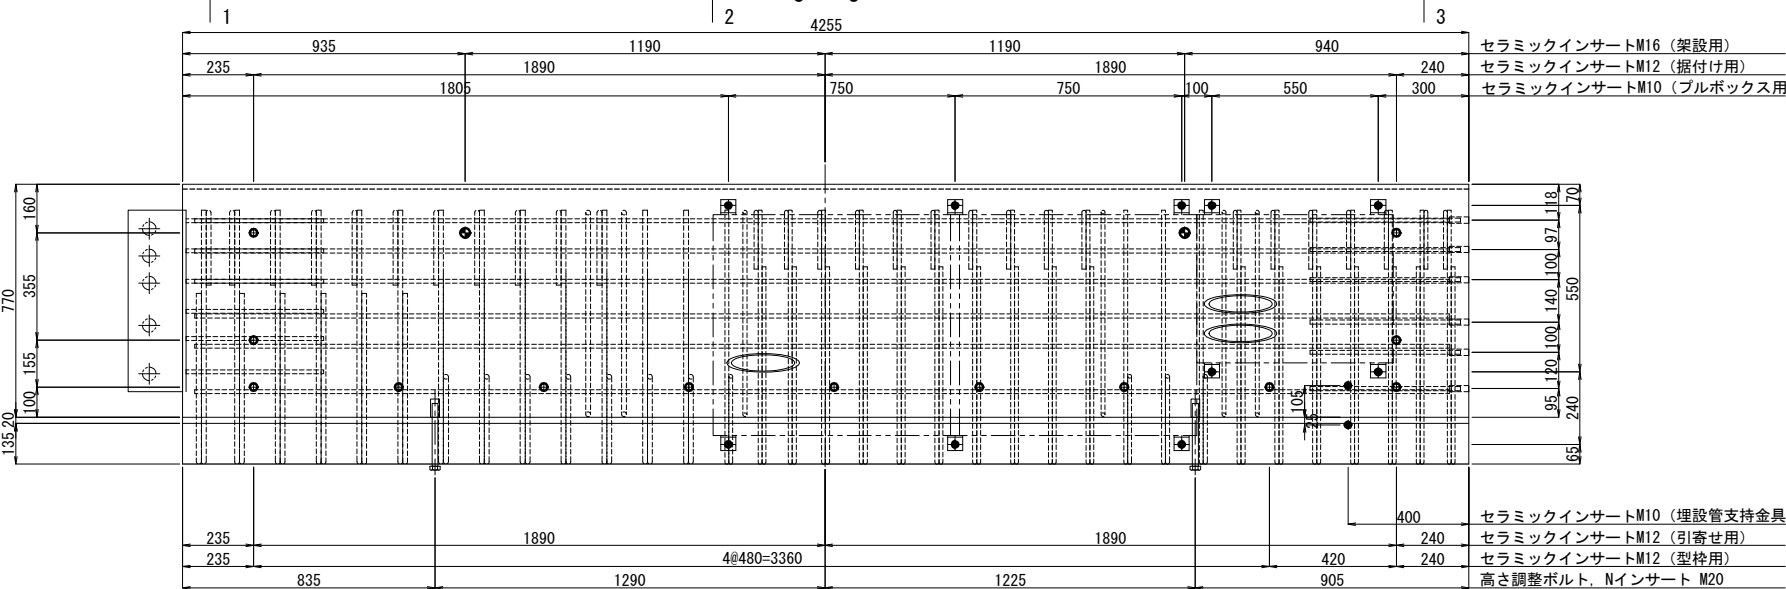


埋設管配置側面図

起点側





5 - 5

終点側

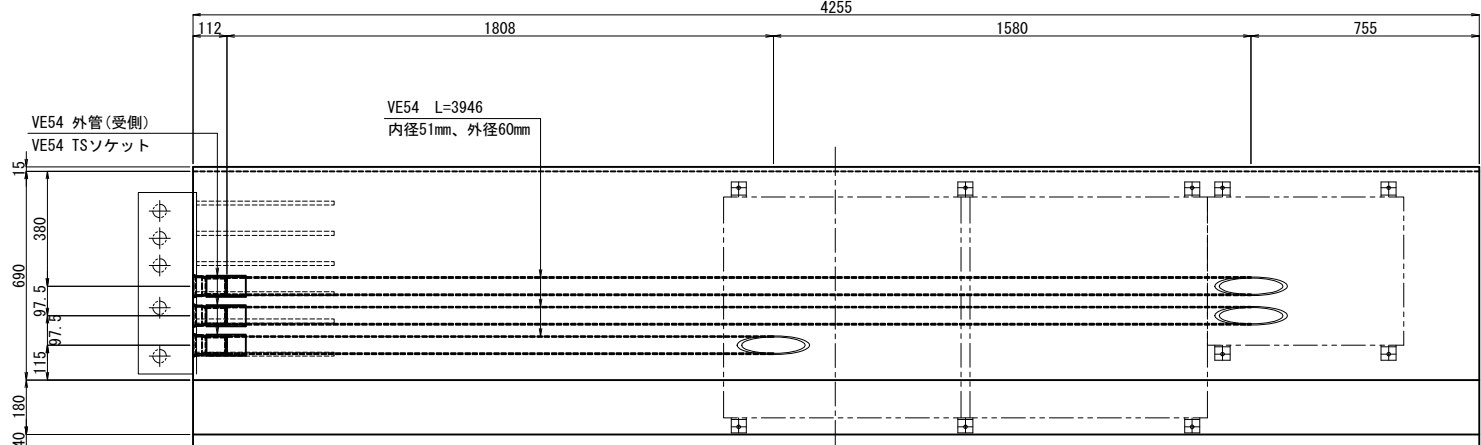

道央自動車道 千歳川大橋(下り線) 床版取替工事			
図面の種類	千歳川大橋(下り線) P18-P24 プレキャスト壁高欄詳細図(24)		
縮 尺	図 示	図面番号	/
設計会社名	戸田建設株式会社		
施工会社名	戸田建設株式会社		
事務所名	東日本高速道路株式会社 北海道支社 札幌管理事務所		

S=1:25

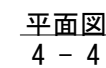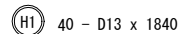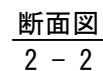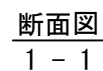

※ 鉄筋記号の  は塗装鉄筋を示す。

※ インサートおよび埋設管などの詳細位置は、壁高欄詳細図(26)を参照のこと。

道失自動車道 千歳川大橋（下り線）床版取替工事			
図面の種類	千歳川大橋（下り線）P18-P24 ブレキャスト壁高橋詳細図 (25)		
縮 尺	図 示	図面番号	/
設計会社名	戸田建設株式会社		
施工会社名	戸田建設株式会社		
事務所名	東日本高速道路株式会社 北海道支社 札幌管理事務所		


千歳川大橋(下り線) P18-P24 プレキャスト壁高欄詳細図(26)

S=1:25


[中分側 R-48-0M]

(P18-P19径間 製作数 : 3) (P19-P20径間 製作数 : 3)
(P20-P21径間 製作数 : 4) (P21-P22径間 製作数 : 3)
(P22-P23径間 製作数 : 4) (P23-P24径間 製作数 : 3)


断面図
1 - 1

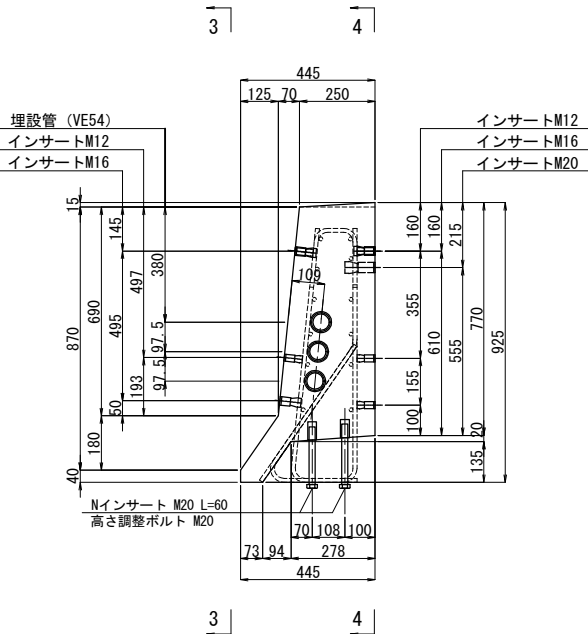


2 - 2

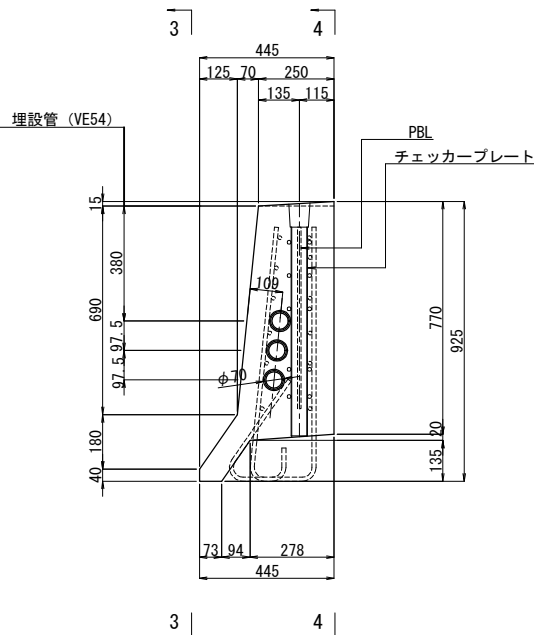

インサート配置側面図

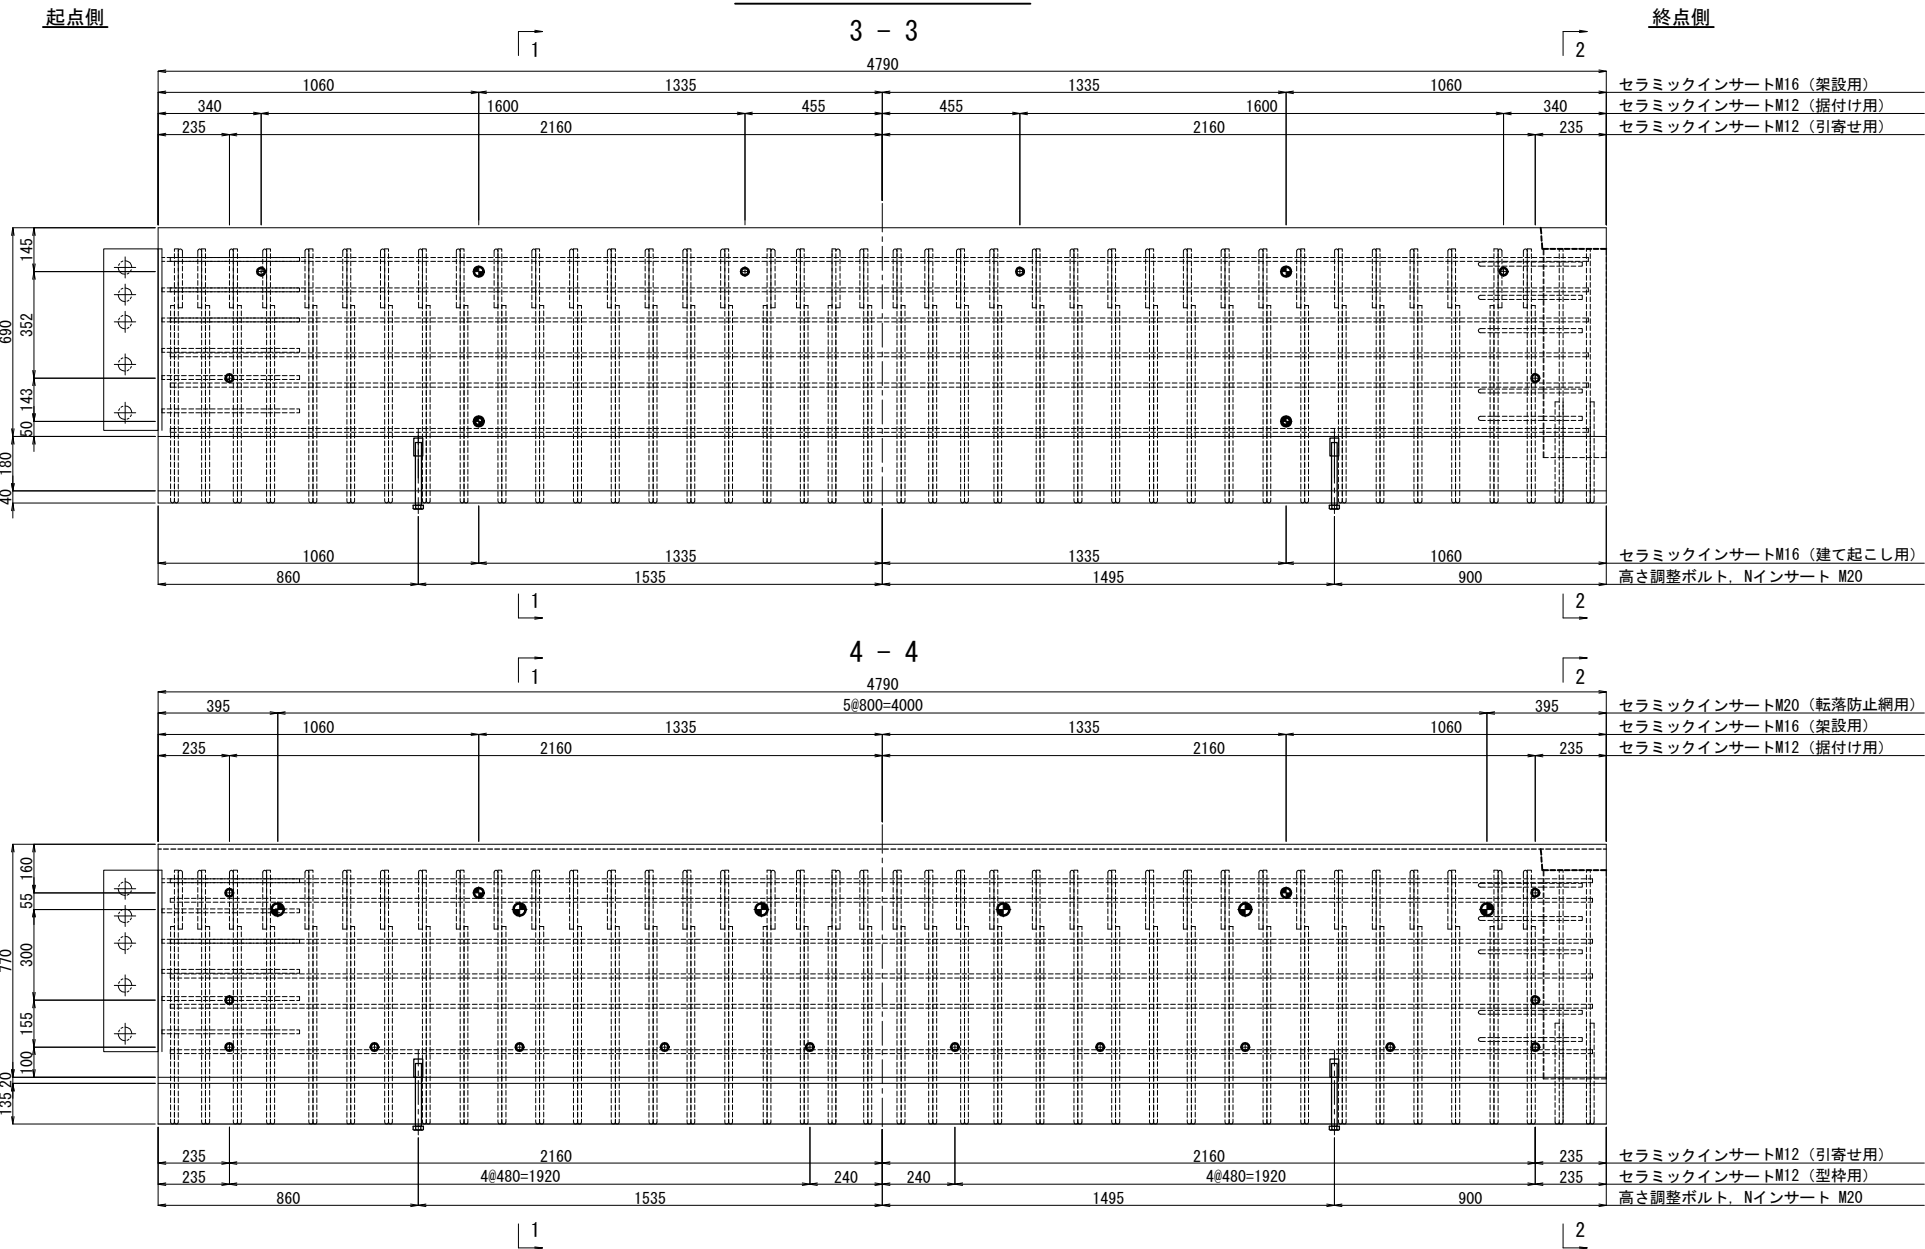





埋設管配置側面図

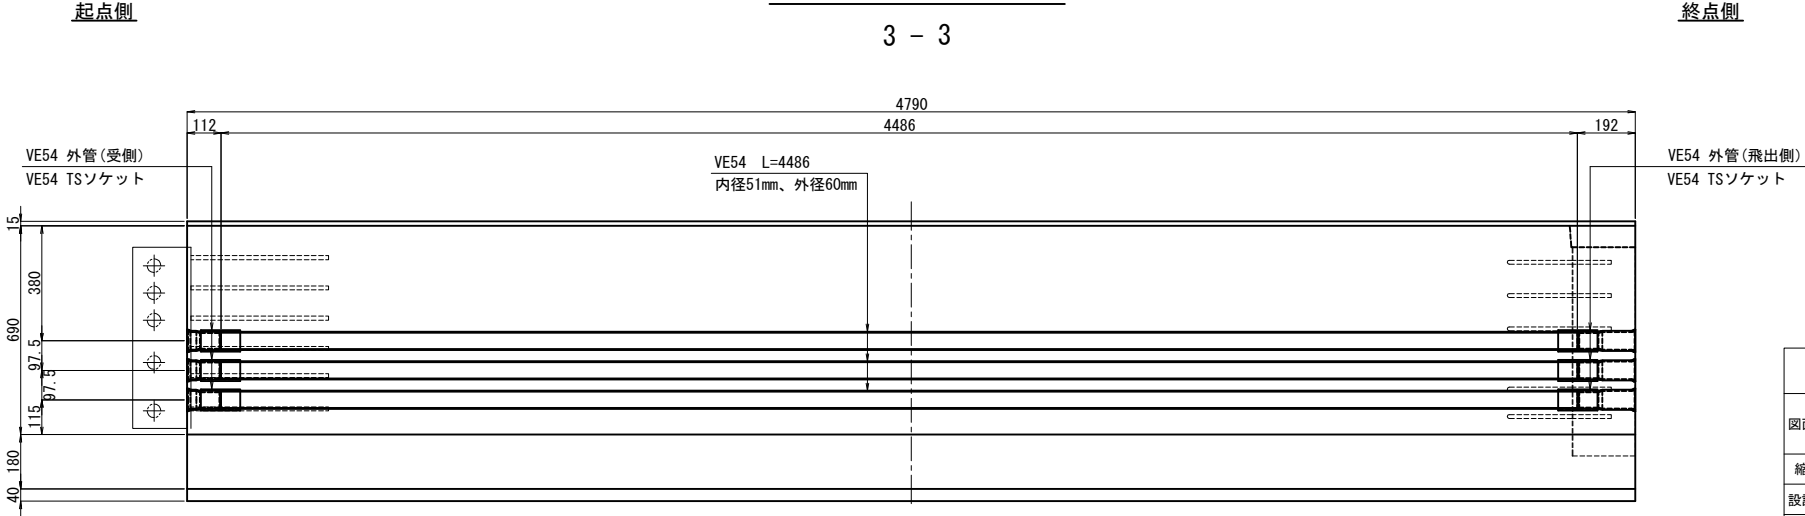

道央自動車道 千歳川大橋(下り線)床版取替工事			
図面の種類	千歳川大橋(下り線) P18-P24 プレキャスト壁高欄詳細図(26)		
縮 尺	図 示	図面番号	/
設計会社名	戸田建設株式会社		
施工会社名	戸田建設株式会社		
事務所名	東日本高速道路株式会社 北海道支社 札幌管理事務所		



千歳川大橋(下り線) P18-P24 プレキャスト壁高欄詳細図(27)

S=1:25

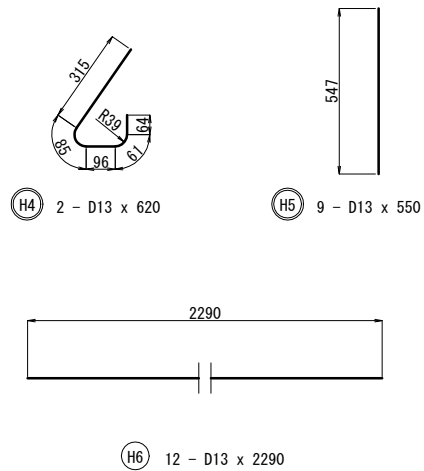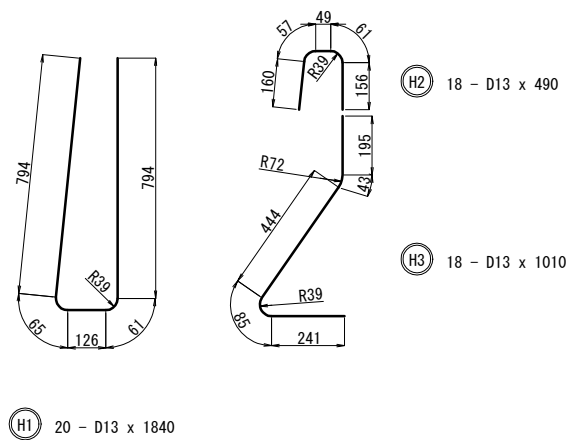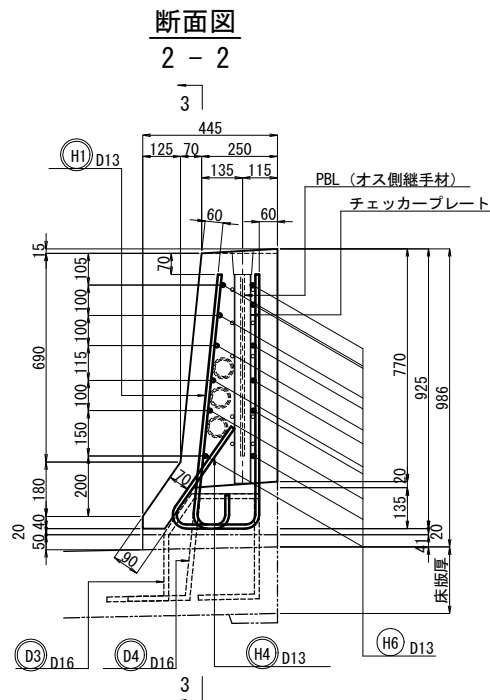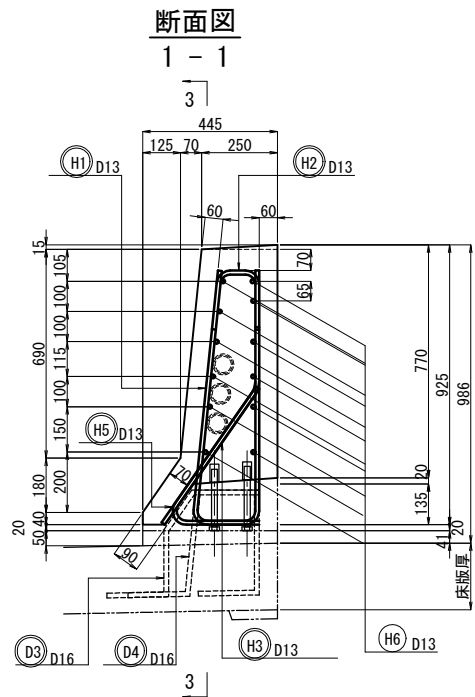

[中分側 R-24-0M]

(P19-P20径間 製作数 : 1) (P20-P21径間 製作数 : 1)
(P21-P22径間 製作数 : 1) (P22-P23径間 製作数 : 1)
(P23-P24径間 製作数 : 1)

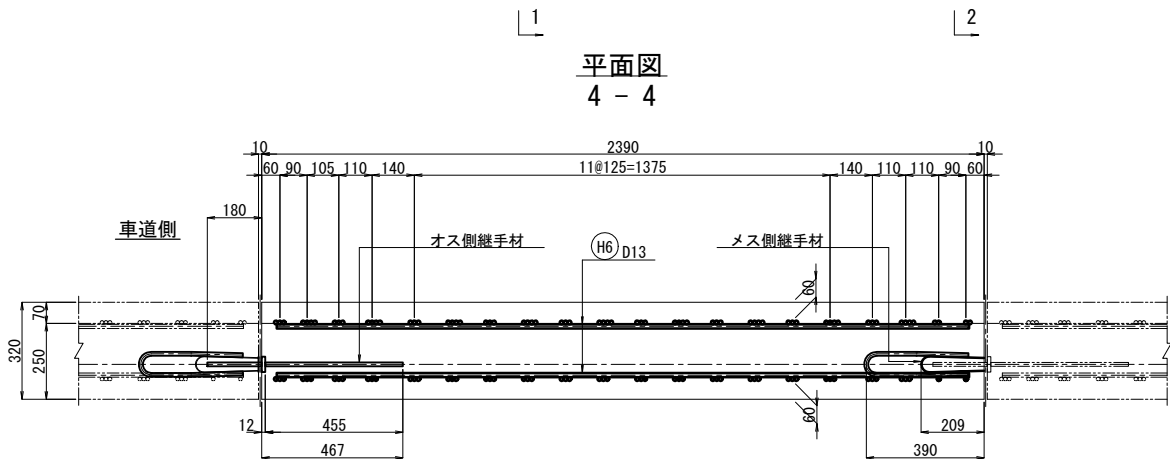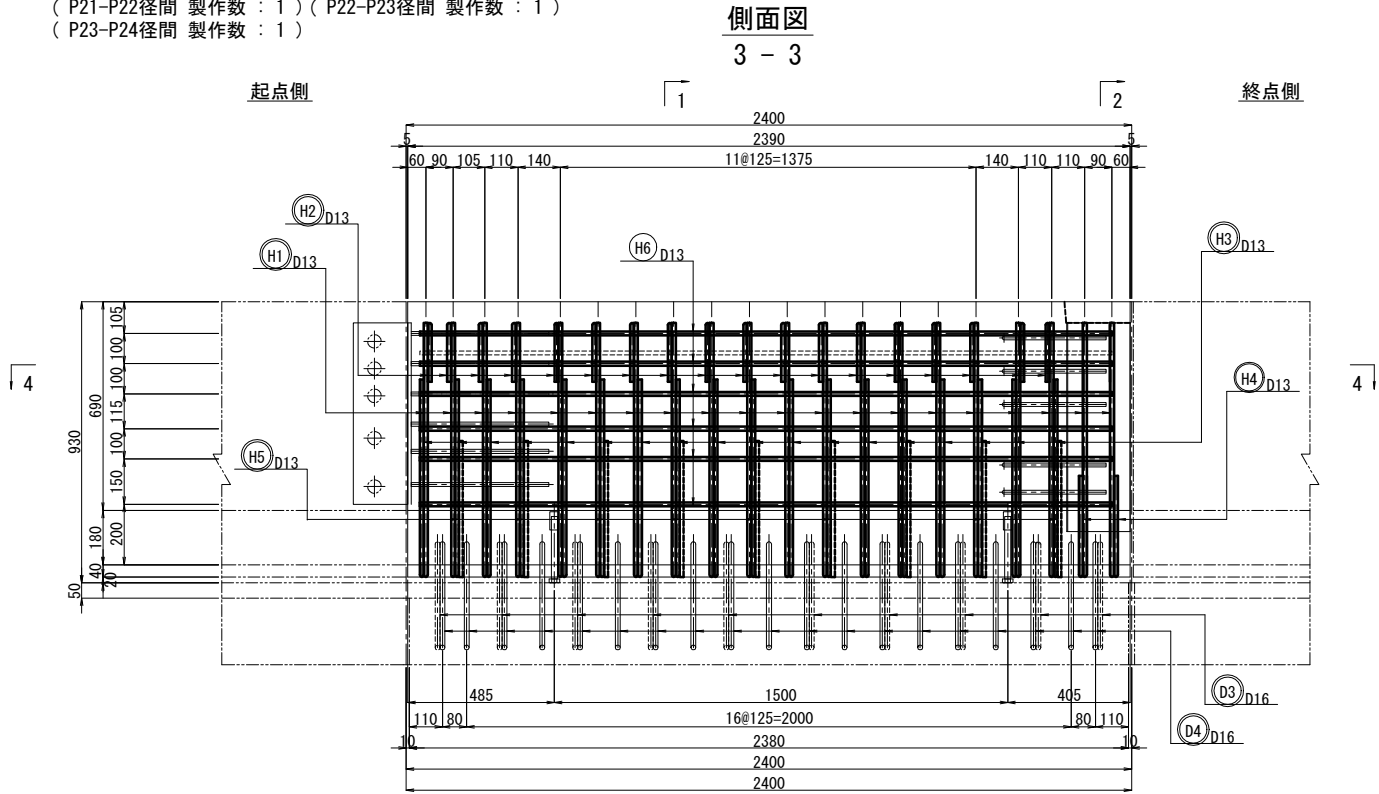

※ 鉄筋記号の○は塗装鉄筋を示す。
※ インサートおよび埋設管などの詳細位置は、壁高欄詳細図(28)を参照のこと。


鉄筋表(1ブロック当り)						
鉄筋番号	材質	長さ (mm)	本数 (本)	単位重量 (kg/m)	1本当り質量 (kg)	質量 (kg)
H1	D13	1840	20	0.995	1.831	37
H2	D13	490	18	0.995	0.488	9
H3	D13	1010	18	0.995	1.005	18
H4	D13	620	2	0.995	0.617	1
H5	D13	550	9	0.995	0.547	5
H6	D13	2290	12	0.995	2.279	27
合 計						97 kg
鉄筋質量集計(SD345)						
				普通鉄筋	塗装鉄筋	
				D13	27 kg	70 kg
				合計	27 kg	97 kg

道央自動車道 千歳川大橋(下り線)床版取替工事			
図面の種類	千歳川大橋(下り線) P18-P24 プレキャスト壁高欄詳細図(27)		
縮 尺	図 示	図面番号	/
設計会社名	戸田建設株式会社		
施工会社名	戸田建設株式会社		
事務所名	東日本高速道路株式会社 北海道支社 札幌管理事務所		


[中分側 R-24-0M]

(P19-P20径間 製作数 : 1) (P20-P21径間 製作数 : 1)
(P21-P22径間 製作数 : 1) (P22-P23径間 製作数 : 1)
(P23-P24径間 製作数 : 1)


断面図
1 - 1

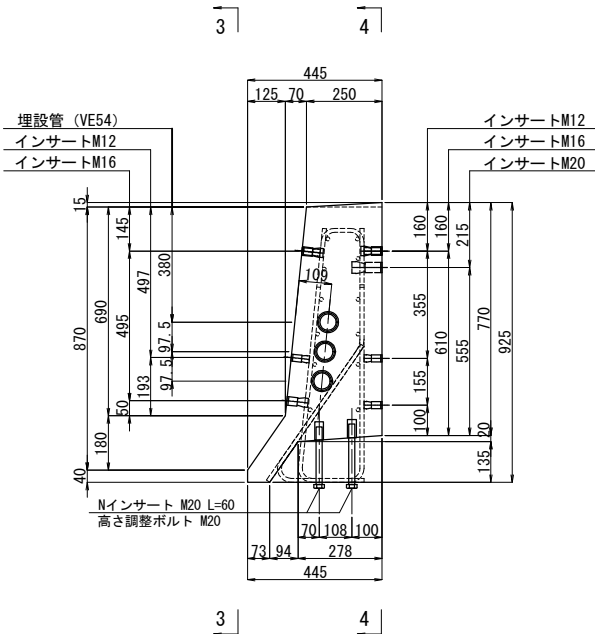


2 - 2

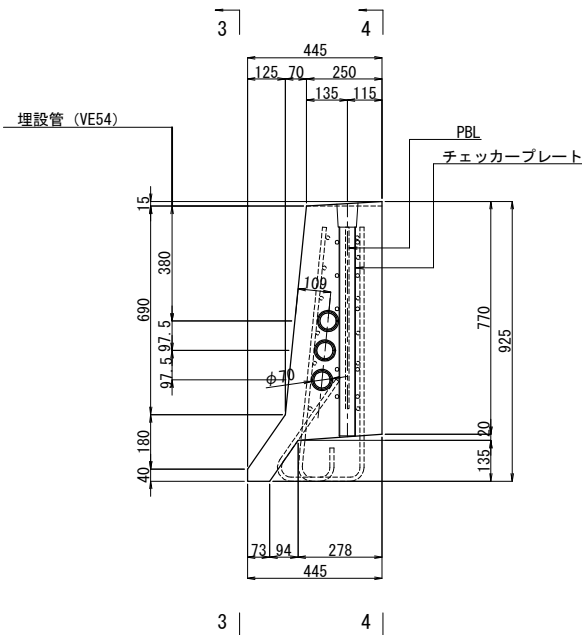


インサート配置側面図

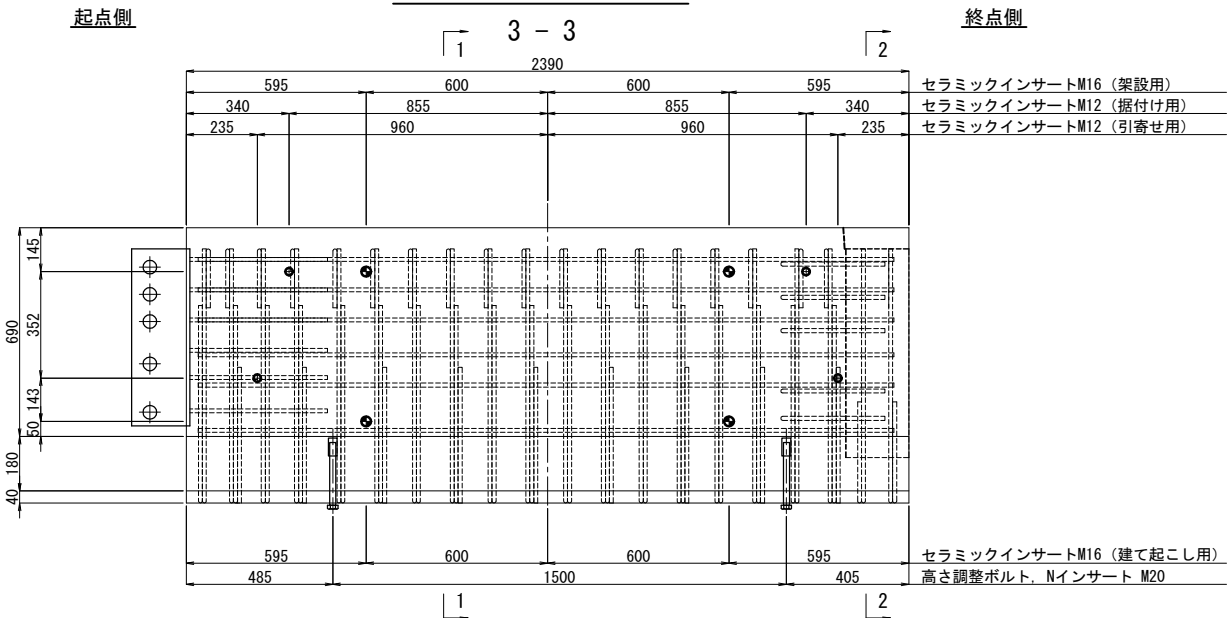

4 - 4

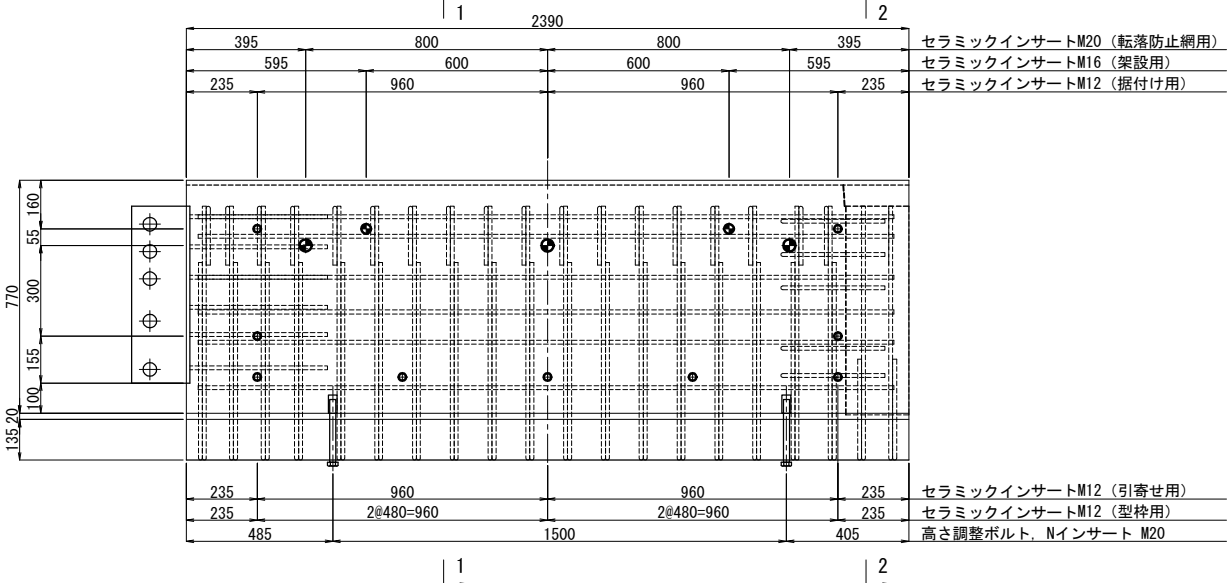

埋設管配置側面図

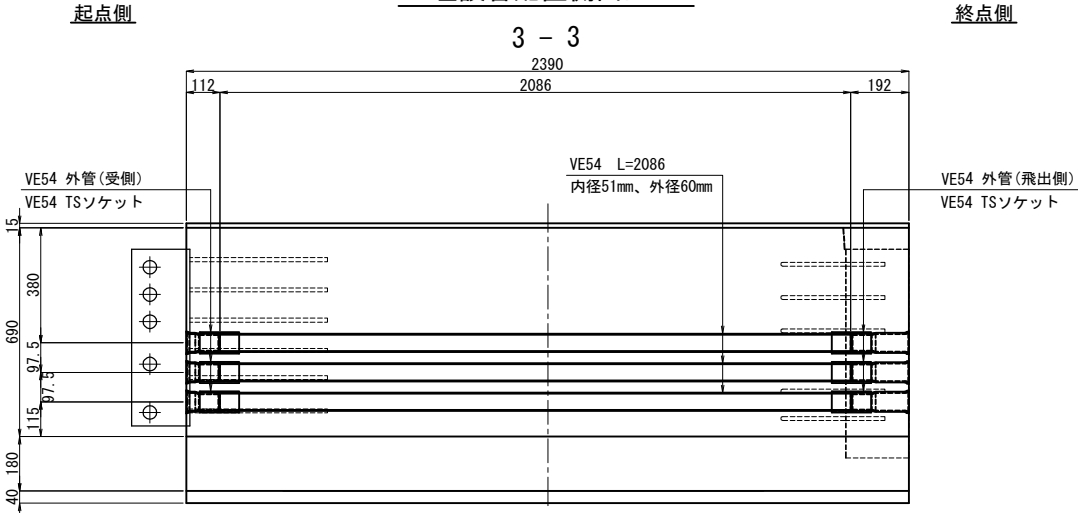


道央自動車道 千歳川大橋(下り線) 床版取替工事			
図面の種類	千歳川大橋(下り線) P18-P24 プレキャスト壁高欄詳細図(28)		
縮 尺	図 示	図面番号	/
設計会社名	戸田建設株式会社		
施工会社名	戸田建設株式会社		
事務所名	東日本高速道路株式会社 北海道支社 札幌管理事務所		


S=1 : 25

(P18-P19径間 製作数 : 1)


1 - 1

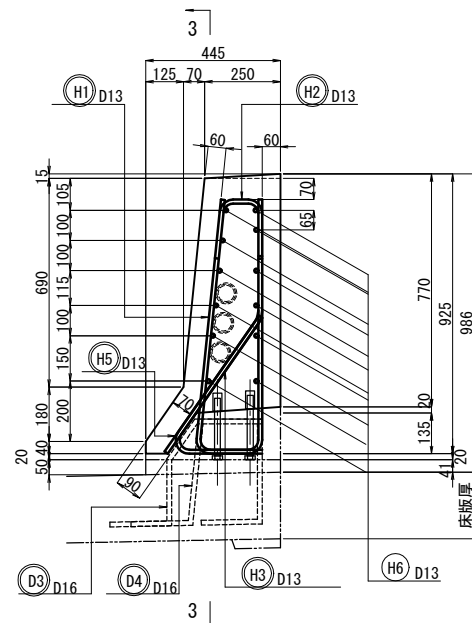

2 - 2

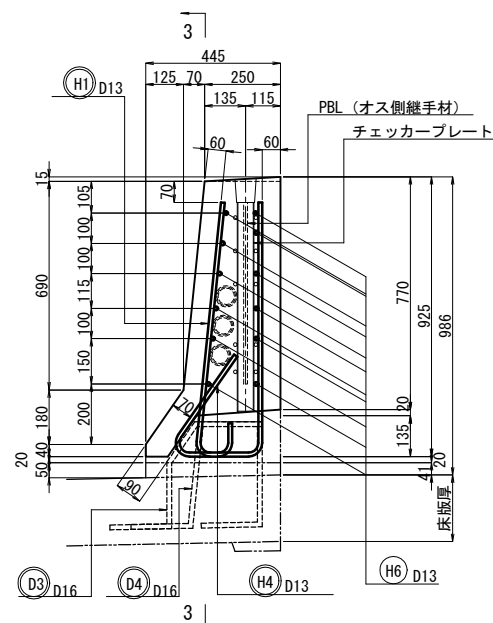


H1 25 - D13 x 1840

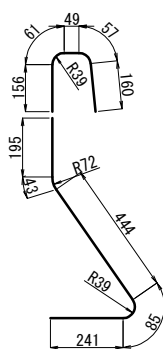

② H2 23 - D13 x 490


23 - D13 x 1010

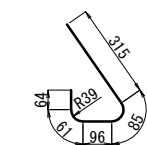


④ H4 2 - D13 x 630




H5 12 - D13 x 550

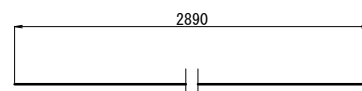

⑥ 12 - D13 x 2890
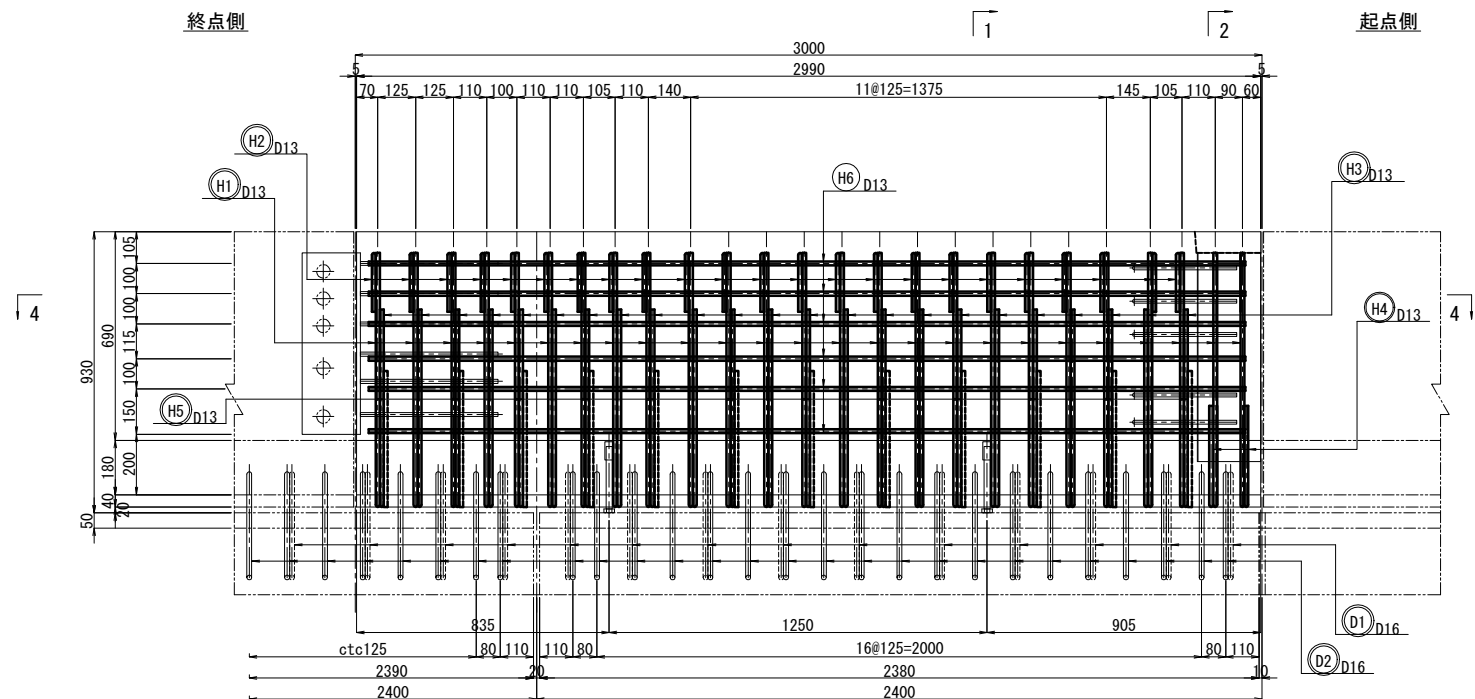
$$\overline{3 - 3}$$


4 - 4

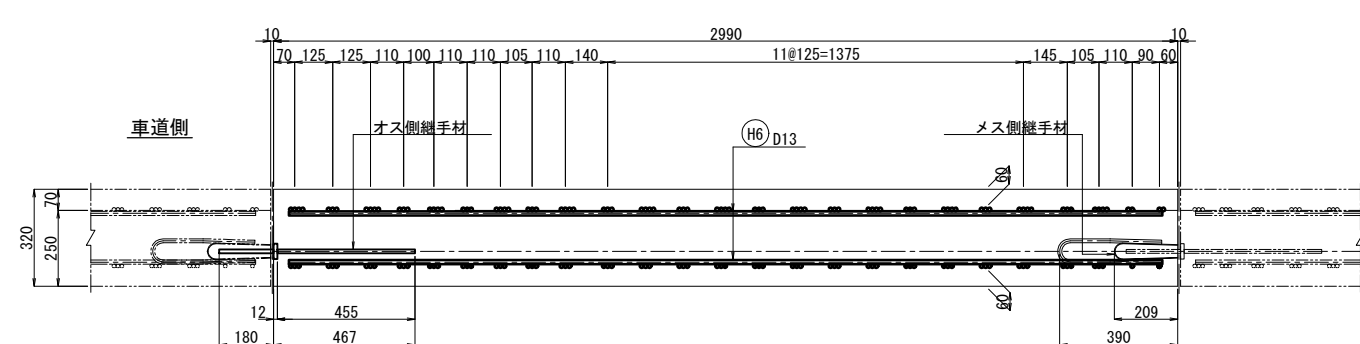

※ 鉄筋記号の は塗装鉄筋を示す。

※ インサートおよび埋設管などの詳細位置は、壁高欄詳細図(30)を参照のこと。

鉄筋表(1ブロック当り)

鉄筋番号	材質	長さ (mm)	本数 (本)	単位重量 (kg/m)	1本当り質量 (kg)	質 量 (kg)	備 考
H1	D13	1840	25	0.995	1.831	46	EP塗装
H2	D13	490	23	0.995	0.488	11	EP塗装
H3	D13	1010	23	0.995	1.005	23	EP塗装
H4	D13	620	2	0.995	0.617	1	EP塗装
H5	D13	550	12	0.995	0.547	7	EP塗装
H6	D13	2890	12	0.995	2.876	35	
合 計						123	kg
鉄筋質量集計 (SD345)							
				普通鉄筋	塗装鉄筋		
D13				35 kg	88 kg	123 kg	
合計				35 kg	88 kg	123 kg	

道央自動車道 千歳川大橋（下り線）床版取替工事			
図面の種類	千歳川大橋（下り線）P18-P24 プレキャスト壁高欄詳細図 (29)		
縮 尺	図 示	図面番号	/
設計会社名	戸田建設株式会社		
施工会社名	戸田建設株式会社		
事務所名	東日本高速道路株式会社 北海道支社 札幌管理事務所		

千歳川大橋(下り線) P18-P24 プレキャスト壁高欄詳細図(30)


S=1:25

[中分側 R-30-0M]


(P18-P19径間 製作数 : 1)

断面図

1 - 1

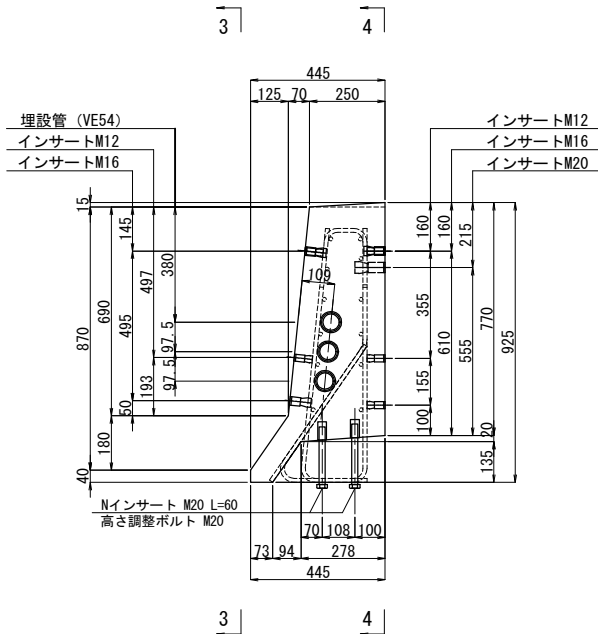

2 - 2

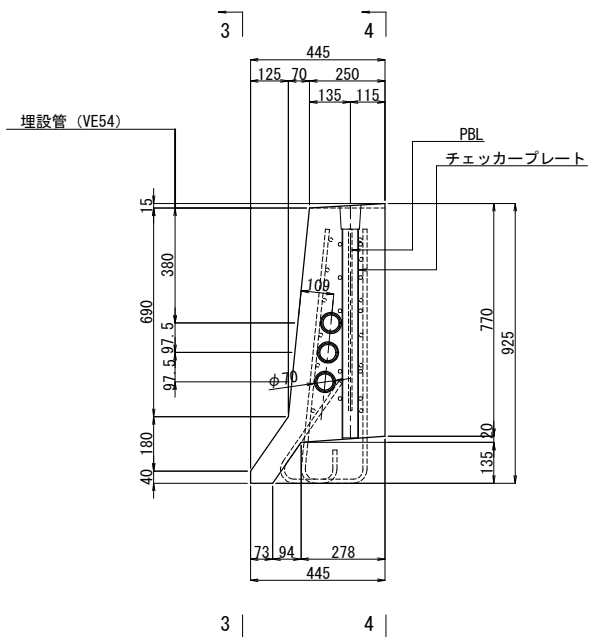


インサート配置側面図


起点側

3 - 3

終点側

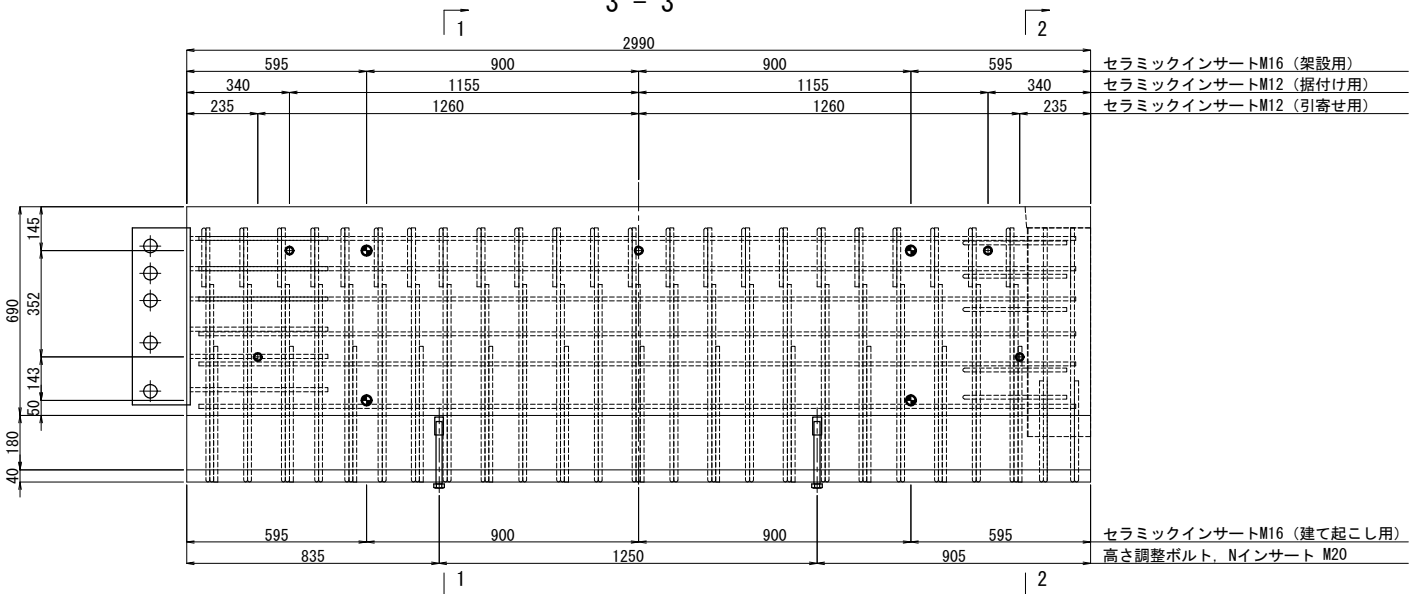

4 - 4

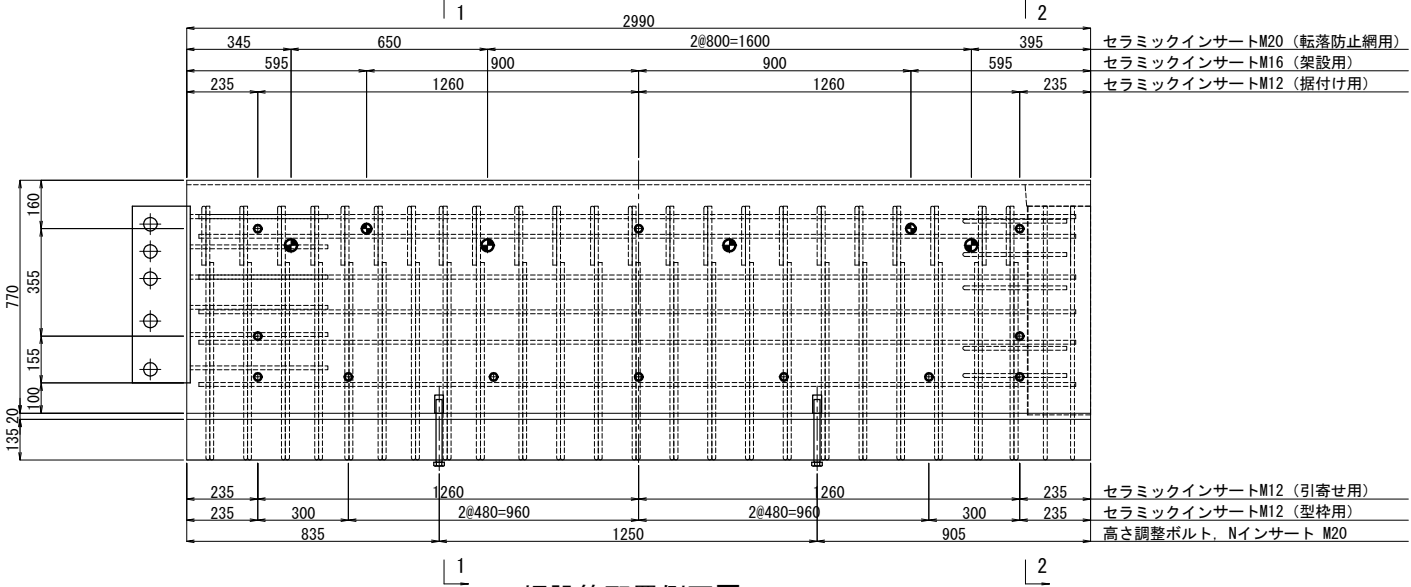


埋設管配置側面図

起点側

3 - 3

終点側

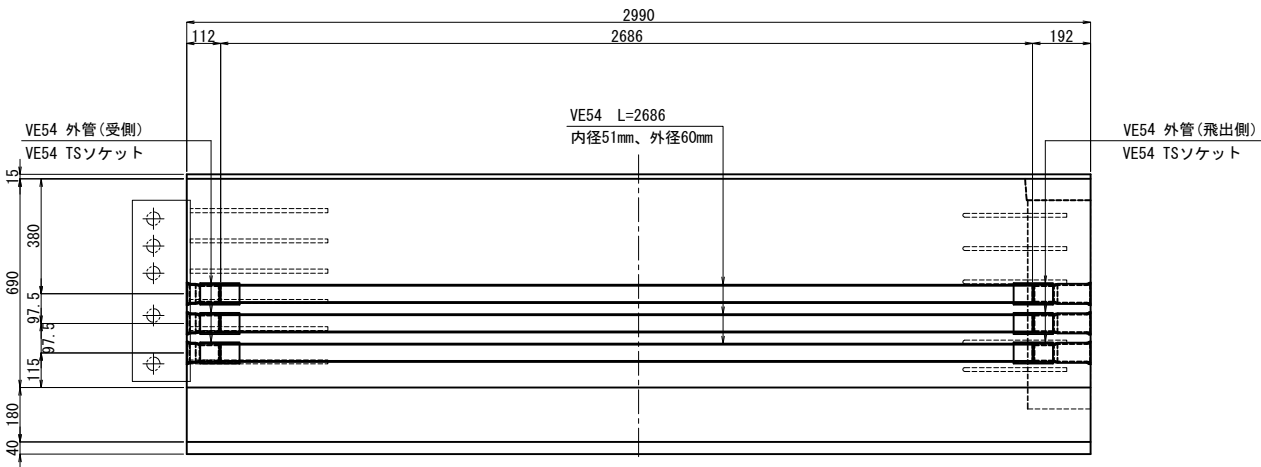


道央自動車道 千歳川大橋(下り線) 床版取替工事			
図面の種類	千歳川大橋(下り線) P18-P24 プレキャスト壁高欄詳細図(30)		
縮 尺	図 示	図面番号	/
設計会社名	戸田建設株式会社		
施工会社名	戸田建設株式会社		
事務所名	東日本高速道路株式会社 北海道支社 札幌管理事務所		

千歳川大橋(下り線) P18-P24 プレキャスト壁高欄詳細図(31)

S=1:25


断面図

1 - 1

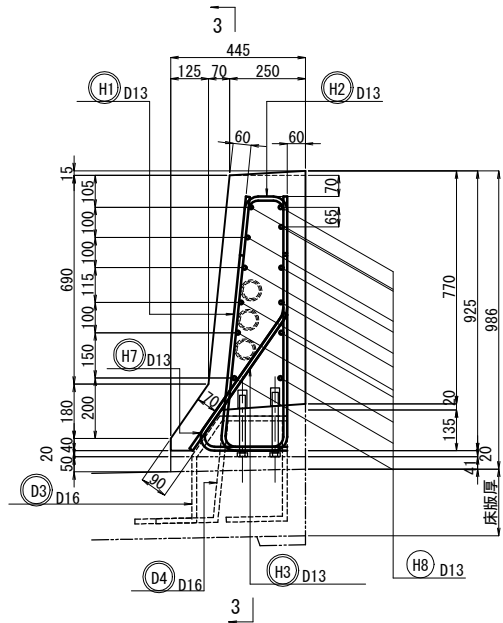

断面図

2 - 2

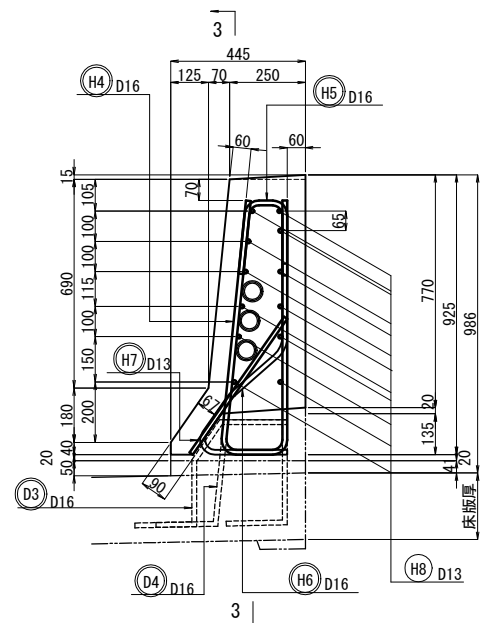


[中分側 R-48-0F]

(P18-P19径間 製作数 : 1) (P19-P20径間 製作数 : 1)
(P20-P21径間 製作数 : 1) (P21-P22径間 製作数 : 1)


側面図

3 - 3

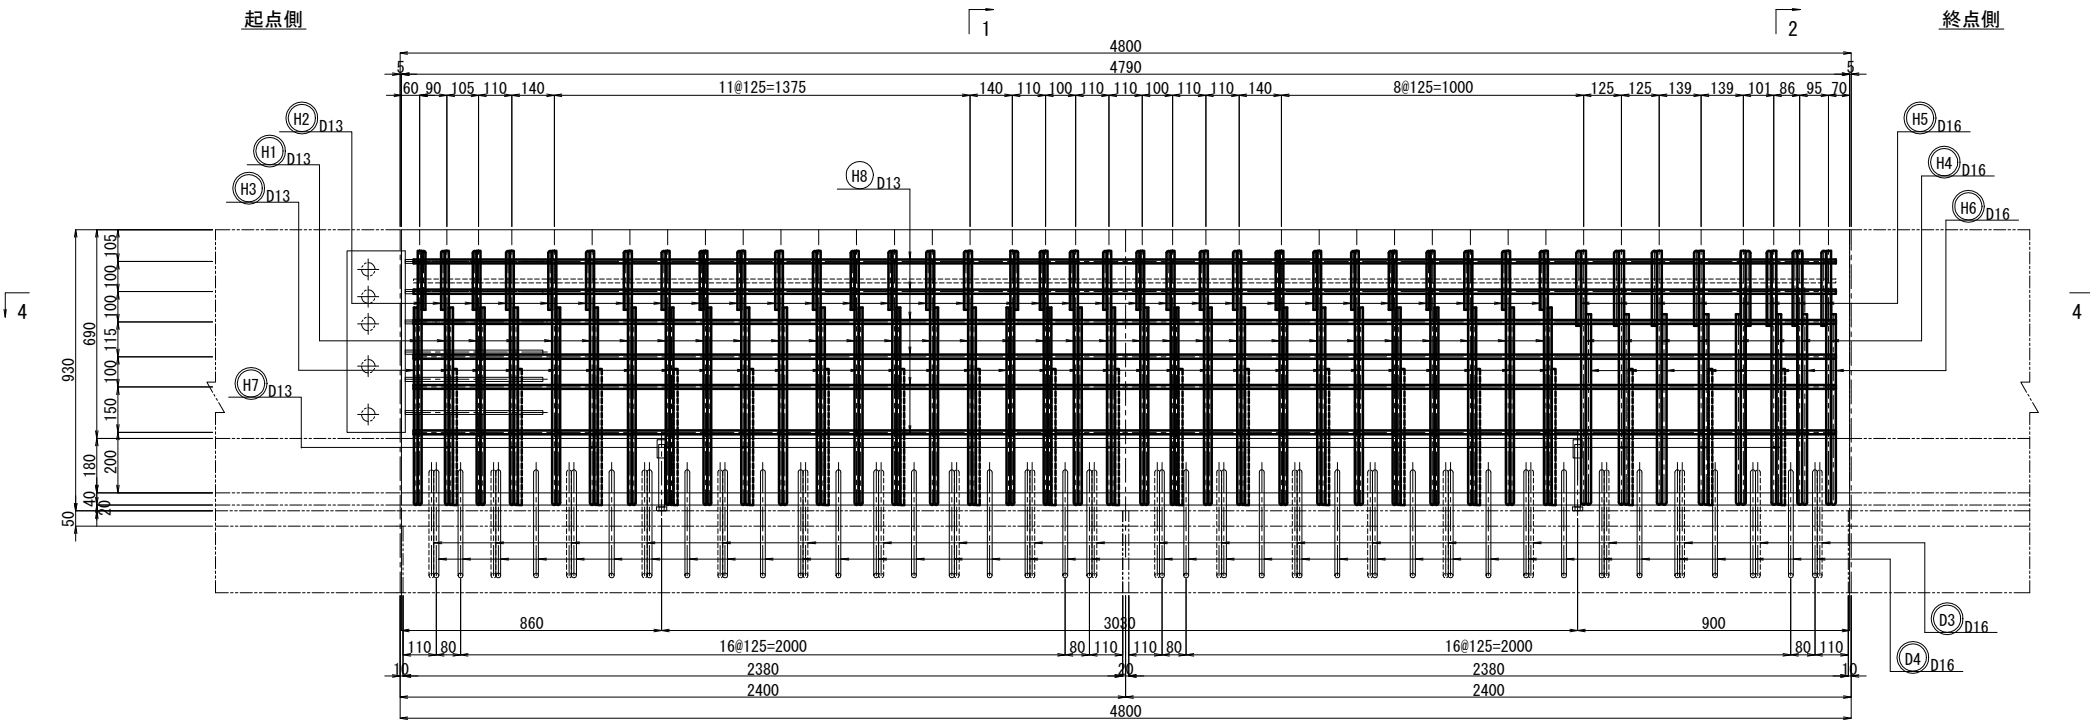


平面図

4 - 4

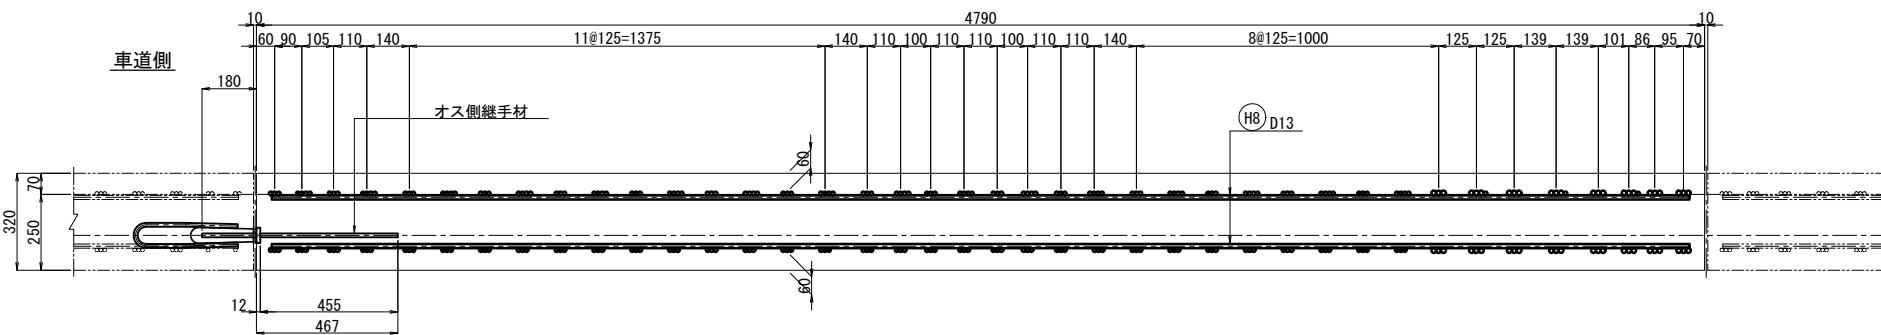

※ 鉄筋記号の○は塗装鉄筋を示す。
※ インサートおよび埋設管などの詳細位置は、壁高欄詳細図(32)を参照のこと。

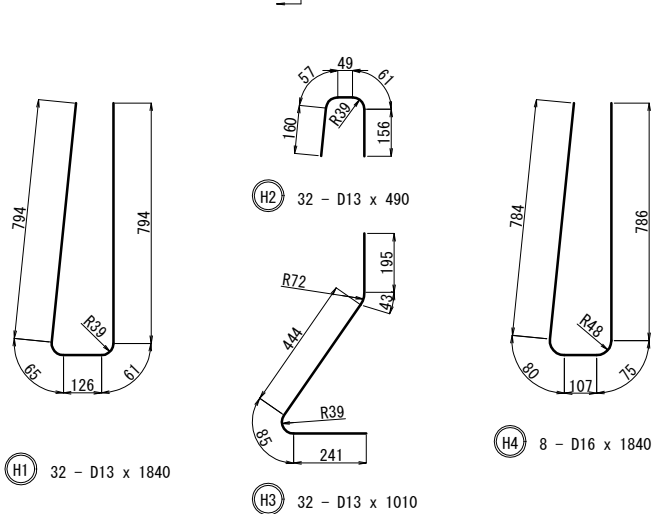

鉄筋表(1ブロック当り)						
鉄筋番号	材質	長さ (mm)	本数 (本)	単位重量 (kg/m)	1本当り質量 (kg)	質量 (kg)
H1	D13	1840	32	0.995	1.831	59
H2	D13	490	32	0.995	0.488	16
H3	D13	1010	32	0.995	1.005	32
H4	D16	1840	8	1.56	2.870	23
H5	D16	570	8	1.56	0.889	7
H6	D16	990	8	1.56	1.544	12
H7	D13	550	19	0.995	0.547	10
H8	D13	4690	12	0.995	4.667	56
合 計					215	kg
鉄筋質量集計(SD345)						
		普通鉄筋		塗装鉄筋		
		D16	0 kg	42 kg	42 kg	
		D13	56 kg	117 kg	173 kg	
		合計	56 kg	159 kg	215 kg	

道央自動車道 千歳川大橋(下り線) 床版取替工事			
図面の種類	千歳川大橋(下り線) P18-P24 プレキャスト壁高欄詳細図(31)		
縮 尺	図 示	図面番号	/
設計会社名	戸田建設株式会社		
施工会社名	戸田建設株式会社		
事務所名	東日本高速道路株式会社 北海道支社 札幌管理事務所		


千歳川大橋(下り線) P18-P24 プレキャスト壁高欄詳細図(32)

S=1:25


[中分側 R-48-0F]

(P18-P19径間 製作数 : 1) (P19-P20径間 製作数 : 1)
(P20-P21径間 製作数 : 1) (P21-P22径間 製作数 : 1)


断面図
1 - 1

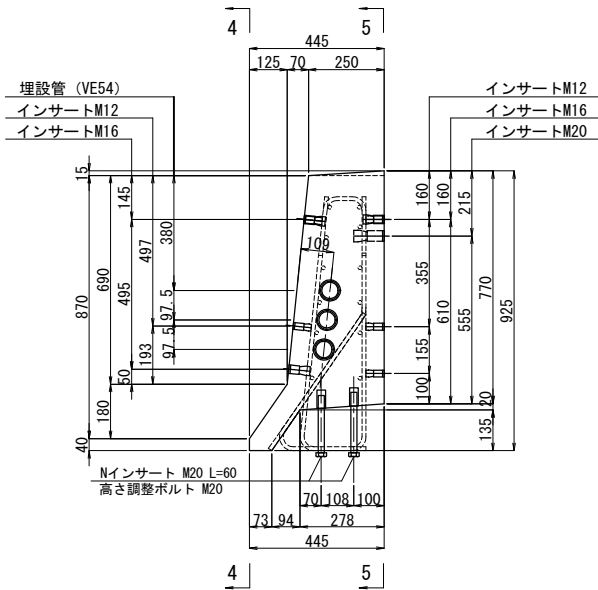

2 - 2

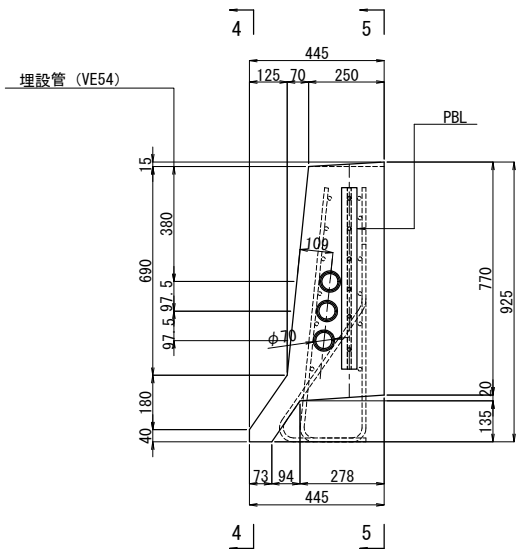


3 - 3

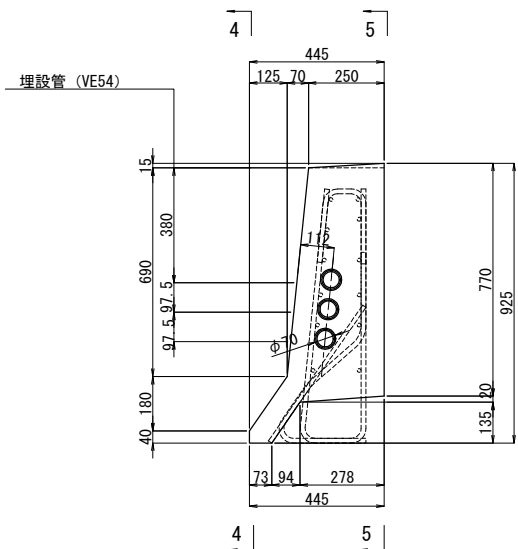


インサート配置側面図

4 - 4

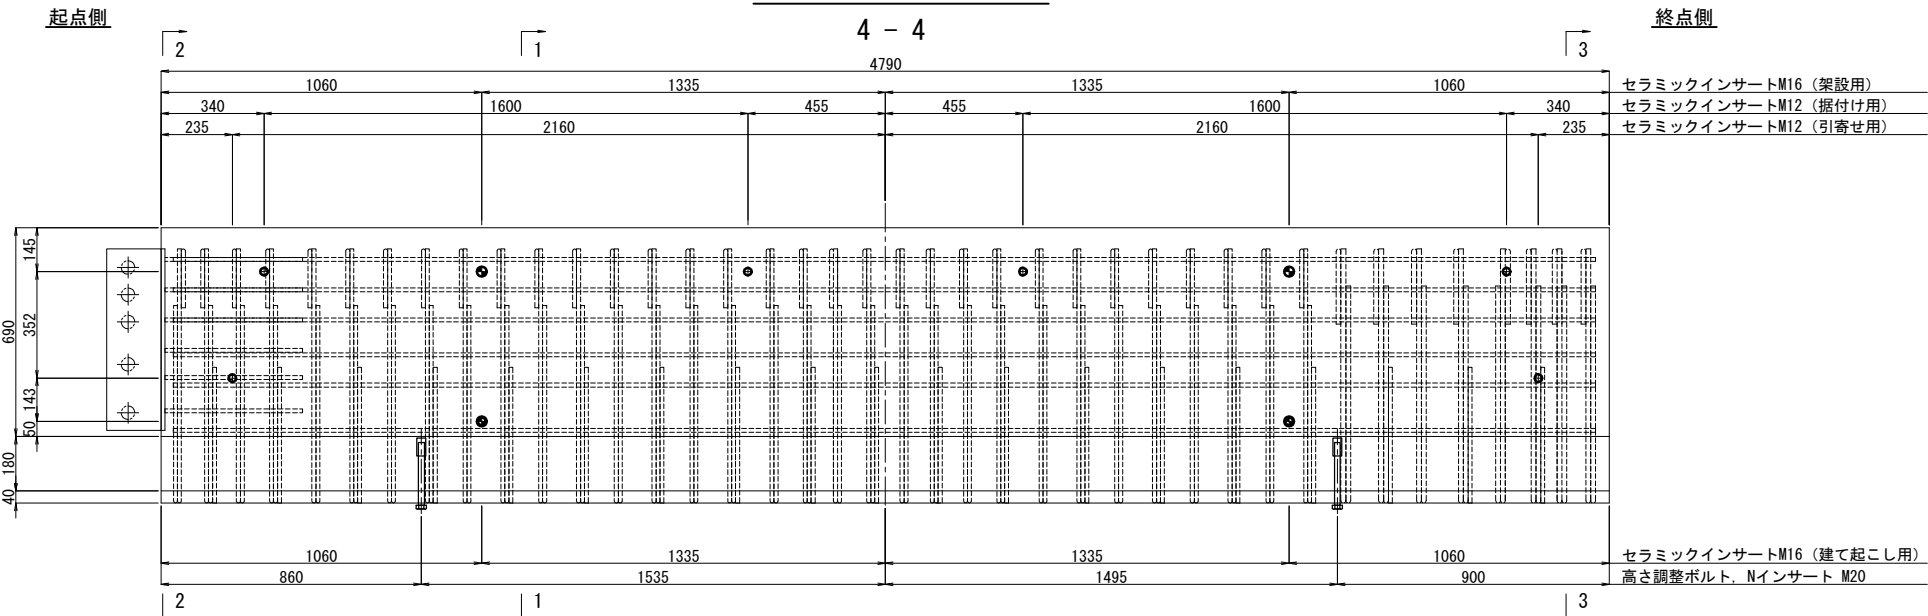


5 - 5

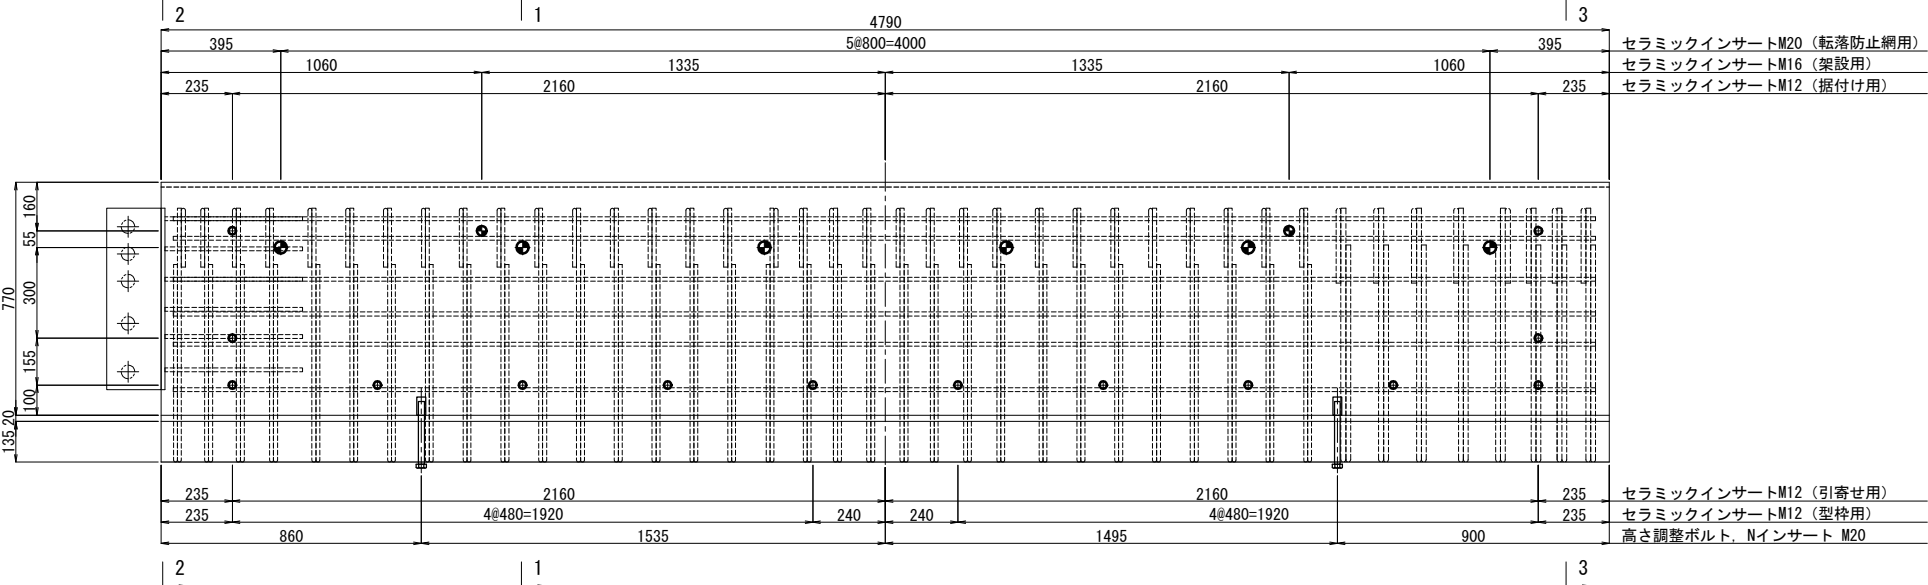

埋設管配置側面図

4 - 4

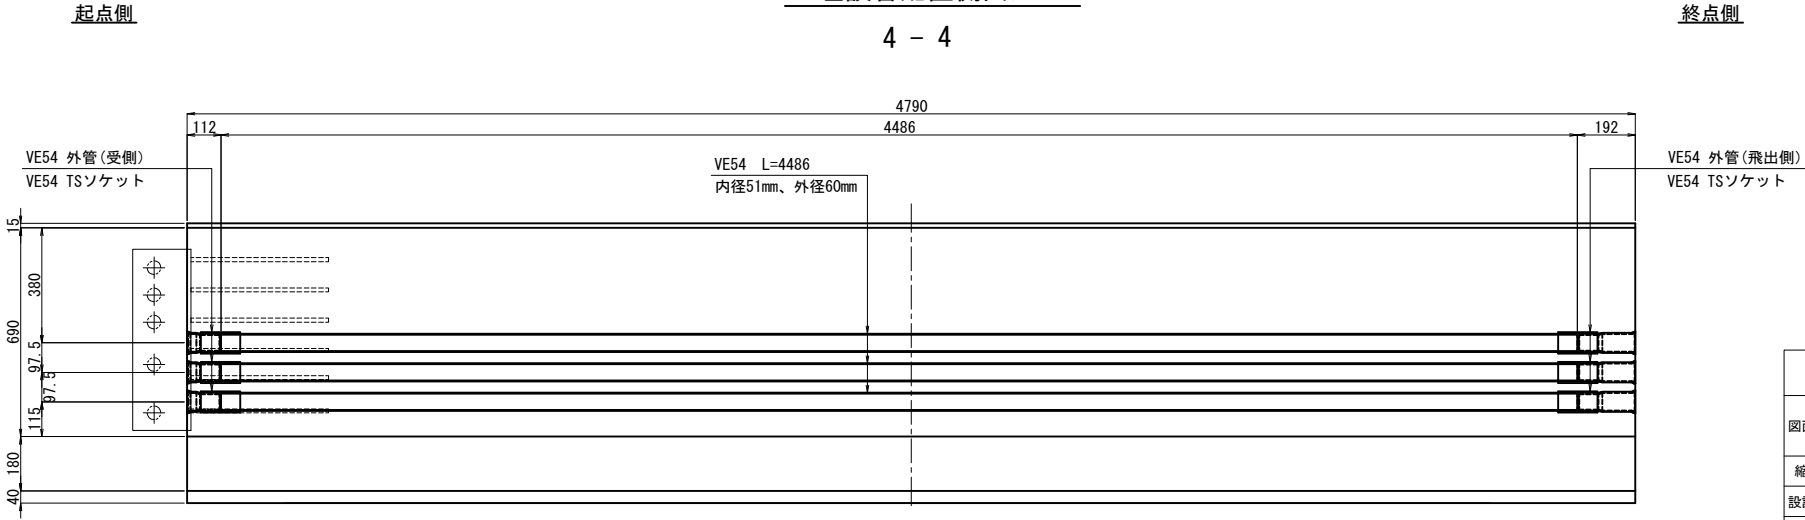

道央自動車道 千歳川大橋(下り線) 床版取替工事			
図面の種類	千歳川大橋(下り線) P18-P24 プレキャスト壁高欄詳細図(32)		
縮 尺	図 示	図面番号	/
設計会社名	戸田建設株式会社		
施工会社名	戸田建設株式会社		
事務所名	東日本高速道路株式会社 北海道支社 札幌管理事務所		

千歳川大橋(下り線) P18-P24 プレキャスト壁高欄詳細図(33)


S=1:25

[中分側 R-48-FM]

(P19-P20径間 製作数 : 1) (P20-P21径間 製作数 : 1)
(P21-P22径間 製作数 : 1) (P22-P23径間 製作数 : 1)
(P23-P24径間 製作数 : 1)


断面図

1 - 1

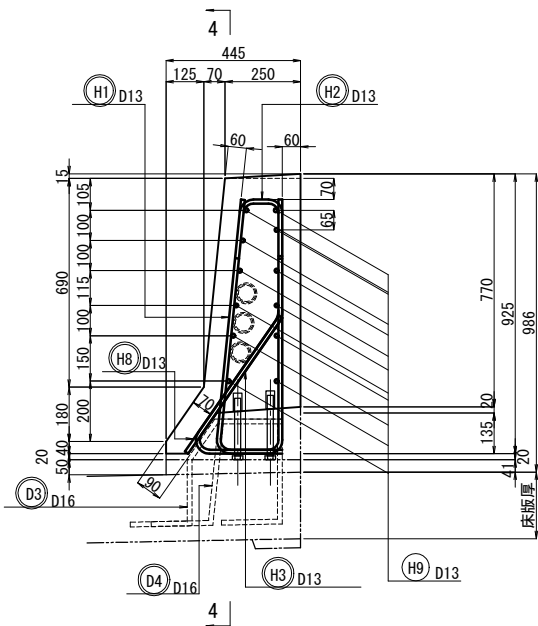


断面図

2 - 2

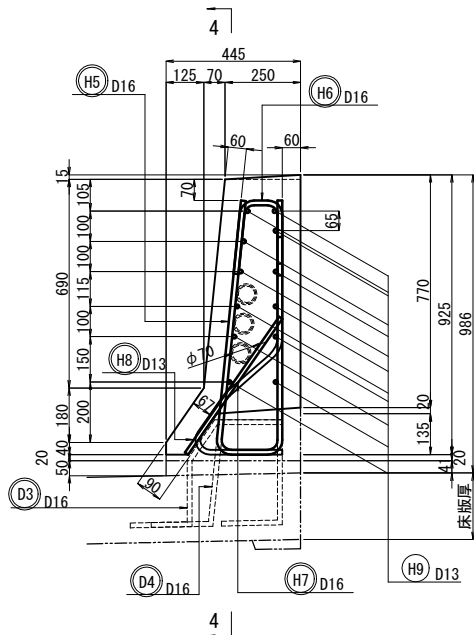


断面図

3 - 3

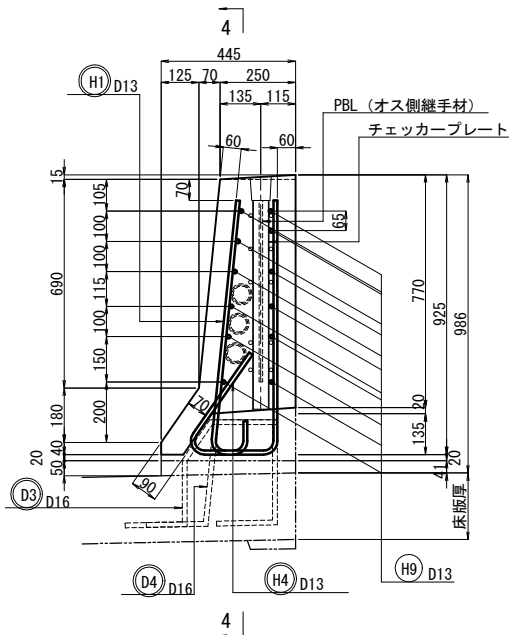


側面図

4 - 4





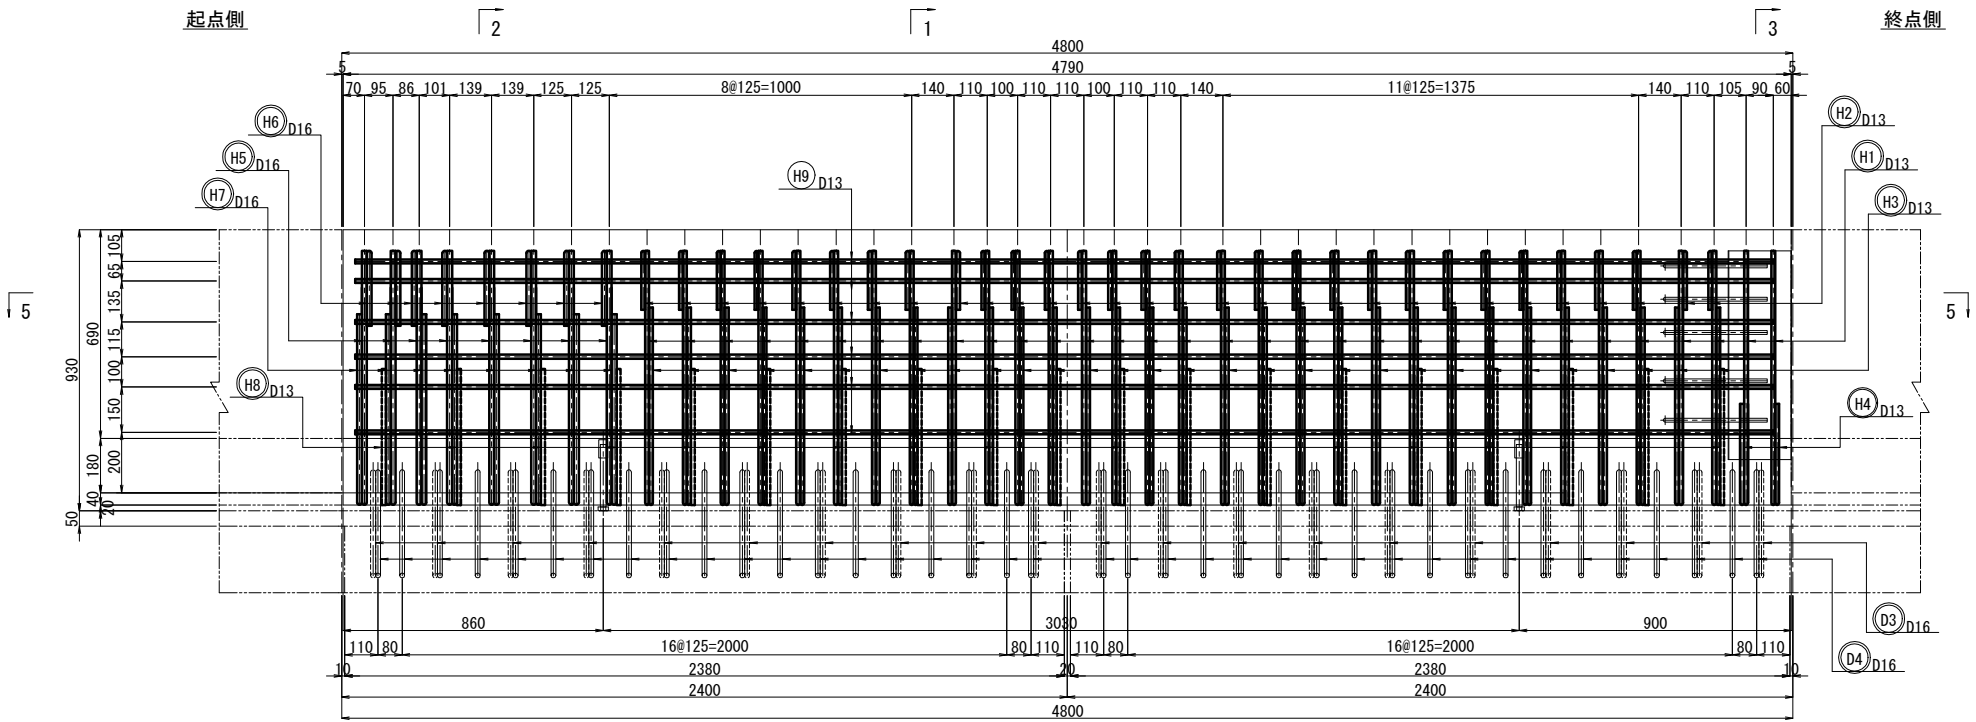


平面図

5 - 5

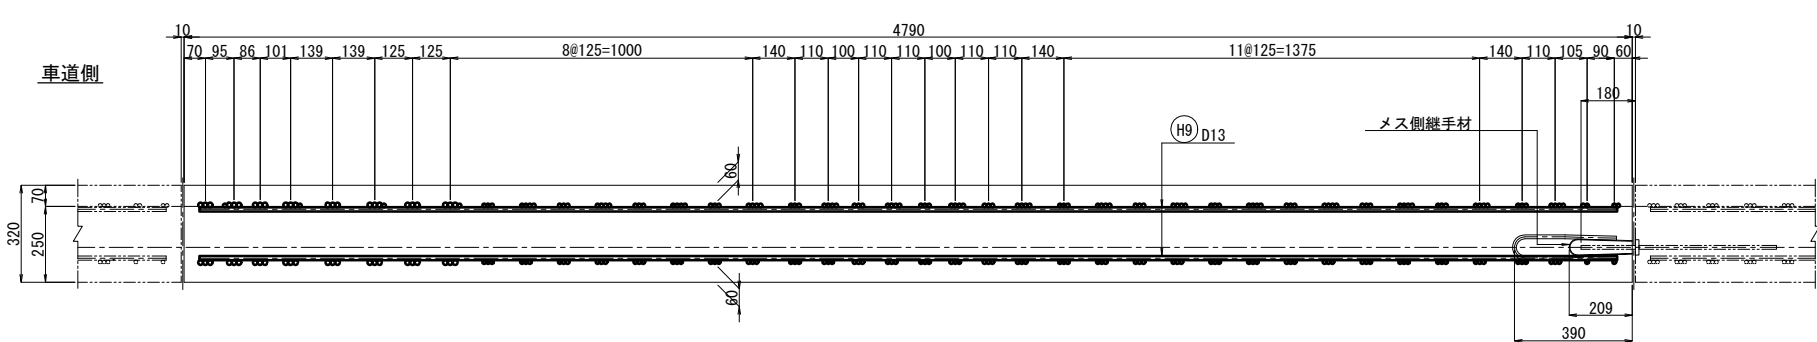

※ 鉄筋記号の  は塗装鉄筋を示す。
※ インサートおよび埋設管などの詳細位置は、壁高欄詳細図(34)を参照のこと。

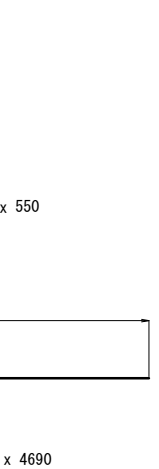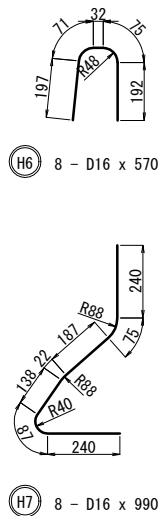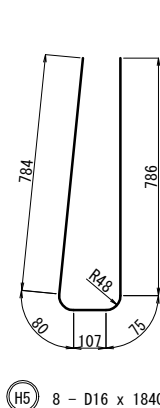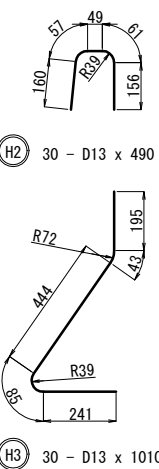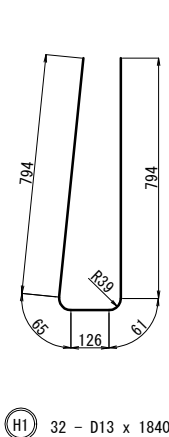

鉄筋表(1ブロック当り)						
鉄筋番号	材質	長さ (mm)	本数 (本)	単位重量 (kg/m)	1本当り質量 (kg)	備考
H1	D13	1840	32	0.995	1.831	EP塗装
H2	D13	490	30	0.995	0.488	EP塗装
H3	D13	1010	30	0.995	1.005	EP塗装
H4	D13	620	2	0.995	0.617	EP塗装
H5	D16	1840	8	1.56	2.870	EP塗装
H6	D16	570	8	1.56	0.889	EP塗装
H7	D16	990	8	1.56	1.544	EP塗装
H8	D13	550	19	0.995	0.547	EP塗装
H9	D13	4690	12	0.995	4.667	EP塗装
合 計					213	kg
鉄筋質量集計(SD345)						
		普通鉄筋		塗装鉄筋		
D16		0 kg		42 kg		42 kg
D13		56 kg		115 kg		171 kg
合計		56 kg		157 kg		213 kg

道央自動車道 千歳川大橋(下り線) 床版取替工事			
図面の種類	千歳川大橋(下り線) P18-P24 プレキャスト壁高欄詳細図(33)		
縮 尺	図 示	図面番号	/
設計会社名	戸田建設株式会社		
施工会社名	戸田建設株式会社		
事務所名	東日本高速道路株式会社 北海道支社 札幌管理事務所		







千歳川大橋(下り線) P18-P24 プレキャスト壁高欄詳細図(34)

S=1:25

[中分側 R-48-FM]

(P19-P20径間 製作数 : 1) (P20-P21径間 製作数 : 1)
(P21-P22径間 製作数 : 1) (P22-P23径間 製作数 : 1)
(P23-P24径間 製作数 : 1)

インサート配置側面図

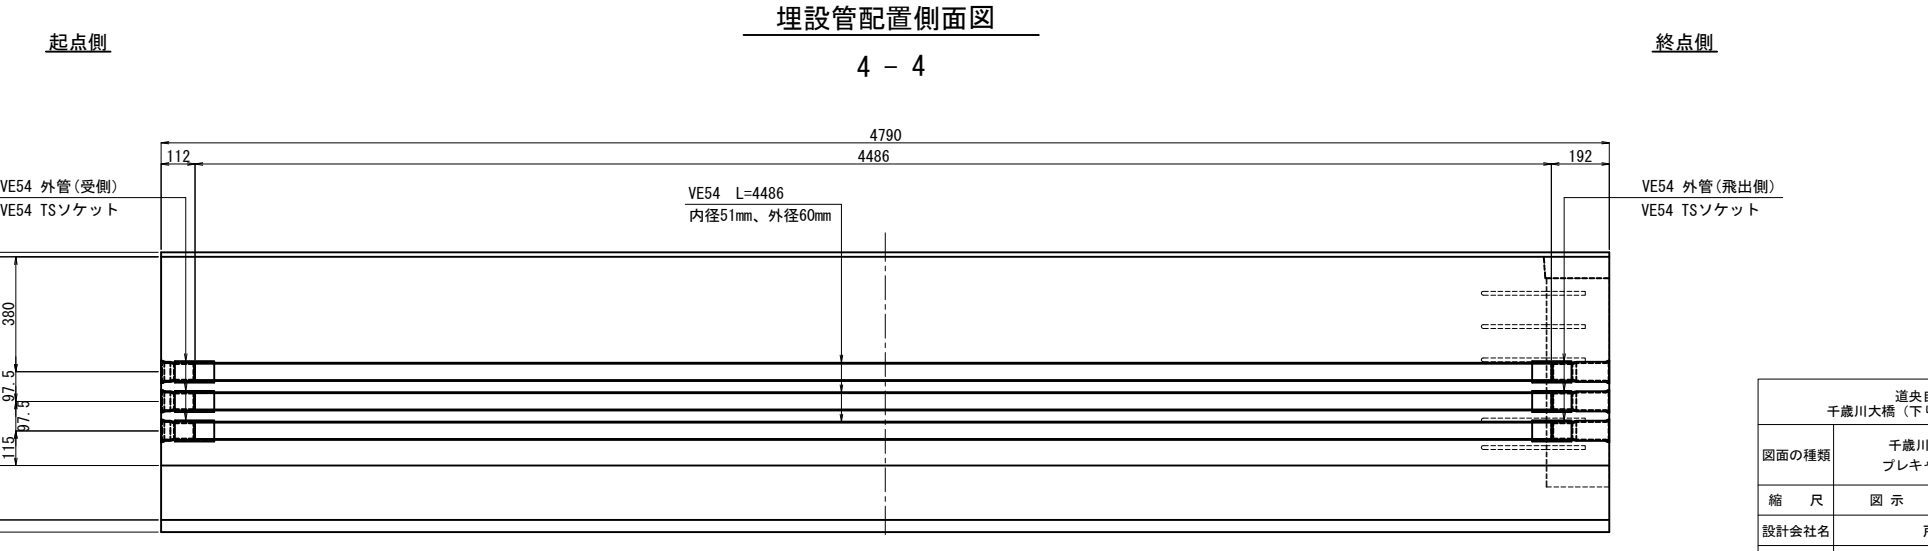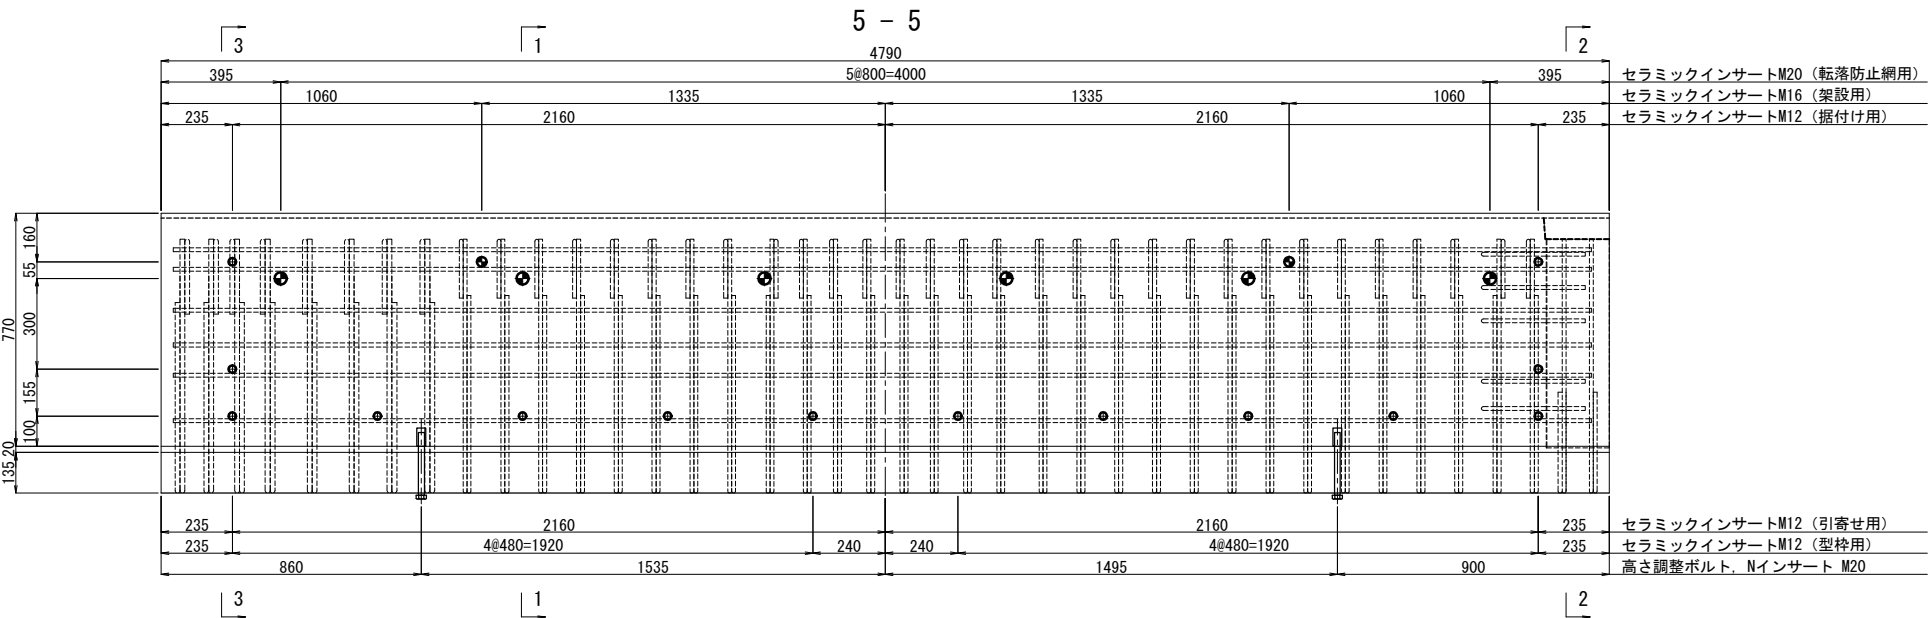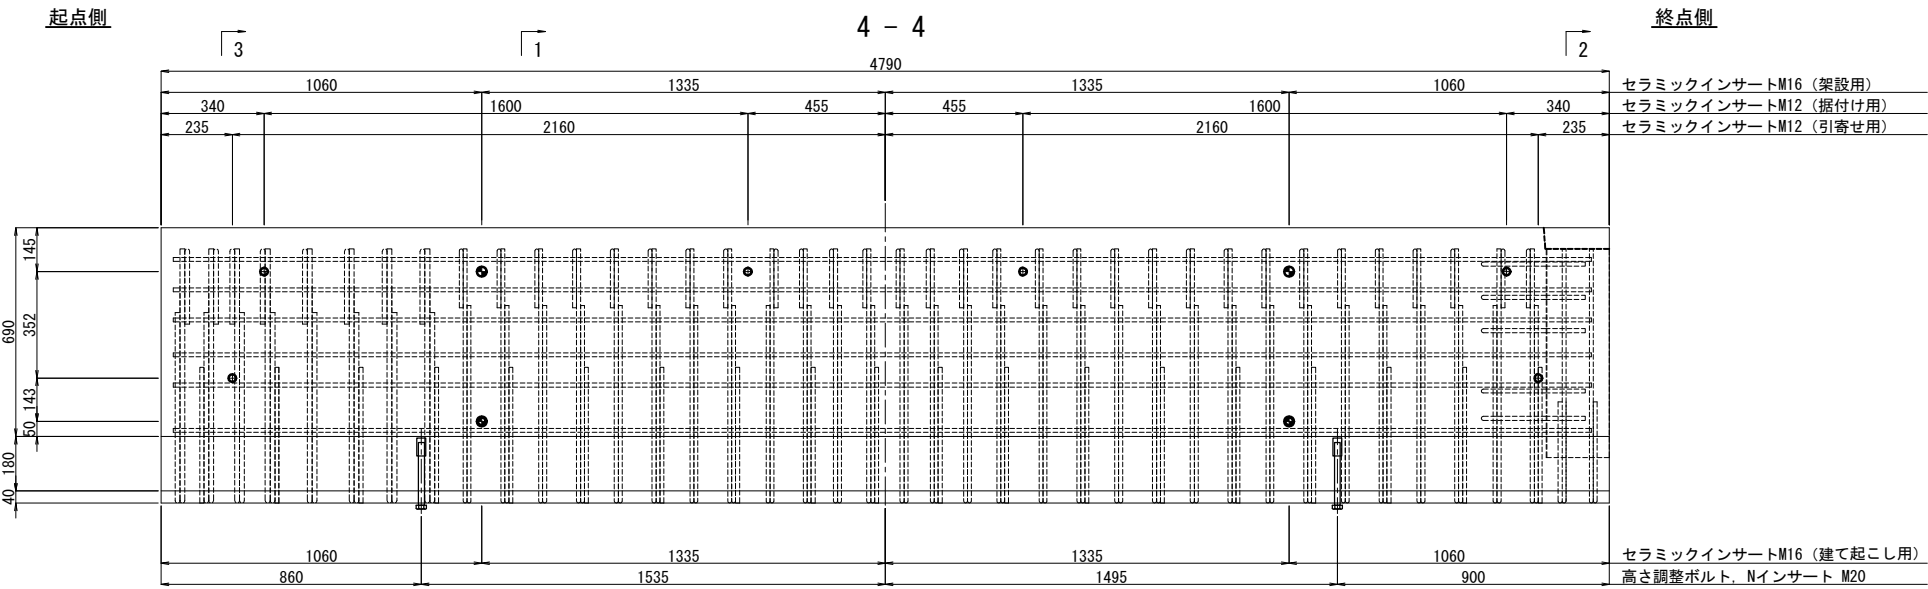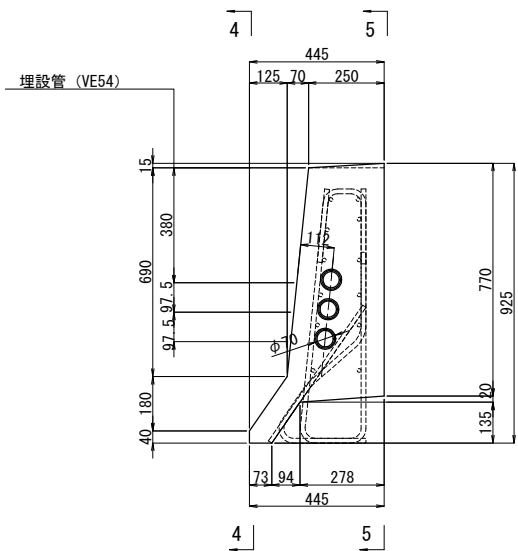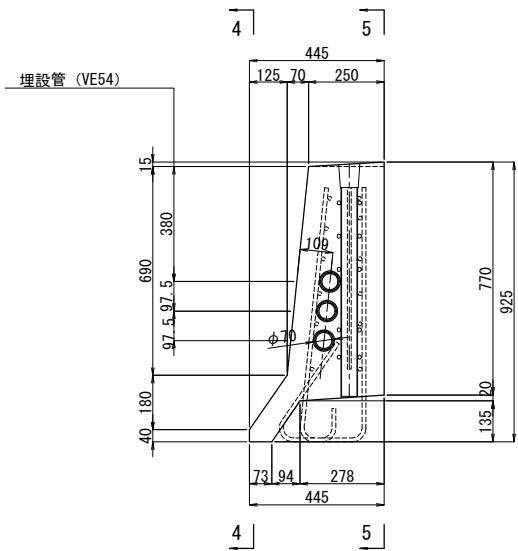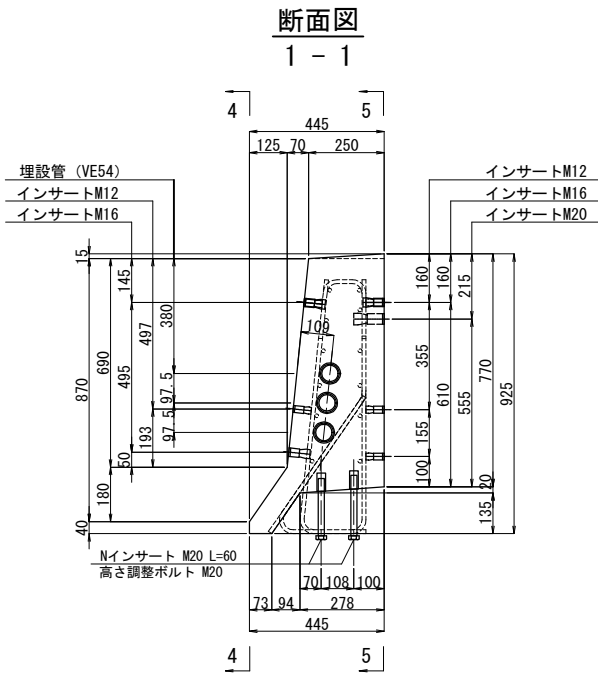

道央自動車道 千歳川大橋(下り線) 床版取替工事			
図面の種類	千歳川大橋(下り線) P18-P24 プレキャスト壁高欄詳細図(34)		
縮 尺	図 示	図面番号	/
設計会社名	戸田建設株式会社		
施工会社名	戸田建設株式会社		
事務所名	東日本高速道路株式会社 北海道支社 札幌管理事務所		

千歳川大橋(下り線) P18-P24 プレキャスト壁高欄詳細図(35)


S=1:25

[中分側 R-24-FF]

(P21上 製作数 : 1)


断面図

1 - 1

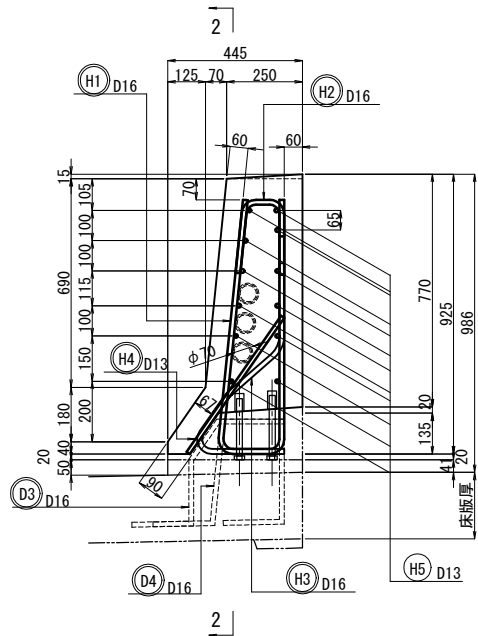






側面図

2 - 2

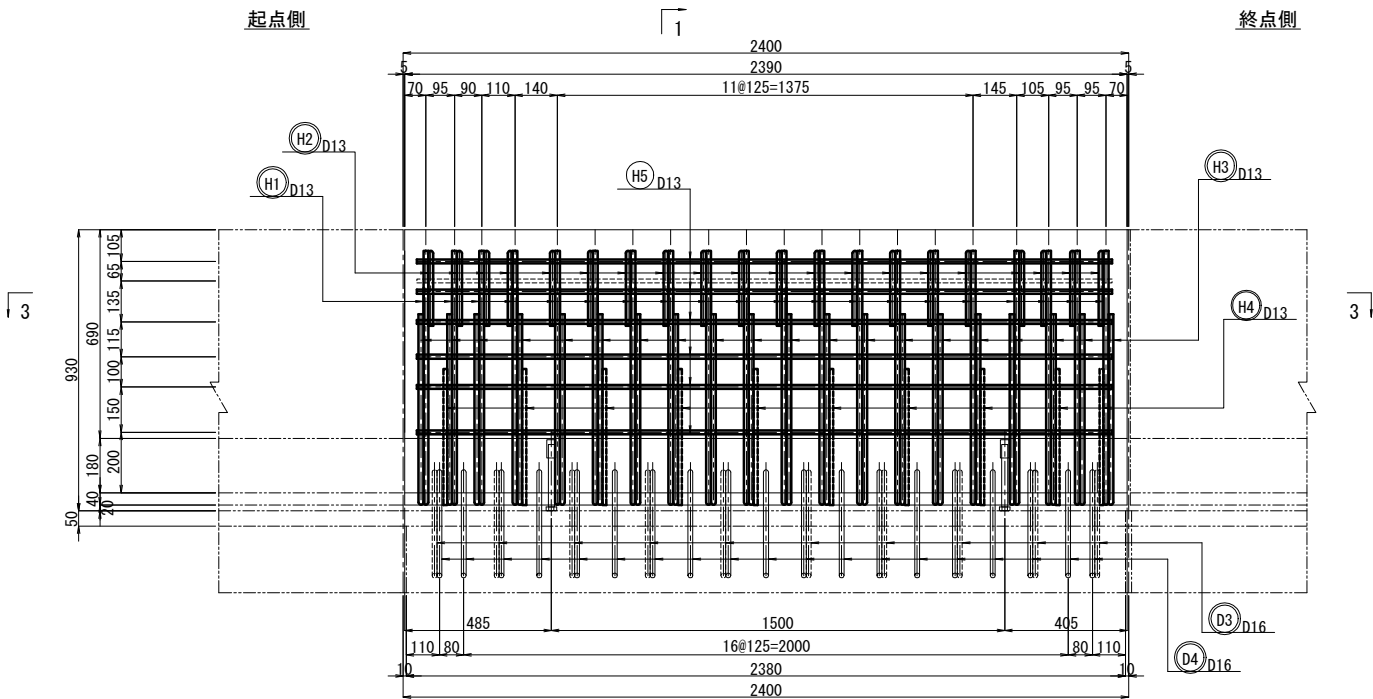

平面図

3 - 3

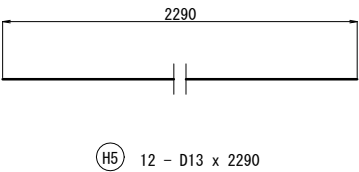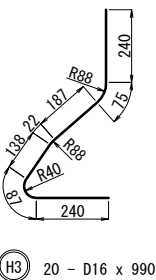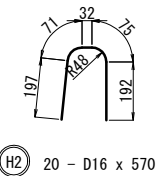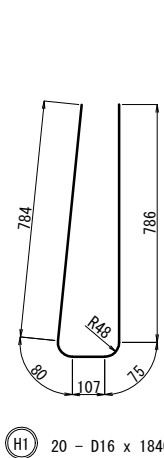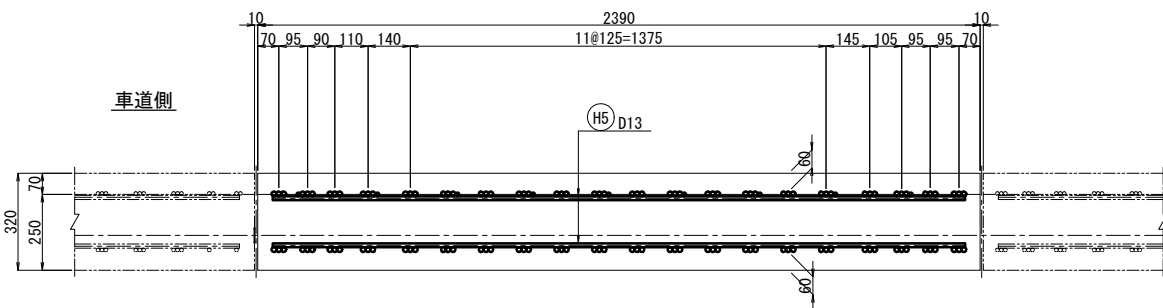

鉄筋表(1ブロック当り)

鉄筋番号	材質	長さ (mm)	本数 (本)	単位重量 (kg/m)	1本当り質量 (kg)	質量 (kg)	備考
H1	D16	1840	20	1.56	2.870	57	EP塗装
H2	D16	570	20	1.56	0.889	18	EP塗装
H3	D16	990	20	1.56	1.544	31	EP塗装
H4	D13	550	10	0.995	0.547	5	EP塗装
H5	D13	2290	12	0.995	2.279	27	
合 計						138	kg
鉄筋質量集計 (SD345)							
				普通鉄筋	塗装鉄筋		
				D16	0 kg	106 kg	106 kg
				D13	27 kg	5 kg	32 kg
				合計	27 kg	111 kg	138 kg

※ 鉄筋記号の○は塗装鉄筋を示す。

※ インサートおよび埋設管などの詳細位置は、壁高欄詳細図(36)を参照のこと。


道央自動車道 千歳川大橋(下り線)床版取替工事			
図面の種類	千歳川大橋(下り線) P18-P24 プレキャスト壁高欄詳細図(35)		
縮 尺	図 示	図面番号	/
設計会社名	戸田建設株式会社		
施工会社名	戸田建設株式会社		
事務所名	東日本高速道路株式会社 北海道支社 札幌管理事務所		

[中分側 R-24-FF]

(P21上 製作数 : 1)


断面図

1 - 1

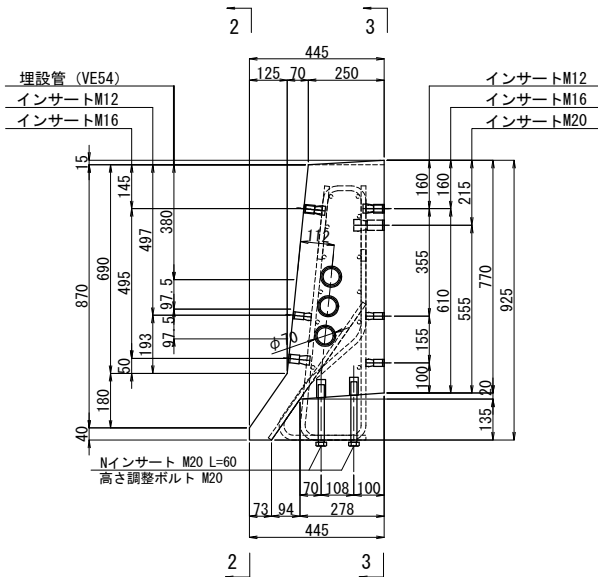


インサート配置側面図

2 - 2

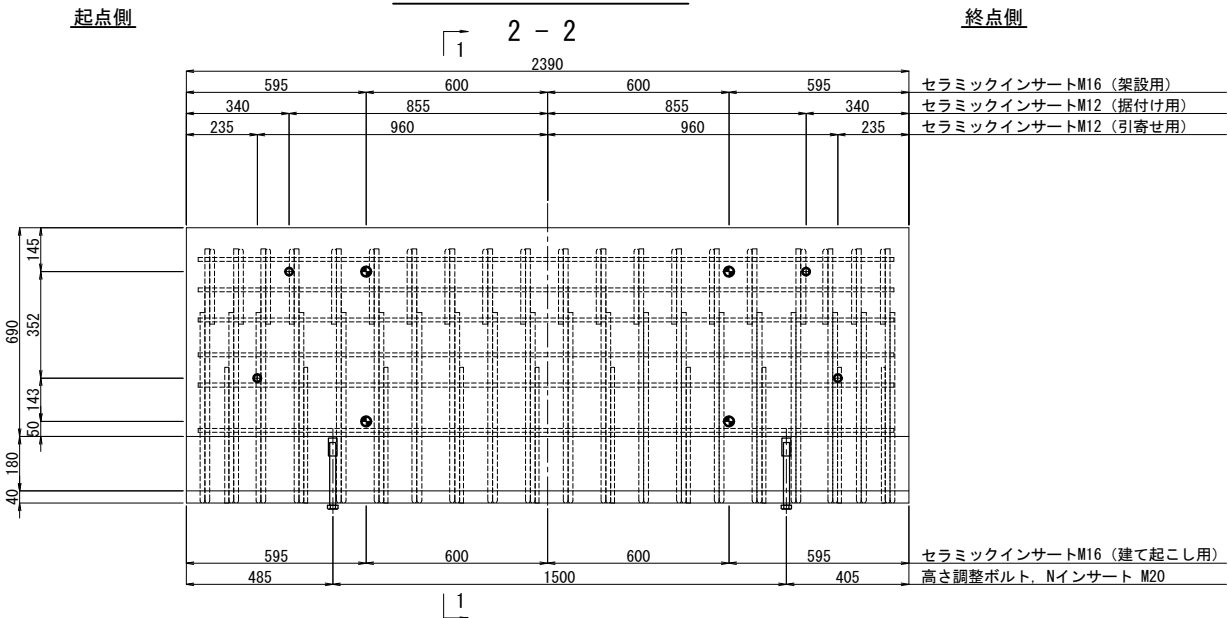


3 - 3

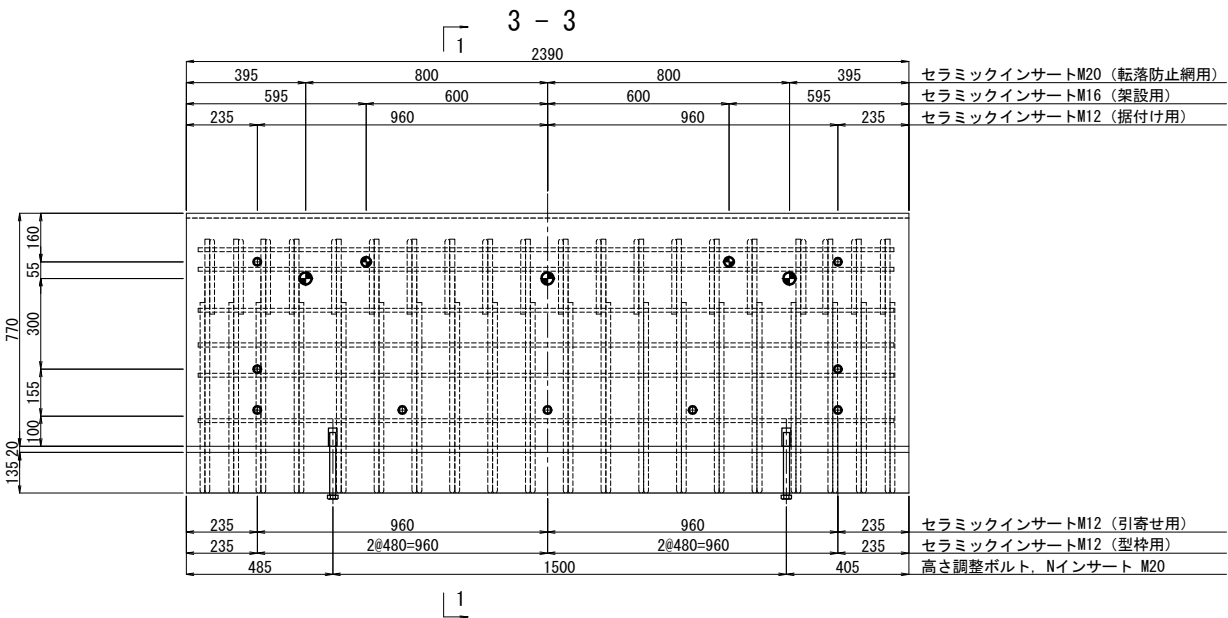

埋設管配置側面図

2 - 2

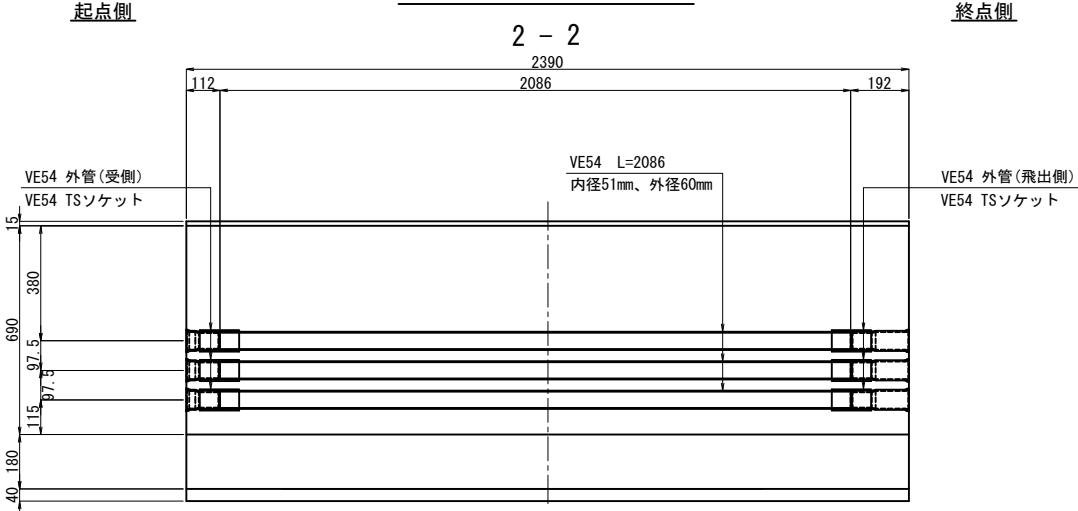

道央自動車道 千歳川大橋(下り線) 床版取替工事			
図面の種類	千歳川大橋(下り線) P18-P24 プレキャスト壁高欄詳細図(36)		
縮 尺	図 示	図面番号	/
設計会社名	戸田建設株式会社		
施工会社名	戸田建設株式会社		
事務所名	東日本高速道路株式会社 北海道支社 札幌管理事務所		

千歳川大橋(下り線) P18-P24 プレキャスト壁高欄詳細図(37)


S=1:25

[中分側 R-E3-0M]

(P23-P24径間 製作数 : 1)


断面図

1 - 1

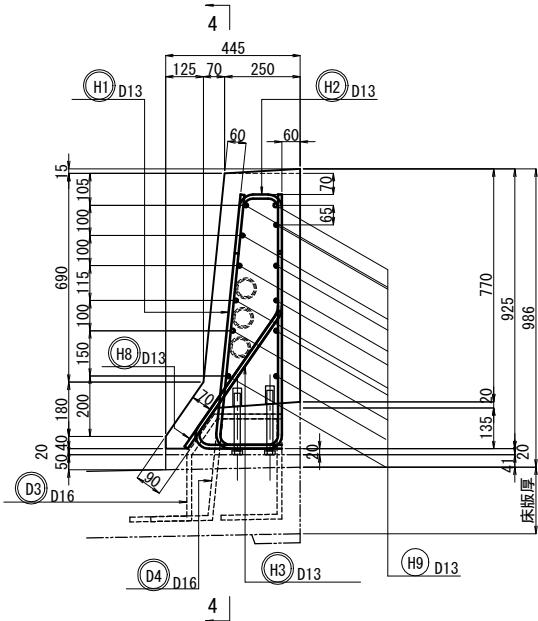


断面図

2 - 2

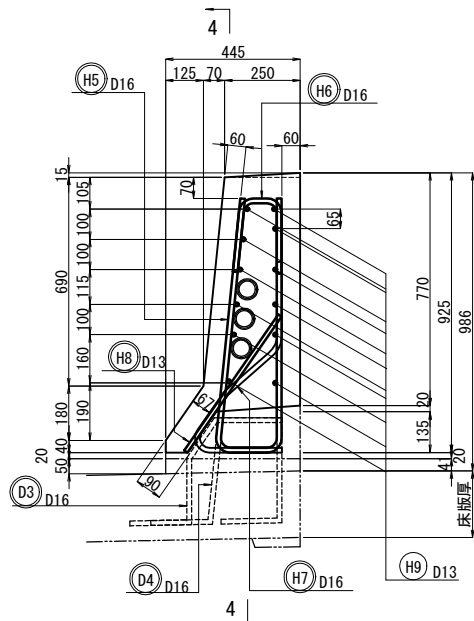


断面図

3 - 3

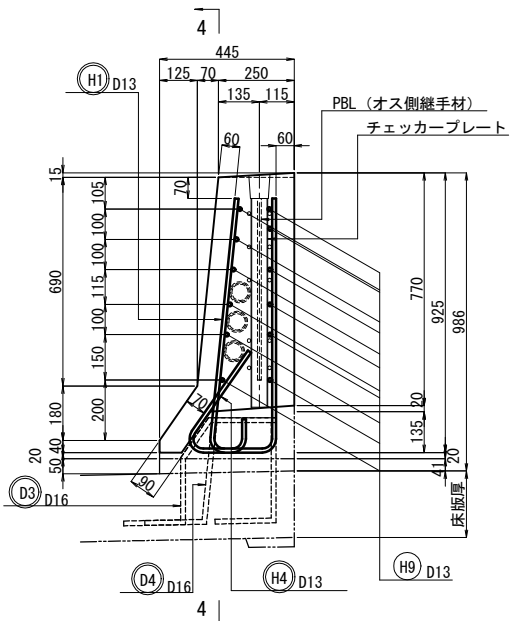


側面図

4 - 4

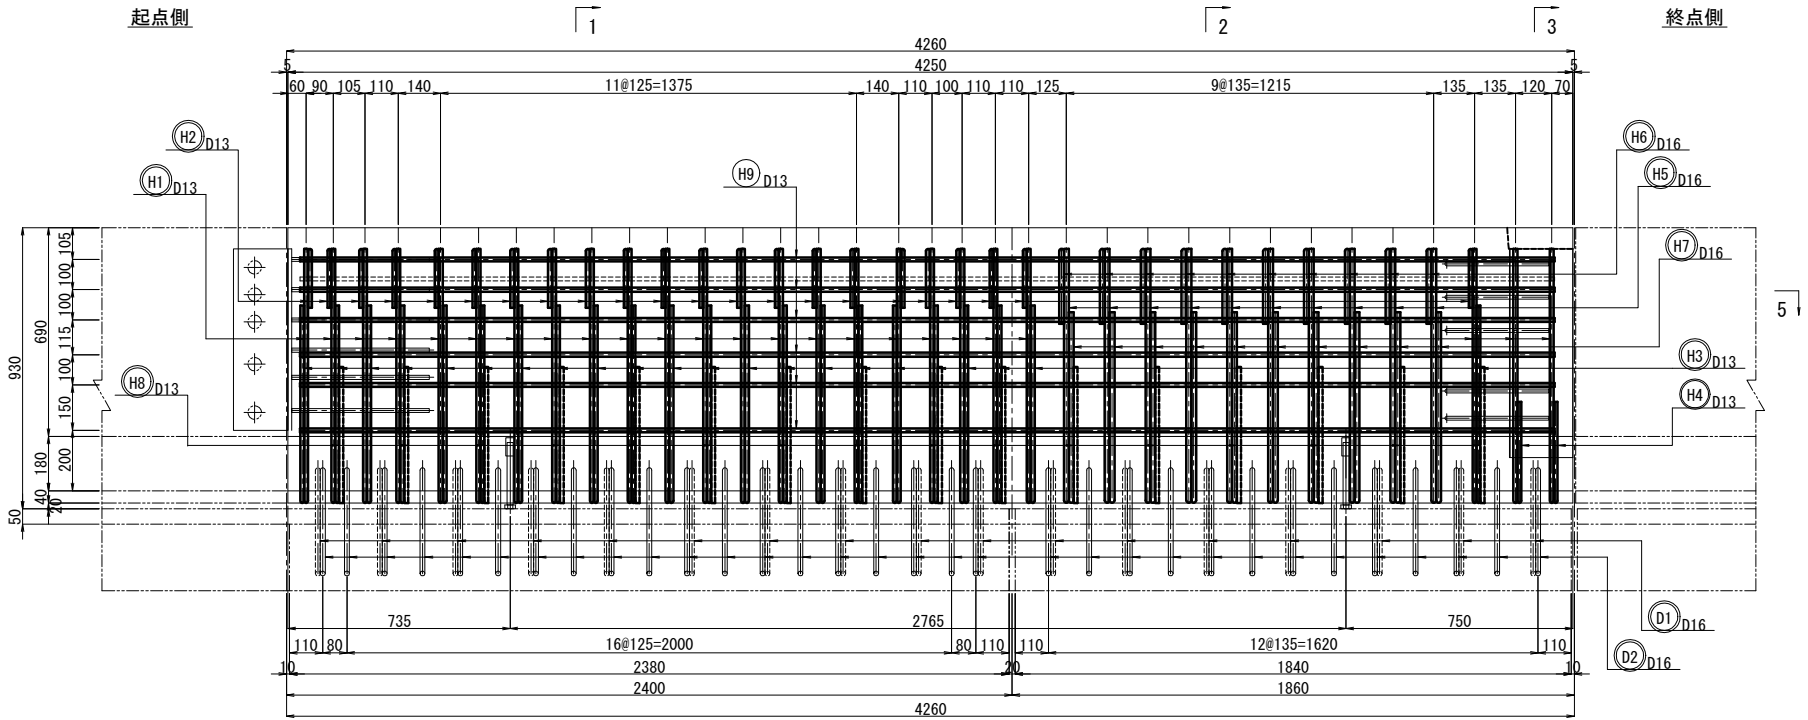




平面図

5 - 5

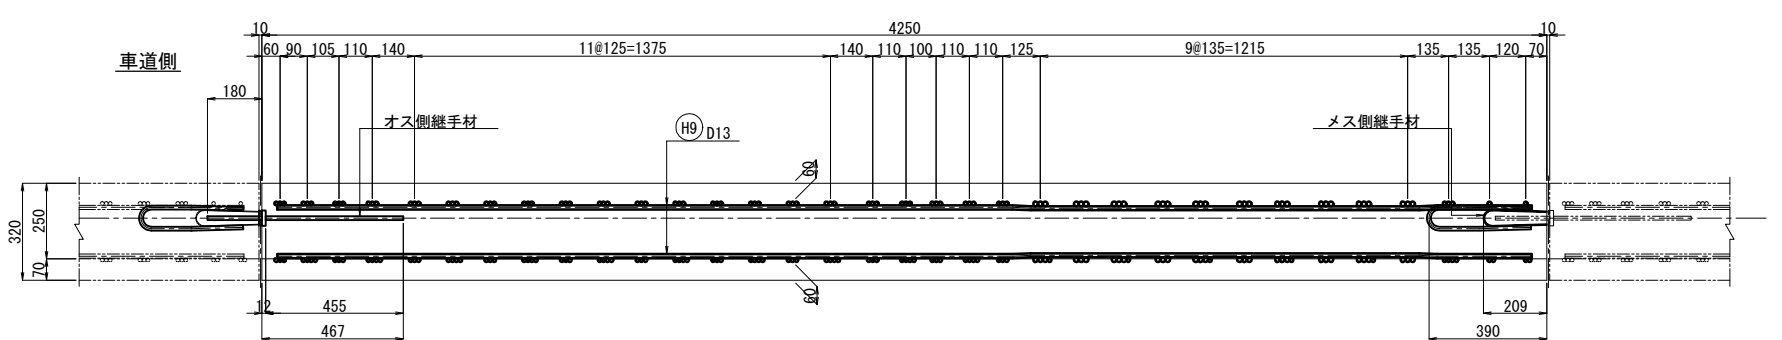

※ 鉄筋記号の○は塗装鉄筋を示す。
※ インサートおよび埋設管などの詳細位置は、壁高欄詳細図(38)を参照のこと。

鉄筋表(1ブロック当り)						
鉄筋番号	材質	長さ (mm)	本数	単位重量 (kg/m)	1本当り質量 (kg)	質量 (kg)
H1	D13	1840	24	0.995	1.831	44
H2	D13	490	22	0.995	0.488	11
H3	D13	1010	22	0.995	1.005	22
H4	D13	620	2	0.995	0.627	1
H5	D16	1840	10	1.56	2.870	29
H6	D16	570	10	1.56	0.889	9
H7	D16	990	10	1.56	1.544	15
H8	D13	550	16	0.995	0.547	9
H9	D13	4150	12	0.995	4.129	50
合 計						190 kg
鉄筋質量集計 (SD345)						
		普通鉄筋		塗装鉄筋		
D16		0 kg		53 kg		53 kg
D13		50 kg		87 kg		137 kg
合計		50 kg		140 kg		190 kg

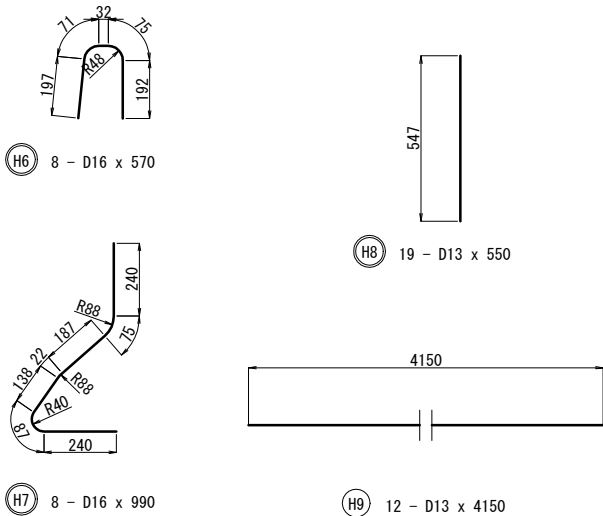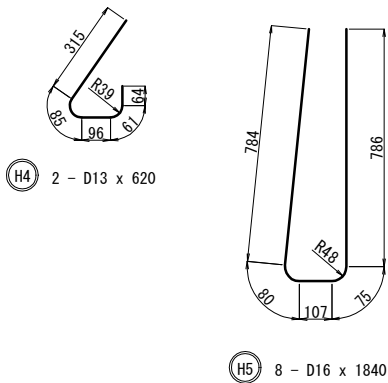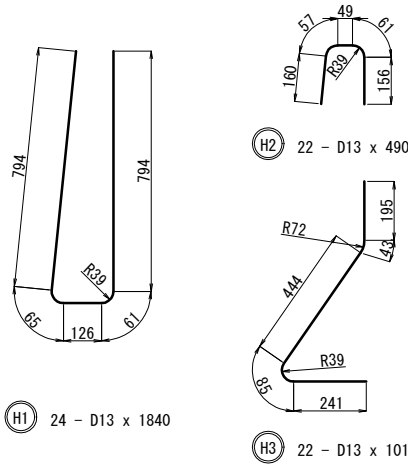

道央自動車道 千歳川大橋(下り線) 床版取替工事			
図面の種類	千歳川大橋(下り線) P18-P24 プレキャスト壁高欄詳細図(37)		
縮 尺	図 示	図面番号	/
設計会社名	戸田建設株式会社		
施工会社名	戸田建設株式会社		
事務所名	東日本高速道路株式会社 北海道支社 札幌管理事務所		

千歳川大橋(下り線) P18-P24 プレキャスト壁高欄詳細図(38)


S=1:25

[中分側 R-E3-0M]


(P23-P24径間 製作数 : 1)

断面図

1 - 1

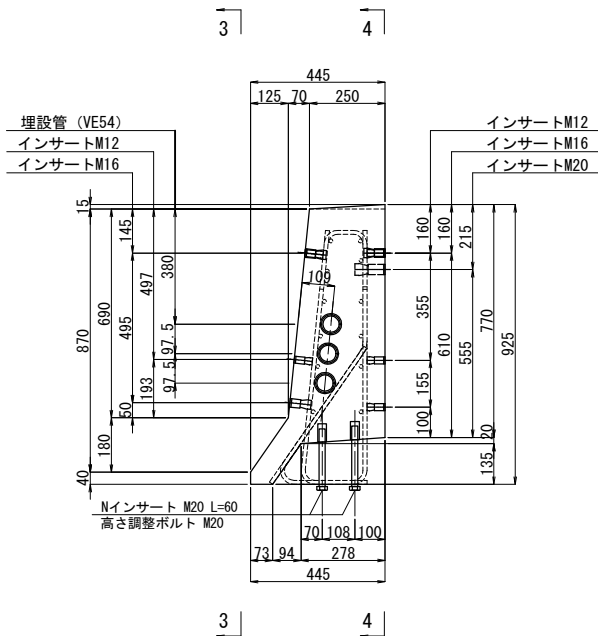


2 - 2

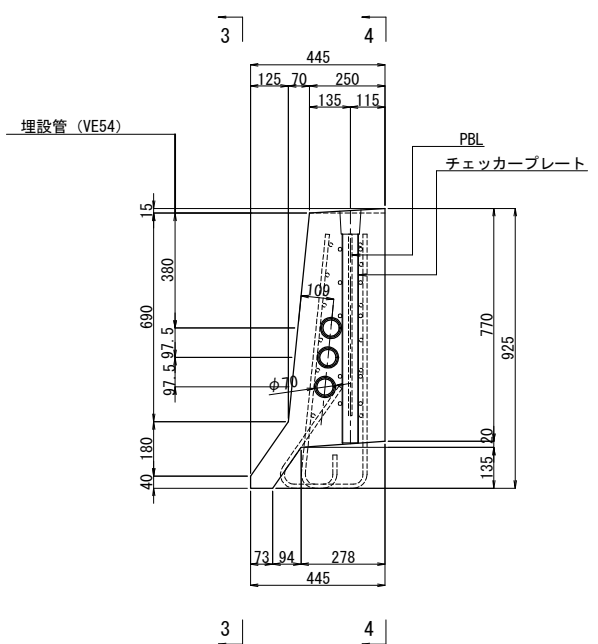


インサート配置側面図

3 - 3

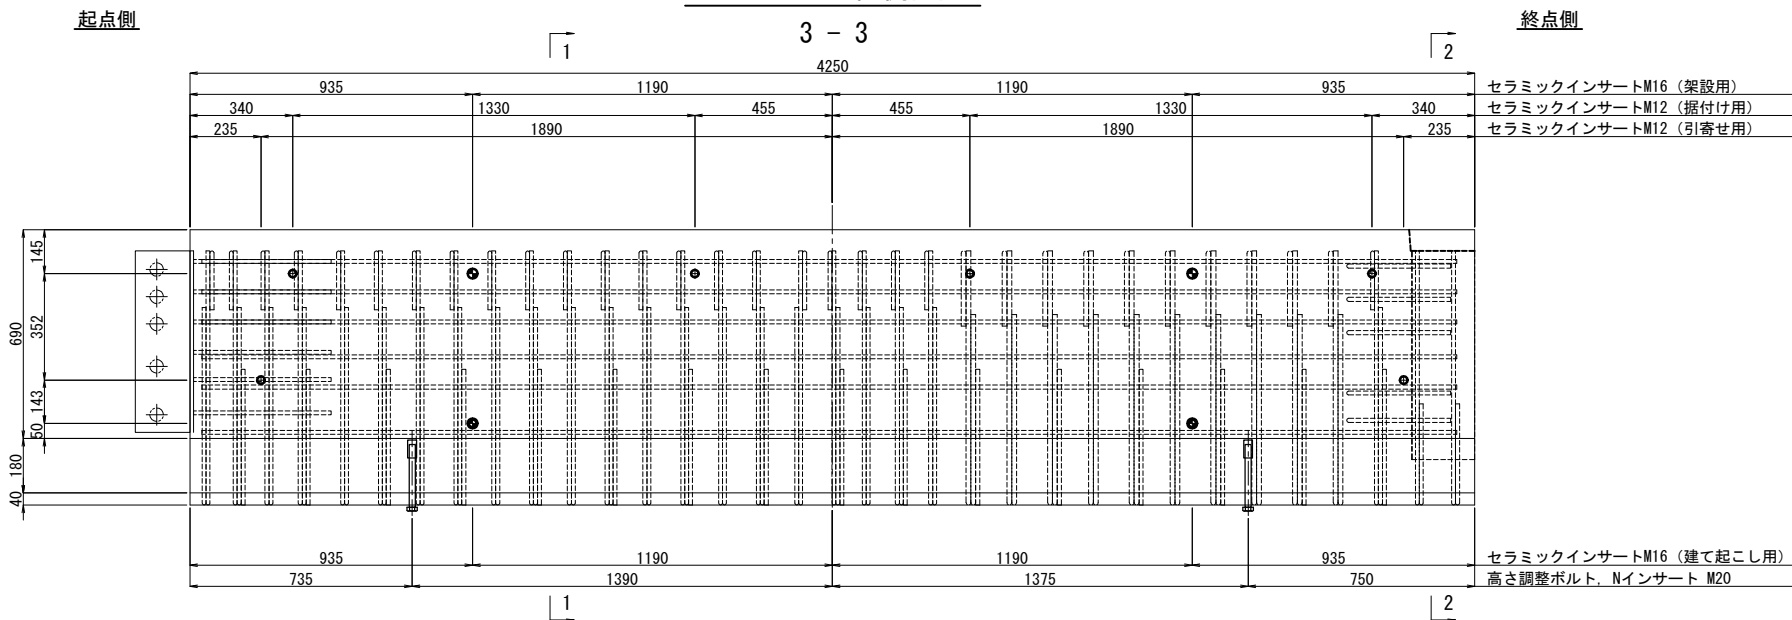


4 - 4

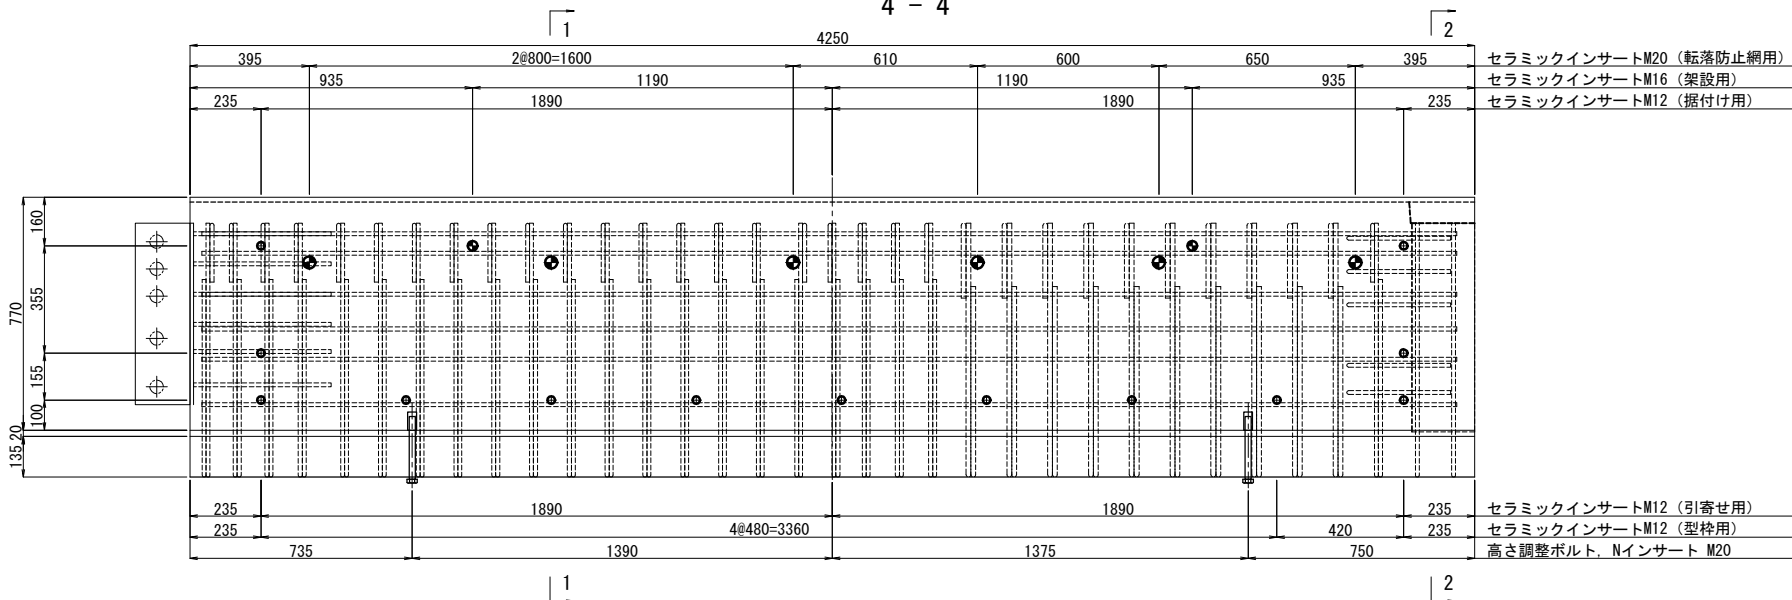

埋設管配置側面図

3 - 3

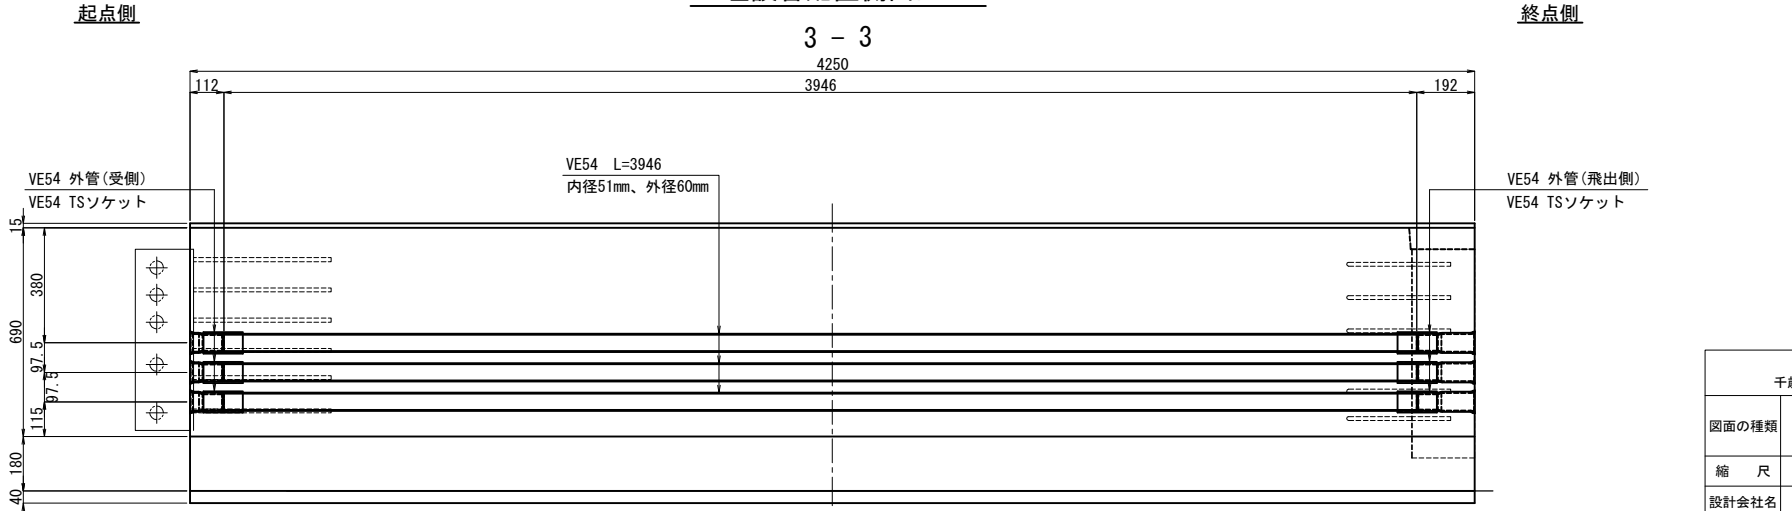


道央自動車道 千歳川大橋(下り線)床版取替工事			
図面の種類	千歳川大橋(下り線) P18-P24 プレキャスト壁高欄詳細図(38)		
縮 尺	図 示	図面番号	/
設計会社名	戸田建設株式会社		
施工会社名	戸田建設株式会社		
事務所名	東日本高速道路株式会社 北海道支社 札幌管理事務所		


S=1 : 25

(P18-P19径間 製作数 : 1) (P19-P20径間 製作数 : 1)
(P21-P22径間 製作数 : 1)


1 - 1

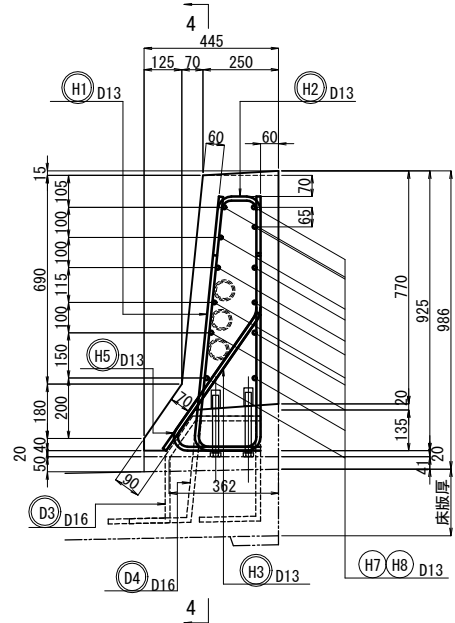


4 - 4

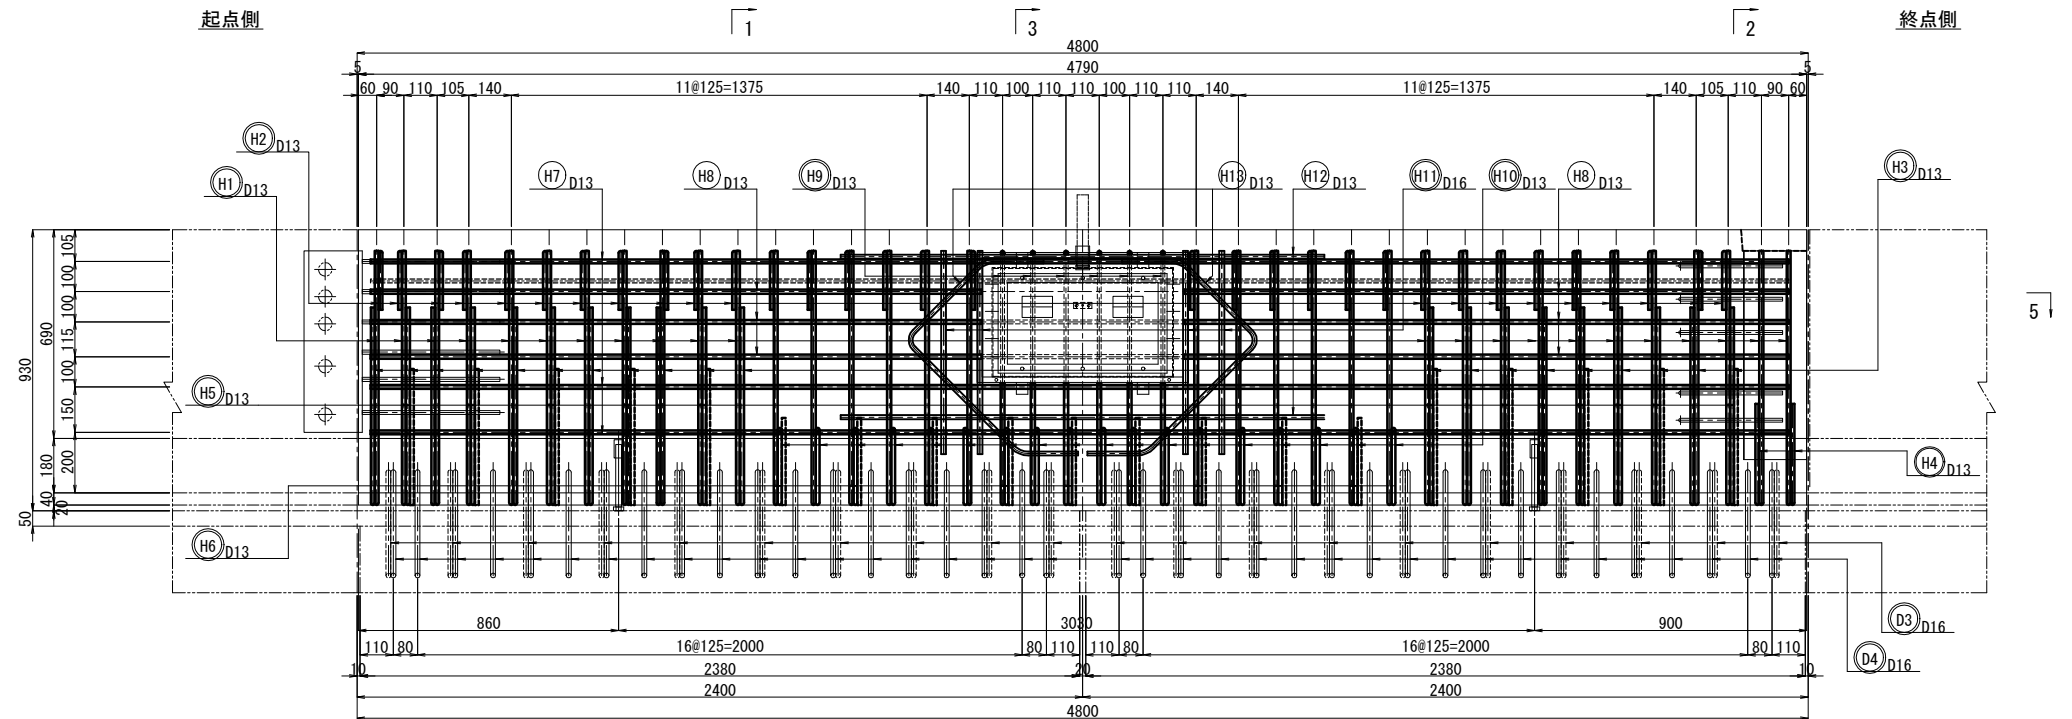


2 - 2

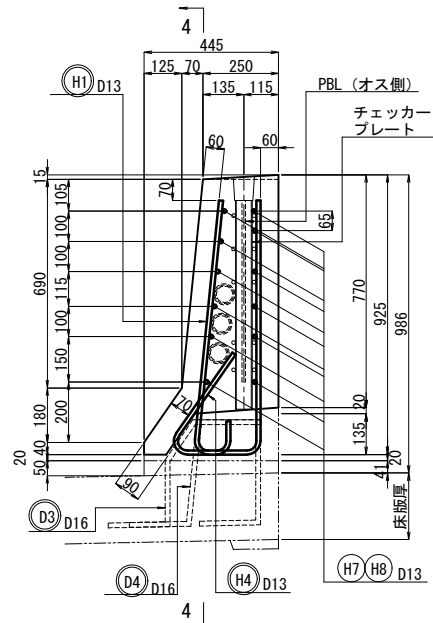








3 - 3

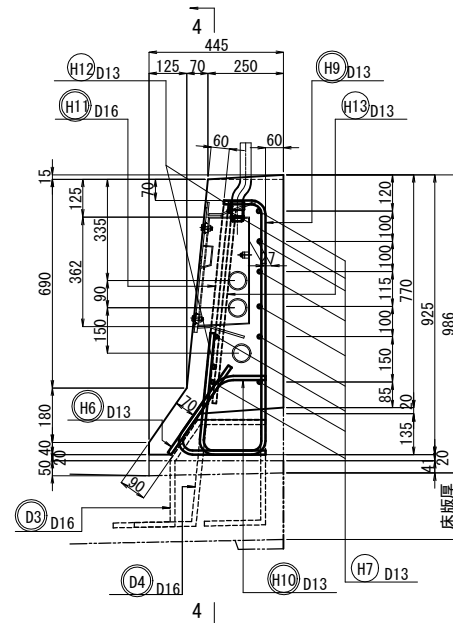

5 - 5

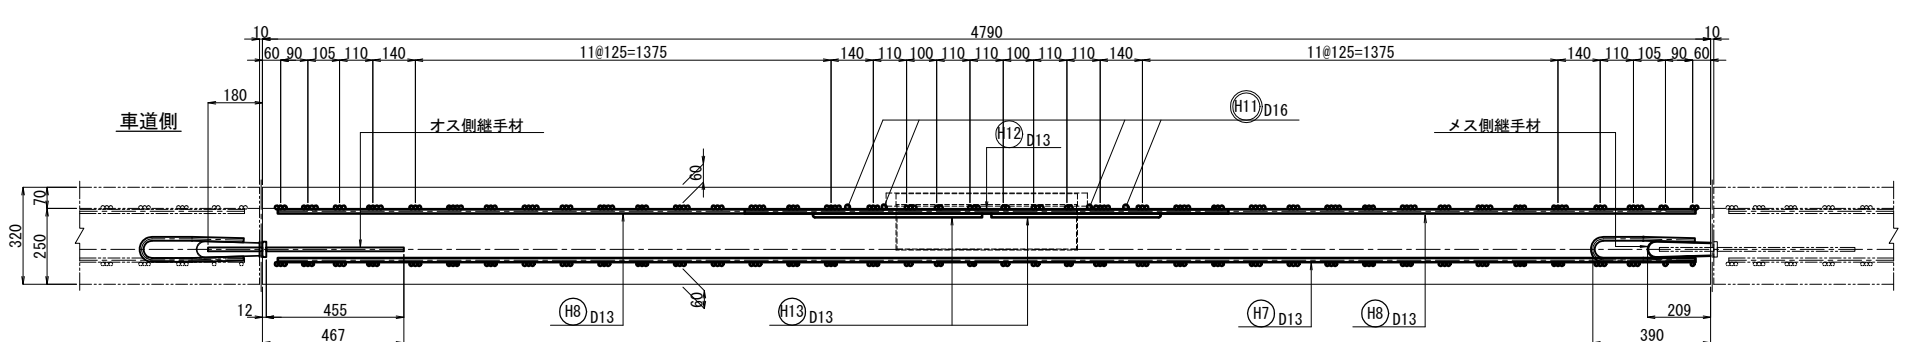

※ インサートおよび埋設管などの詳細位置は、壁高欄詳細図(40)を参照のこと。

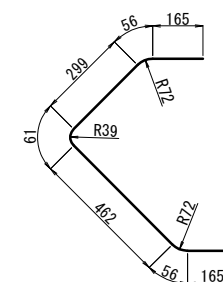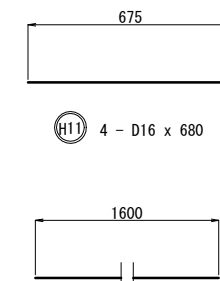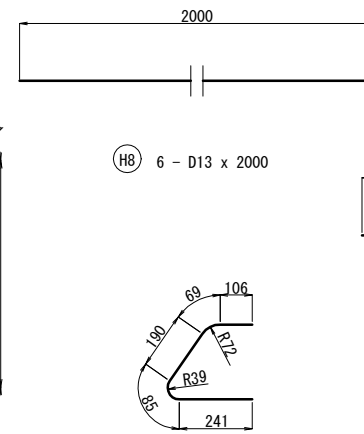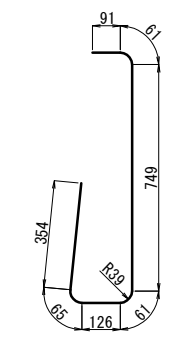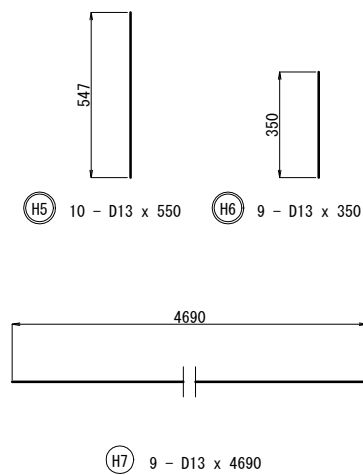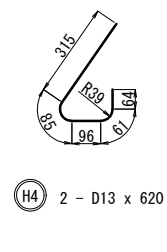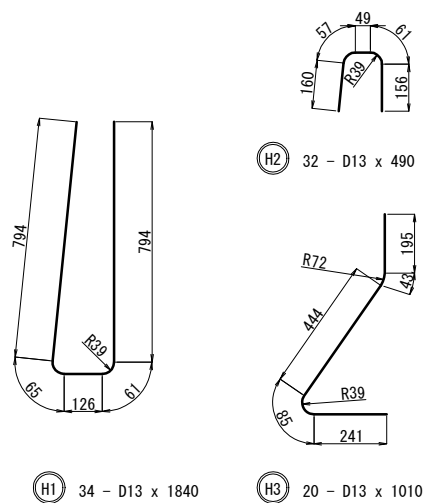

道央自動車道 千歳川大橋（下り線）床版取替工事			
図面の種類	千歳川大橋（下り線）P18～P24 プレキャスト重高欄詳細図 (39)		
縮 尺	図 示	図面番号	/
設計会社名	戸田建設株式会社		
施工会社名	戸田建設株式会社		
事務所名	東日本高速道路株式会社 北海道支社 札幌管理事務所		

千歳川大橋(下り線) P18-P24 プレキャスト壁高欄詳細図(40)



S=1:25

[中分側 R-48-0M-SP]


(P18-P19径間 製作数 : 1) (P19-P20径間 製作数 : 1)
(P21-P22径間 製作数 : 1)

※スノーボール用アンカーの埋込深さについては共通詳細図(9)を参照のこと。


断面図
1 - 1

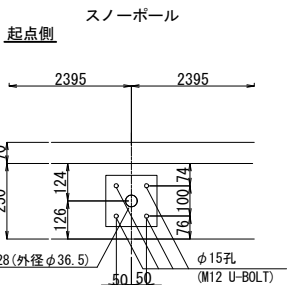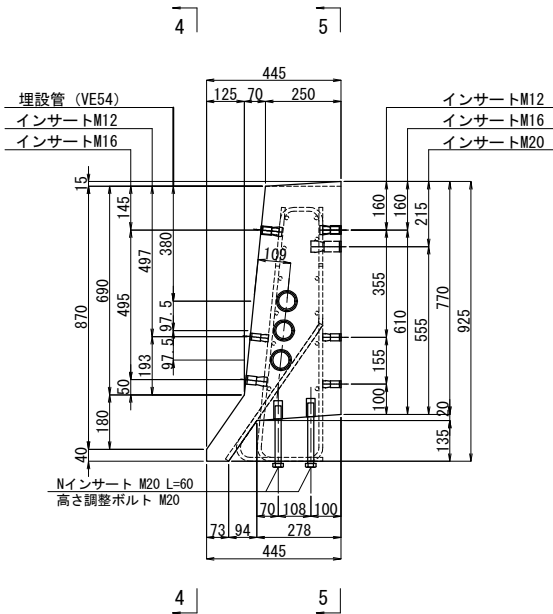


インサート配置側面図

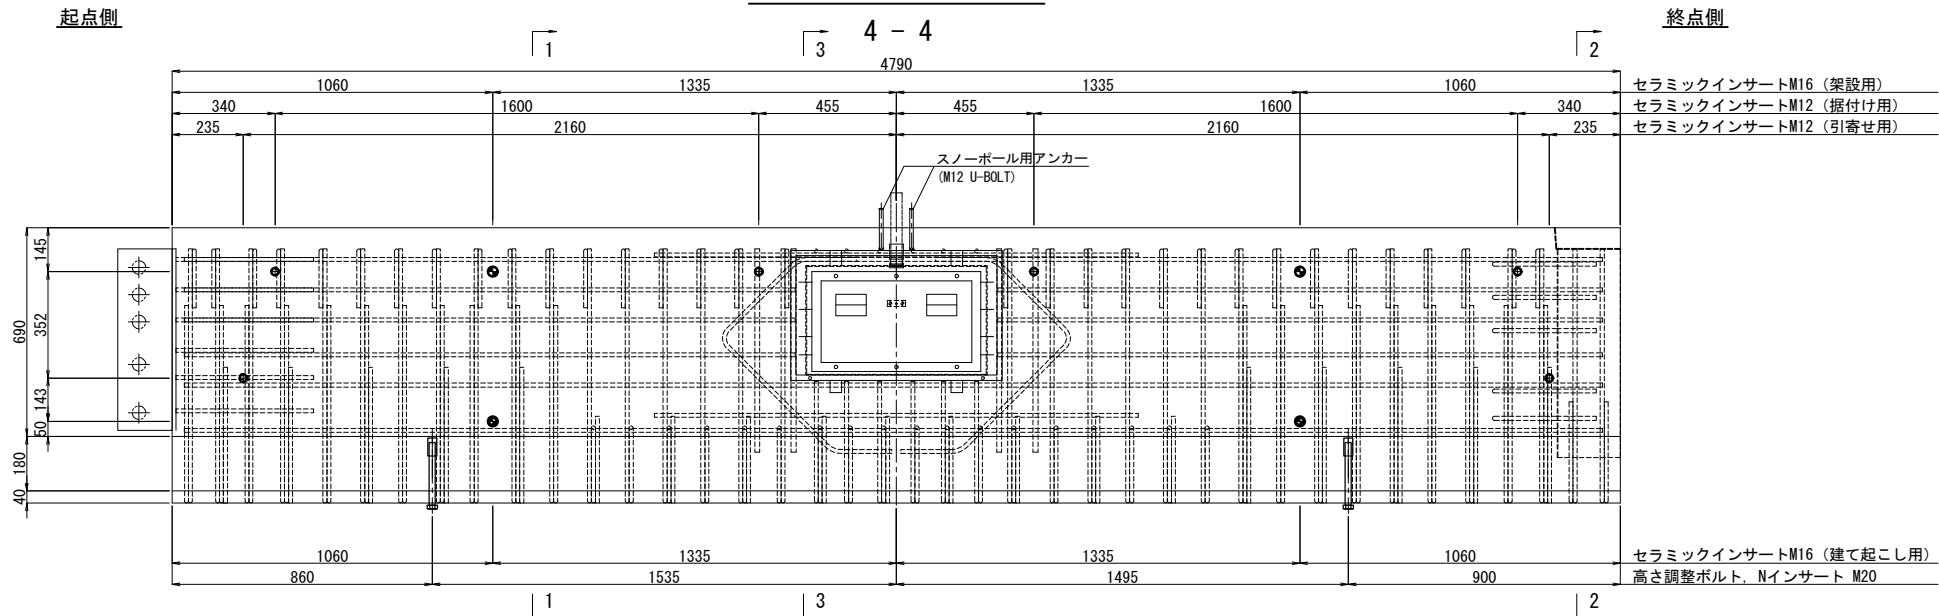


2 - 2

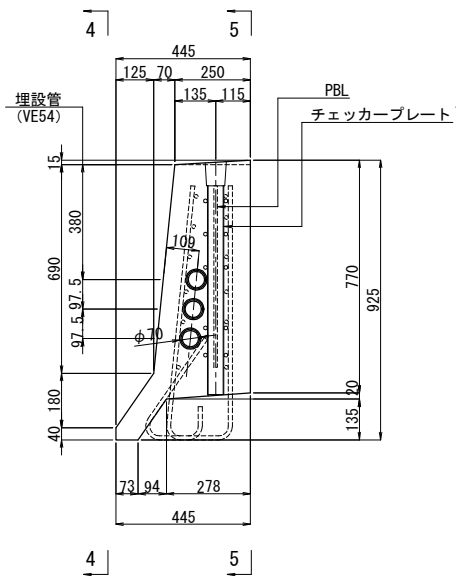

3 - 3

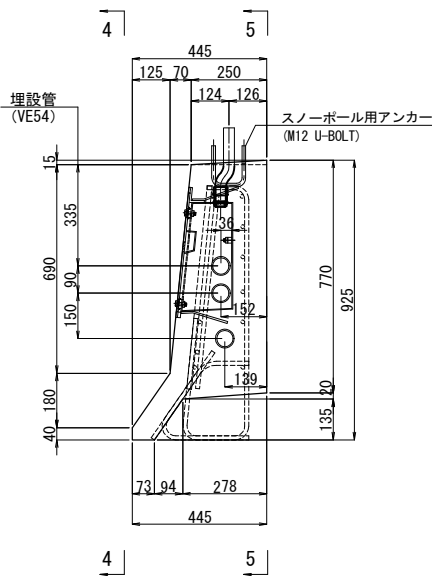


5 - 5

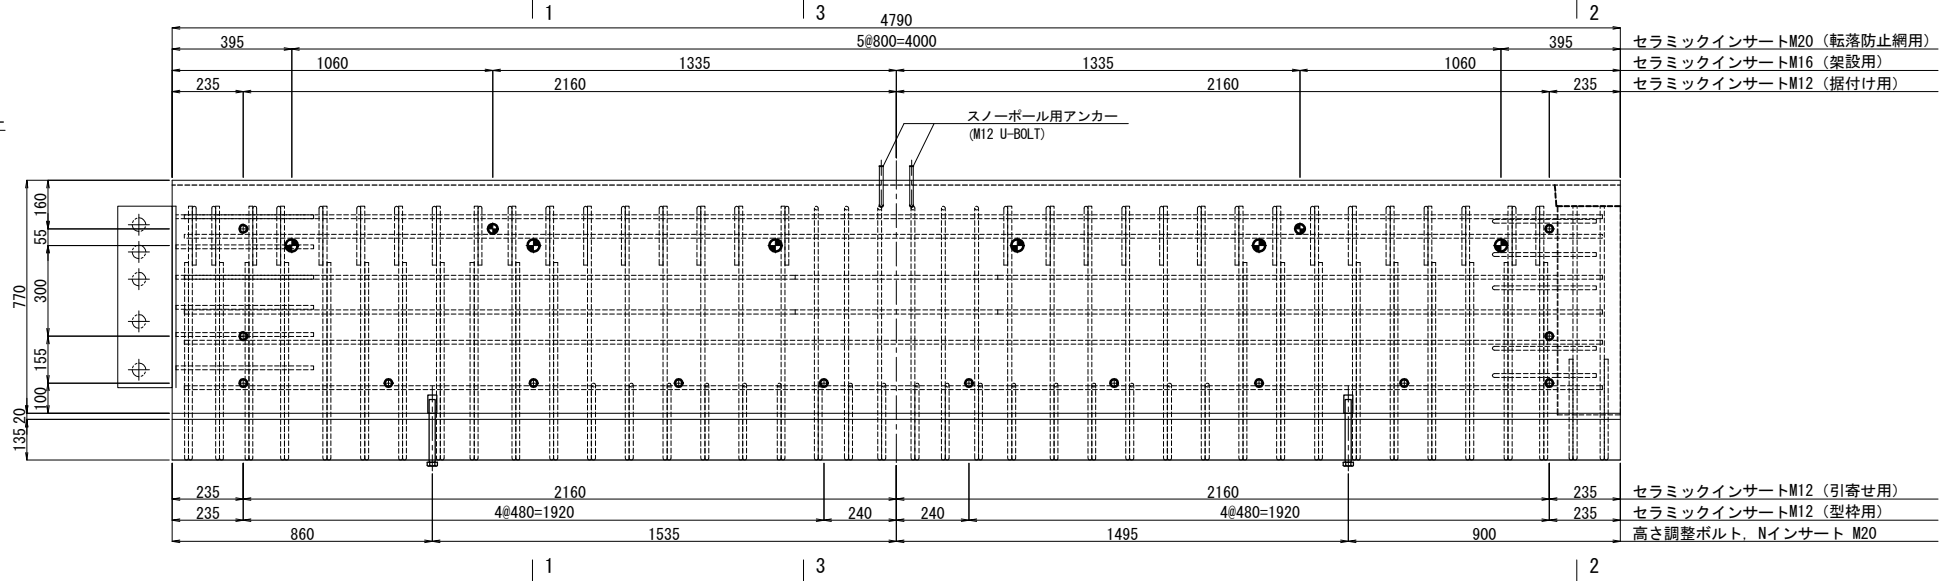

鉄筋表(1ブロック当り)

鉄筋番号	材質	長さ (mm)	本数 (本)	単位重量 (kg/m)	1本当り質量 (kg)	質 量 (kg)	備考
H1	D13	1840	34	0.995	1.831	62	EP塗装
H2	D13	490	32	0.995	0.488	16	EP塗装
H3	D13	1010	20	0.995	1.005	20	EP塗装
H4	D13	620	2	0.995	0.617	1	EP塗装
H5	D13	550	10	0.995	0.547	5	EP塗装
H6	D13	350	9	0.995	0.348	3	EP塗装
H7	D13	4690	9	0.995	4.667	42	
H8	D13	2000	6	0.995	1.990	12	
H9	D13	1510	6	0.995	1.502	9	EP塗装
H10	D13	700	18	0.995	0.697	13	EP塗装
H11	D16	680	4	1.56	1.061	4	EP塗装
H12	D13	1600	2	0.995	1.592	3	
H13	D13	1270	2	0.995	1.264	3	
合 計						193	kg
鉄筋質量集計 (SD345)							
				普通鉄筋	塗装鉄筋		
				D16	0 kg	4 kg	4 kg
				D13	60 kg	129 kg	189 kg
合計				60 kg	133 kg	193 kg	

埋設管配置側面図

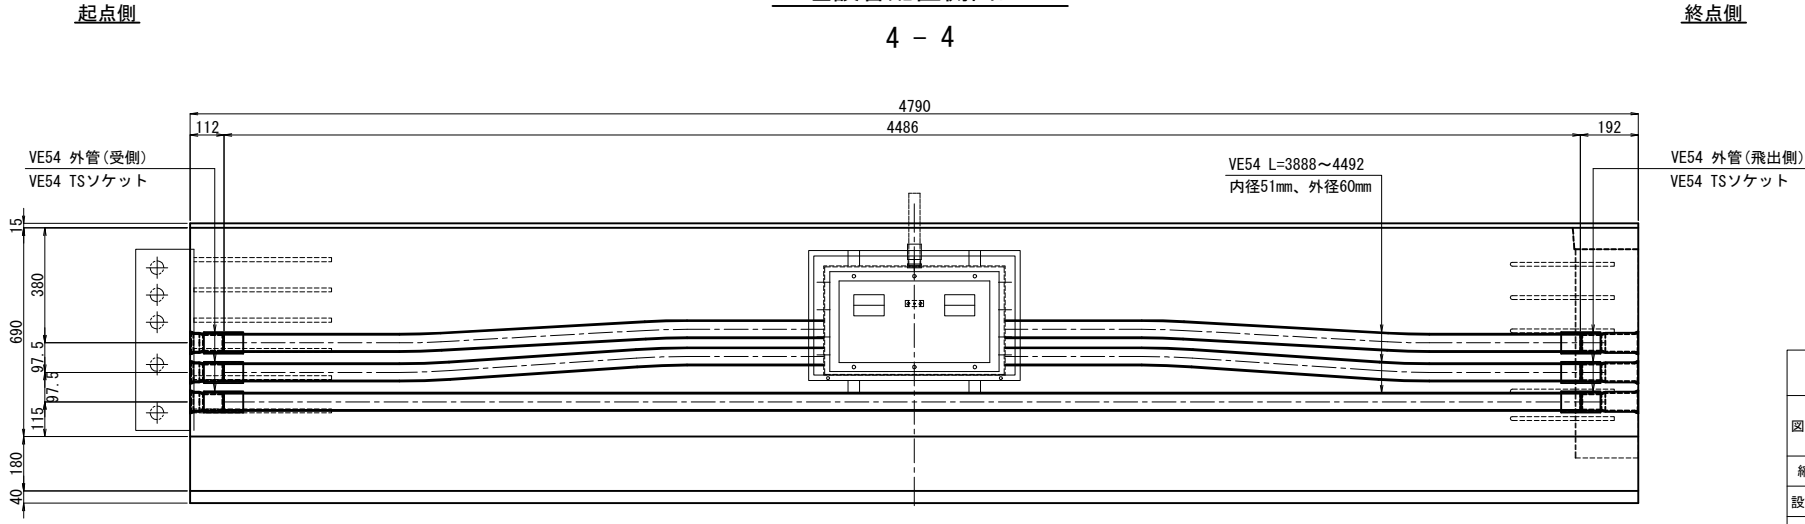

道央自動車道 千歳川大橋(下り線) 床版取替工事			
図面の種類	千歳川大橋(下り線) P18-P24 プレキャスト壁高欄詳細図(40)		
縮 尺	図 示	図面番号	/
設計会社名	戸田建設株式会社		
施工会社名	戸田建設株式会社		
事務所名	東日本高速道路株式会社 北海道支社 札幌管理事務所		

千歳川大橋(下り線) P18-P24 プレキャスト壁高欄詳細図(41)


S=1:25

[中分側 R-48-0F-SP]

(P22-P23径間 製作数 : 1)


断面図

1 - 1

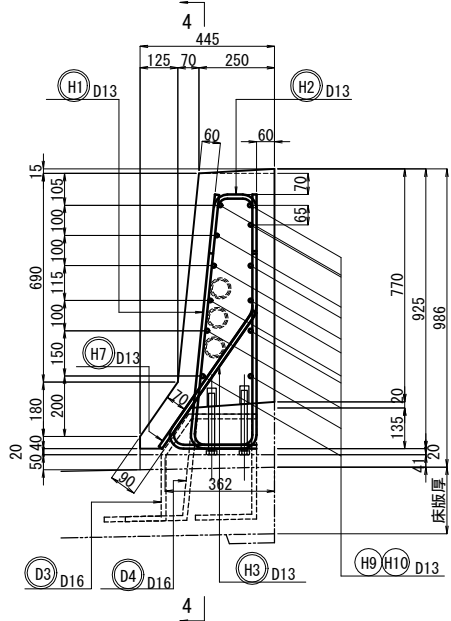


断面図

2 - 2

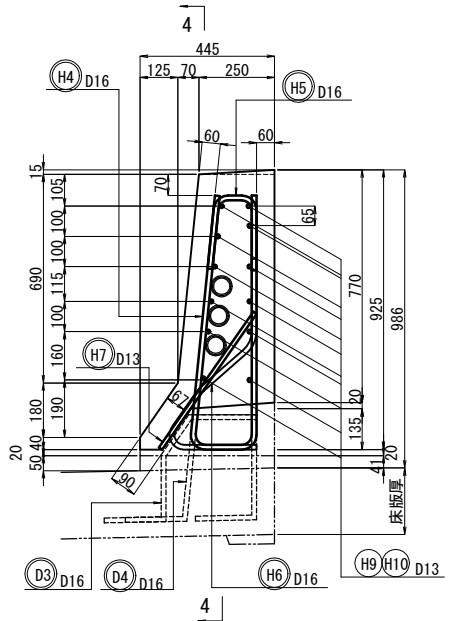


断面図

3 - 3

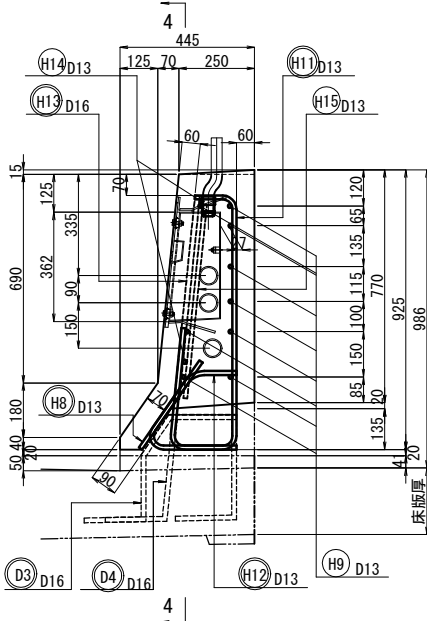


側面図

4 - 4





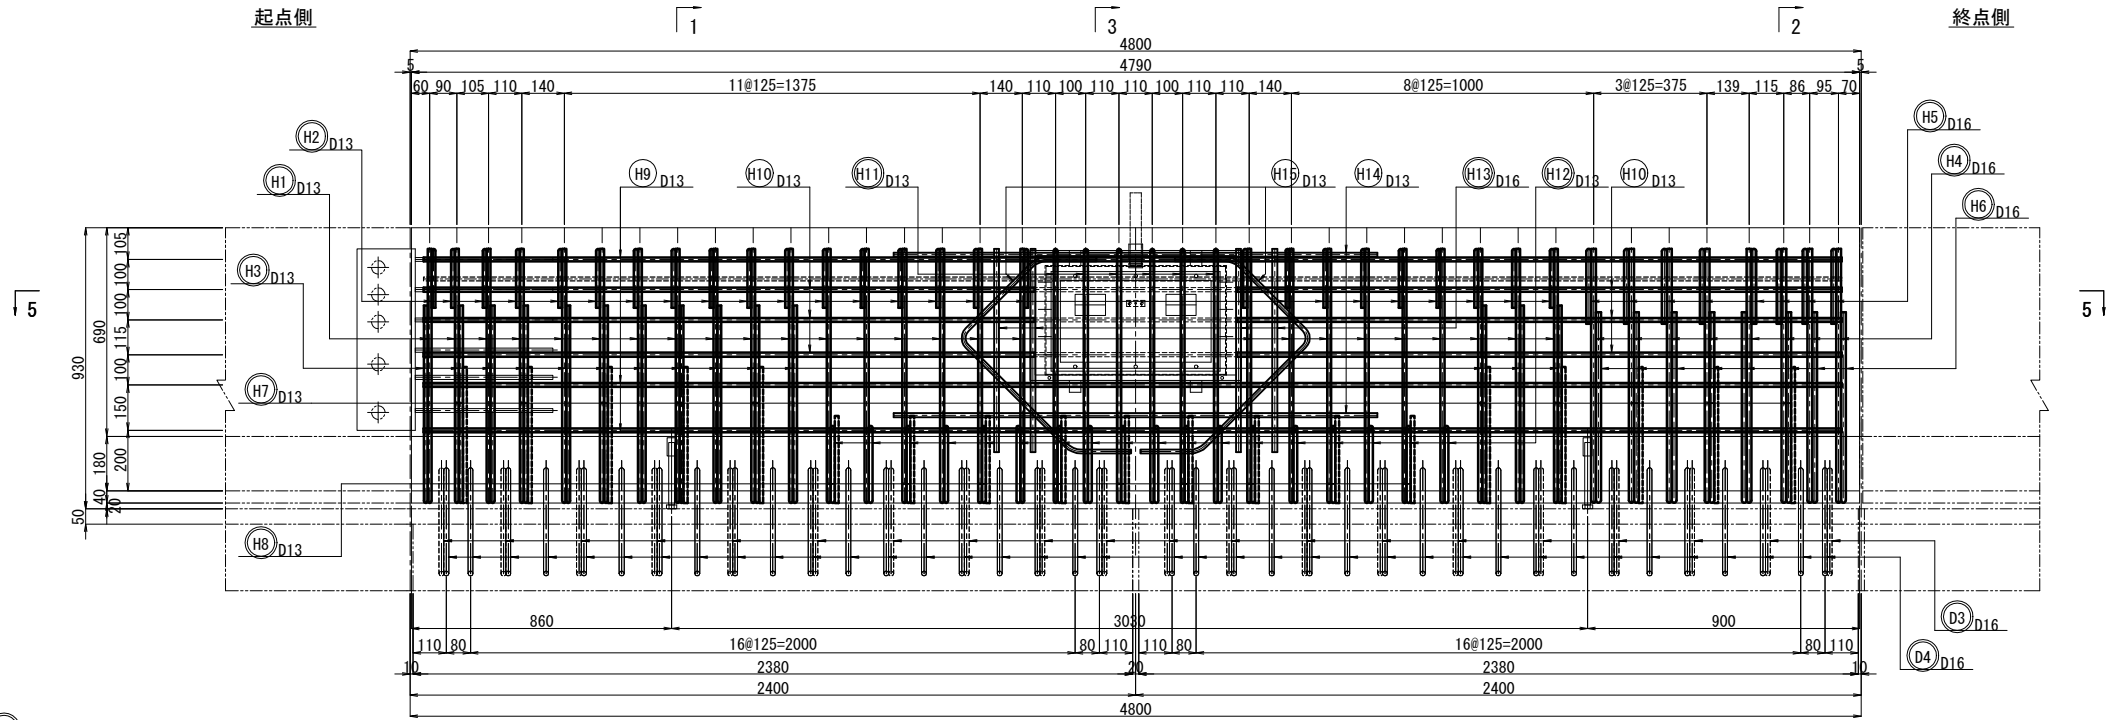


平面図

5 - 5

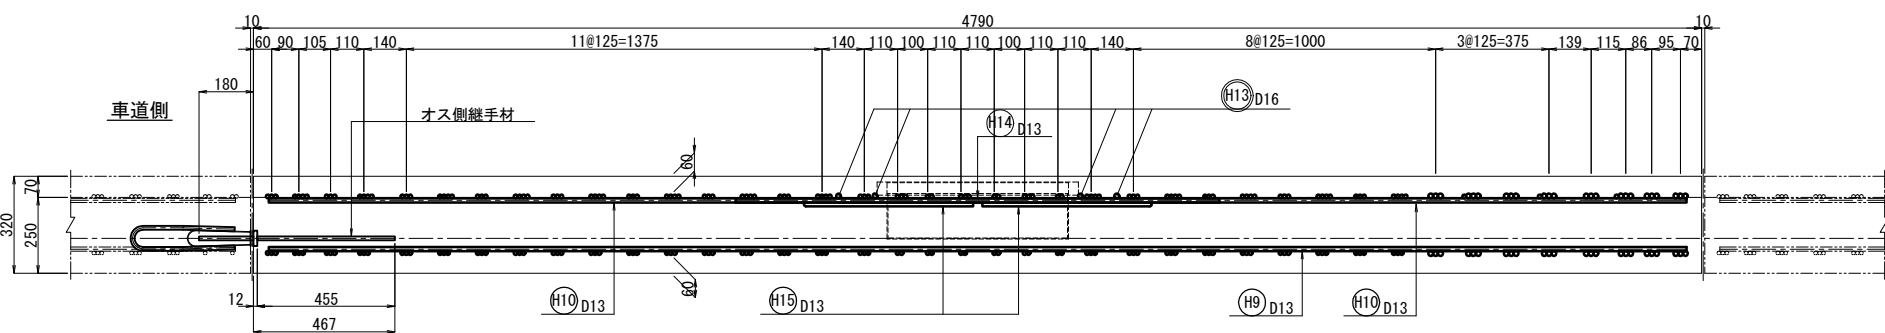

※ 鉄筋記号の○は塗装鉄筋を示す。
※ インサートおよび埋設管などの詳細位置は、壁高欄詳細図(42)を参照のこと。

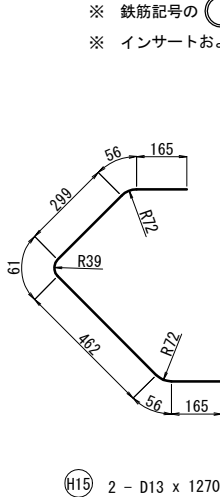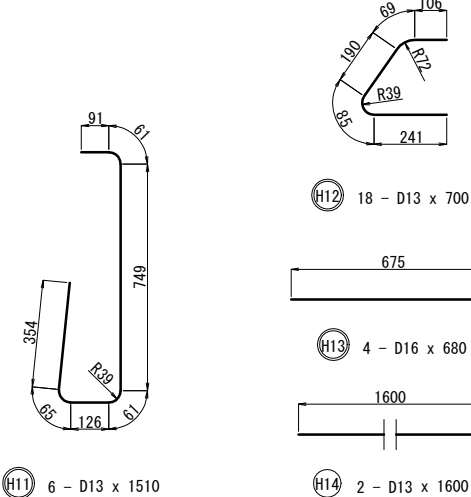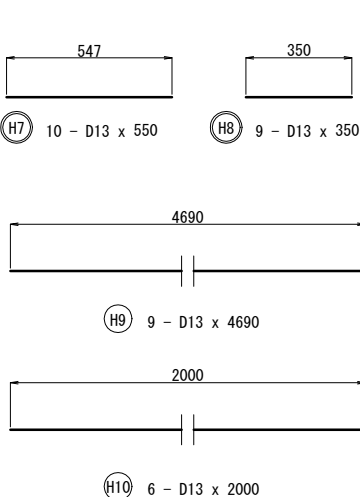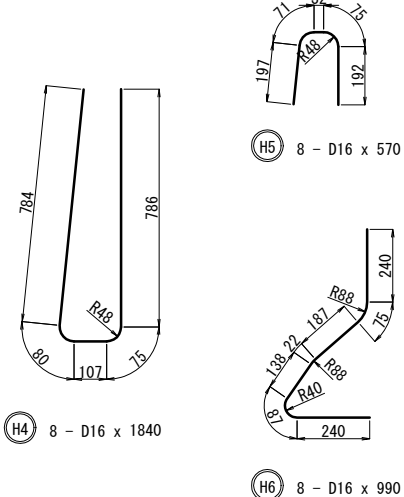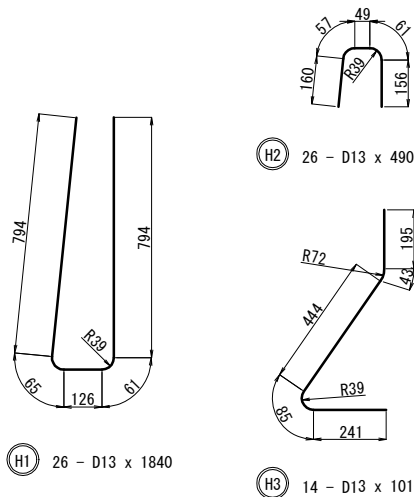

道央自動車道 千歳川大橋(下り線) 床版取替工事			
図面の種類	千歳川大橋(下り線) P18-P24 プレキャスト壁高欄詳細図(41)		
縮尺	図示	図面番号	/
設計会社名	戸田建設株式会社		
施工会社名	戸田建設株式会社		
事務所名	東日本高速道路株式会社 北海道支社 札幌管理事務所		

千歳川大橋(下り線) P18-P24 プレキャスト壁高欄詳細図(42)

S=1:25



[中分側 R-48-0F-SP]

(P22-P23径間 製作数 : 1)

※スノーボール用アンカーの埋込深さについては共通詳細図(9)を参照のこと。

断面図


1 - 1

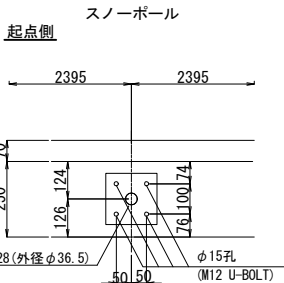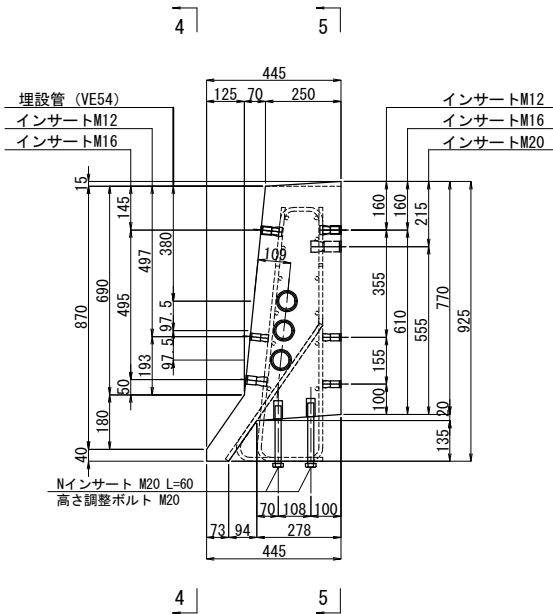

起点側


インサート配置側面図

4 - 4

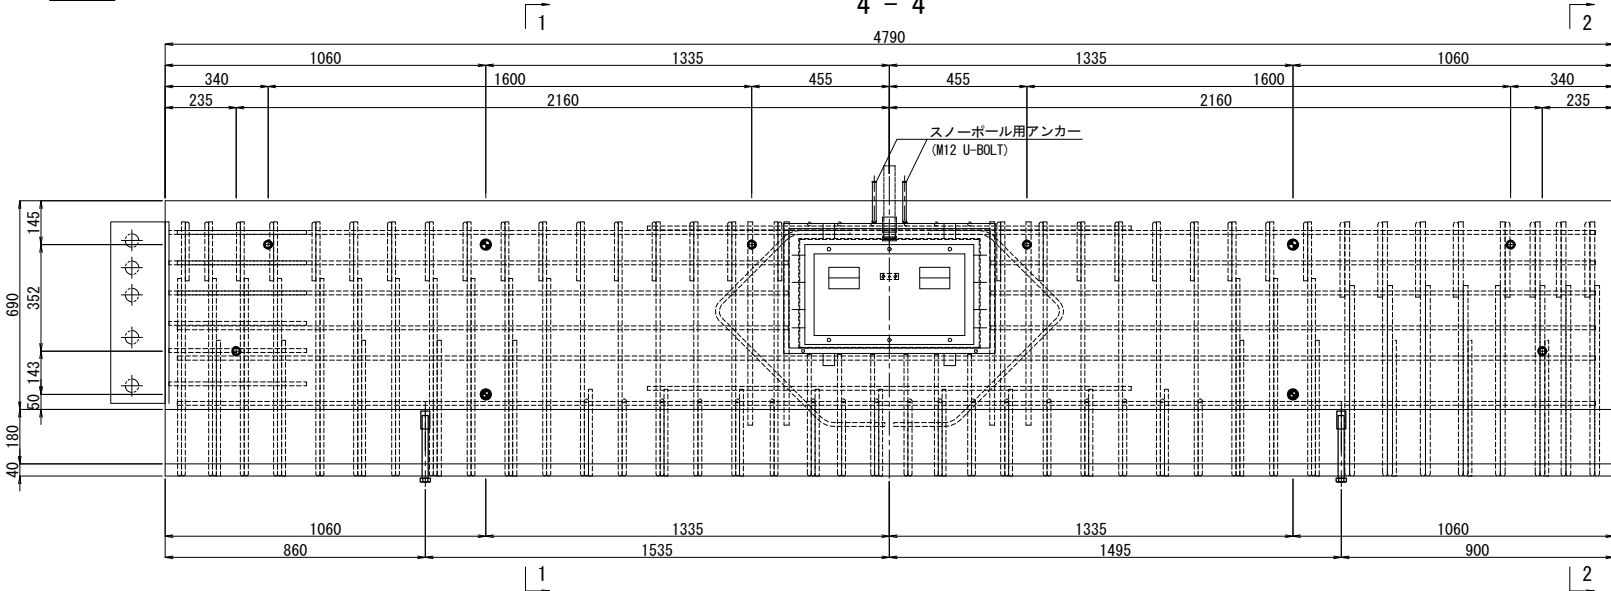


終点側


2 - 2

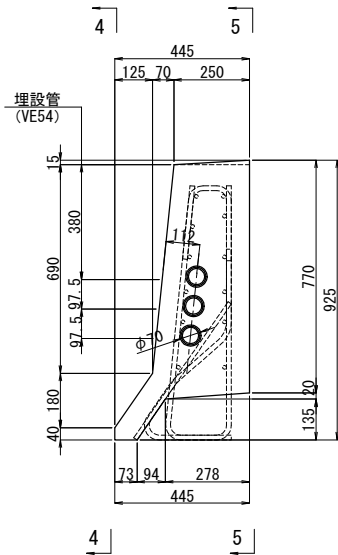

3 - 3

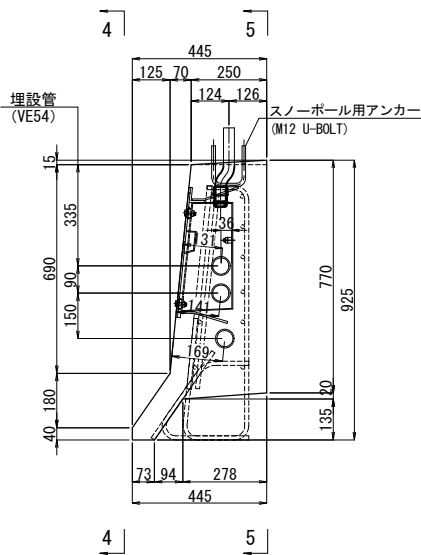

5 - 5

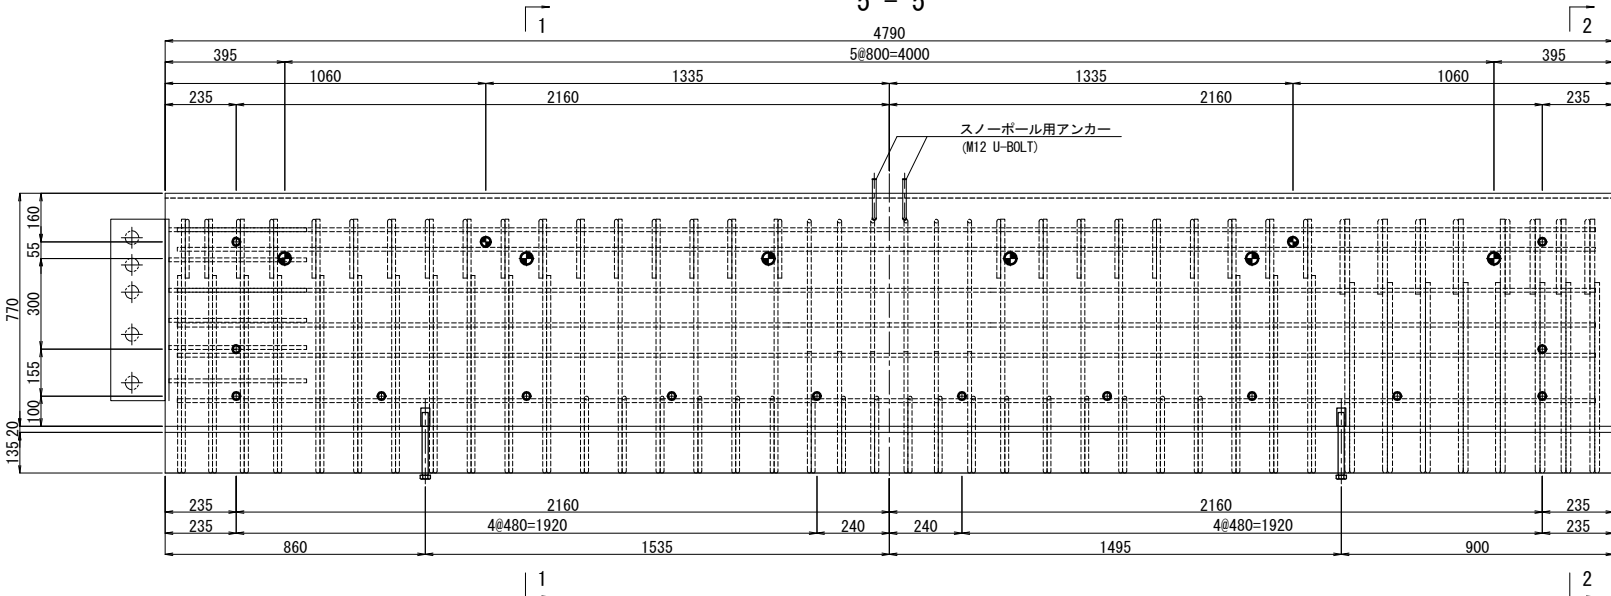


終点側

鉄筋表(1ブロック当り)

鉄筋番号	材質	長さ (mm)	本数 (本)	単位重量 (kg/m)	1本当り質量 (kg)	質量 (kg)	備考
H1	D13	1840	26	0.995	1.831	48	EP塗装
H2	D13	490	26	0.995	0.488	13	EP塗装
H3	D13	1010	14	0.995	1.005	14	EP塗装
H4	D16	1840	8	1.56	2.870	23	EP塗装
H5	D16	570	8	1.56	0.889	7	EP塗装
H6	D16	990	8	1.56	1.544	12	EP塗装
H7	D13	550	10	0.995	0.547	5	EP塗装
H8	D13	350	9	0.995	0.348	3	EP塗装
H9	D13	4690	9	0.995	4.667	42	
H10	D13	2000	6	0.995	1.990	12	
H11	D13	1510	6	0.995	1.502	9	EP塗装
H12	D13	700	18	0.995	0.697	13	EP塗装
H13	D16	680	4	1.56	1.061	4	EP塗装
H14	D13	1600	2	0.995	1.592	3	
H15	D13	1270	2	0.995	1.264	3	
合 計						211	kg
鉄筋質量集計 (SD345)							
		普通鉄筋		塗装鉄筋			
		D16		0 kg		46 kg	
		D13		60 kg		165 kg	
		合計		60 kg		211 kg	

埋設管配置側面図

4 - 4

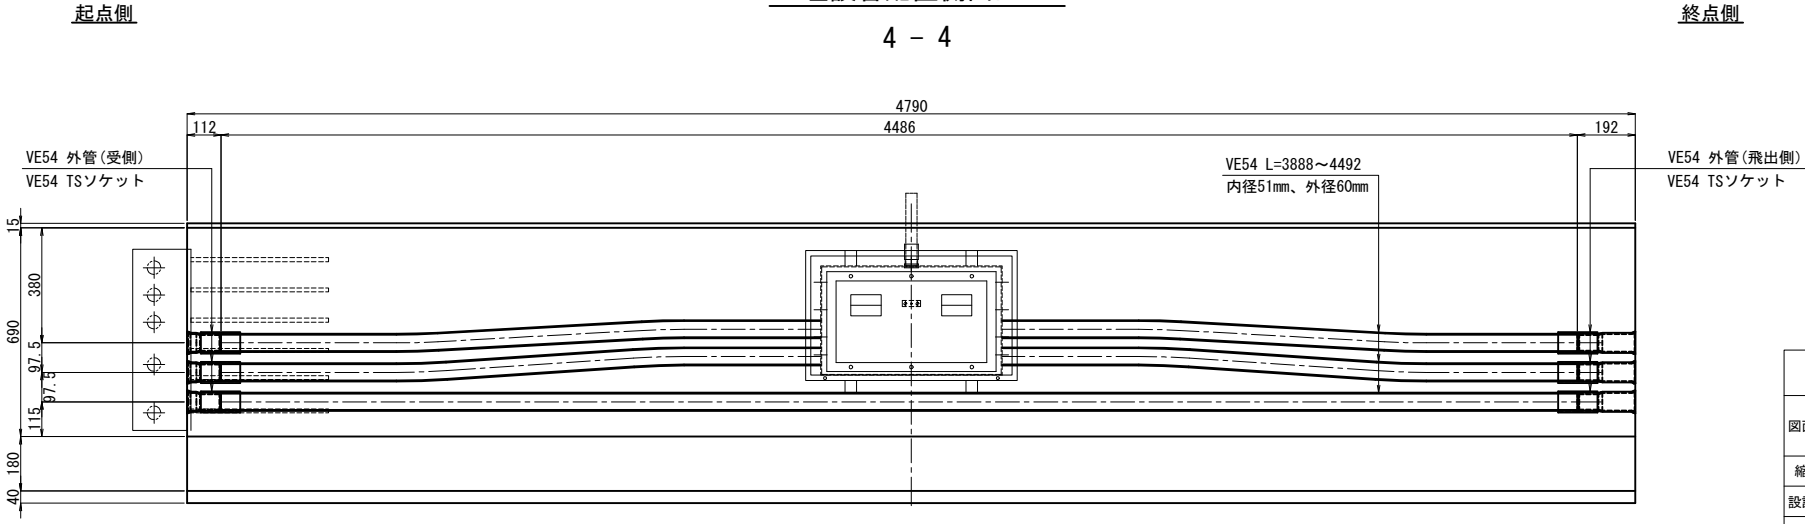

道央自動車道 千歳川大橋(下り線)床版取替工事			
図面の種類	千歳川大橋(下り線) P18-P24 プレキャスト壁高欄詳細図(42)		
縮 尺	図 示	図面番号	/
設計会社名	戸田建設株式会社		
施工会社名	戸田建設株式会社		
事務所名	東日本高速道路株式会社 北海道支社 札幌管理事務所		

千歳川大橋(下り線) P18-P24 プレキャスト壁高欄詳細図(43)


S=1:25

[中分側 R-E2-JM-PB]

(P18-P19径間 製作数 : 1)


断面図

1 - 1

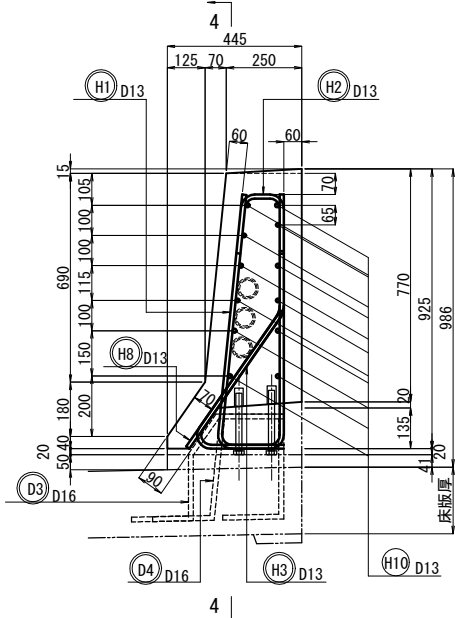


断面図

2 - 2

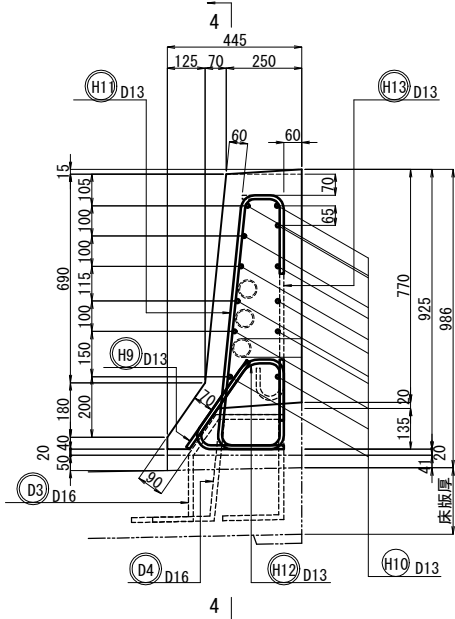


断面図

3 - 3

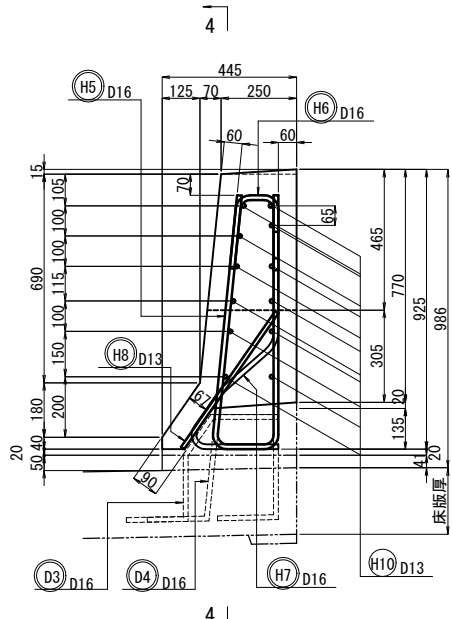


側面図

4 - 4











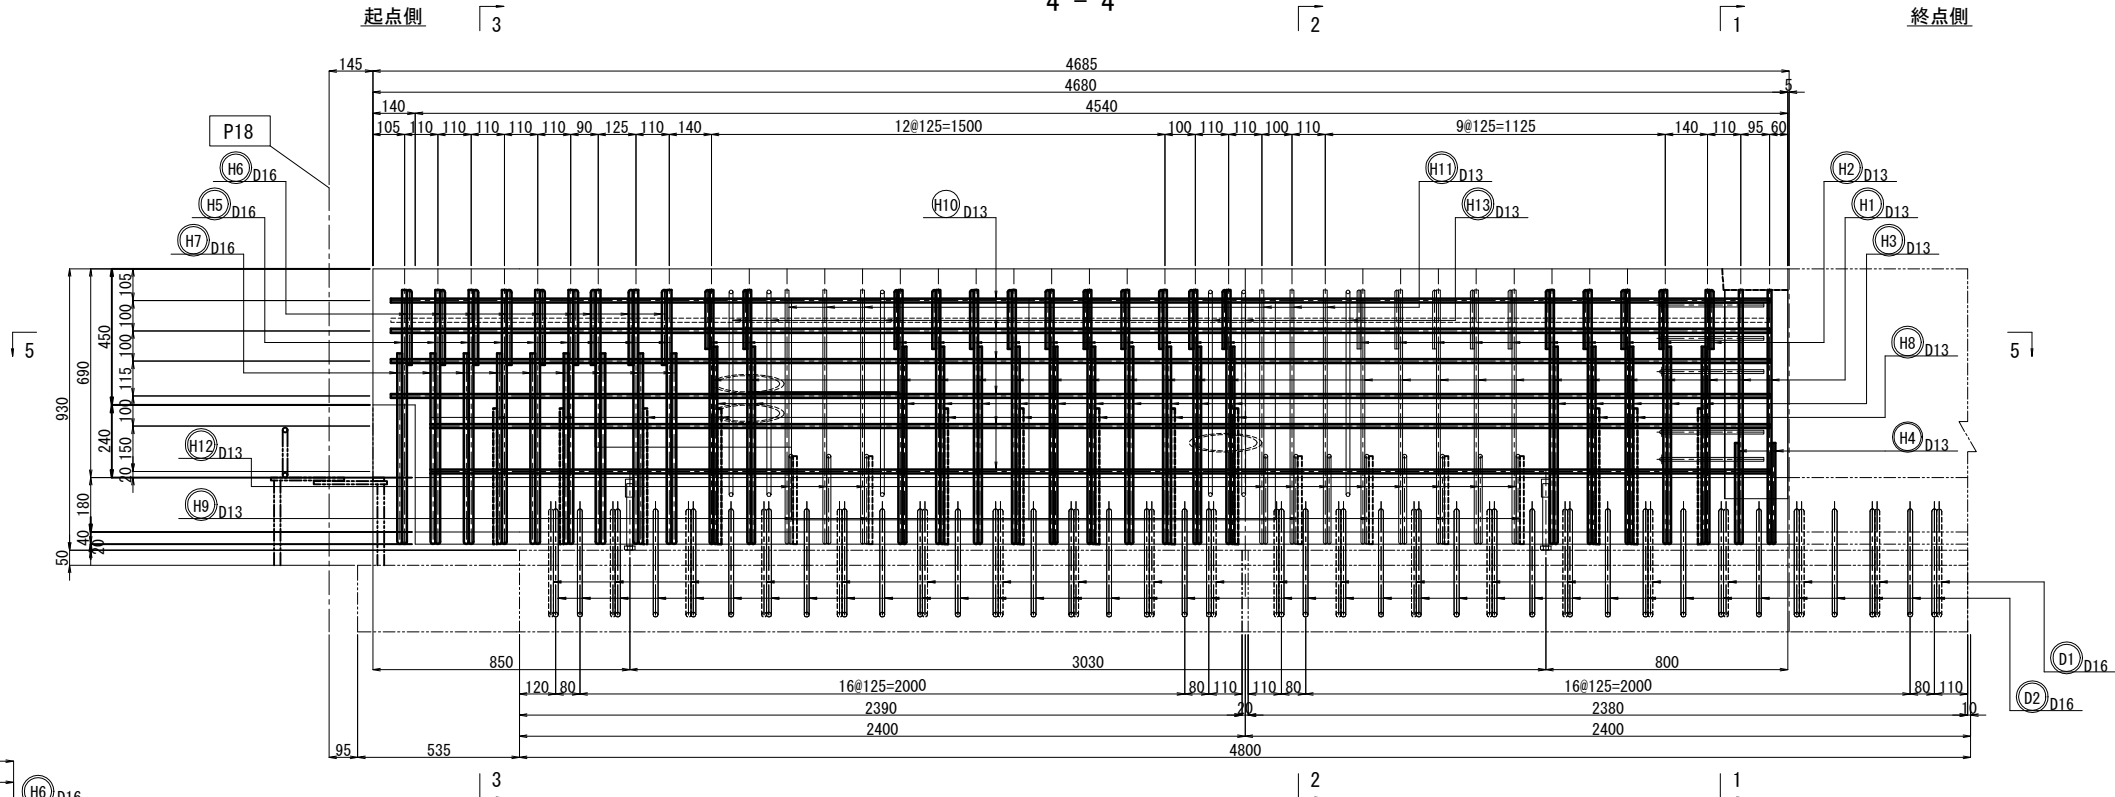


平面図

5 - 5

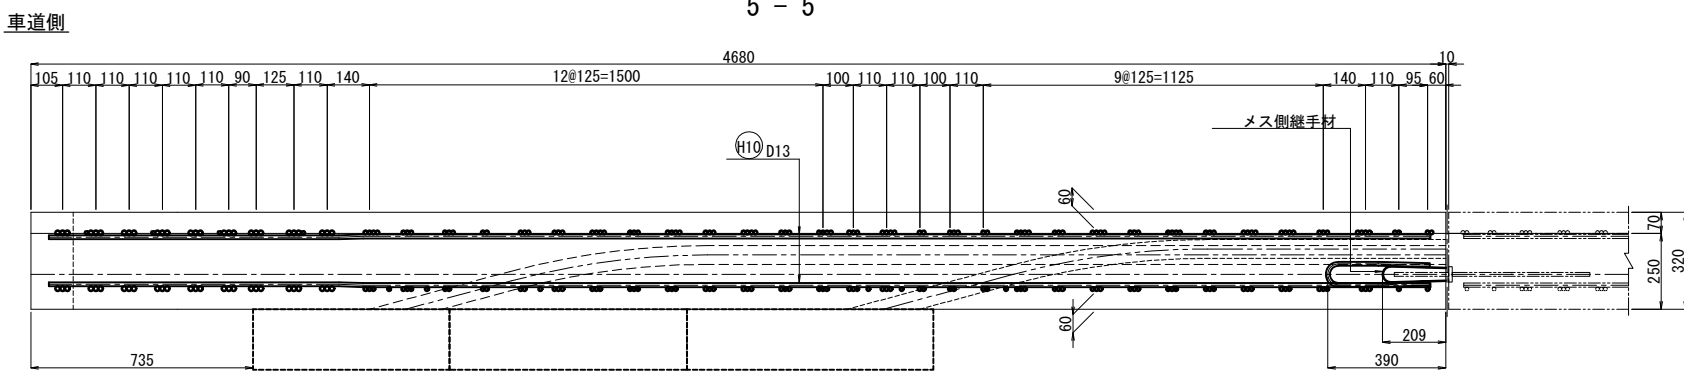

※ 鉄筋記号の  は塗装鉄筋を示す。
※ インサートおよび埋設管などの詳細位置は、壁高欄詳細図(44)を参照のこと。

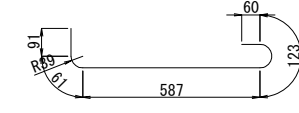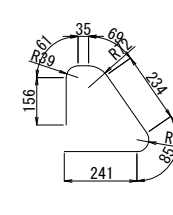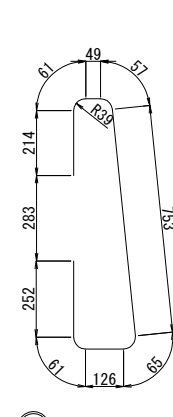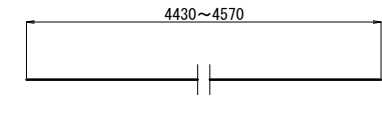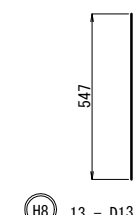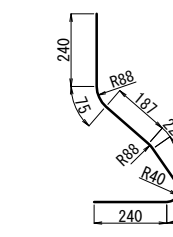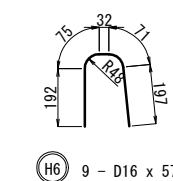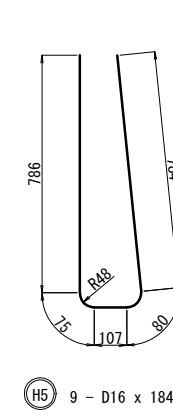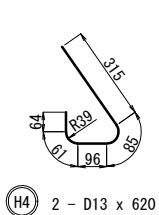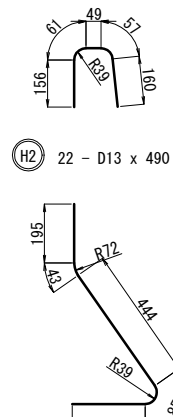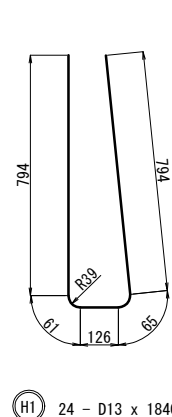

道央自動車道 千歳川大橋(下り線)床版取替工事			
図面の種類	千歳川大橋(下り線) P18-P24 プレキャスト壁高欄詳細図(43)		
縮 尺	図 示	図面番号	/
設計会社名	戸田建設株式会社		
施工会社名	戸田建設株式会社		
事務所名	東日本高速道路株式会社 北海道支社 札幌管理事務所		

千歳川大橋(下り線) P18-P24 プレキャスト壁高欄詳細図(44)


S=1:25

[中分側 R-E2-JM-PB]


(P18-P19径間 製作数 : 1)

断面図


1 - 1

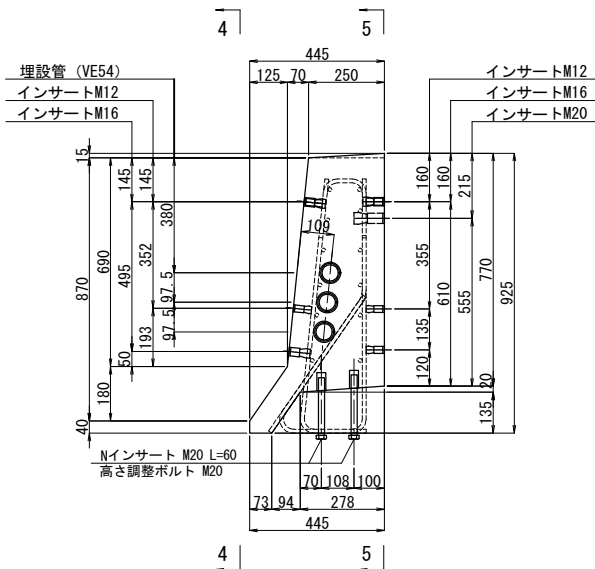


2 - 2

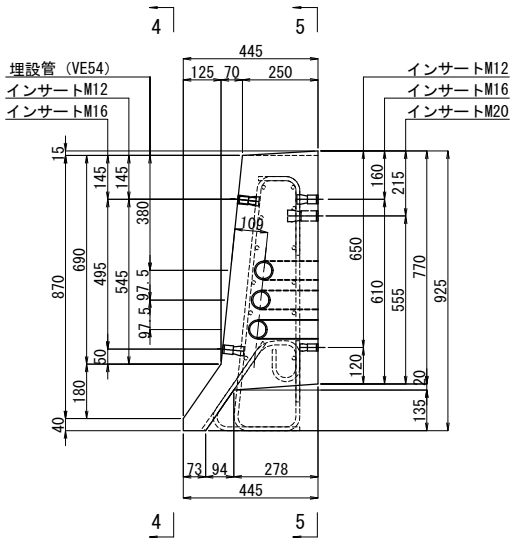

3 - 3

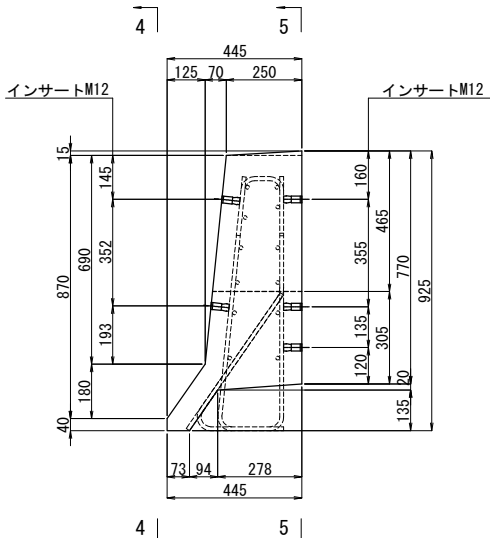


インサート配置側面図

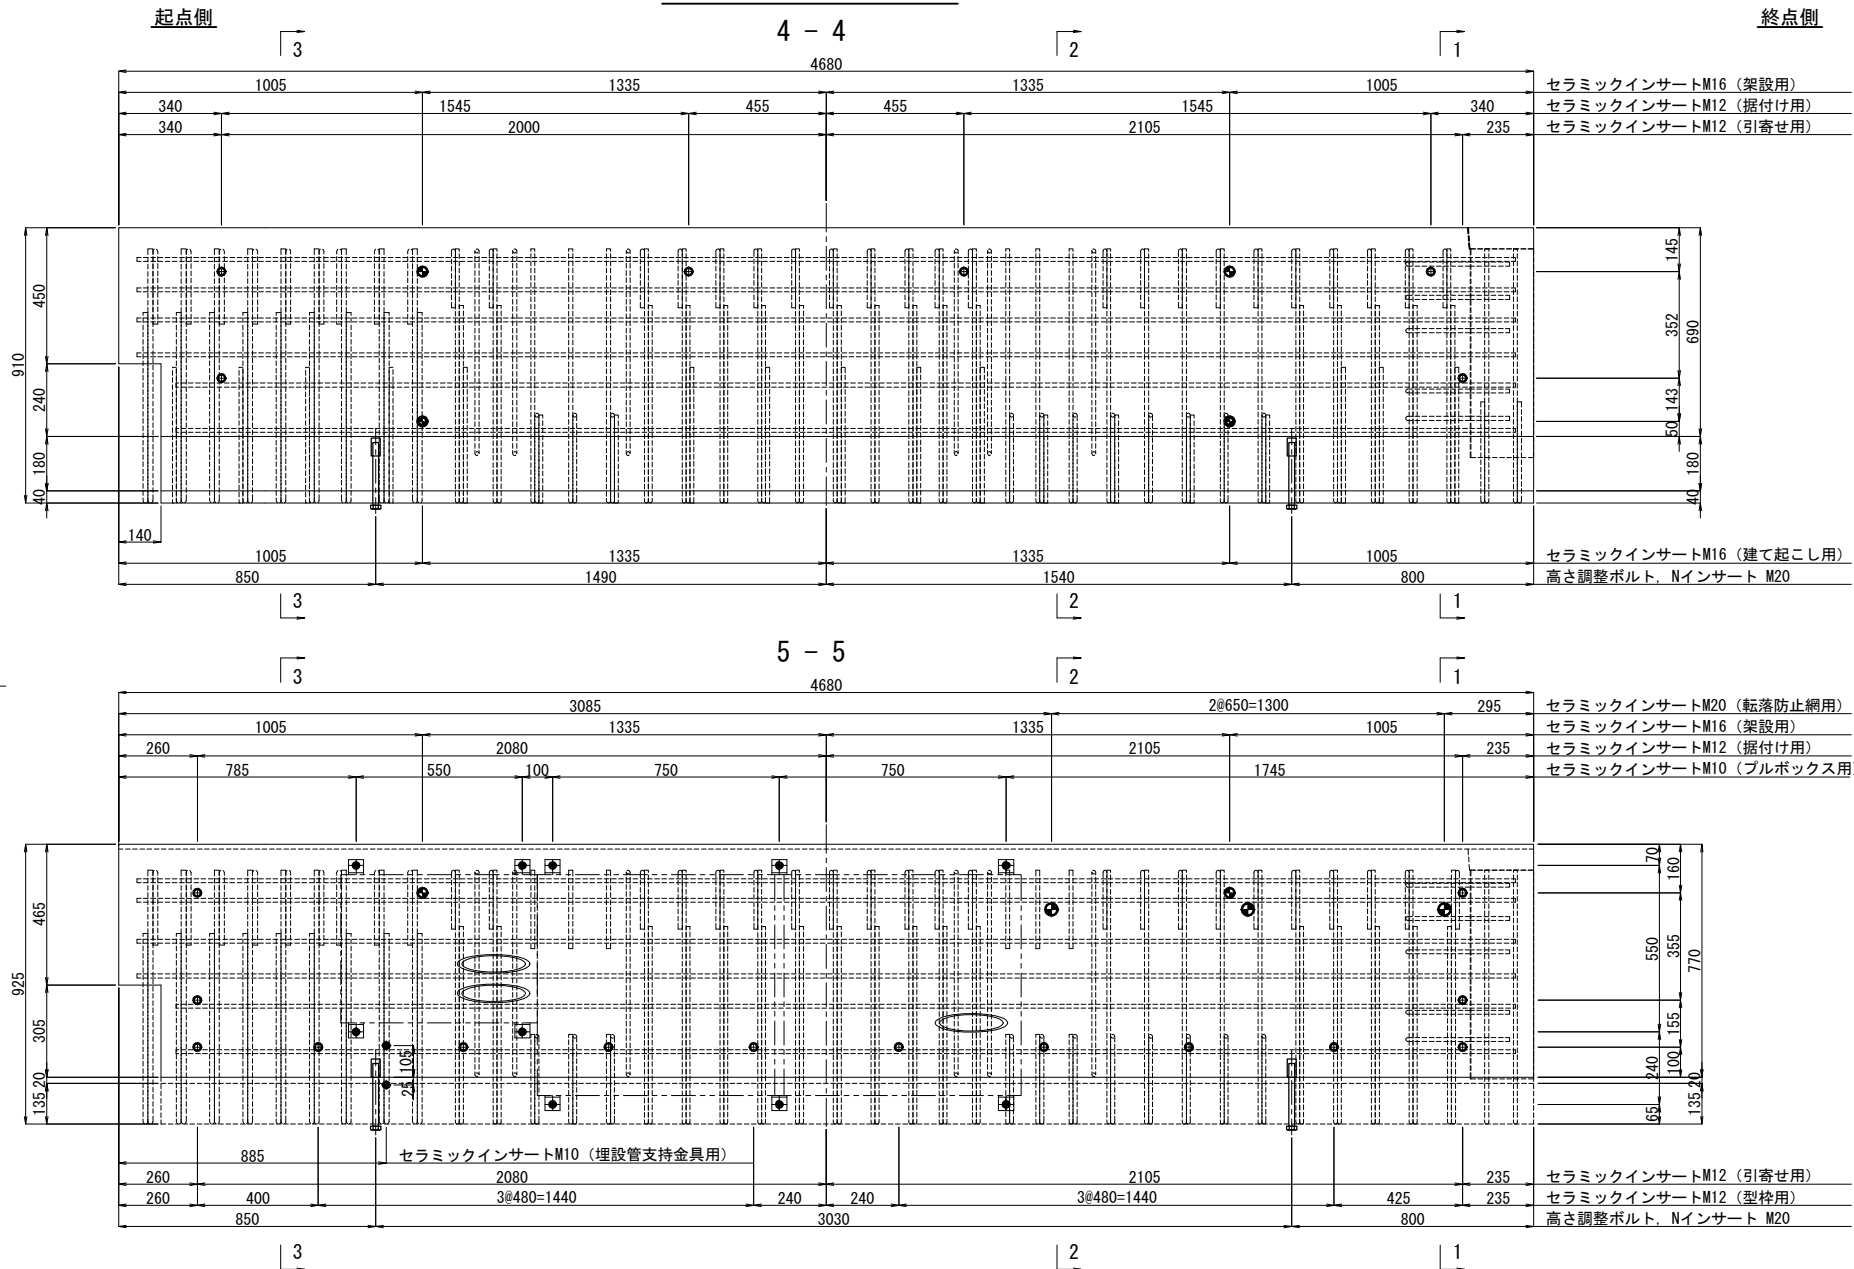

鉄筋表(1ブロック当り)

鉄筋番号	材質	長さ (mm)	本数 (本)	単位重量 (kg/m)	1本当り質量 (kg)	質量 (kg)	備考
H1	D13	1840	24	0.995	1.831	44	EP塗装
H2	D13	490	22	0.995	0.488	11	EP塗装
H3	D13	1010	17	0.995	1.005	17	EP塗装
H4	D13	620	2	0.995	0.617	1	EP塗装
H5	D16	1840	9	1.56	2.870	26	EP塗装
H6	D16	570	9	1.56	0.889	8	EP塗装
H7	D16	990	9	1.56	1.544	14	EP塗装
H8	D13	550	13	0.995	0.547	7	EP塗装
H9	D13	350	6	0.995	0.348	2	EP塗装
H10	D13	4500	12	0.995	4.478	54	
H11	D13	1640	6	0.995	1.632	10	EP塗装
H12	D13	890	11	0.995	0.886	10	EP塗装
H13	D13	930	6	0.995	0.925	6	EP塗装
合 計						210	kg
鉄筋質量集計 (SD345)							
				普通鉄筋	塗装鉄筋		
				D16	0 kg	48 kg	
				D13	54 kg	108 kg	
				合計	54 kg	156 kg	
						210 kg	

埋設管配置側面図

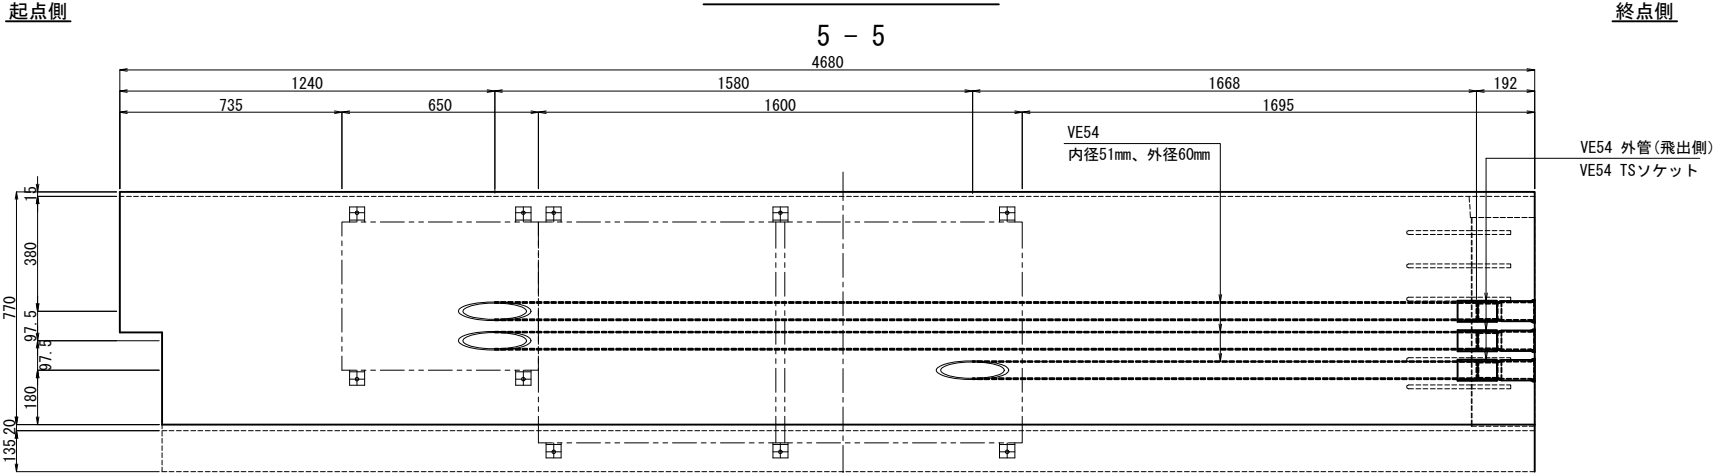

道央自動車道 千歳川大橋(下り線) 床版取替工事			
図面の種類	千歳川大橋(下り線) P18-P24 プレキャスト壁高欄詳細図(44)		
縮 尺	図 示	図面番号	/
設計会社名	戸田建設株式会社		
施工会社名	戸田建設株式会社		
事務所名	東日本高速道路株式会社 北海道支社 札幌管理事務所		

千歳川大橋(下り線) P18-P24 プレキャスト壁高欄詳細図(45)


S=1:25

[中分側 R-E3-0J-PB]

(P23-P24径間 製作数 : 1)


断面図

1 - 1

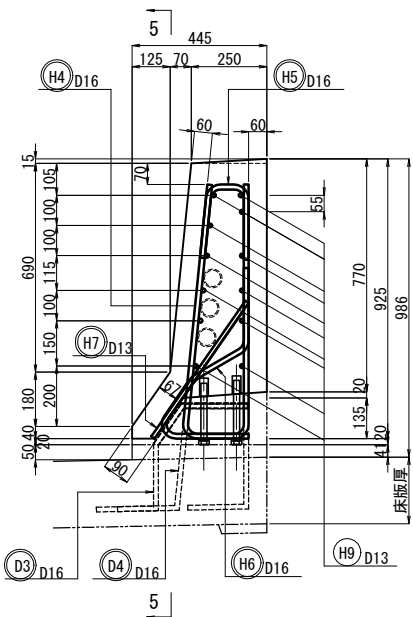


断面図

2 - 2 (3 - 3)

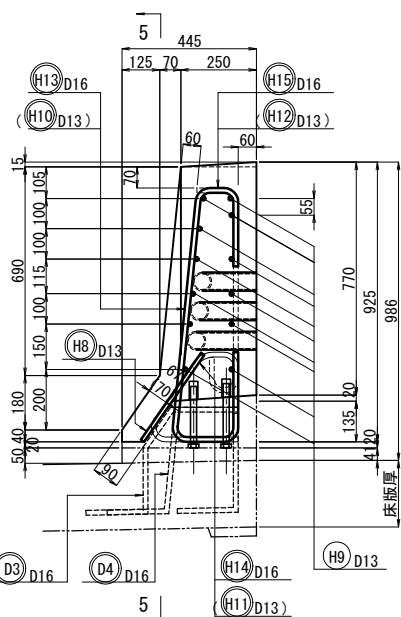



側面図

5 - 5

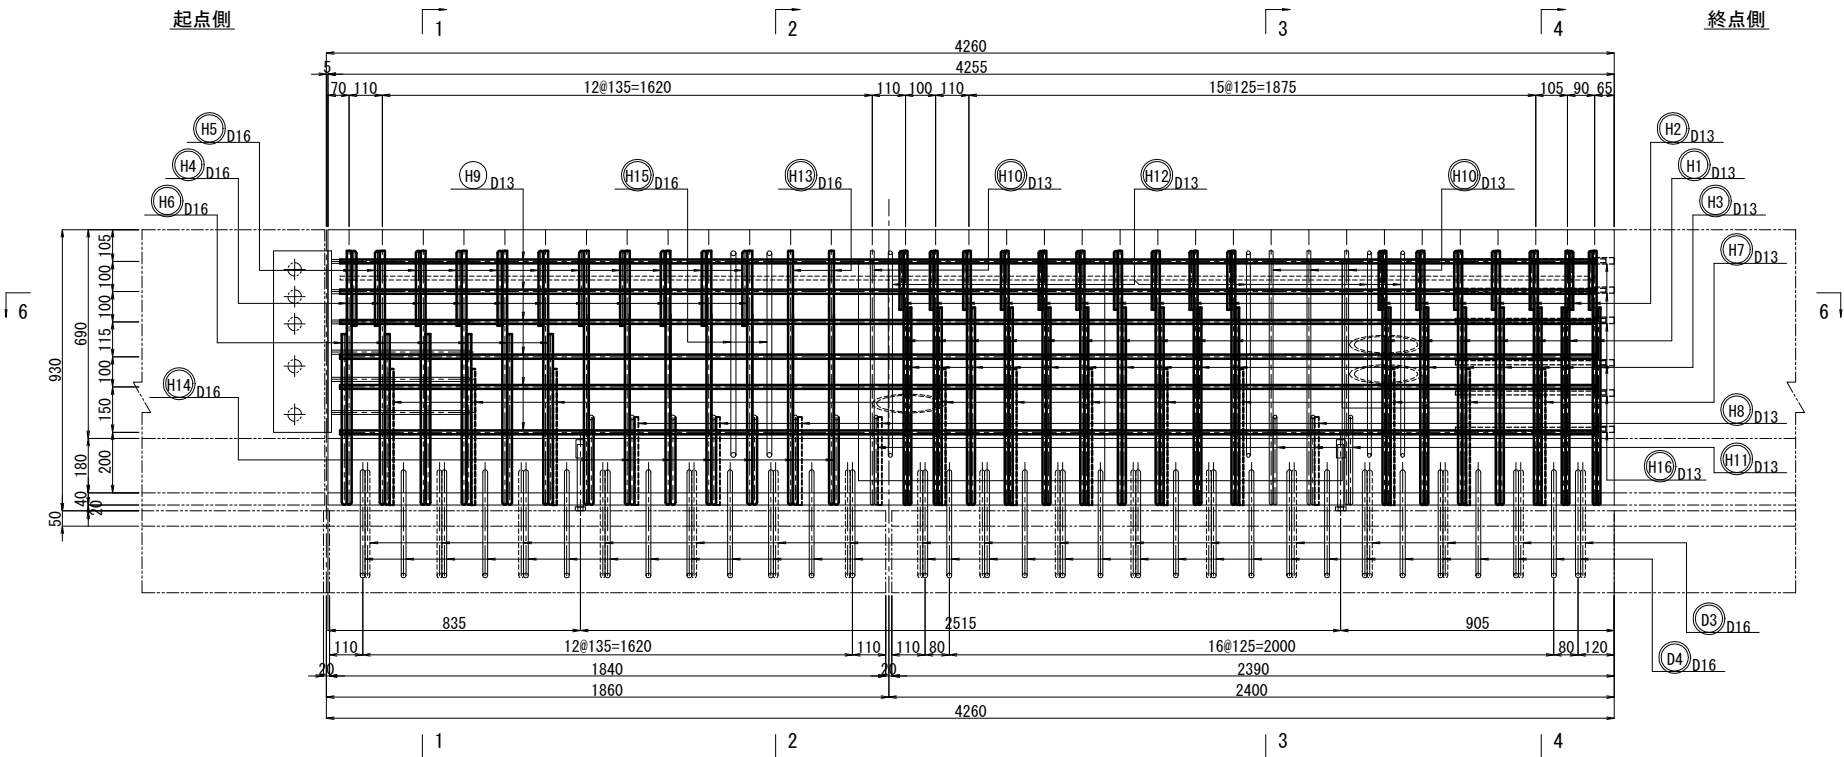


断面図


4 - 4

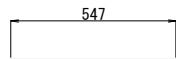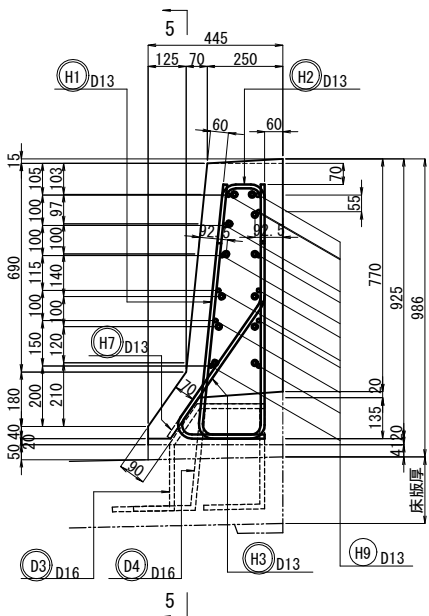

H7 11 - D13 x 550

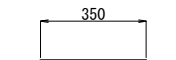


H8 5 - D13 x 350

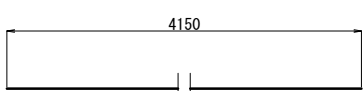

H9 12 - D13 x 4150


平面図

6 - 6

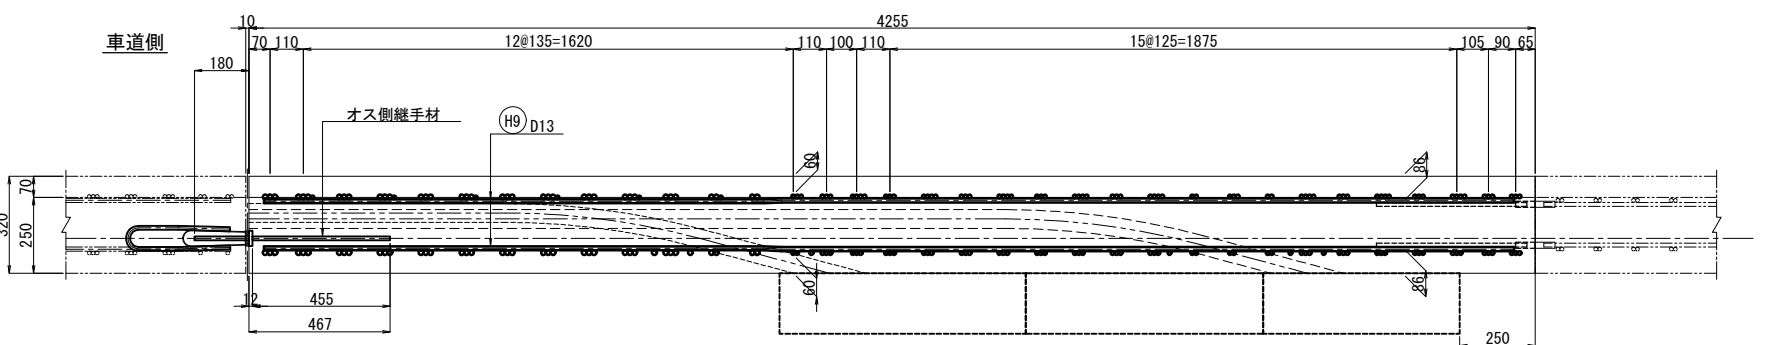


※ 鉄筋記号の $\bigcirc$ は塗装鉄筋を示す。


※ インサートおよび埋設管などの詳細位置は、壁高欄詳細図(46)を参照のこと。

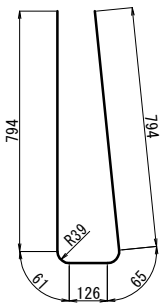


H1 17 - D13 x 1840

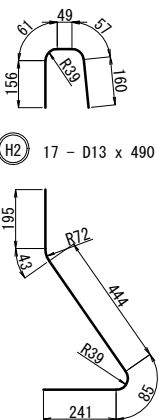


H2 17 - D13 x 490

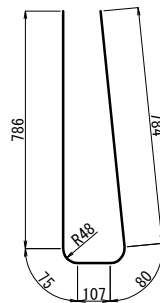


H4 11 - D16 x 1840

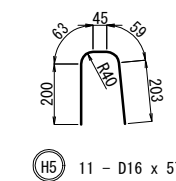


H5 11 - D16 x 570

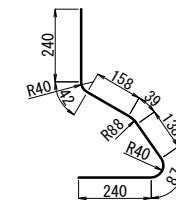


H6 6 - D16 x 950

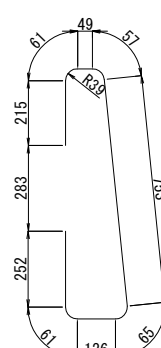


H10 4 - D13 x 1640

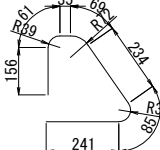


H11 4 - D13 x 890

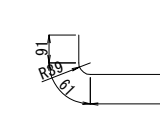


H12 4 - D13 x 930

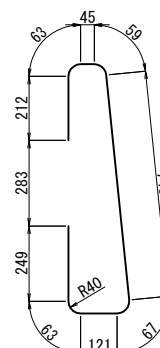


H13 2 - D16 x 1630

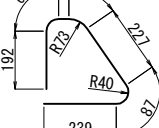

H14 7 - D16 x 920

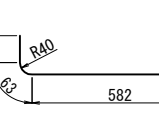

H15 2 - D16 x 930

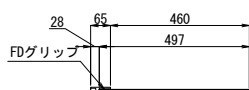

H16 12 - D13 x 500

道央自動車道 千歳川大橋(下り線) 床版取替工事			
図面の種類	千歳川大橋(下り線) P18-P24 プレキャスト壁高欄詳細図(45)		
縮 尺	図 示	図面番号	/
設計会社名	戸田建設株式会社		
施工会社名	戸田建設株式会社		
事務所名	東日本高速道路株式会社 北海道支社 札幌管理事務所		