

千歳川大橋(下り線) P18-P24 プレキャスト壁高欄詳細図(46)


S=1:25

[中分側 R-E3-0J-PB]


(P23-P24径間 製作数 : 1)

断面図


1 - 1

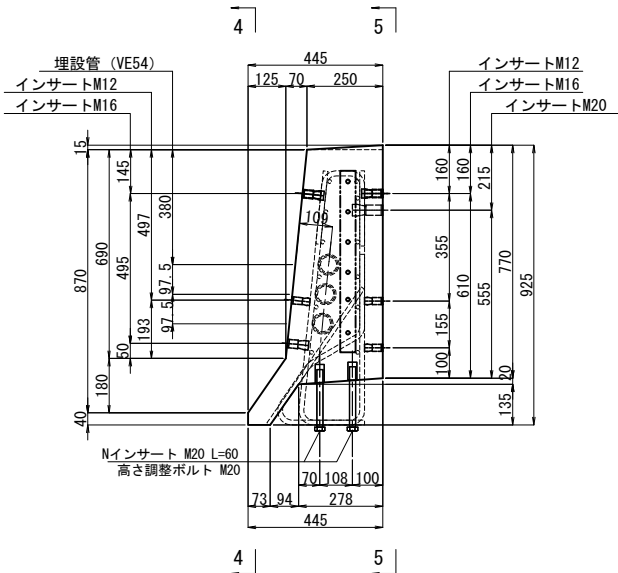

2 - 2

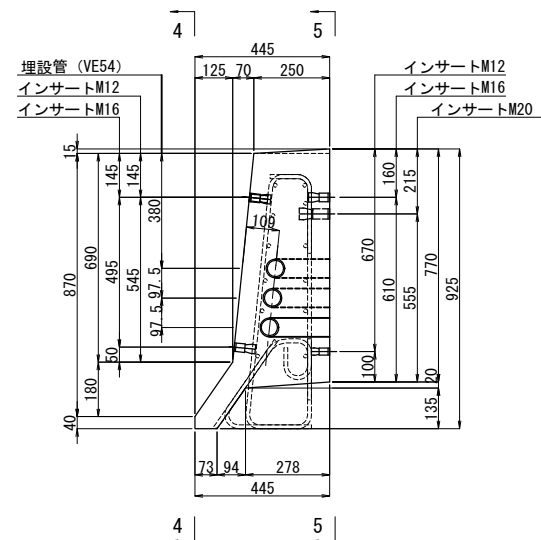


3 - 3

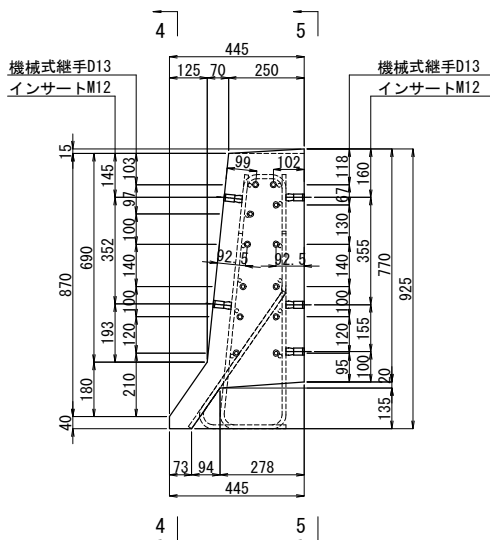


インサート配置側面図

4 - 4

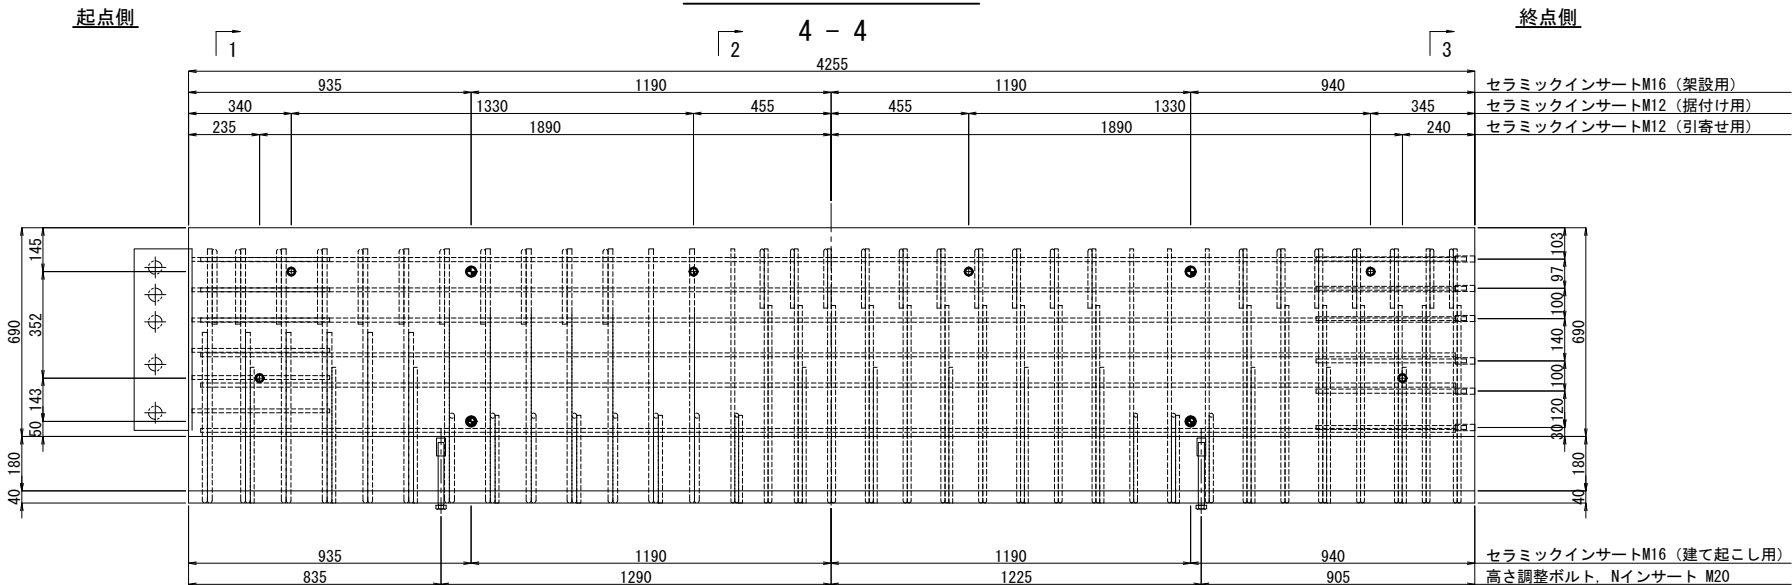

5 - 5

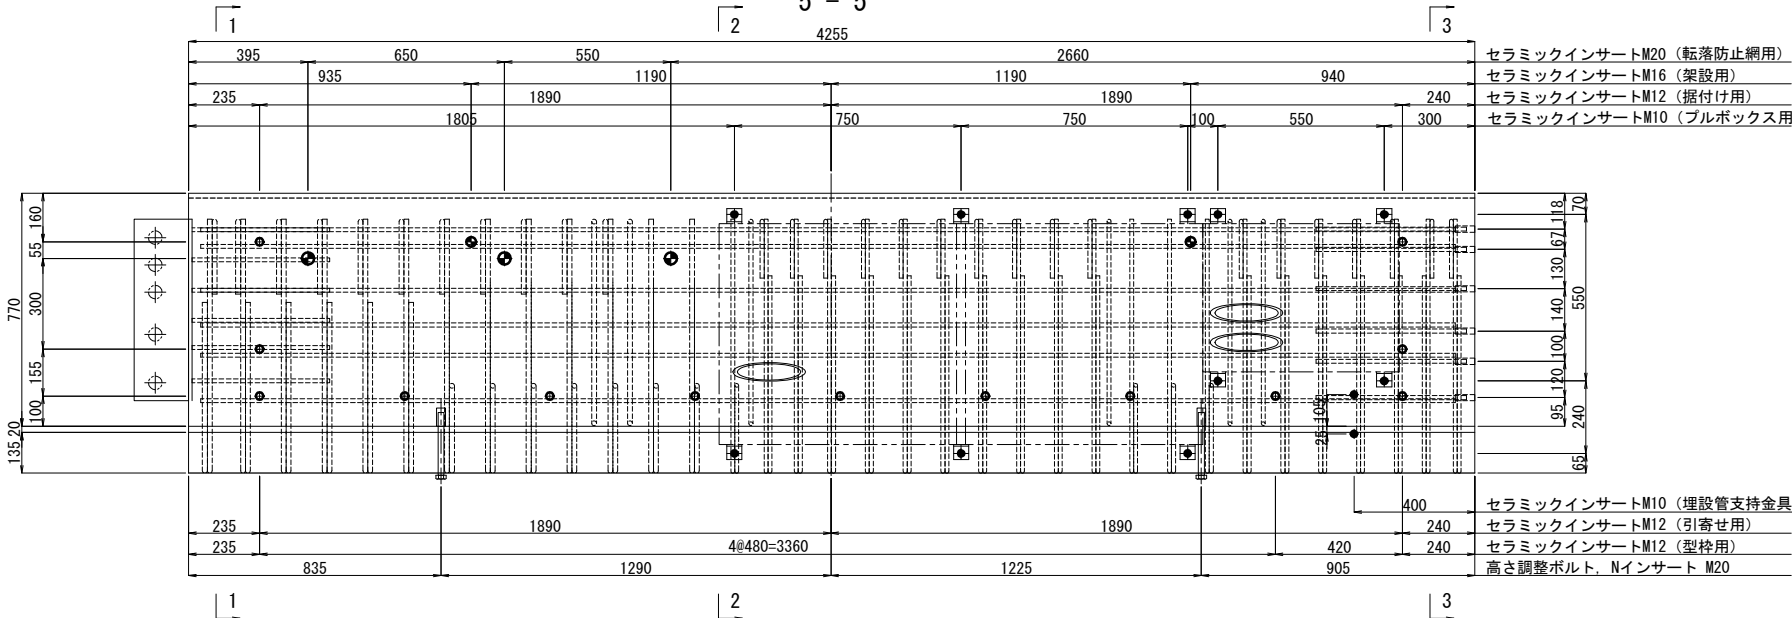


鉄筋表(1ブロック当り)

鉄筋番号	材質	長さ (mm)	本数 (本)	単位重量 (kg/m)	1本当り質量 (kg)	質量 (kg)	備考
H1	D13	1840	17	0.995	1.831	31	EP塗装
H2	D13	490	17	0.995	0.488	8	EP塗装
H3	D13	1010	17	0.995	1.005	17	EP塗装
H4	D16	1840	11	1.56	2.870	32	EP塗装
H5	D16	570	11	1.56	0.889	10	EP塗装
H6	D16	950	6	1.56	1.482	9	EP塗装
H7	D13	550	11	0.995	0.547	6	EP塗装
H8	D13	350	5	0.995	0.348	2	EP塗装
H9	D13	4150	12	0.995	4.129	50	
H10	D13	1640	4	0.995	1.632	7	EP塗装
H11	D13	890	4	0.995	0.886	4	EP塗装
H12	D13	930	4	0.995	0.925	4	EP塗装
H13	D16	1630	2	1.56	2.543	5	EP塗装
H14	D16	920	7	1.56	1.435	10	EP塗装
H15	D16	930	2	1.56	1.451	3	EP塗装
H16	D13	500	12	0.995	0.498	6	EP塗装
合 計						204	kg
鉄筋質量集計(SD345)							
				普通鉄筋	塗装鉄筋		
				D16	0 kg	69 kg	69 kg
				D13	50 kg	85 kg	135 kg
				合計	50 kg	154 kg	204 kg
				機械式継手 D13		12 組	

埋設管配置側面図

5 - 5

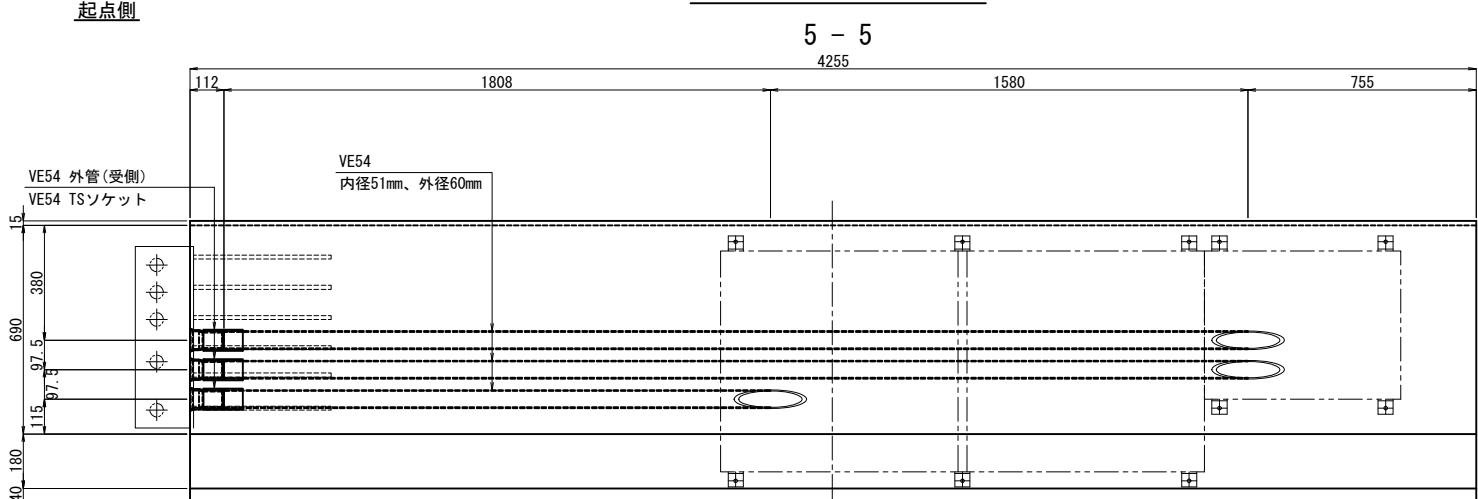

道央自動車道 千歳川大橋(下り線)床版取替工事			
図面の種類	千歳川大橋(下り線) P18-P24 プレキャスト壁高欄詳細図(46)		
縮 尺	図 示	図面番号	/
設計会社名	戸田建設株式会社		
施工会社名	戸田建設株式会社		
事務所名	東日本高速道路株式会社 北海道支社 札幌管理事務所		


千歳川大橋（下り線）P15-P24 場所打ち壁高欄詳細図 S=1:20



[P15路肩側・中分側]


断面図

1 - 1

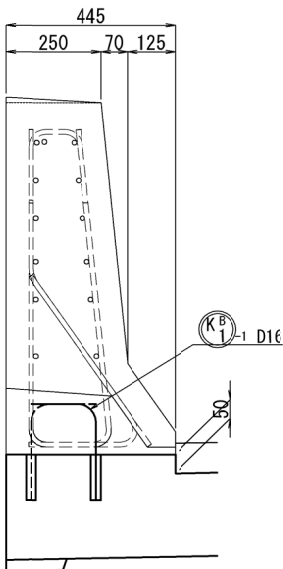

側面図


2 - 2

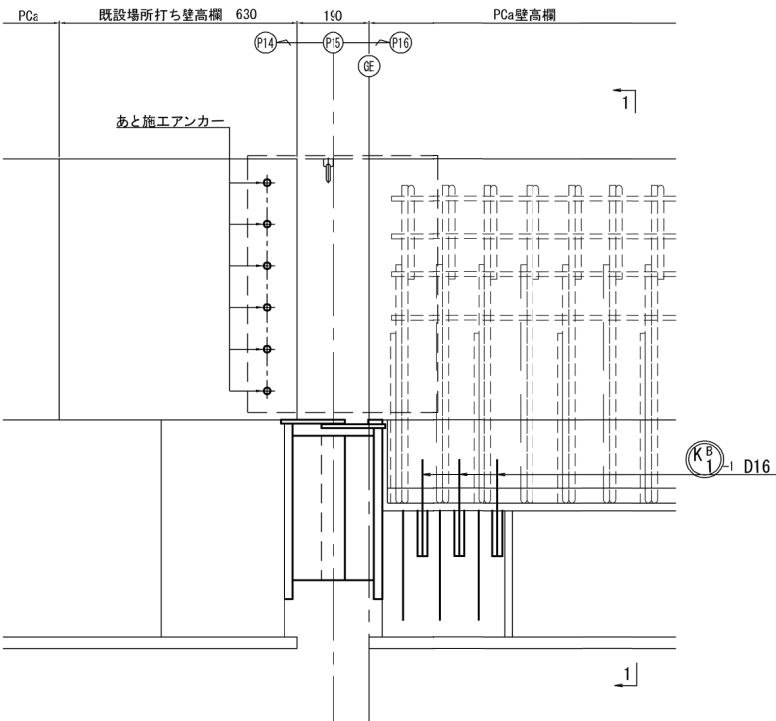

[P24路肩側・中分側]


側面図

2 - 2

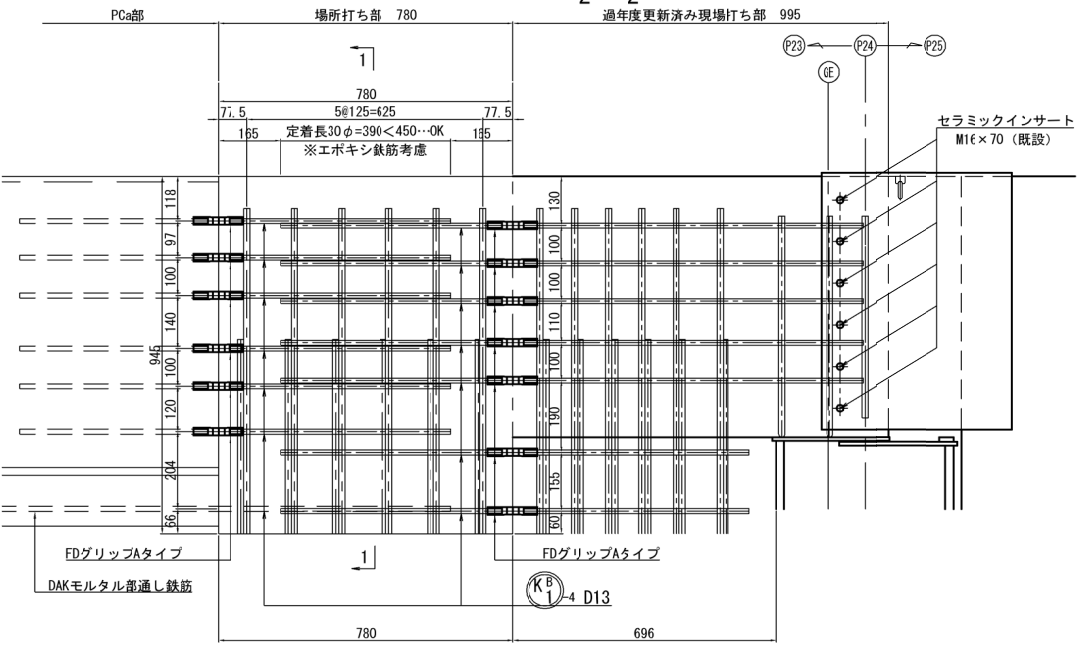


断面図

1 - 1

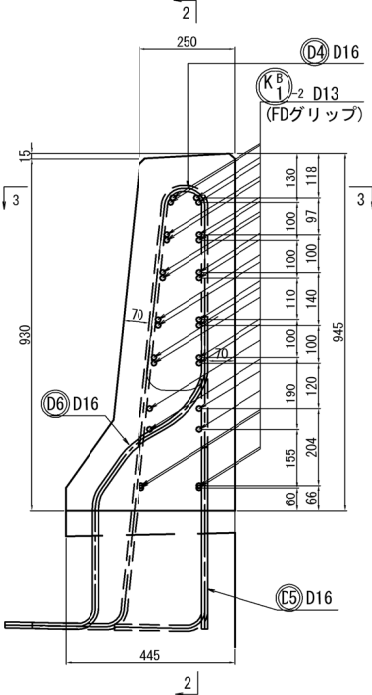

平面図

3 - 3

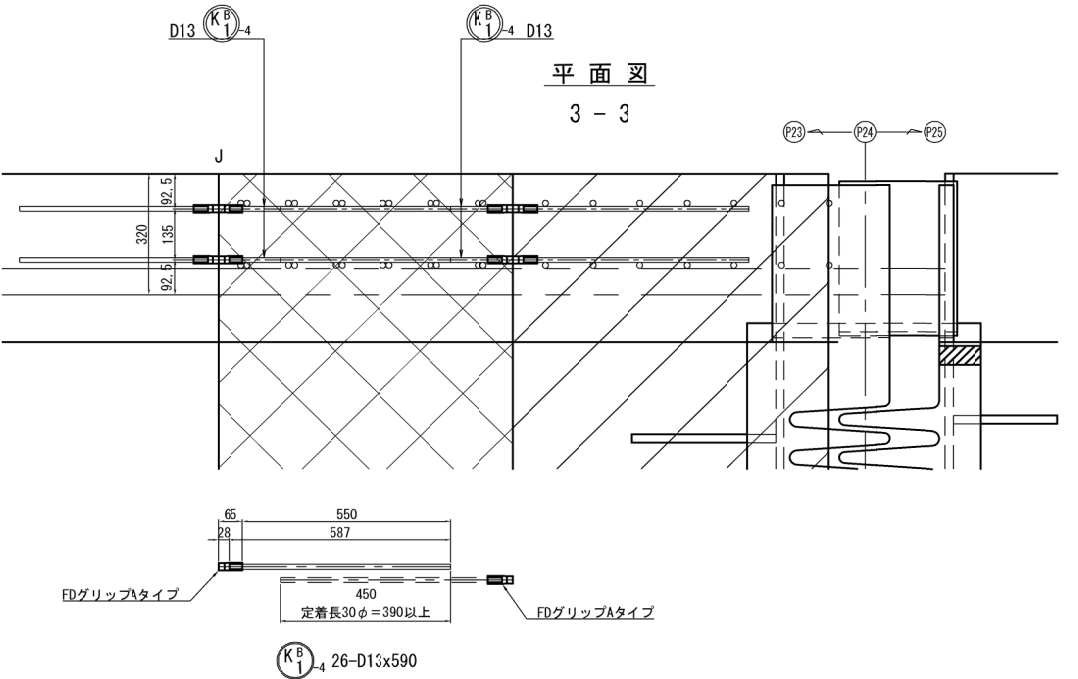

鉄筋表

記号	径	長さ (mm)	本数	単位質量 (kg/m)	1本当り質量 (kg/本)	質量 (kg)	適用
KB1-1	D16	410	6	0.995	0.41	3	7
計							3 kg
鉄筋質量集計 (SD345)							
			普通鉄筋	塗妻鉄筋	溶融亜鉛めっき鉄筋	合計	
	D13	-	0 kg	-	-	0 kg	
	D16	-	3 kg	-	-	3 kg	
	合計	-	3 kg	-	-	3 kg	

※エポキシ樹脂塗装鉄筋

鉄筋表

記号	径	長さ (mm)	本数	単位質量 (kg/m)	1本当り質量 (kg/本)	質量 (kg)	適用
KB1-4	D13	590	26	0.995	0.59	15	15 kg
計							15 kg
鉄筋質量集計 (SD345)							
			普通鉄筋	塗妻鉄筋	溶融亜鉛めっき鉄筋	合計	
	D13	-	15 kg	-	-	15 kg	
	D16	-	0 kg	-	-	0 kg	
	合計	-	15 kg	-	-	15 kg	

※エポキシ樹脂塗装鉄筋


D4, D5, D6に関しては、床版工にて計上する。

道央自動車道 千歳川大橋（下り線）床版取替工事			
図面の種類	千歳川大橋（下り線）P15-P24 場所打ち壁高欄詳細図		
縮尺	図示	図面番号	/
設計会社名	戸田建設株式会社		
施工会社名	戸田建設株式会社		
事務所名	東日本高速道路株式会社 北海道支社 札幌管理事務所		


千歳川大橋（下り線） 伸縮継手詳細図（11）

S=1:50


P18橋脚

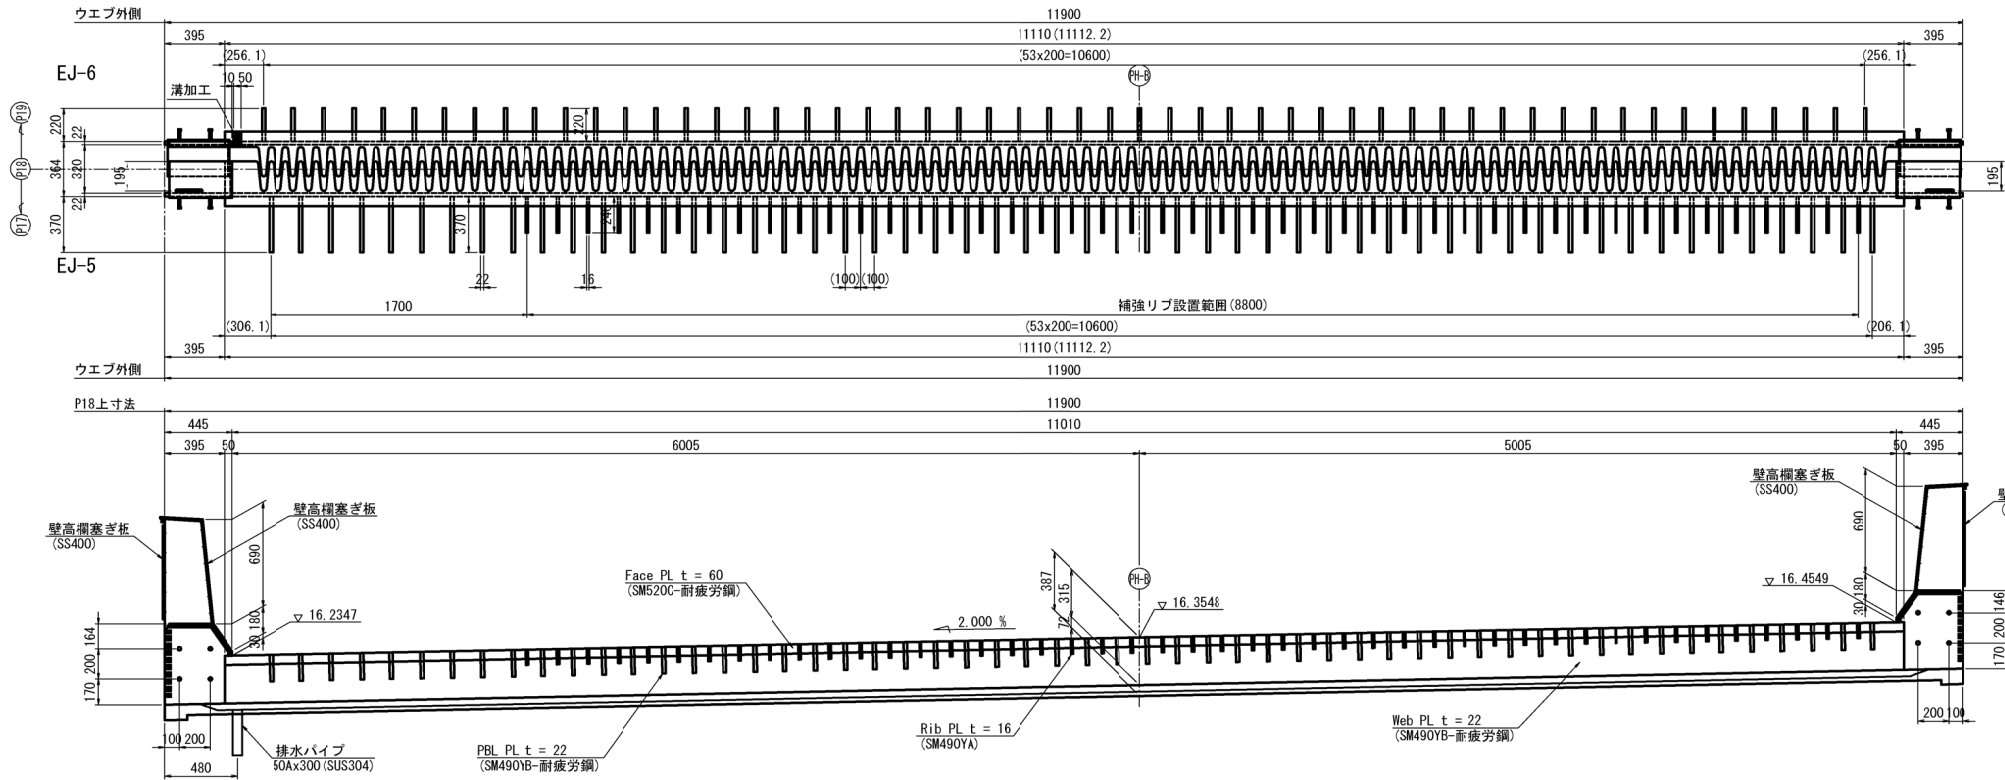


断面図 S=1:25

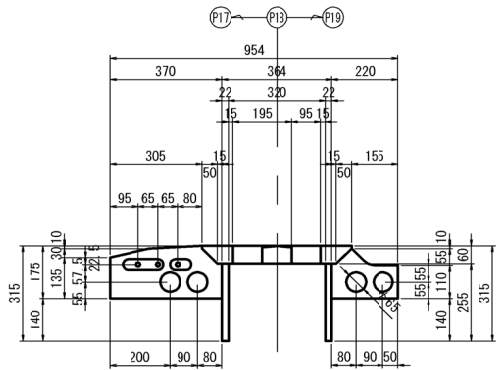


フェイスプレート詳細図 S=1:25

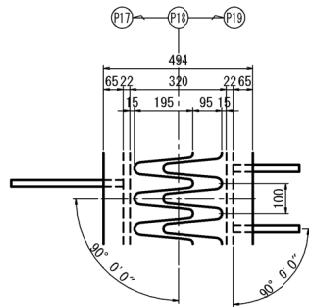


断面図 S=1:25

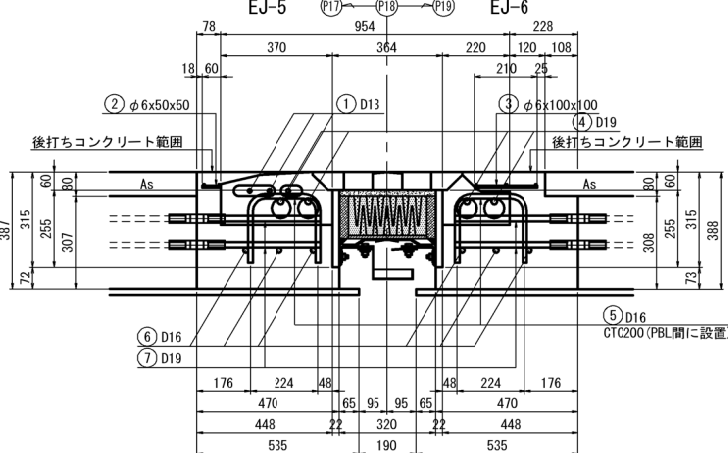


壁高欄塞ぎ板詳細図 S=1:25

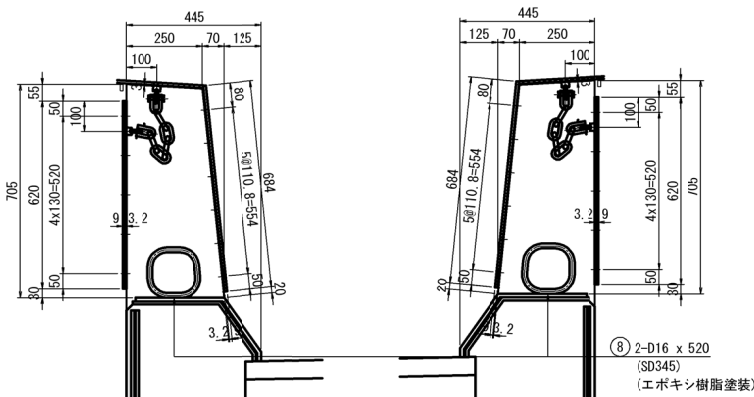


遊間グラフ

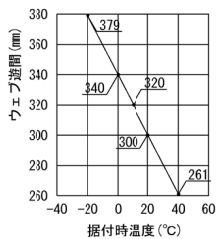


プラウ誘導板詳細図 S=1:25

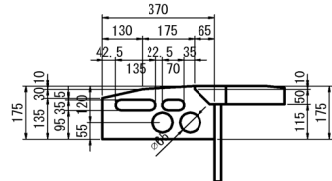


補強リブ詳細図 S=1:25

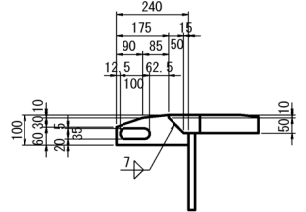

非排水断面図 S=1:25

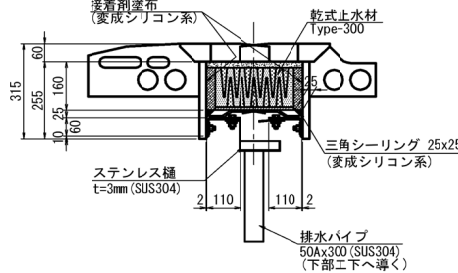

フェイスプレート先端加工 S=1:25

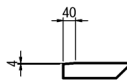

鉄筋表

記号	径	長さ	本数	単位質量	1本当り質量	質量	摘要
※ ①	D13	112.0	3	C.995	11.15	33	—
②	φ6x50x50	60x11310	—	E.88	—	6	—
③	φ6x100x100	210x11310	—	A.44	—	10	—
※ ④	D19	112.0	4	2.25	25.22	101	—
※ ⑤	D16	630	107	1.56	0.98	105	—
※ ⑥	D16	112.0	6	1.56	17.49	105	—
※ ⑦	D19	340	256	1.56	0.59	151	—
※ ⑧	D16	520	2	1.56	0.81	2	—
合計							Ɛ13
D19							252 kg
D16							212 kg
D13							33 kg
φ6x50x50							6 kg
φ6x100x100							10 kg
合計							Ɛ13 kg

※印は塗装鉄筋を示す。


設計条件

温度変化移動量	122.9 mm
遊間量	190 mm


材料表

記号	項目	種別	規格	数量	備考
1	SEFジョイント100	車道部	185	11.900 m	止水樋付
2	塞ぎ板	壁高欄	SS400	2 組	メッキ
3	鉄筋	網鉄筋	SR235 (相当)	6 kg	
4	鉄筋	補強筋	SD345	497 kg	
5	後打ちコンクリート		24N/mm2以上	4.98 m3	

後打ちコン部寸法図

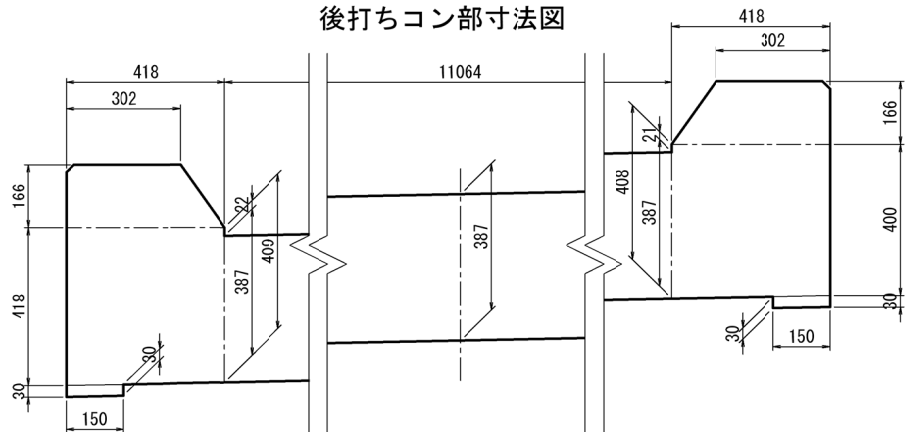

配置図

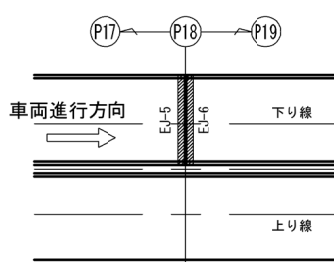

注記)


- 施工において図面相当品とする。
- 後打ち部コンクリートの強度は24N/mm2以上とすること。
- () 内寸法は勾配なり寸法を示す。

道央自動車道 千歳川大橋（下り線）床版取替工事			
図面の種類	千歳川大橋（下り線） 伸縮継手詳細図（11）		
縮尺	図示	図面番号	
設計会社名	戸田建設株式会社		
施工会社名	戸田建設株式会社		
事務所名	東日本高速道路株式会社 北海道支社		


千歳川大橋（下り線） 伸縮継手詳細図（12）
P18橋脚

S=1:25



壁高欄塞ぎ板詳細図

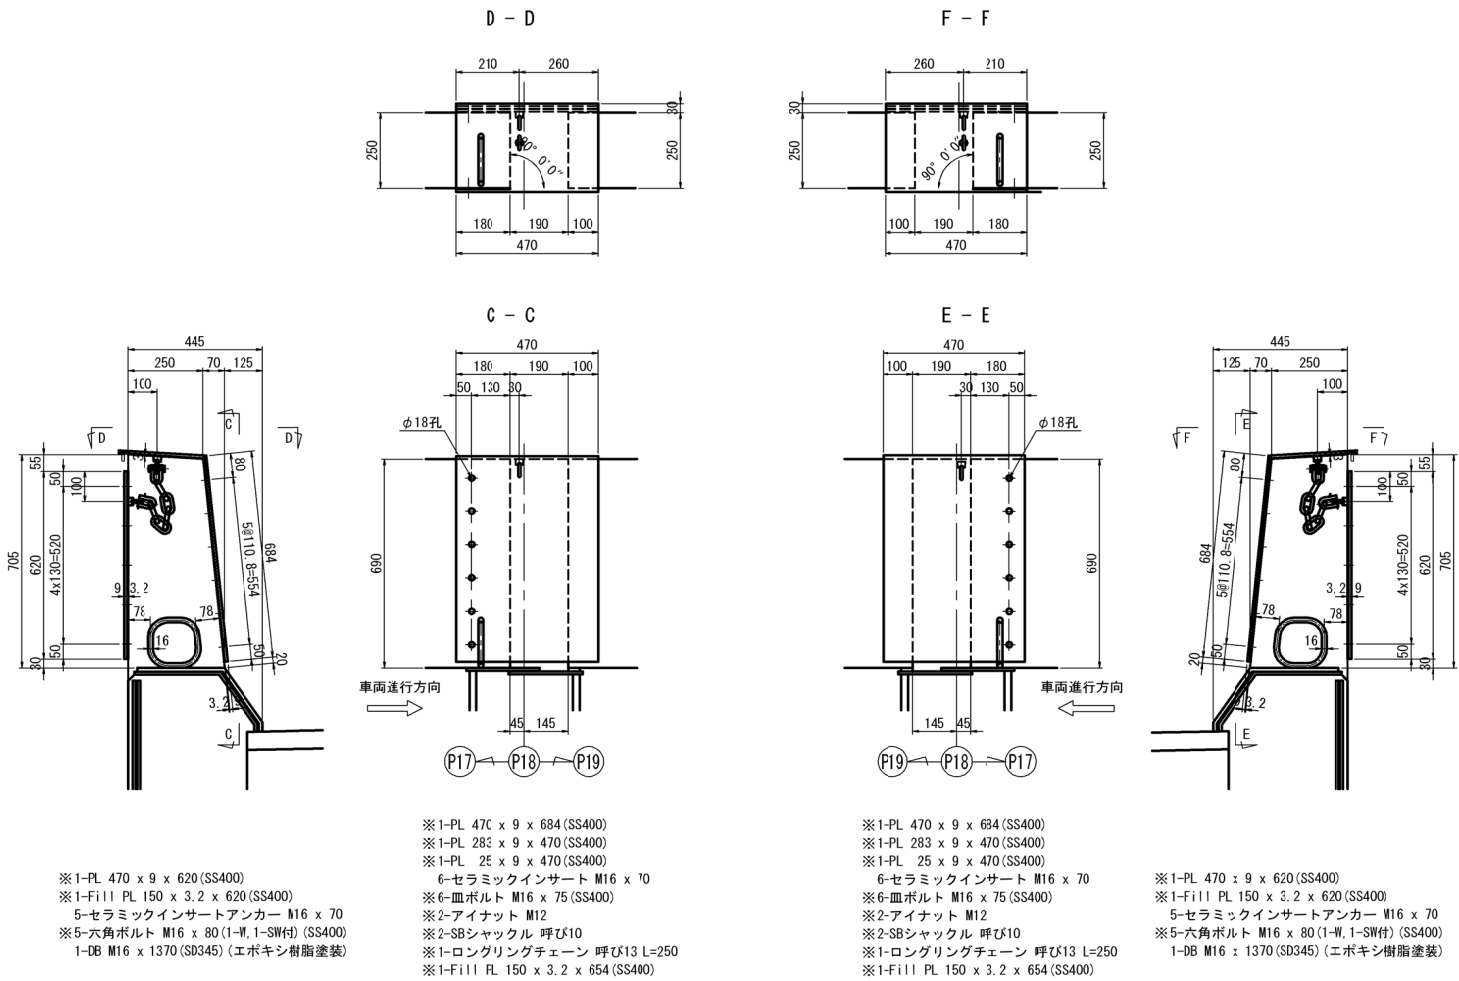

“a”部詳細図 S=1:12.5

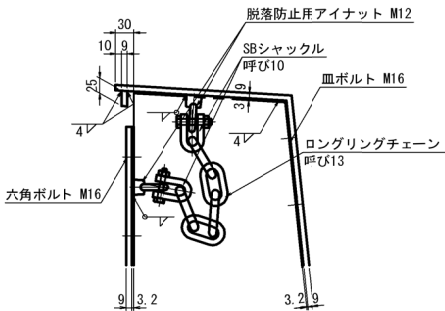

取付ボルト詳細 S=1:7.5

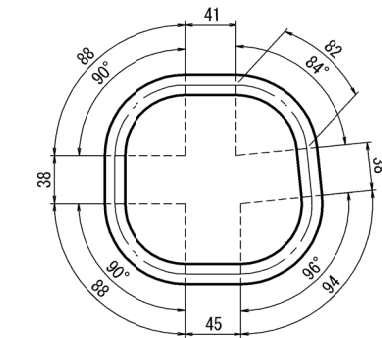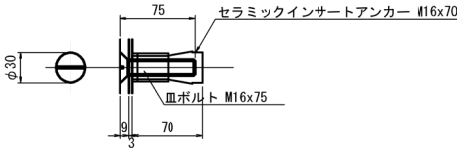


2-D16 x 520 (SD345) (エポキシ樹脂塗装)

注記)
1. 特記なき材質は全てSM400Aを示す。
2. ※印の部材は溶融亜鉛メッキを施す。亜鉛の膜厚は、
JIS H 8641 HDZT77とする。ただし、ボルト・ナット類は
HDZ749とする。


道央自動車道 千歳川大橋（下り線）床版取替工事			
図面の種類	千歳川大橋（下り線） 伸縮継手詳細図（12）		
縮尺	図示	図面番号	
設計会社名	戸田建設株式会社		
施工会社名	戸田建設株式会社		
事務所名	東日本高速道路株式会社 北海道支社		

千歳川大橋（下り線）P15-P24 コンクリート表面被覆工詳細図（1）


側面図 S = 1:600

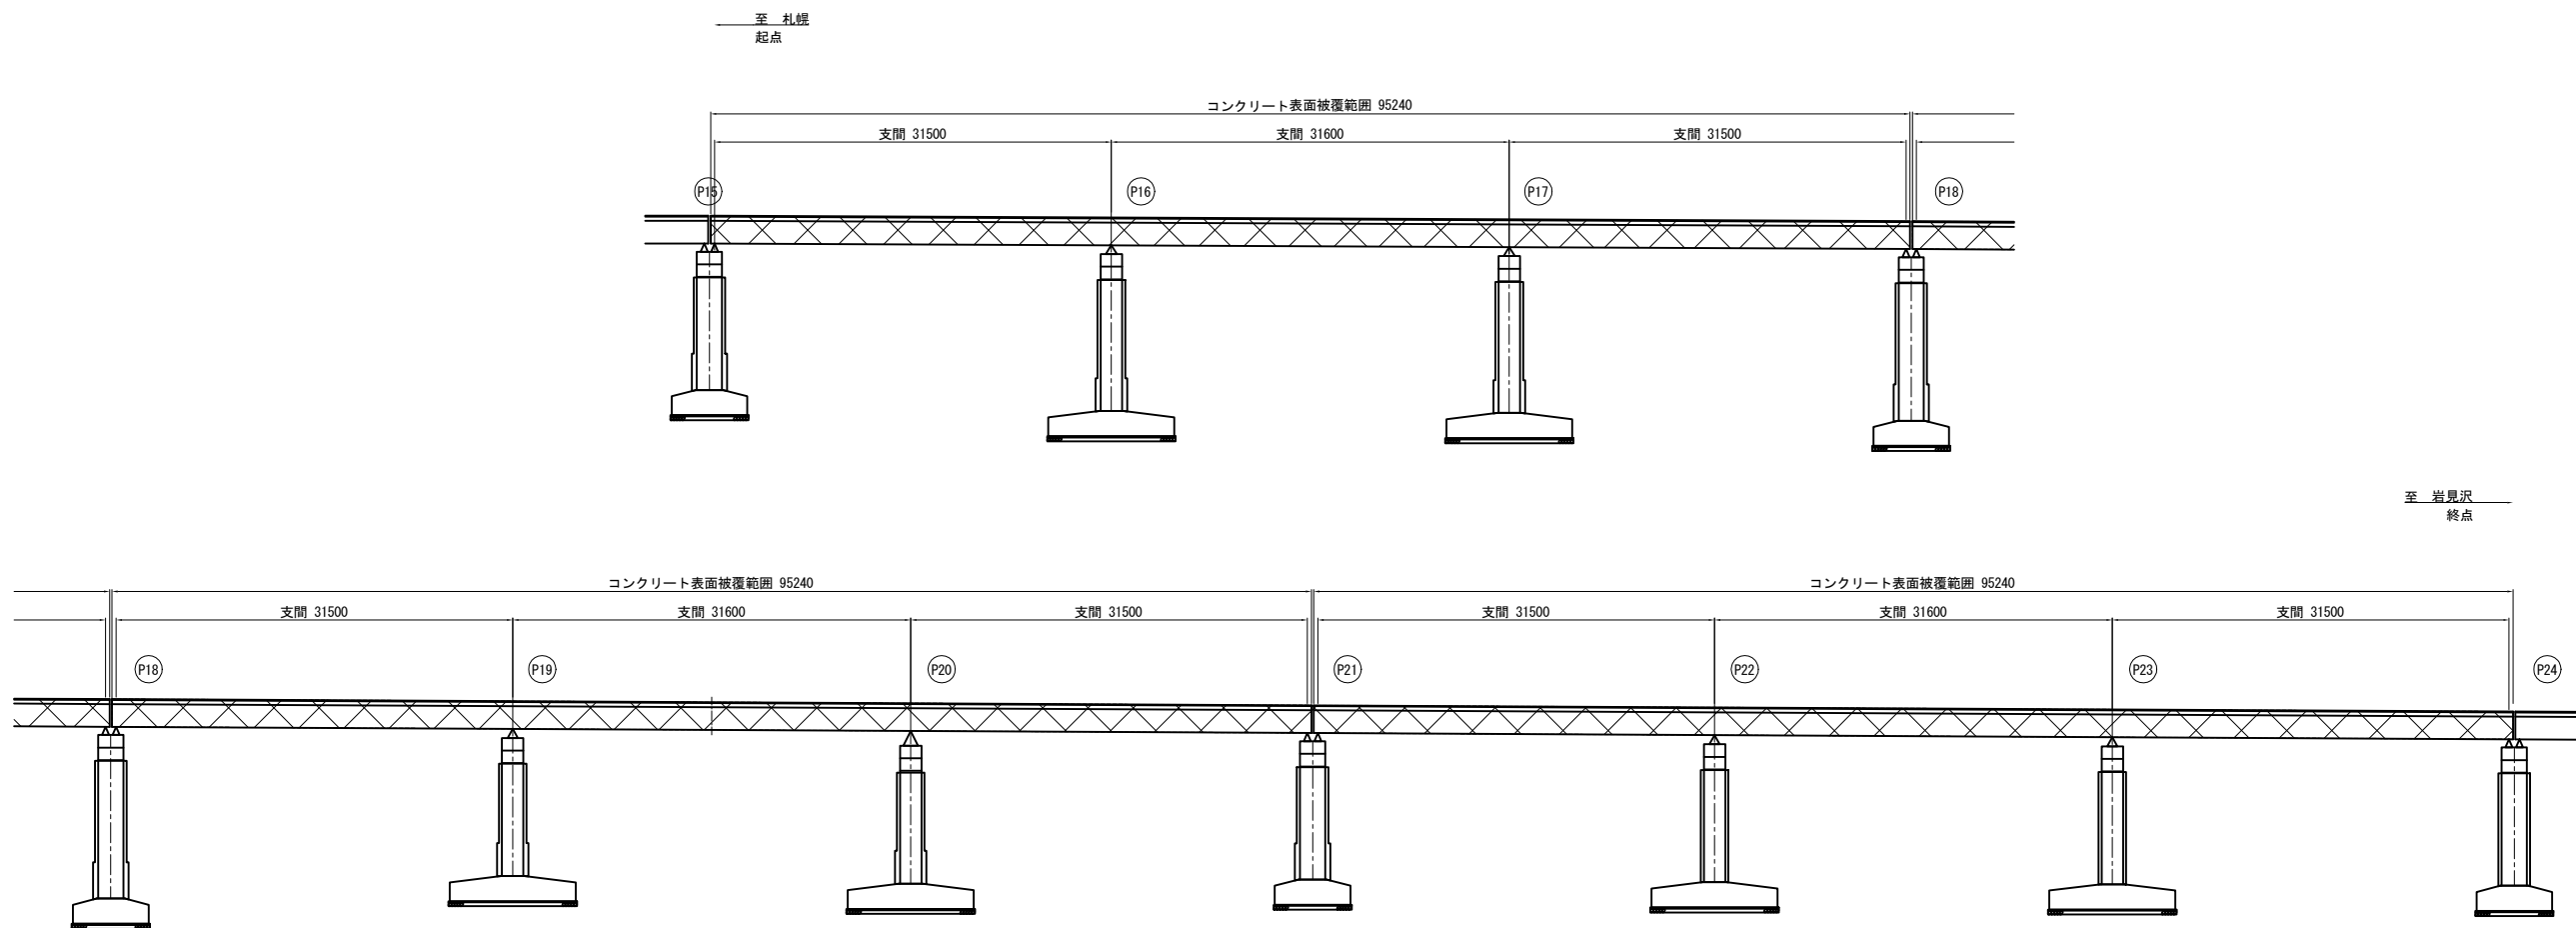

平面図 S = 1:250

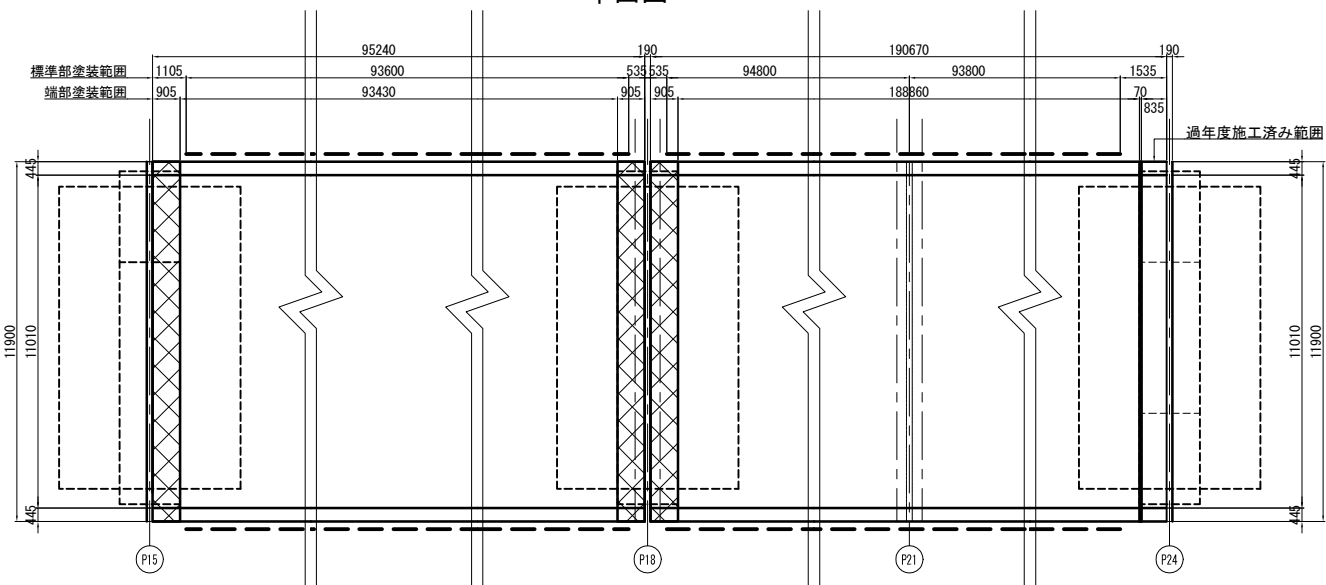

平面図 S = 1:200

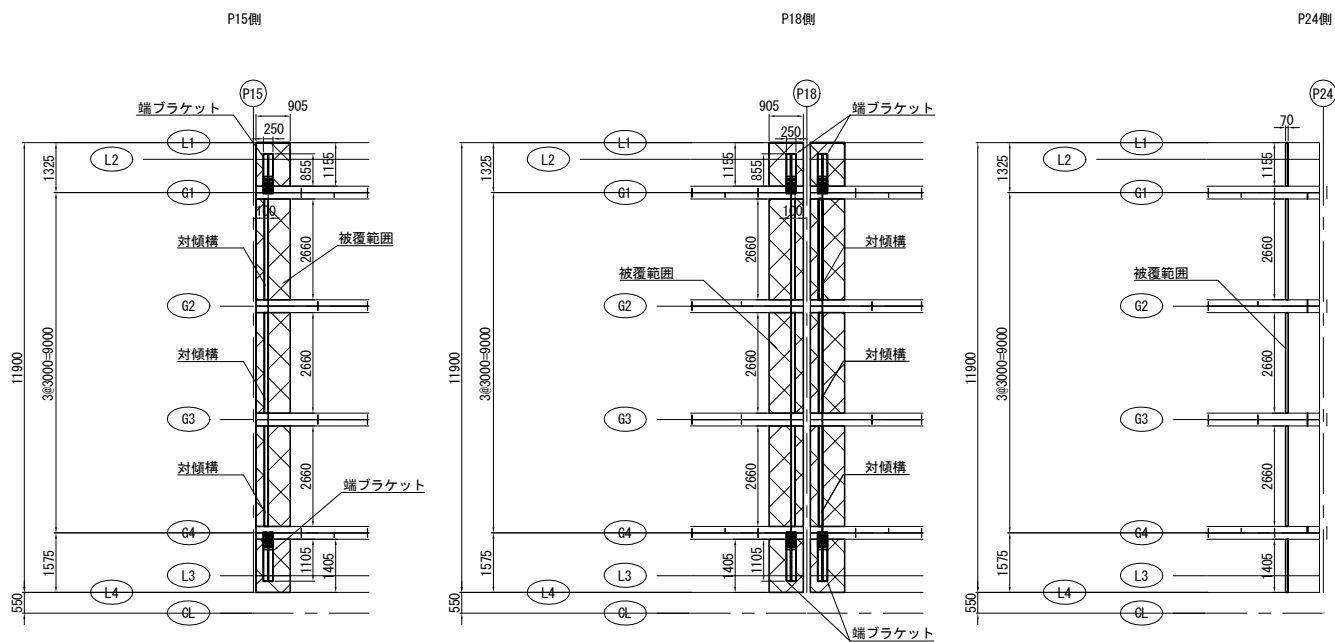


道央自動車道 千歳川大橋（下り線）床版取替工事			
図面の種類	千歳川大橋（下り線）P15-P24 コンクリート表面被覆工詳細図（1）		
縮 尺	図示	図面番号	/
設計会社名	戸田建設株式会社		
施工会社名	戸田建設株式会社		
事務所名	東日本高速道路株式会社 北海道支社 北広島管理事務所		


	道失自動車道 千歳川大橋（下り線）床版取替工事
図面の種類	千歳川大橋（下り線）P15-P24 コンクリート表面被覆工詳細図（②）
縮 尺	図 示 図面番号 /
設計会社名	戸田建設株式会社
施工会社名	戸田建設株式会社
事務所名	東日本高速道路株式会社 北海道支社 北広島管理事務所

千歳川大橋（下り線）P15-P24 舗装打換え工詳細図

切削工範囲 平面図 S=1:500

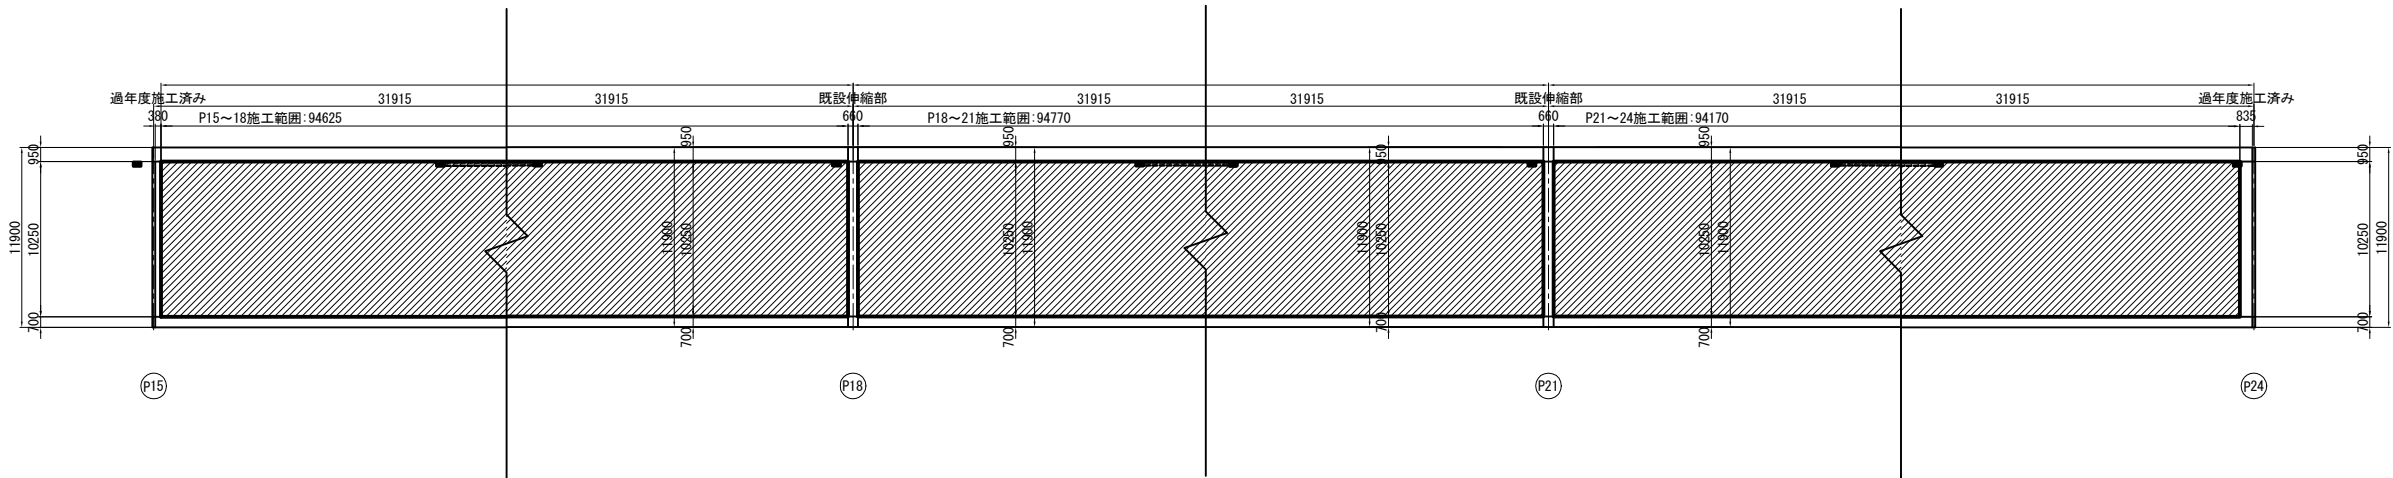


舗装工範囲 平面図 S=1:500

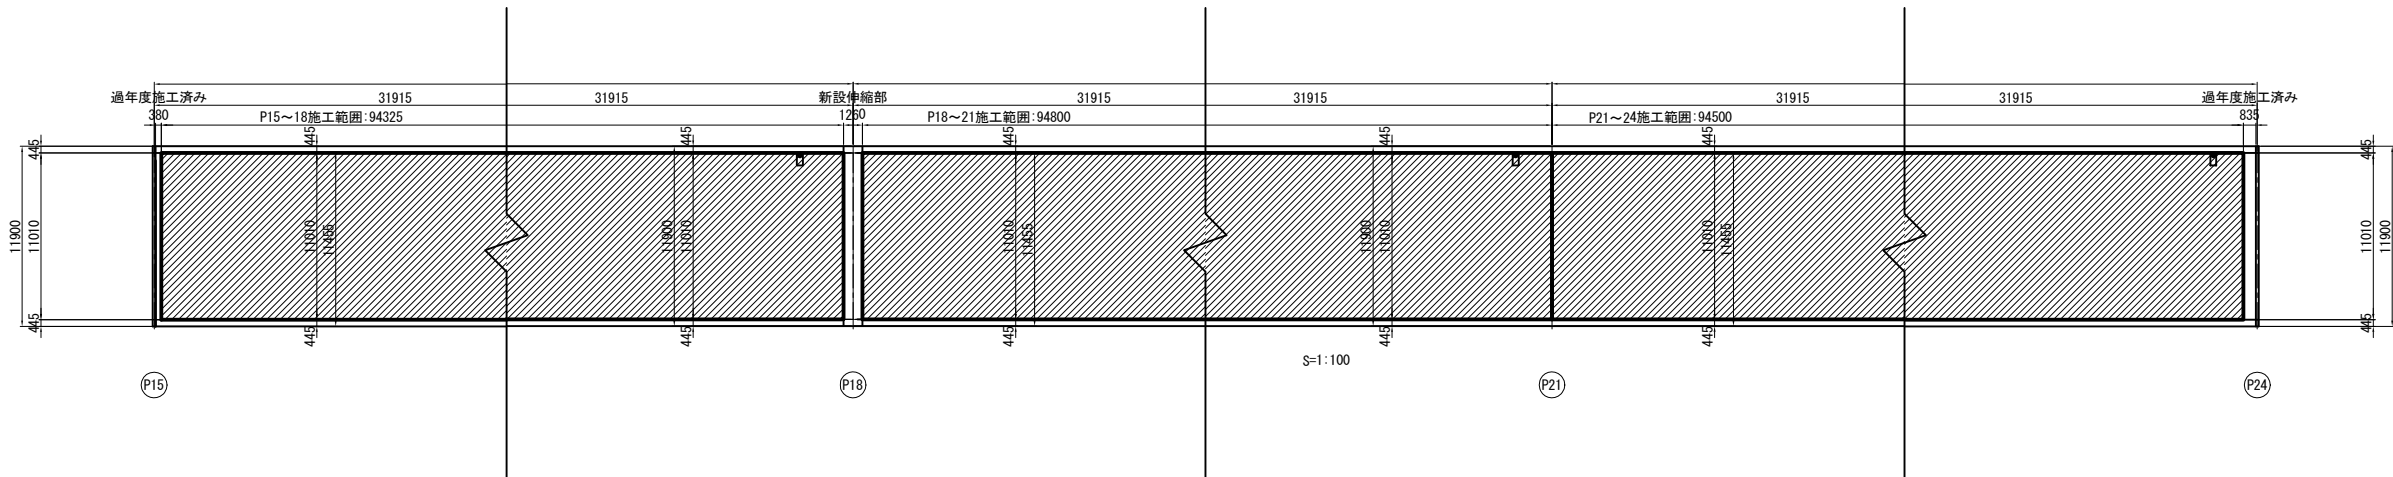


施工時横断面図 S=1:100


切削工

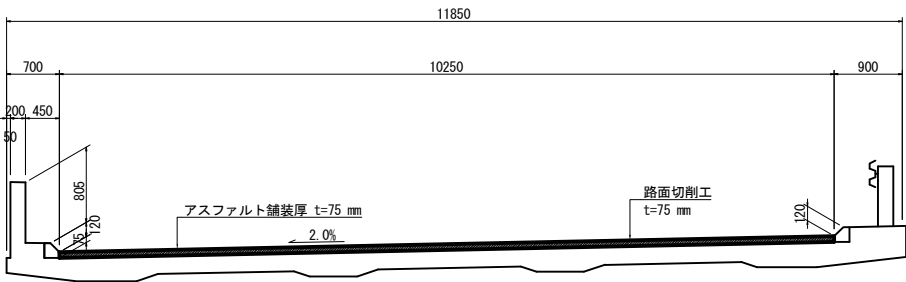

舗装工

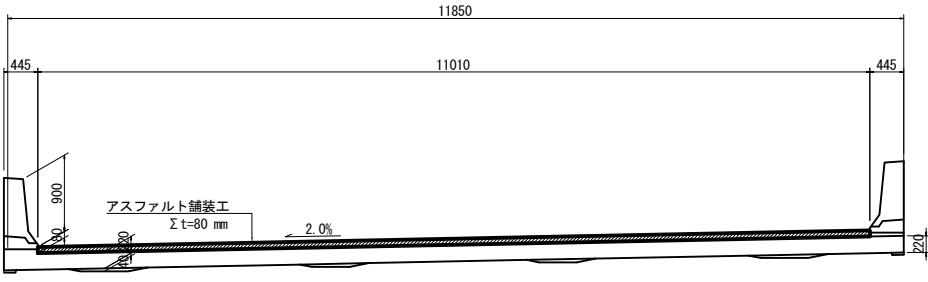

排水樹平面図 S=1:50

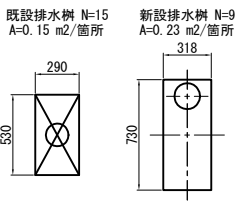


路面切削工・アスファルト舗装工 数量表

項目		単位	P15-18	P18-21	P21-24	合計
路面切削工	アスファルト舗装 t=75mm	m2	969.2	970.7	964.5	2904.3
	アスファルト コンクリート 表層A (t=4cm)	m2	1037.8	1043.0	1039.7	3120.5
	アスファルト コンクリート 橋梁レベリング層A (t=4cm)	m2	1037.8	1043.0	1039.7	3120.5


道央自動車道 千歳川大橋（下り線）床版取替工事				
図面の種類	千歳川大橋（下り線） P15-P24 舗装打換え工詳細図			
縮 尺	図 示	図面番号	/	
設計会社名	戸田建設株式会社			
施工会社名	戸田建設株式会社			
事務所名	東日本高速道路株式会社 北海道支社 北広島管理事務所			

千歳川大橋（下り線）P15-P24 床版防水工詳細図


全体平面図 S=1:500

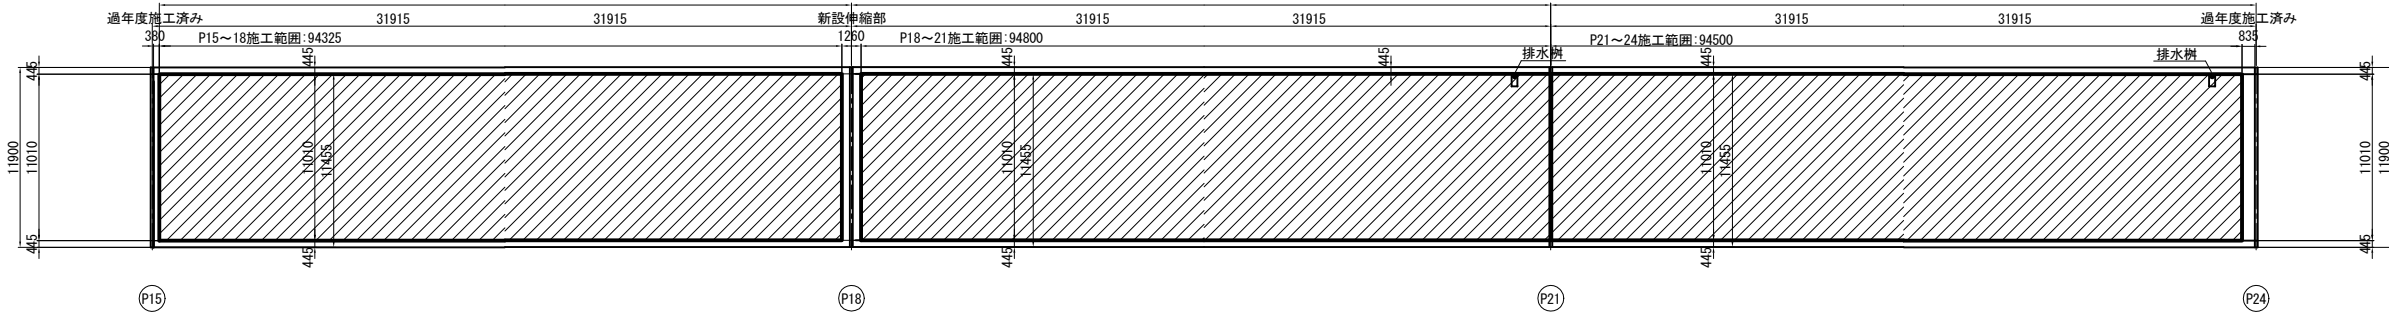


排水柵平面図 S=1:50

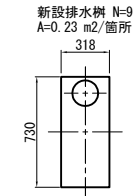

全体断面図 S=1:50

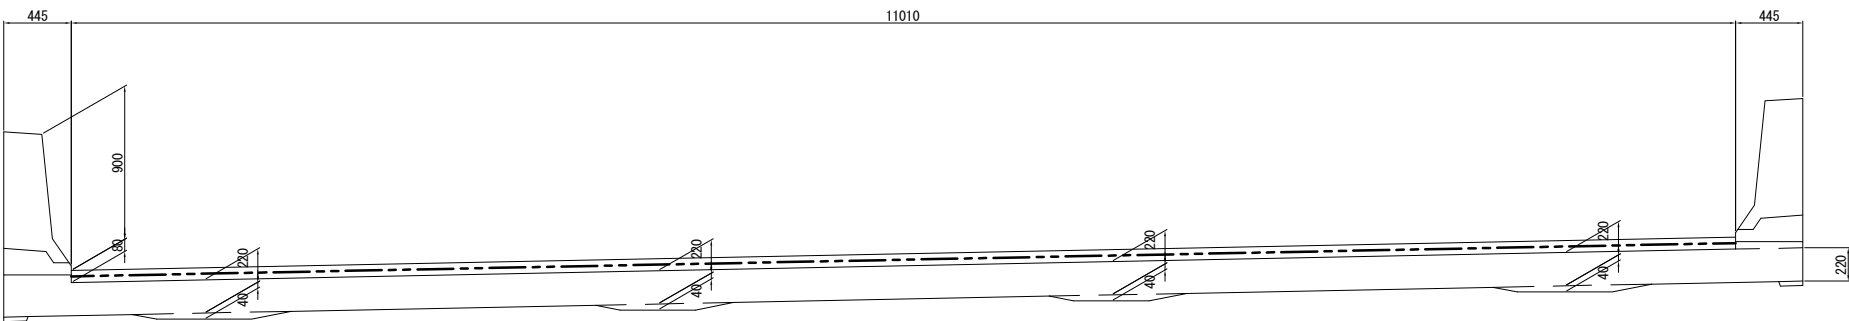


橋軸方向断面図（排水柵部） S=1:10

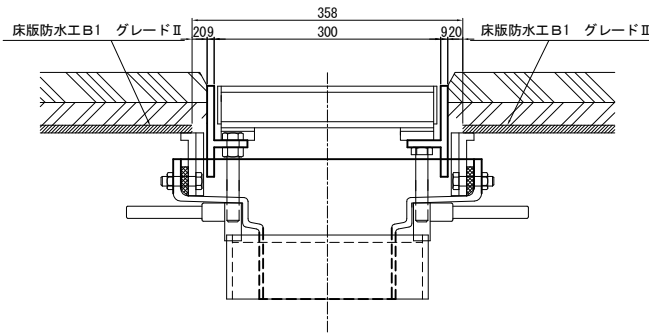


床版防水工 数量表

工種	工種	単位	数量			
			P15-18	P18-21	P21-24	合計
床版防水工	床版防水工（グレードⅡ）	m2	1065.7	1070.3	1066.9	3202.9
	端部保護剤	m2	11.3	11.4	11.3	34.0
端部止水処理工	端部止水処理工A（グレードⅡ）	m2	105.3	105.8	105.5	316.6
床版排水処理工	床版排水処理工	箇所	3	3	3	9


橋軸直角方向断面図（排水柵部） S=1:10

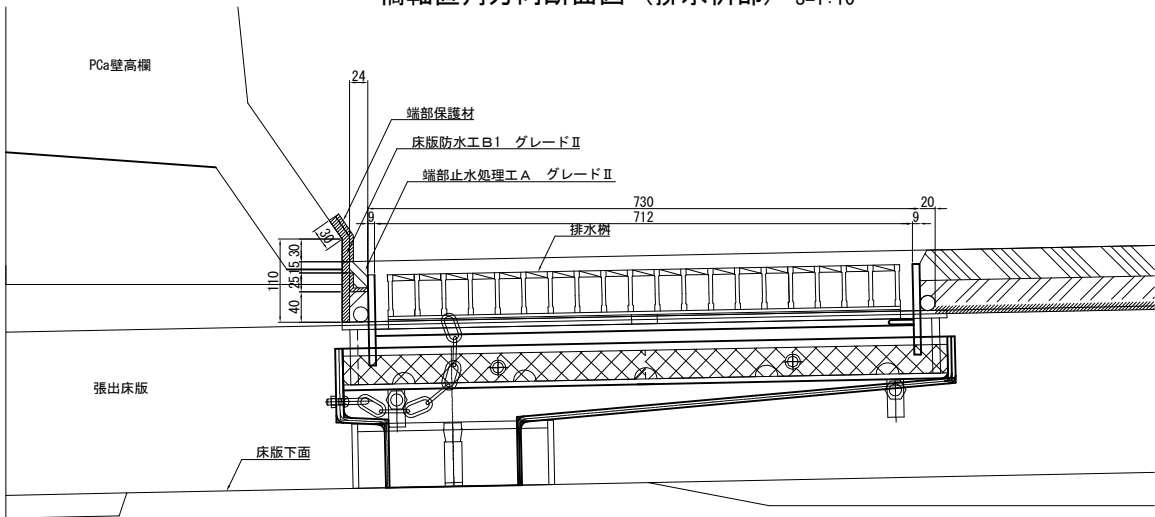


橋軸直角方向断面図 S=1:10

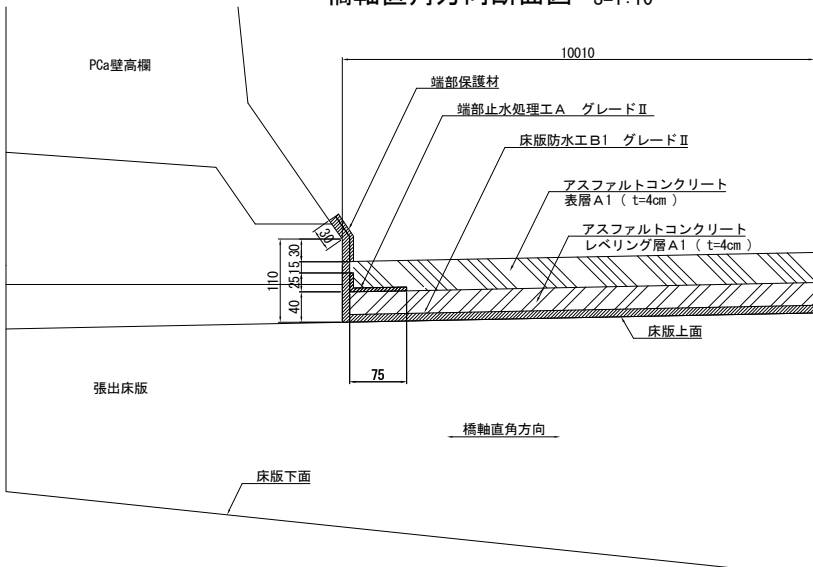

橋軸方向断面図（伸縮装置部） S=1:10

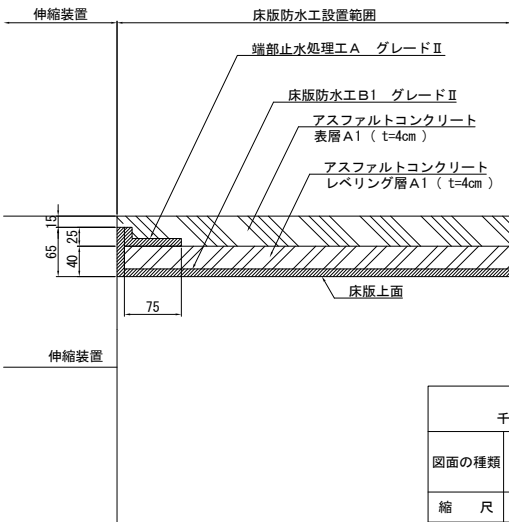

道央自動車道 千歳川大橋（下り線）床版取替工事			
図面の種類	千歳川大橋（下り線） P15-P24 床版防水工詳細図		
縮 尺	図 示	図面番号	/
設計会社名	戸田建設株式会社		
施工会社名	戸田建設株式会社		
事務所名	東日本高速道路株式会社 北海道支社 北広島管理事務所		

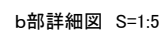風荷重 2kN/m^2 

道央自動車道 千歳川大橋（下り線）床版取替工事			
図面の種類	千歳川大橋（下り線） 飛梁防止柵詳細図（7）		
縮 尺	図 示	図面番号	/
設計会社名	戸田建設株式会社		
施工会社名	戸田建設株式会社		
事務所名	東日本高速道路株式会社 北海道支社 札幌管理事務所		

千歳川大橋（下り線） 飛雪防止柵詳細図（8）

[P15]

数 量 表						
DPH-160(下り線)						
材 料 名	形状寸法	数量	単位	単位重量 (kg)	重量 (kg)	1連当たり
オールアンカー	M8x50 (1緩止N・1W付)	6	組	0.030	0.180	SWCH相当
セラミックインサートアンカー	M20x100	24	組	0.500	12.000	アルミ系セラミックス
M16ボルト	M20x110 (1アンカー用W・1塩ビ W付)	24	組	0.391	9.384	SUS304相当
門扉部	—	—	—	—	284.374	—
				総重量	305.938	


※1 高耐候性めっき鋼板 (Al-19%、Mg-6%) めっき付着量両面300g/㎡以上とする
※2 門扉部以外は再利用。

門扉部(下り線)							
材 料 名	形状寸法	数量	単位	単位重量 (kg)	重量 (kg)	材料規格	表面処理
門柱	H-100x100x6x8 L= 2250	1	本	38.025	38.025	SS400	HDZT77
門柱	H-100x100x6x8 L= 2250	1	本	38.025	38.025	SS400	HDZT77
ベースプレート	t 19 x 150 x 350	2	枚	7.830	15.660	SS400	HDZT77
ワイヤー押えプレート	t 9 x 100 x 100	2	枚	0.707	1.414	SS400	HDZT77
扉枠材	L-75x75x6 H 1080 x W 960	1	基	27.948	27.948	SS400	HDZT77
持手	φ13 L= 304	1	本	0.316	0.316	SS400	HDZT49
縦材	t 6 x 260 (曲) L= 1500	1	本	18.369	18.369	SS400	HDZT77
無孔折板100	t1.6x250 L= 2860	1	枚	10.532	10.532	NSTH400	T30※1
無孔折板100	t1.6x250 L= 1910	5	枚	7.033	35.165	NSTH400	T30※1
無孔折板100	t1.6x250 L= 900	4	枚	3.314	13.256	NSTH400	T30※1
〃 取付ボルト	M8x30 (1緩止N・2W付)	44	組	0.027	1.188	強度区分4.6相当	HDZT49
連結金具	t 6 x 50 x 1500	1	枚	3.533	3.533	SS400	HDZT77
〃 取付ボルト	M8x30 (1緩止N・2W付)	11	組	0.026	0.286	強度区分4.6相当	HDZT49
伸縮プレート(パネル用)	t 6 x 135 x 1500	1	枚	9.538	9.538	SS400	HDZT77
〃 取付ボルト	M8x35 (1緩止N・2W付)	12	組	0.028	0.336	強度区分4.6相当	HDZT49
鍵孔プレート	t 3 x 25 x 50	1	枚	0.029	0.029	SS400	HDZT49
〃 取付プレート	t 6 x 35 x 65	1	枚	0.107	0.107	SS400	HDZT49
〃 取付ボルト	M8x30 (1緩止N・2W付)	2	組	0.027	0.054	強度区分4.6相当	HDZT49
鍵 SUS	t3x65 [B-1048-1]追加工	1	ヶ	0.190	0.190	SUS304	—
〃 取付ボルト	トラス小ネジM6x20 (1緩止N・1W付)	2	組	0.009	0.018	SUS304	—
單車3号	φ50 (1緩止N・1N・1W付)	2	ヶ	0.535	1.070	SUS304	—
ガイドローラー3号	φ22	2	ヶ	0.300	0.600	SUS304	—
〃 取付ボルト	M5x20 (1緩止N・2W付)	4	組	0.007	0.028	SUS304	—
ハンガーレール3号	t1.5x44x57 L= 1815	1	本	4.830	4.830	SUS304	—
ドアハンガー3号	90x106追加工	4	ヶ	0.370	1.480	SUS304	—
端末ドアハンガー3号	90x106追加工	2	ヶ	0.370	0.740	SUS304	—
〃 取付ボルト	M10x45 (1緩止N・2W付)	12	組	0.059	0.708	強度区分4.6相当	HDZT49
〃 固定ボルト	M8x65 (1緩止N付)	2	組	0.036	0.072	強度区分4.6相当	HDZT49
戸当り	t2.5x31x44	2	ヶ	0.160	0.320	SUS304	—
ツナギ材	L-75x75x6 L= 2880	1	本	19.728	19.728	SS400	HDZT77
スペーサー	t 9 x 38 x 38	3	枚	0.102	0.306	SS400	HDZT77
〃 取付ボルト	M12x50 (1緩止N・2W付)	3	組	0.093	0.279	強度区分4.6相当	HDZT49
伸縮プレート(ツナギ材用)	t 6 x 145 x 75	1	枚	0.512	0.512	SS400	HDZT77
スリーブ	φ15.9x1.2 L=14	1	組	0.006	0.006	STKM11A	HDZT49
スペーサー(ツナギ材用)	t 6 x 38 x 75	1	枚	0.134	0.134	SS400	HDZT77
〃 取付ボルト	M12x50 (1緩止N・2W付)	3	組	0.093	0.279	強度区分4.6相当	HDZT49
スペーサー	t 16 x 25 x 80	6	枚	0.251	1.506	SS400	HDZT77
レール	L-75x40x5 L= 2800	1	本	19.376	19.376	SS400	HDZT77
スペーサー	t 4.5 x 38 x 38	3	枚	0.051	0.153	SS400	HDZT77
〃 取付ボルト	M12x50 (1緩止N・1W・1テハ W付)	3	組	0.131	0.393	強度区分4.6相当	HDZT49
伸縮プレート(レール用)	t 6 x 145 x 75	1	枚	0.512	0.512	SS400	HDZT77
レール取付プレート	t 6 x 160 x 50 (曲)	1	本	0.377	0.377	SS400	HDZT77
スリーブ	φ15.9x1.2 L=14	1	組	0.006	0.006	STKM11A	HDZT49
スペーサー(レール用)	t 6 x 38 x 75	1	枚	0.134	0.134	SS400	HDZT77
〃 取付ボルト	M12x50 (1緩止N・2W付)	3	組	0.093	0.279	強度区分4.6相当	HDZT49
ガイドPL	t 4.5 x 38 x 1870	1	枚	2.510	2.510	SS400	HDZT77
水切板	t1.6x274 L= 1640	1	枚	5.644	5.644	NSTH400	T30※1
水切板	t1.6x274 L= 1483	1	枚	5.104	5.104	NSTH400	T30※1
パネル落下防止ワイヤー	φ6.3 (6x19) ※両端エンド ロック加工	1	本	0.547	0.547	G種	ナイロン被覆
パネル落下防止ワイヤー	φ6.3 (6x19) ※両端エンド ロック加工	1	本	0.570	0.570	G種	ナイロン被覆
〃 抜け防止ボルト	M16x35 (1緩止付)	2	組	0.130	0.260	強度区分4.6相当	HDZT49
〃 取付ボルト	M8x30 (1緩止N・171付ット・1SW付)	4	組	0.063	0.252	強度区分4.6相当	HDZT49
M8アイボルト	(1緩止N・1W付)	19	組	0.042	0.798	強度区分4.6相当	HDZT49
門扉用落下防止ワイヤー	φ6.3 (6x19) ※両端エンド ロック加工	1	本	0.446	0.446	G種	ナイロン被覆
〃 固定ボルト	M20x35 (1緩止N付)	2	組	0.213	0.426	強度区分4.6相当	HDZT49
				総重量	284.374		

※1 高耐候めっき鋼板 (Al-19%、Mg-6%) めっき付着量両面300g/㎡以上とする


道央自動車道 千歳川大橋（下り線）床版取替工事			
図面の種類	千歳川大橋（下り線） 飛雪防止柵詳細図（8）		
縮 尺	図 示	図面番号	/
設計会社名	戸田建設株式会社		
施工会社名	戸田建設株式会社		
事務所名	東日本高速道路株式会社 北海道支社 札幌管理事務所		

千歳川大橋(下り線) P15-P24 暫定時転落防止網詳細図(1)

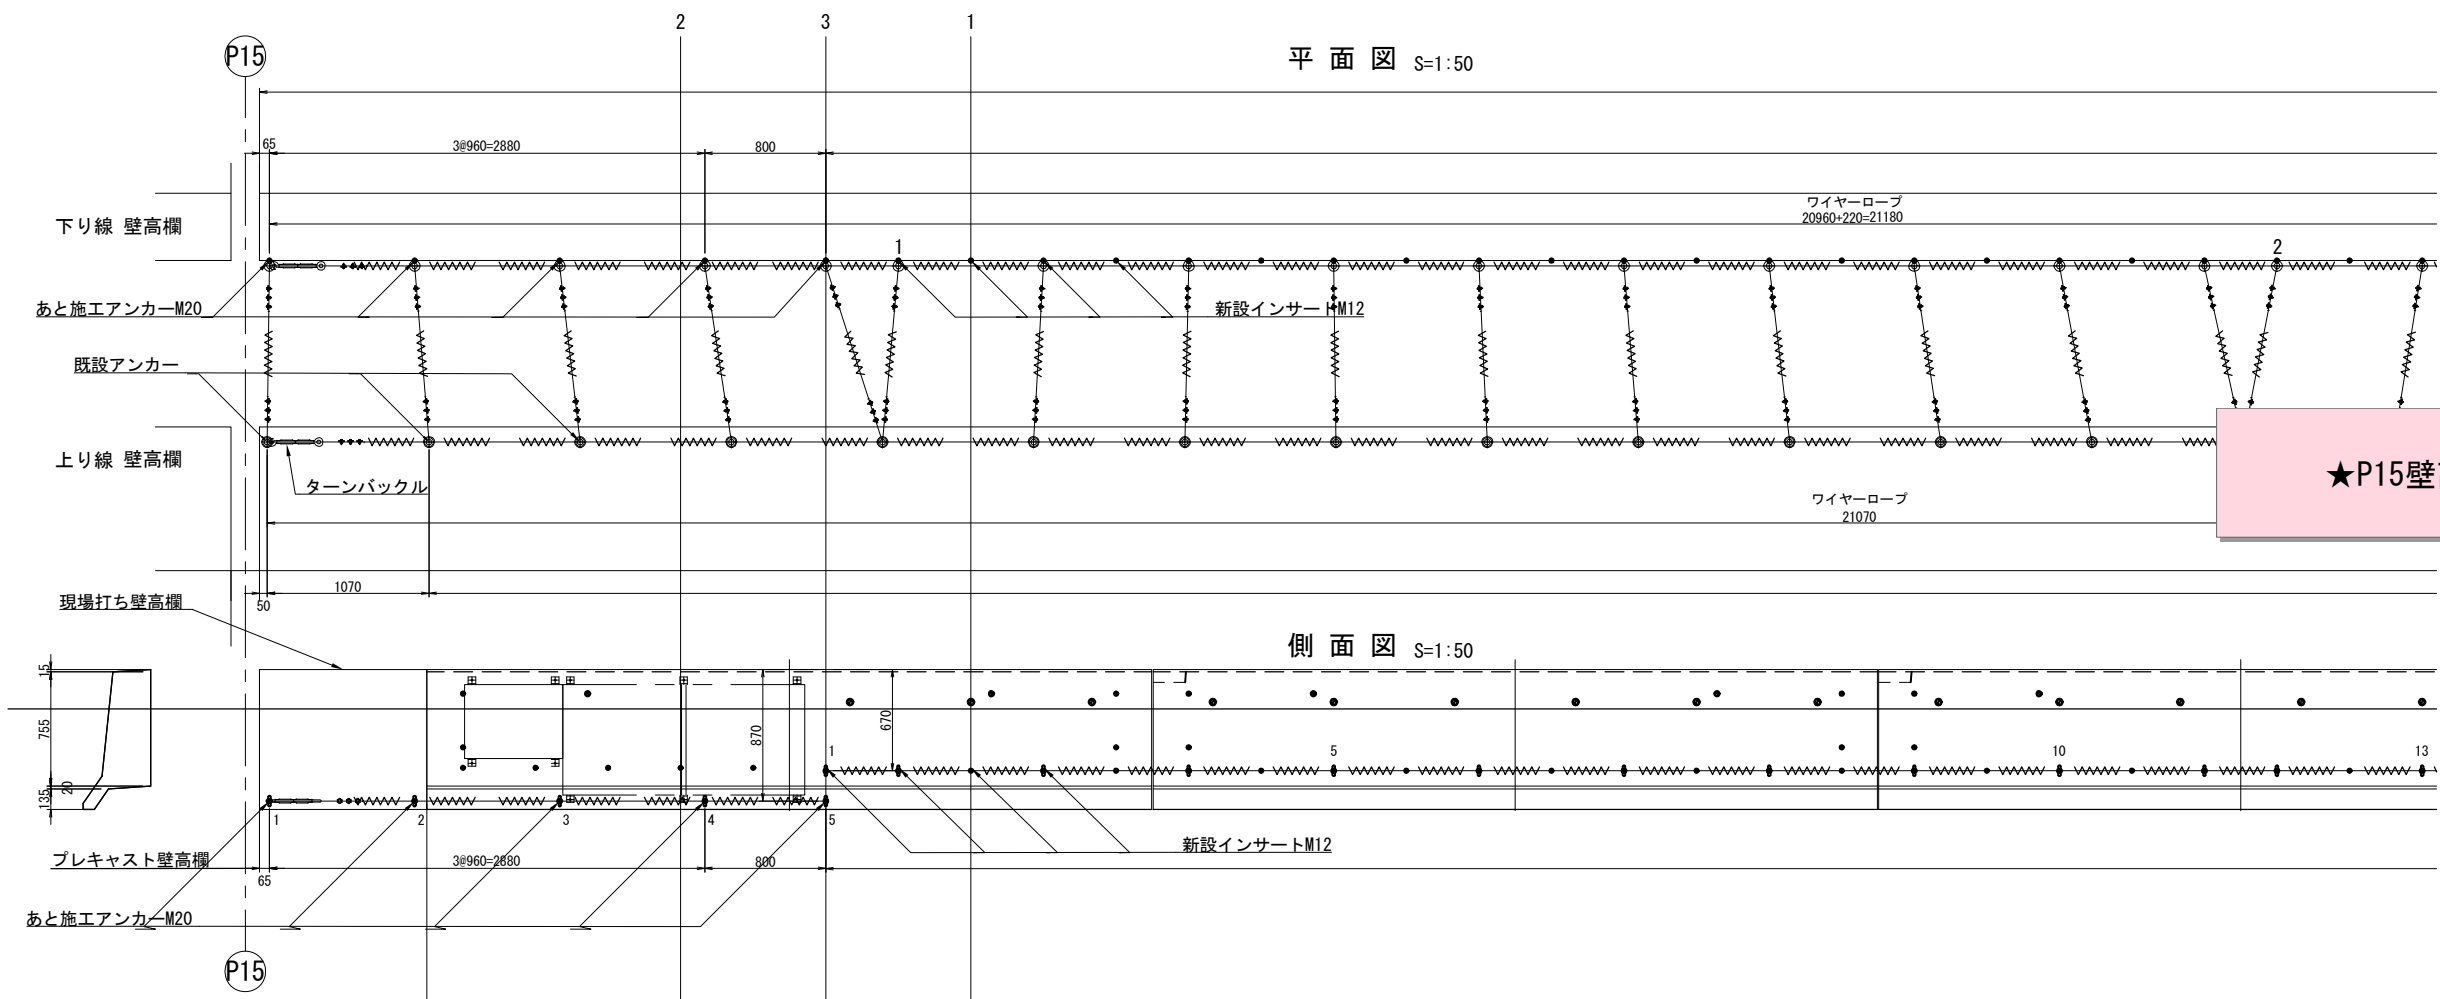

★P15壁高欄ブロック長変更に伴う修正予定

金網およびワイヤーロープ取付詳細図 S=1:10

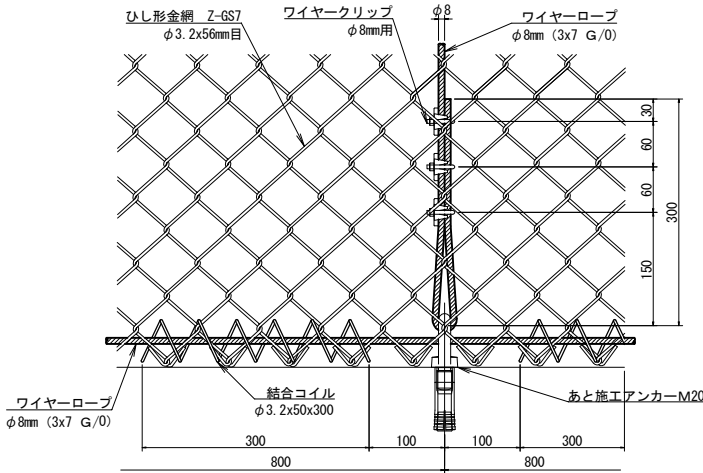


■ 部材リスト・数量表 【 暫定版 】				
部 材 名	規 格	単 位	員 数	表 面 処 理
ひし形金網	φ3.2x56mm目 (JIS G 3552 Z-GS7)	m ²	361.6	亜鉛めっき付着量 380g/m ² 以上
ワイヤーロープ	φ8mm (3x7 G/O)	m	1159.0	素線の亜鉛めっき付着量JIS G3525 G種
結合コイル	φ3.2x50x300 (亜鉛めっき鋼線製)	本	1432	亜鉛めっき付着量 400g/m ² 以上
ワイヤークリップ	φ8mm用	個	2052	亜鉛めっき品 (ドブ)
パイプ式ターンバックル	W5/8	本	48	亜鉛めっき品 (ドブ)
あと施工アンカー (後打ちアンカー)	アイボルト M20 + グリップアンカー M20	本	21	亜鉛めっき品 (ドブ)
インサートアンカー (先埋めアンカー)	セラミックインサートM12 + アイナットM12 + 3種ナットM12 + 寸切ボルトM12x85	個	297	壁高欄埋込 SUS品

【 P15～P24径間 】 ● 数量計算表 【 暫定版 】			
部 材 名	計 算 式		単 位 員 数
ひし形金網	286.98 × 1.26		m ² 361.6
ワイヤーロープ	橋軸方向	下り線 21.78 + 25.56 × 2 + 25.05 + 24.57 + 24.60 × 2 + 24.12 + 24.60 × 3 + 24.08 = 293.72 上り線 21.67 + 25.60 × 2 + 24.67 + 24.55 + 24.60 × 2 + 24.08 + 24.67 + 24.60 × 2 + 23.67 = 292.91	m 1159.0
	橋軸直角方向	1.80 × (297 + 21) = 572.4	


道央自動車道 千歳川大橋(下り線)床版取替工事			
図面の種類	千歳川大橋(下り線) 暫定時転落防止網詳細図(1)		
縮 尺	図 示	図面番号	/
設計会社名	戸田建設株式会社		
施工会社名	戸田建設株式会社		
事務所名	東日本高速道路株式会社 北海道支社 札幌管理事務所		

千歳川大橋(下り線) P15-P24 暫定時転落防止網詳細図(2)


平 面 図 S=1:50

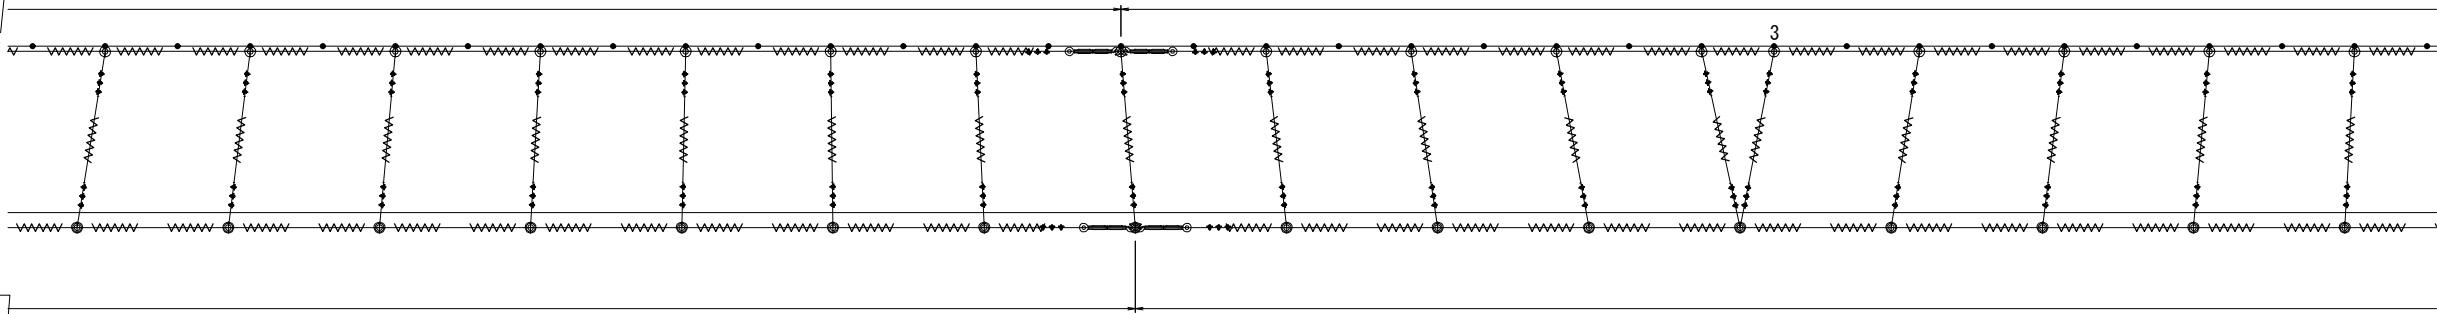


側 面 図 S=1:50

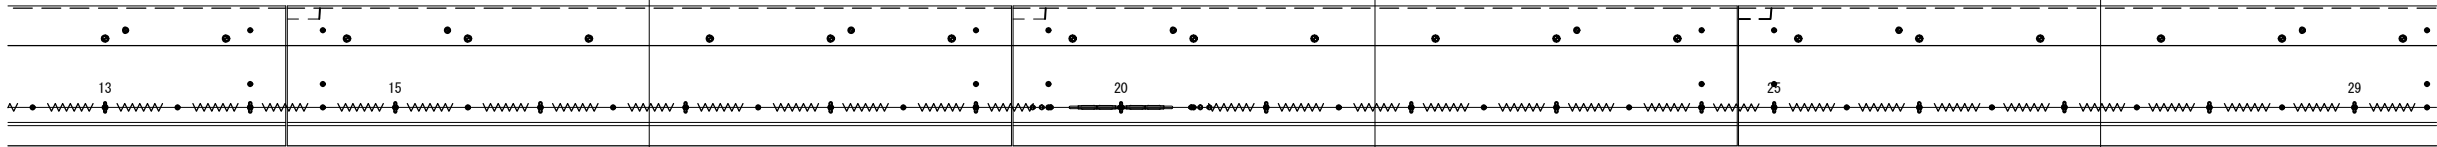

平 面 図 S=1:50

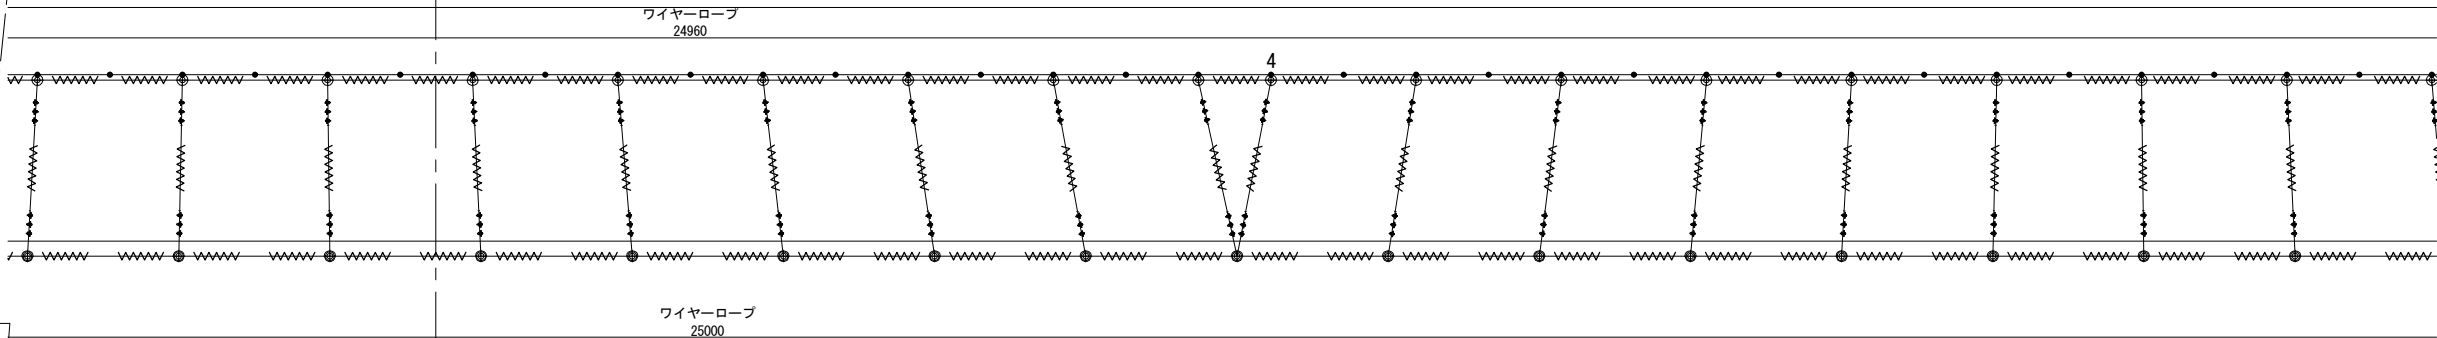


側 面 図 S=1:50

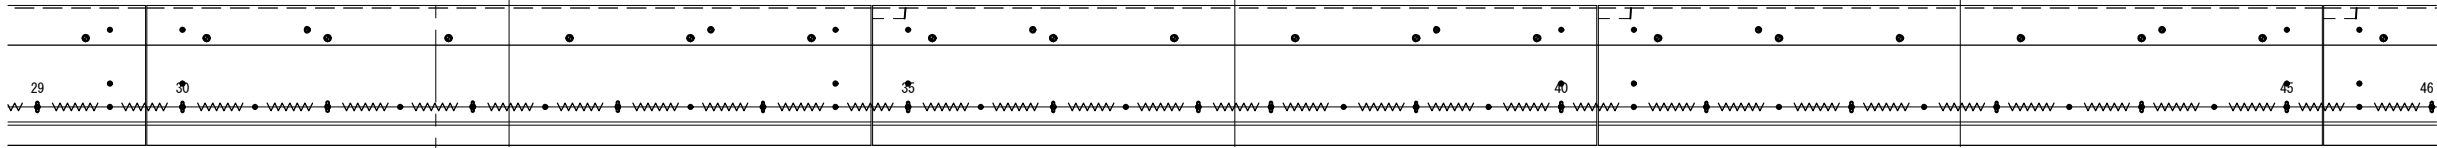


道央自動車道 千歳川大橋(下り線)床版取替工事				
図面の種類	千歳川大橋(下り線) 暫定時転落防止網詳細図(2)			
縮 尺	図 示	図面番号	/	
設計会社名	戸田建設株式会社			
施工会社名	戸田建設株式会社			
事務所名	東日本高速道路株式会社 北海道支社 札幌管理事務所			

千歳川大橋(下り線) P15-P24 暫定時転落防止網詳細図(3)


平面図 S=1:50

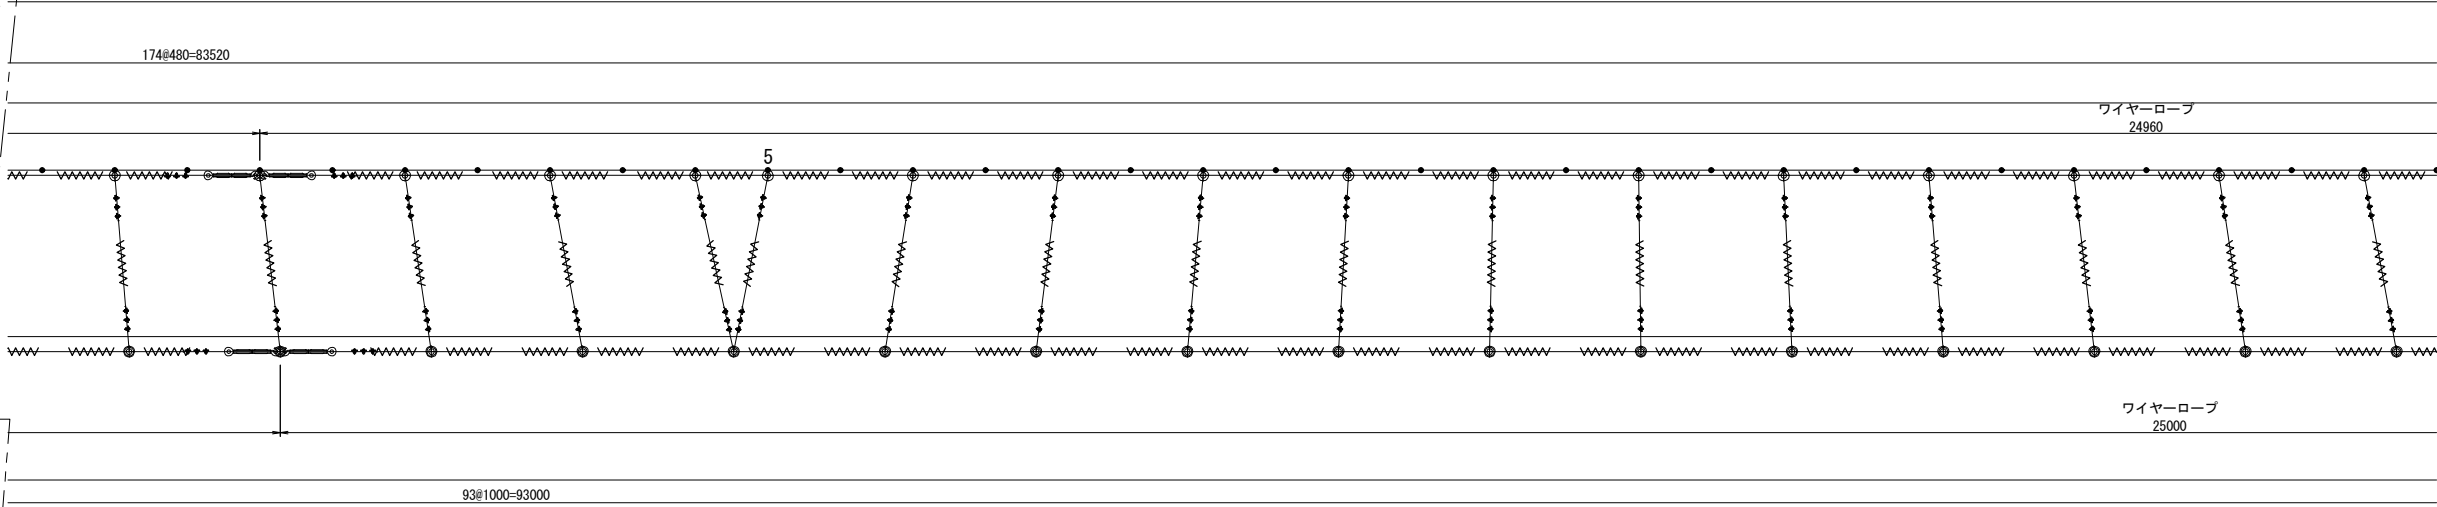


側面図 S=1:50

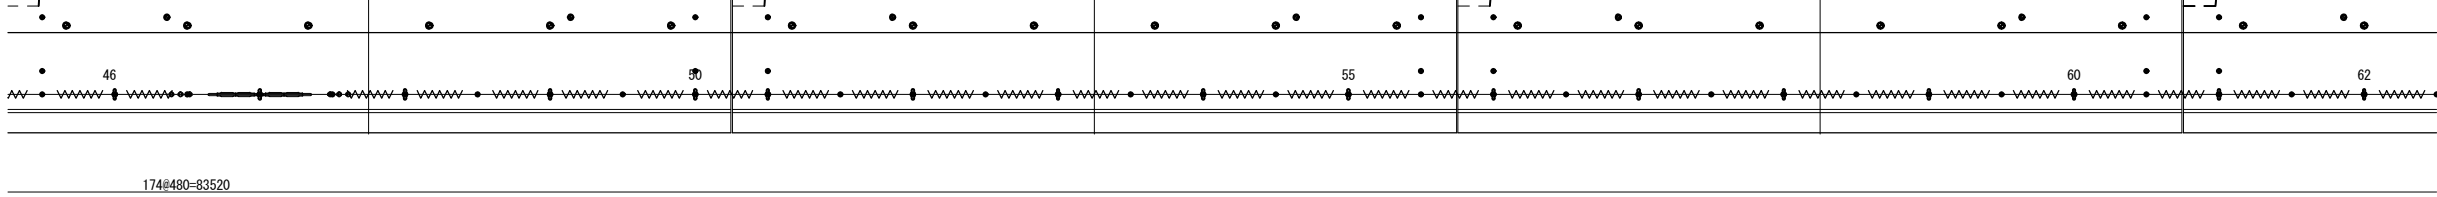

平面図 S=1:50

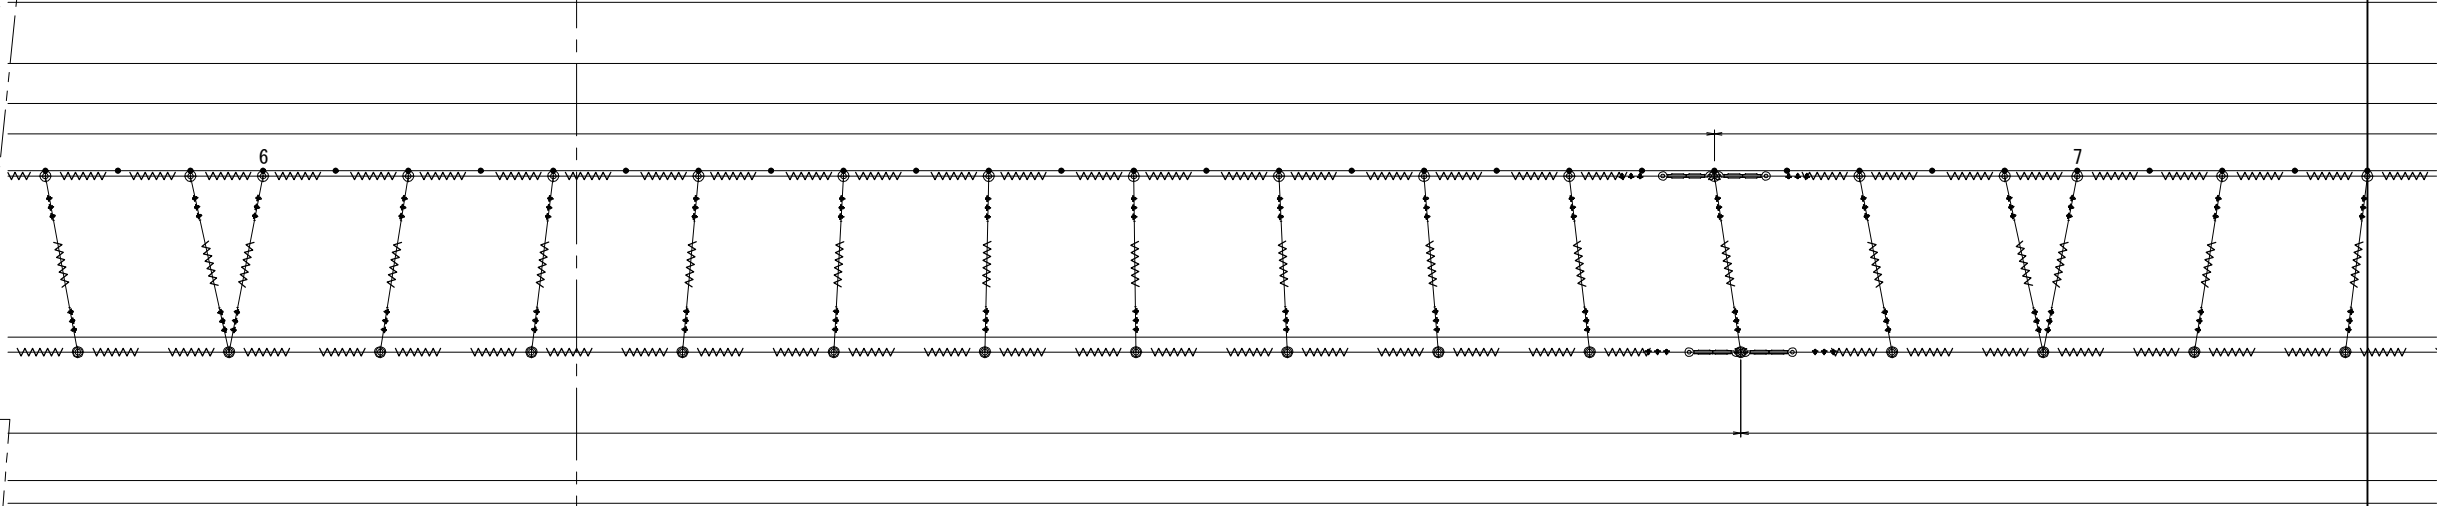


側面図 S=1:50

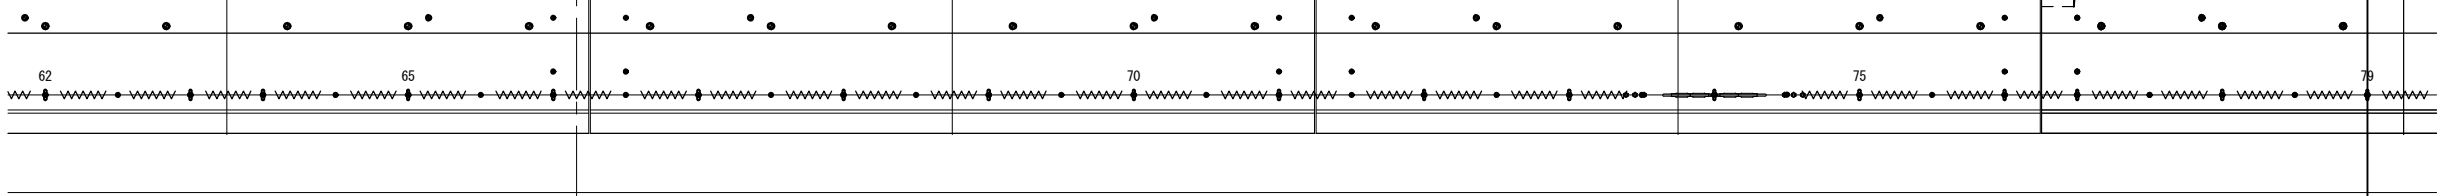


道央自動車道 千歳川大橋(下り線)床版取替工事				
図面の種類	千歳川大橋(下り線) 暫定時転落防止網詳細図(3)			
縮 尺	図 示	図面番号	/	
設計会社名	戸田建設株式会社			
施工会社名	戸田建設株式会社			
事務所名	東日本高速道路株式会社 北海道支社 札幌管理事務所			

千歳川大橋(下り線) P15-P24 暫定時転落防止網詳細図(4)


平面図 S=1:50

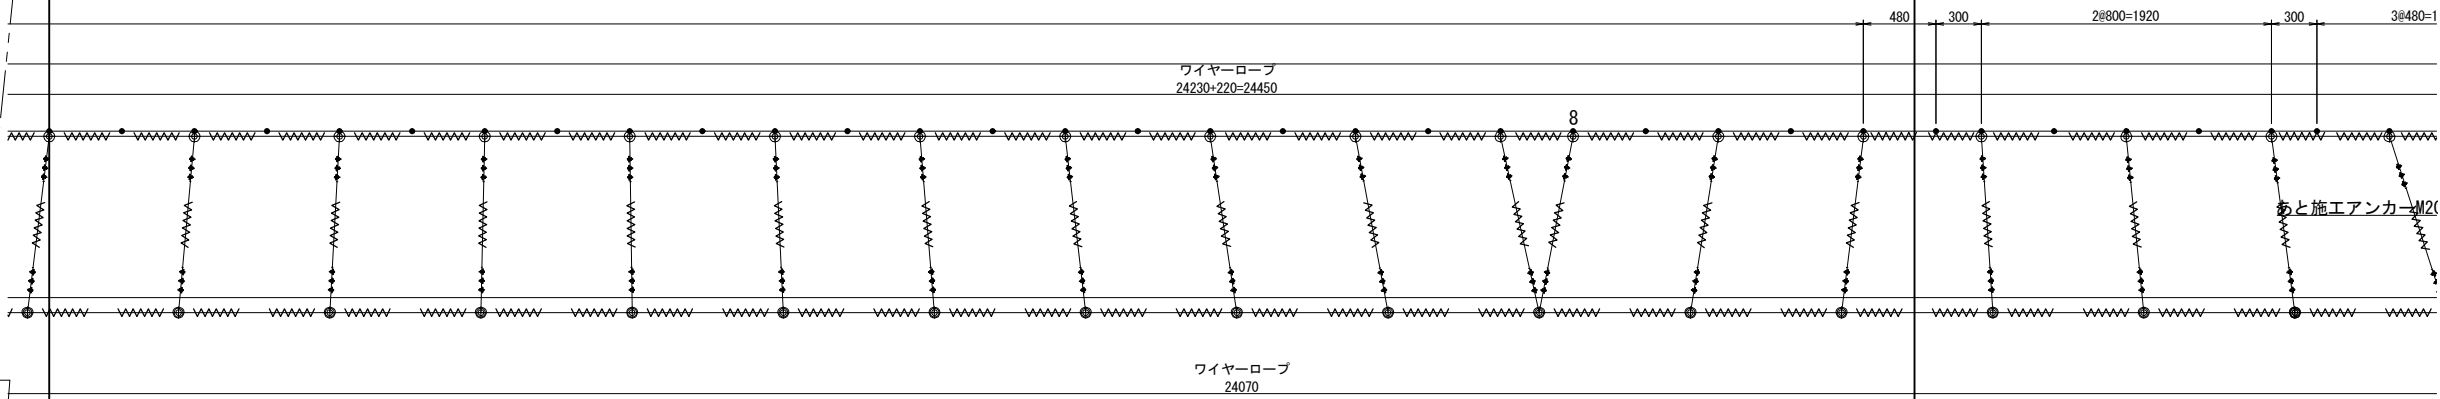


側面図 S=1:50

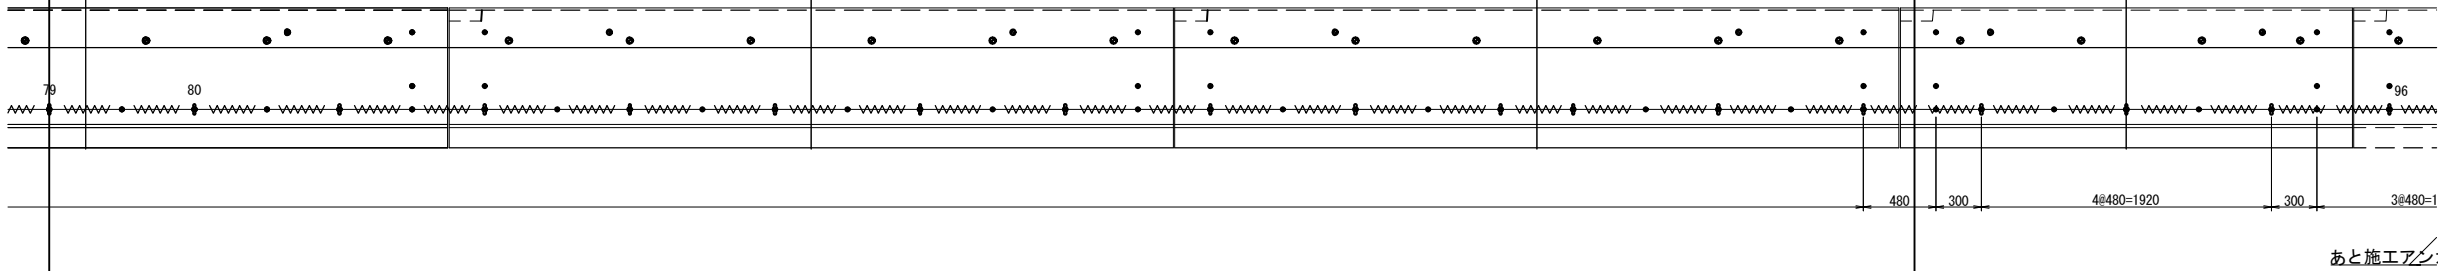

平面図 S=1:50

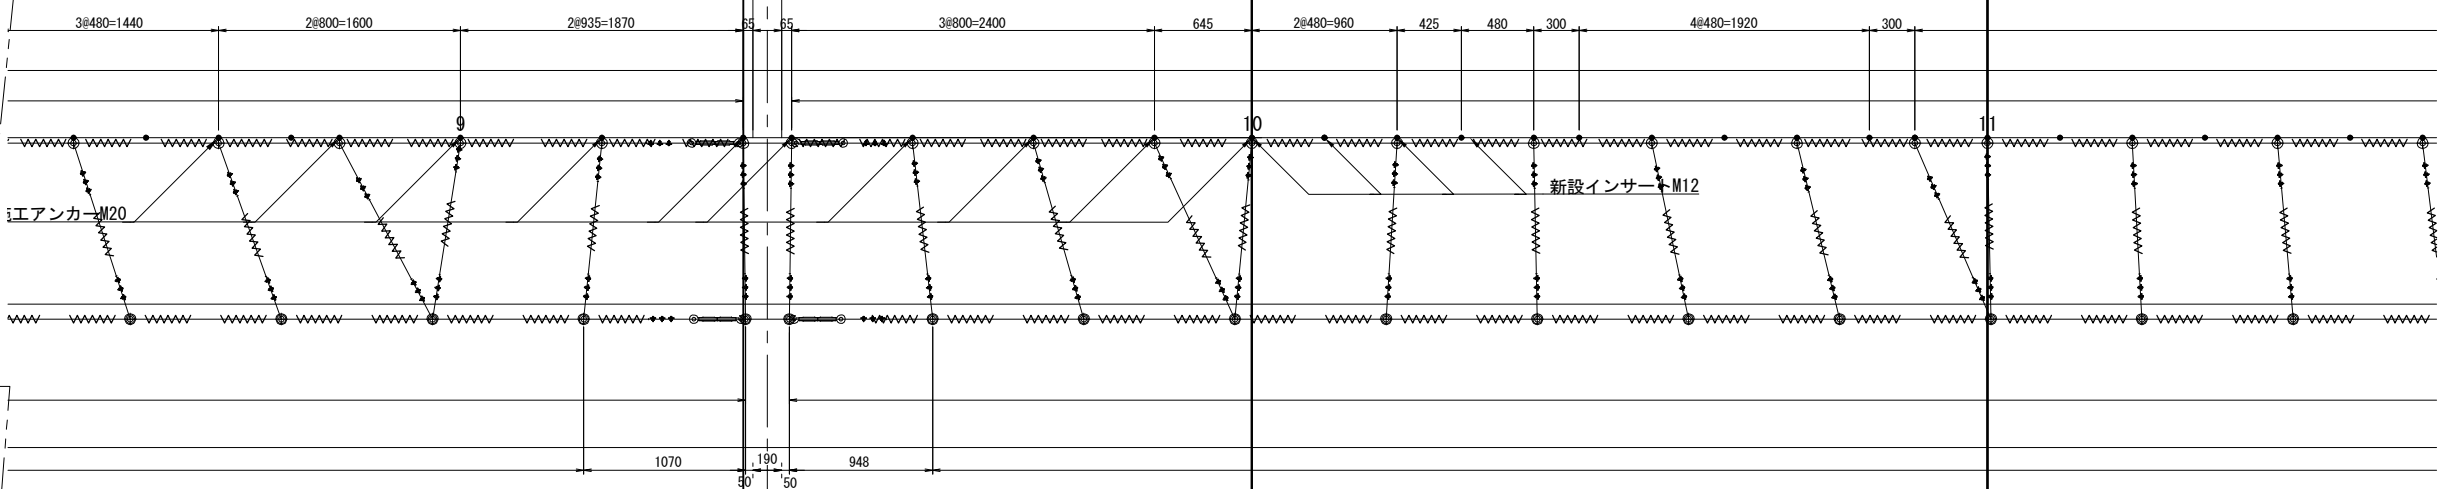


側面図 S=1:50

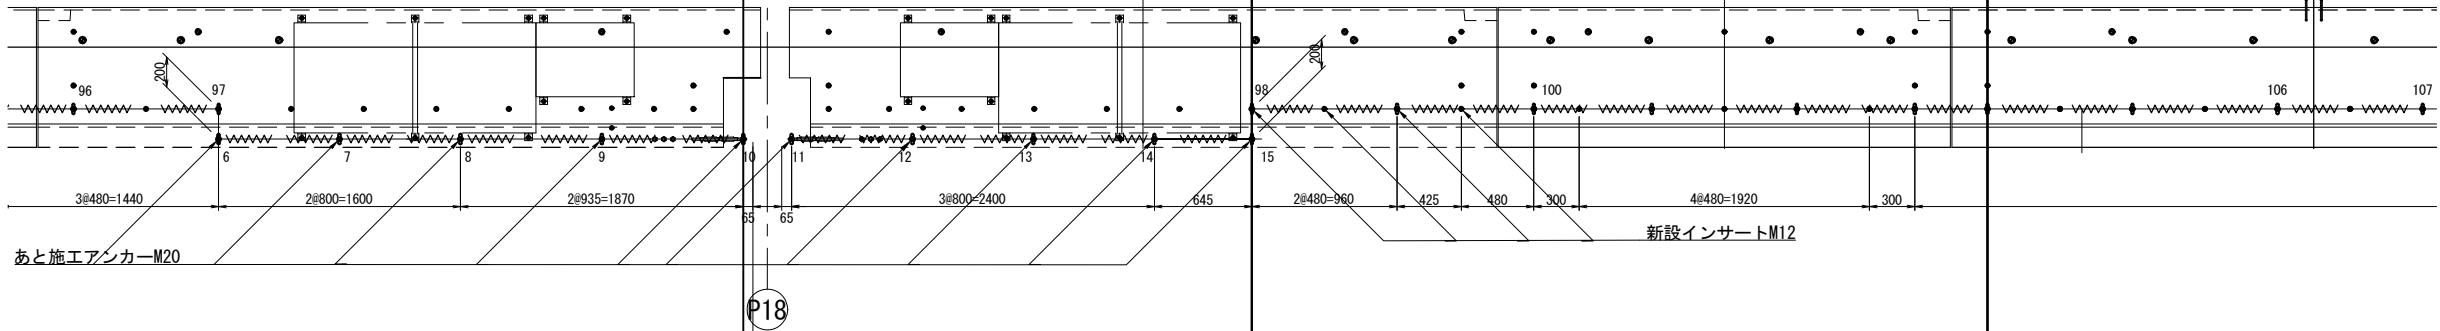


道央自動車道 千歳川大橋(下り線)床版取替工事				
図面の種類	千歳川大橋(下り線) 暫定時転落防止網詳細図(4)			
縮 尺	図 示	図面番号	/	
設計会社名	戸田建設株式会社			
施工会社名	戸田建設株式会社			
事務所名	東日本高速道路株式会社 北海道支社 札幌管理事務所			

千歳川大橋(下り線) P15-P24 暫定時転落防止網詳細図(5)


平面図 S=1:50

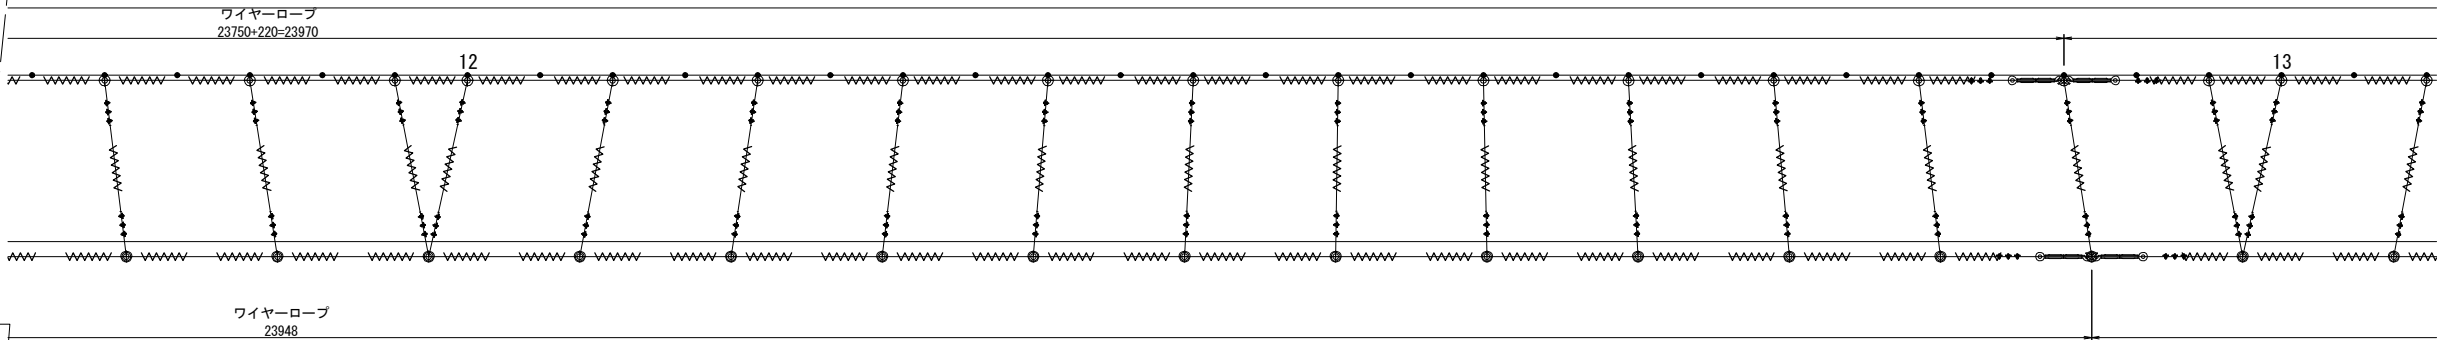


側面図 S=1:50

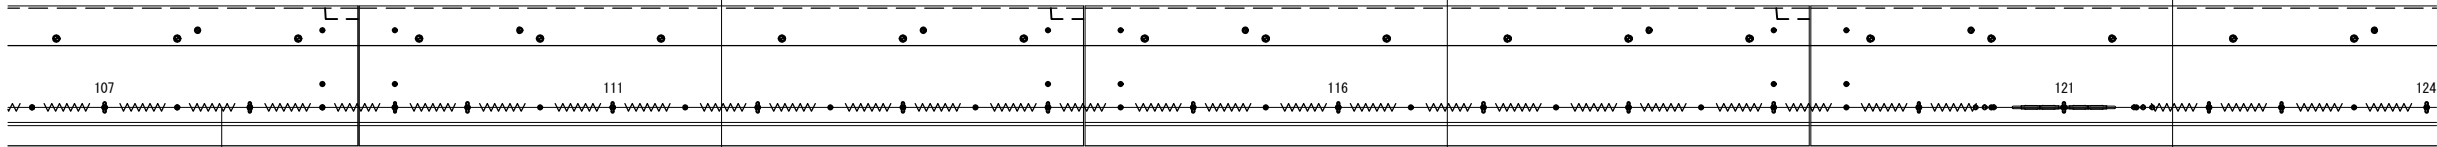

平面図 S=1:50

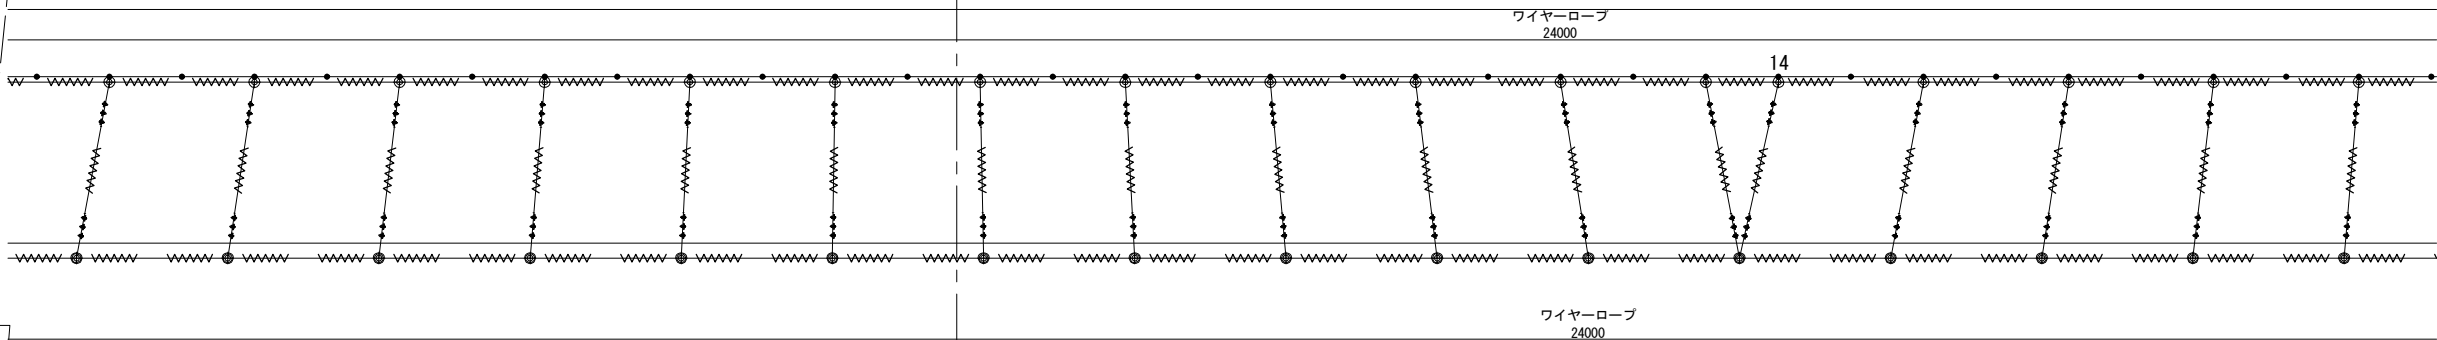

側面図 S=1:50

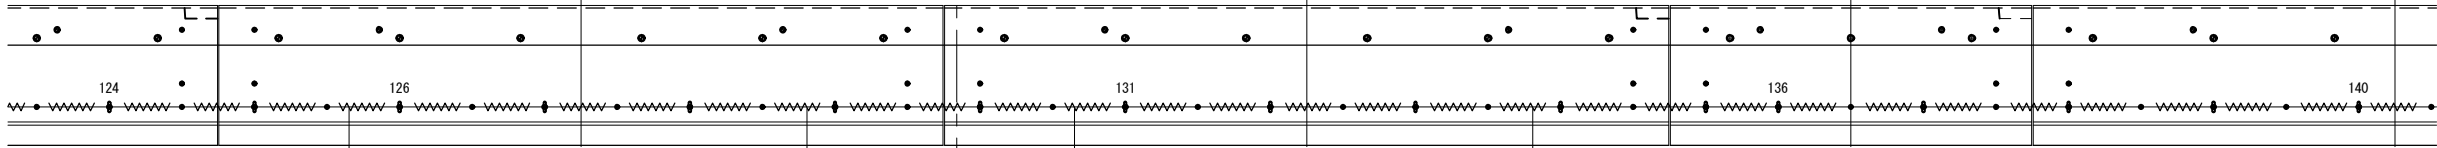

道央自動車道 千歳川大橋（下り線）床版取替工事				
図面の種類	千歳川大橋（下り線） 暫定時転落防止網詳細図(5)			
縮 尺	図 示	図面番号	/	
設計会社名	戸田建設株式会社			
施工会社名	戸田建設株式会社			
事務所名	東日本高速道路株式会社 北海道支社 札幌管理事務所			

千歳川大橋(下り線) P15-P24 暫定時転落防止網詳細図(6)

平面図 S=1:50

ひし形金網 286100×220×4=286980

15

91@1000=91000

側面図 S=1:50

140

141

146

151

156

157

P20

平面図 S=1:50

ワイヤーロープ
24000

16

ワイヤーロープ
24000

側面図 S=1:50

157

161

166

171

173

P20

道央自動車道 千歳川大橋（下り線）床版取替工事				
図面の種類	千歳川大橋（下り線） 暫定時転落防止網詳細図(6)			
縮 尺	図 示	図面番号	/	
設計会社名	戸田建設株式会社			
施工会社名	戸田建設株式会社			
事務所名	東日本高速道路株式会社 北海道支社 札幌管理事務所			

千歳川大橋(下り線) P15-P24 暫定時転落防止網詳細図(7)

平面図 S=1:50

ワイヤーロープ
23520

ワイヤーロープ
23482

側面図 S=1:50

P21 平面図 S=1:50

368#480=176640

50

側面図 S=1:50


368#480=176640

P21


道央自動車道 千歳川大橋(下り線)床版取替工事			
図面の種類	千歳川大橋(下り線) 暫定時転落防止網詳細図(7)		
縮 尺	図 示	図面番号	/
設計会社名	戸田建設株式会社		
施工会社名	戸田建設株式会社		
事務所名	東日本高速道路株式会社 北海道支社 札幌管理事務所		

千歳川大橋(下り線) P15-P24 暫定時転落防止網詳細図(8)


平面図 S=1:50

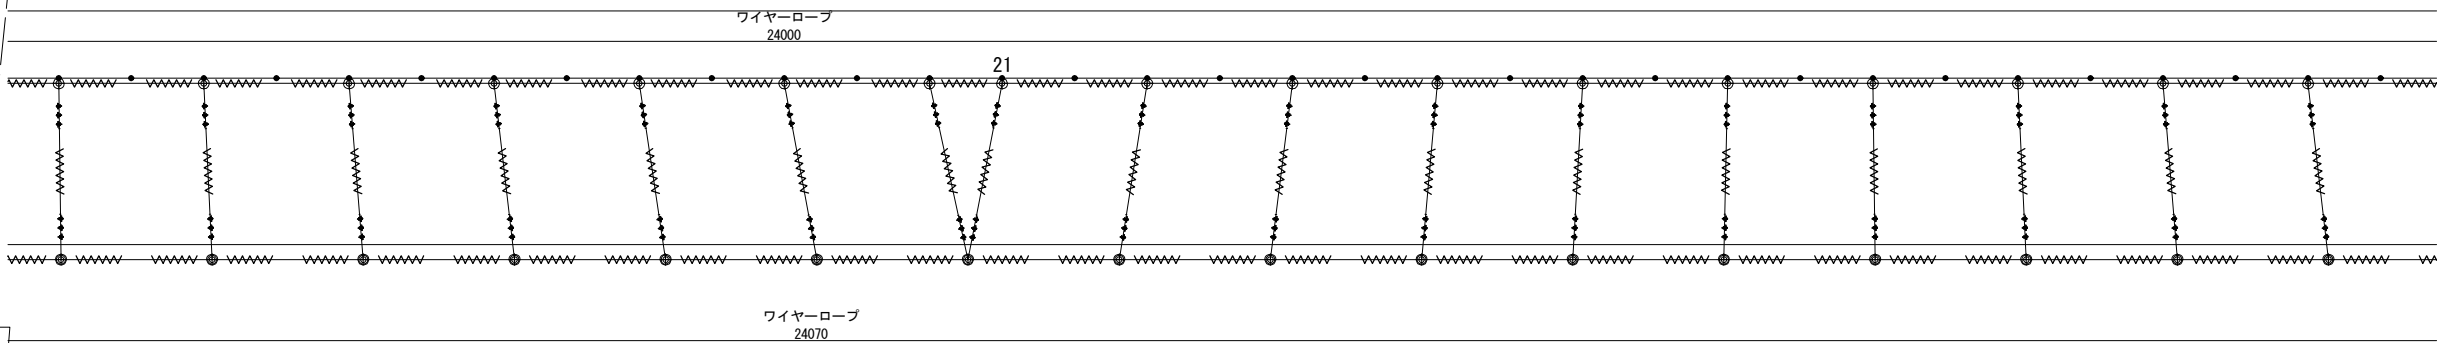


側面図 S=1:50

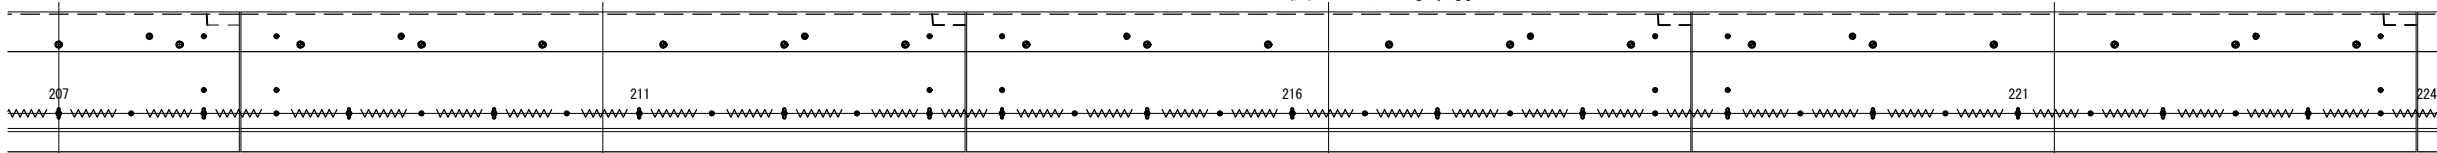

平面図 S=1:50 P22

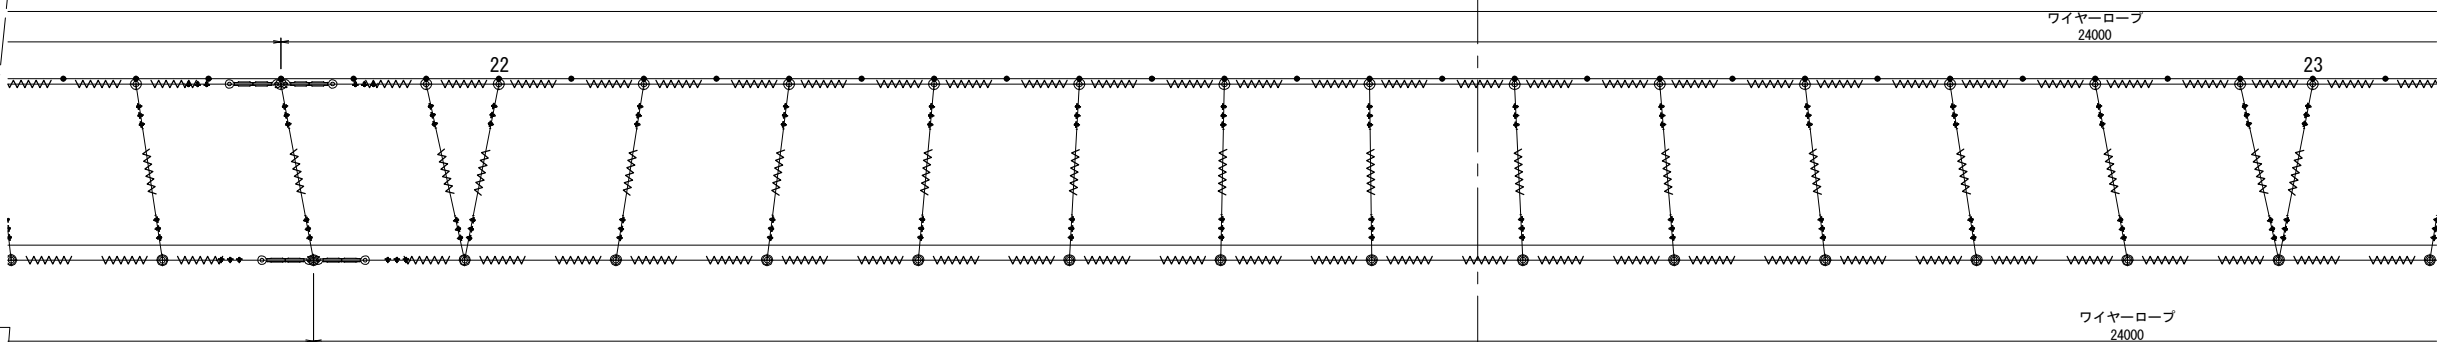


側面図 S=1:50

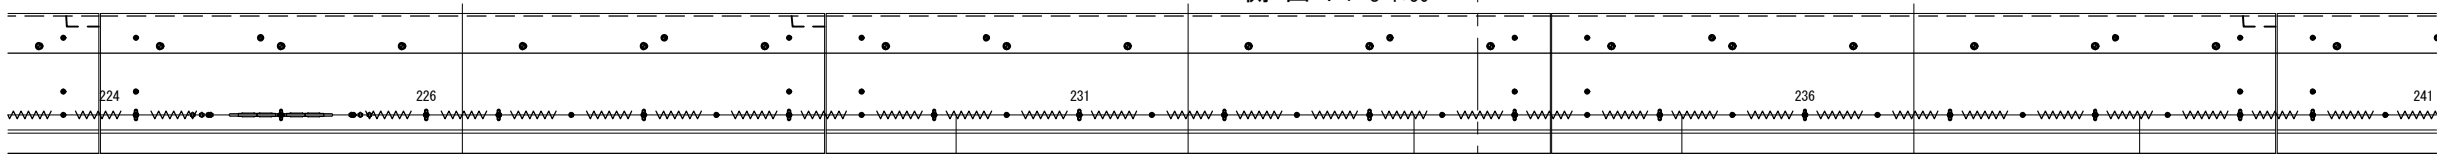


道央自動車道 千歳川大橋(下り線)床版取替工事				
図面の種類	千歳川大橋(下り線) 暫定時転落防止網詳細図(8)			
縮 尺	図 示	図面番号	/	
設計会社名	戸田建設株式会社			
施工会社名	戸田建設株式会社			
事務所名	東日本高速道路株式会社 北海道支社 札幌管理事務所			

千歳川大橋(下り線) P15-P24 暫定時転落防止網詳細図(9)


平面図 S=1:50

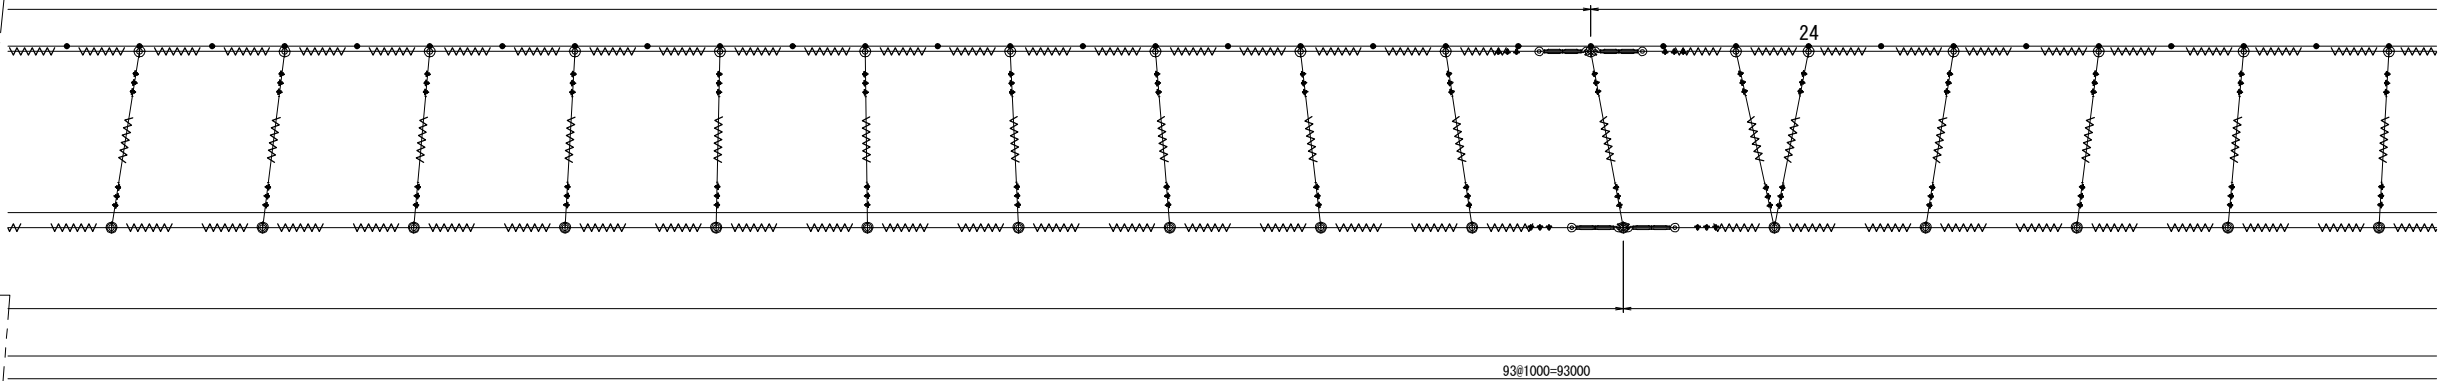


側面図 S=1:50

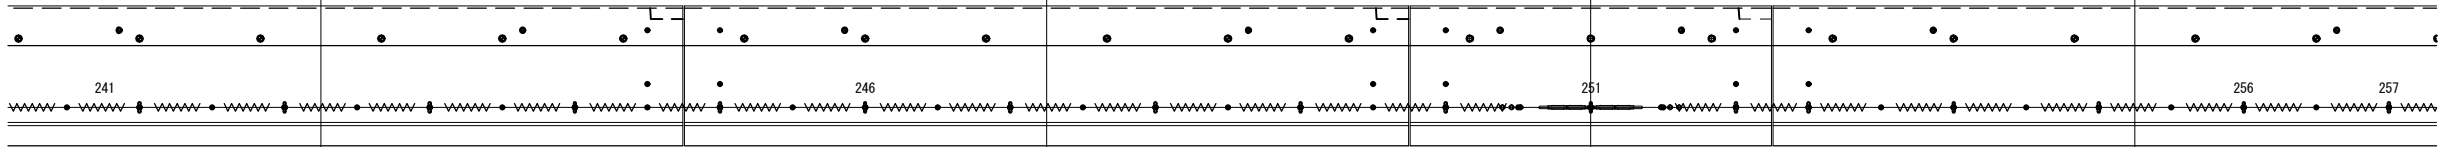

平面図 S=1:50

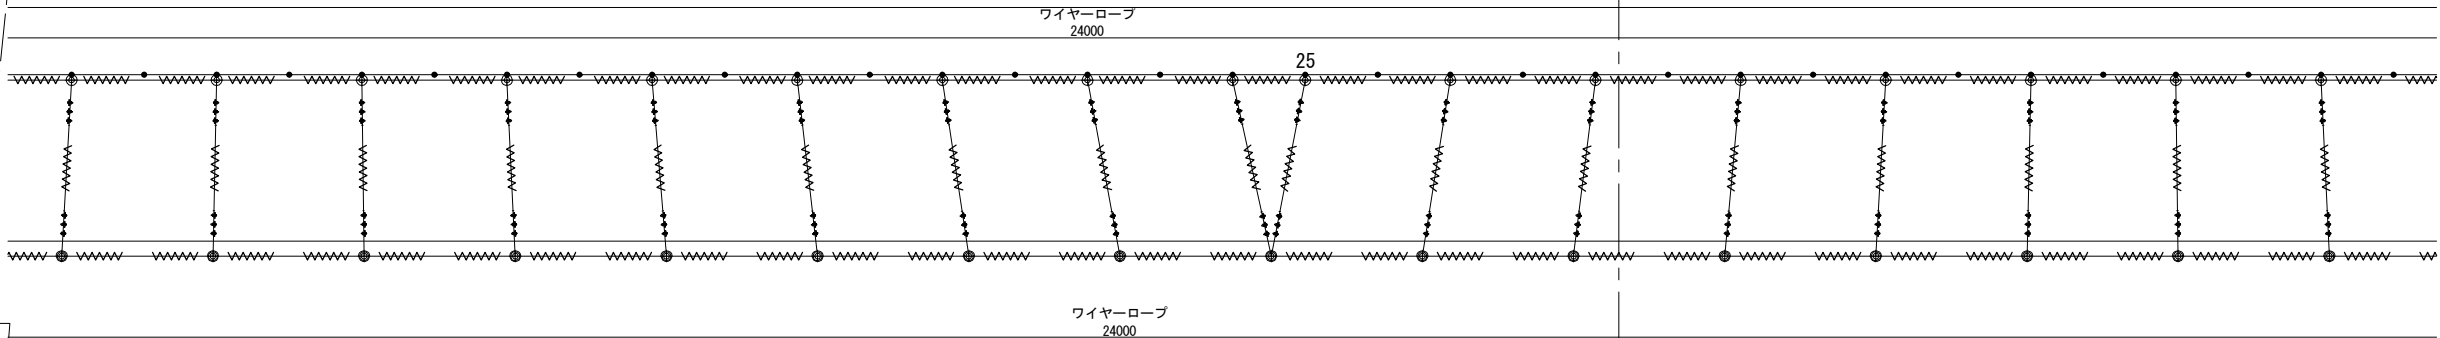


側面図 S=1:50

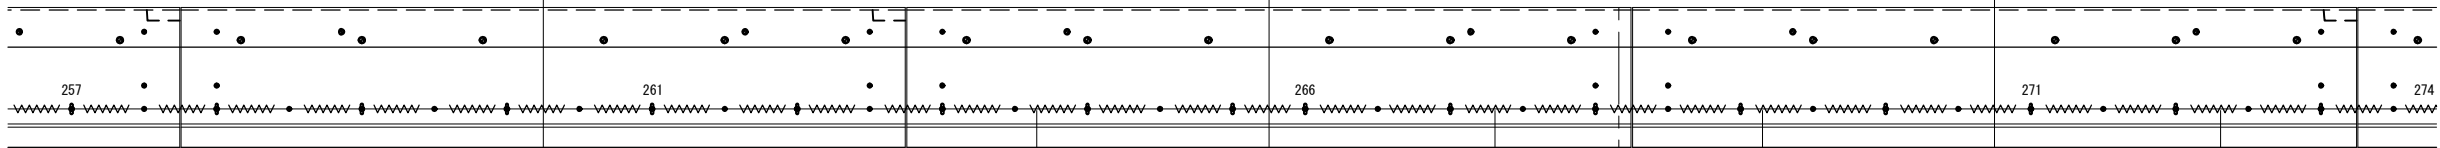


道央自動車道 千歳川大橋(下り線)床版取替工事				
図面の種類	千歳川大橋(下り線) 暫定時転落防止網詳細図(9)			
縮 尺	図 示	図面番号	/	
設計会社名	戸田建設株式会社			
施工会社名	戸田建設株式会社			
事務所名	東日本高速道路株式会社 北海道支社 札幌管理事務所			

千歳川大橋(下り線) P15-P24 暫定時転落防止網詳細図(10)


平面図 S=1:50

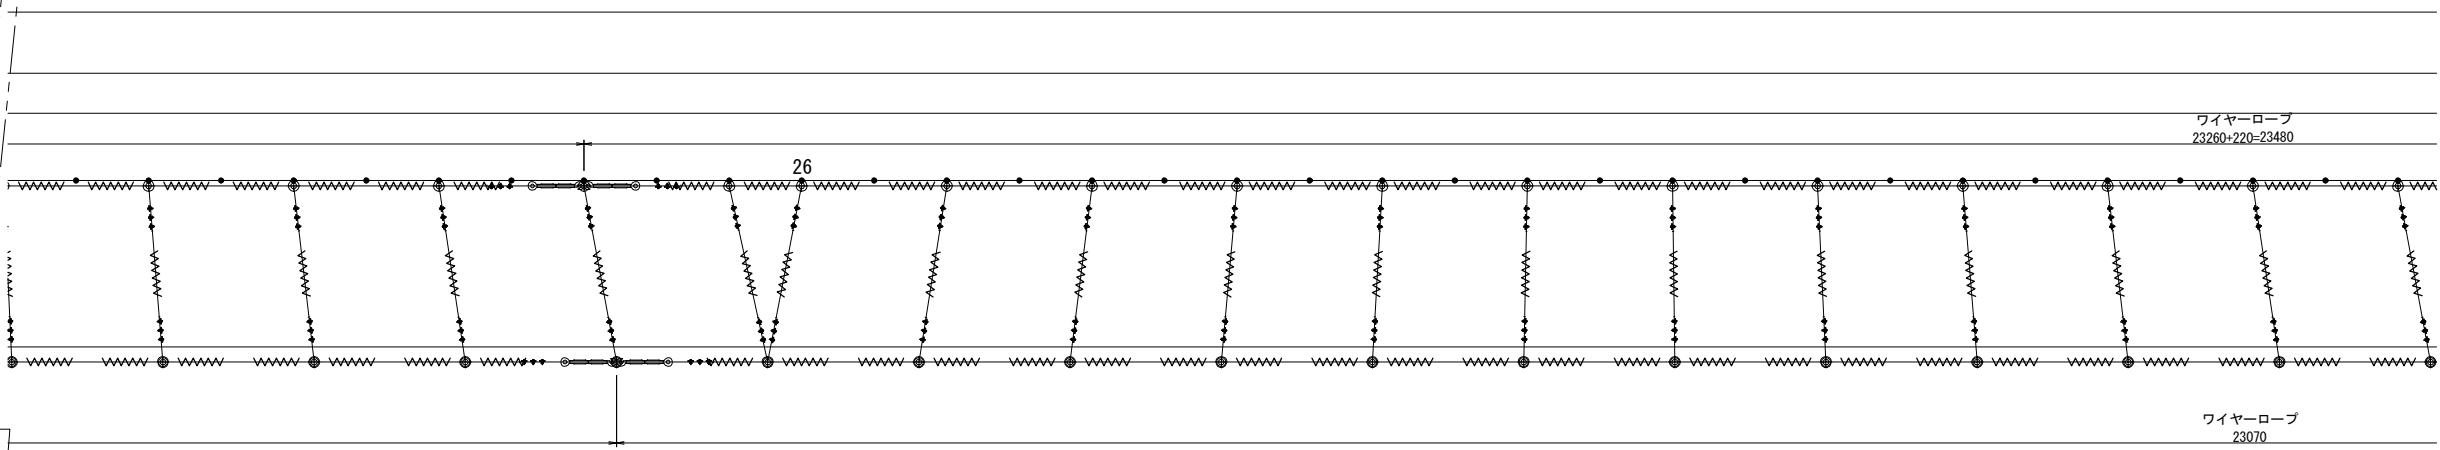


側面図 S=1:50

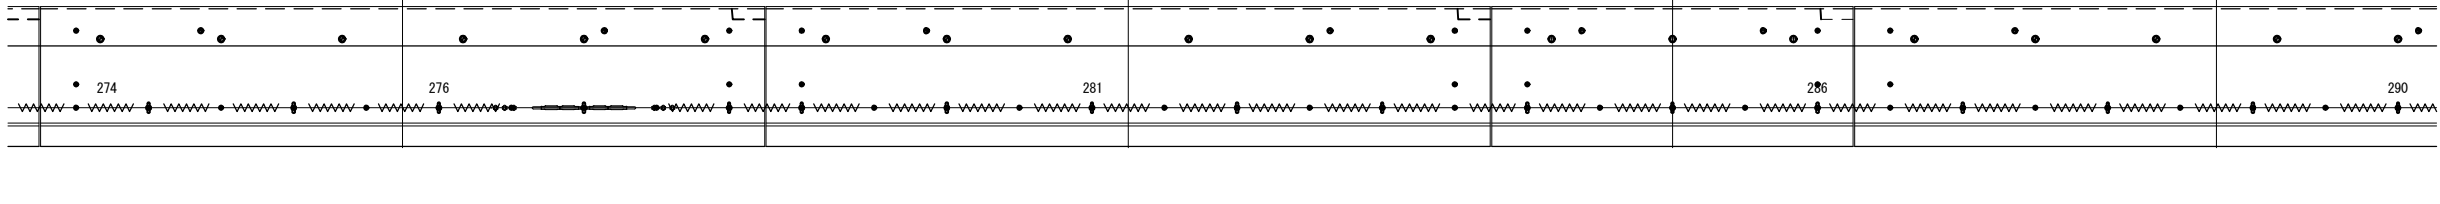

平面図 S=1:50

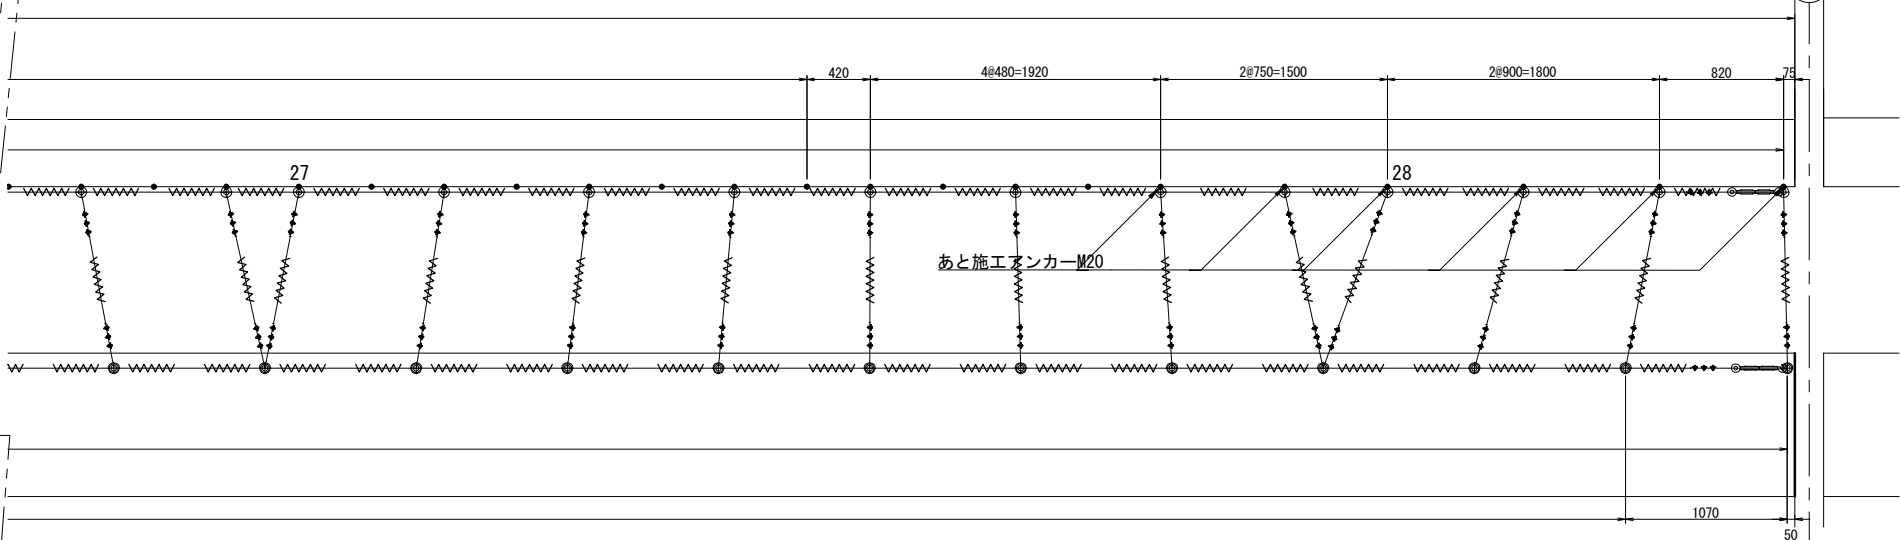


側面図 S=1:50

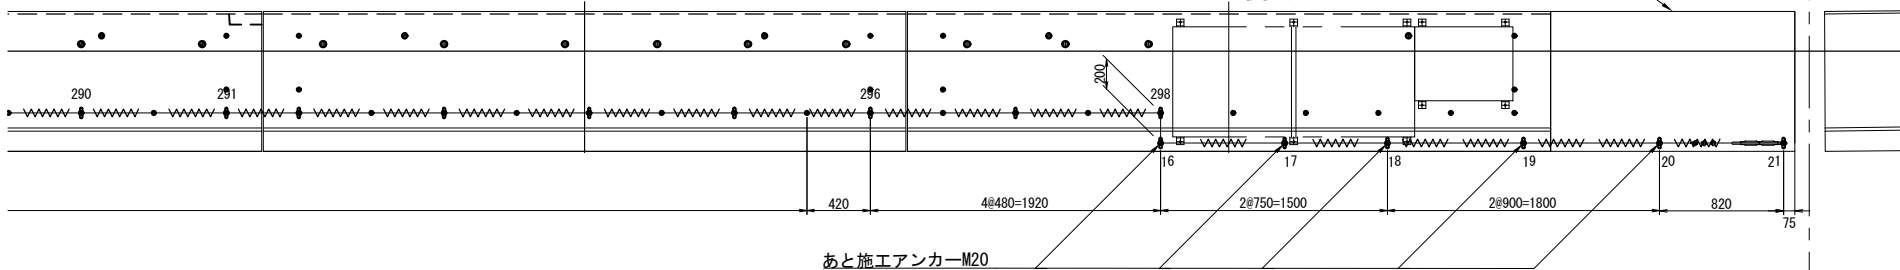


道央自動車道 千歳川大橋（下り線）床版取替工事				
図面の種類	千歳川大橋（下り線） 暫定時転落防止網詳細図（10）			
縮 尺	図 示	図面番号	/	
設計会社名	戸田建設株式会社			
施工会社名	戸田建設株式会社			
事務所名	東日本高速道路株式会社 北海道支社 札幌管理事務所			

千歳川大橋(下り線) P15-P24 転落防止網詳細図(1)

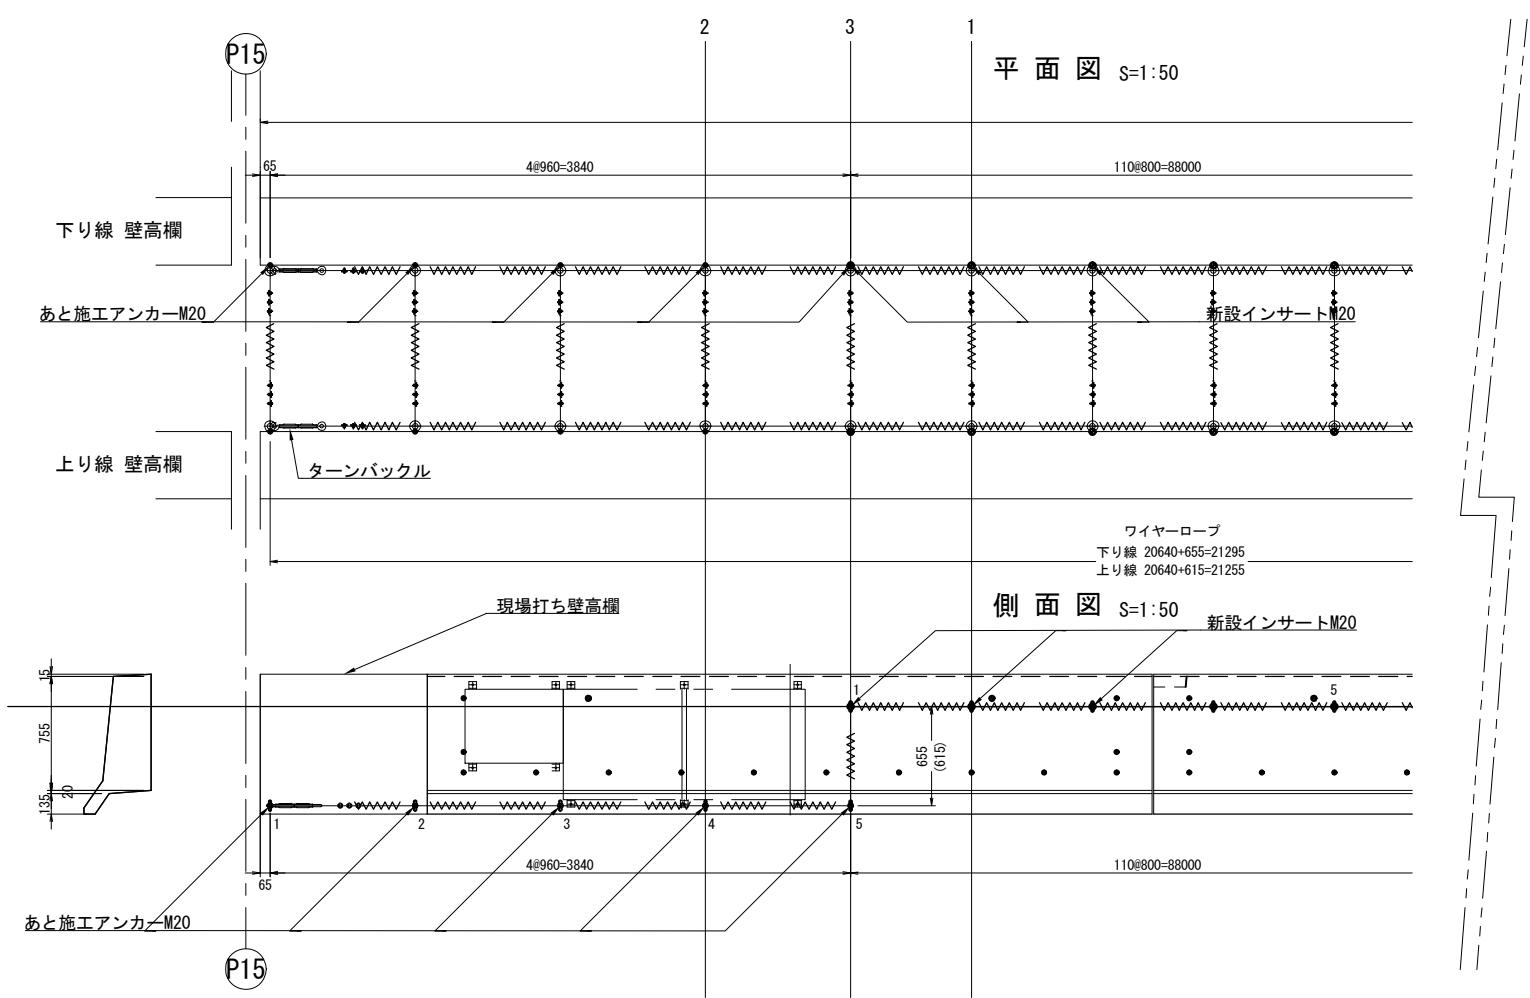

金網およびワイヤーロープ取付詳細図 S=1:10

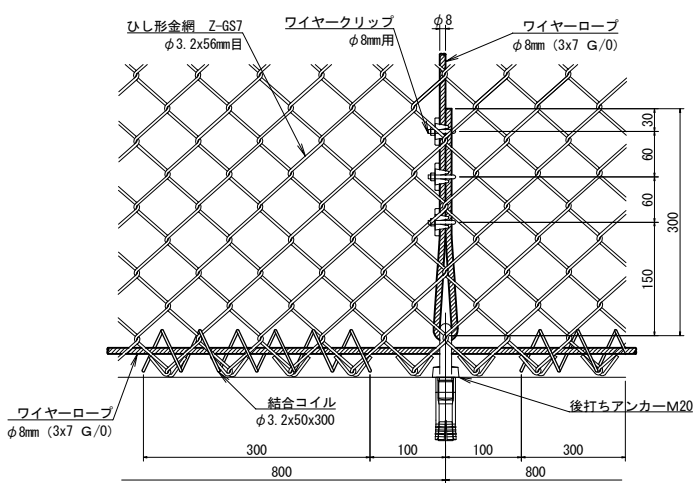

■ 部材リスト・数量表

部 材 名	規 格	単 位	員 数	表 面 処 理
ひし形金網	φ3.2x56mm目 (JIS G 3552 Z-GS7)	m ²	320.5	亜鉛めっき付着量 380g/m ² 以上
ワイヤーロープ	φ8mm (3x7 G/O)	m	1193.4	素線の亜鉛めっき付着量JIS G3525 G種
結合コイル	φ3.2x50x300 (亜鉛めっき鋼線製)	本	1743	亜鉛めっき付着量 400g/m ² 以上
ワイヤークリップ	φ8mm用	個	2322	亜鉛めっき品 (ドブ)
パイプ式ターンバックル	W5/8	本	48	亜鉛めっき品 (ドブ)
あと施工アンカー (後打ちアンカー)	アイボルト M20 + グリッパンアンカー M20	本	42	亜鉛めっき品 (ドブ)
インサートアンカー (先埋めアンカー)	セラミックインサートM20 + アイナットM20 + 3種ナットM20 + 寸切ボルトM20x85	個	684	壁高欄埋込 SUS品

【 P15~P24径間 】

● 数量計算表

部 材 名	計 算 式	単 位	員 数
ひし形金網	288.72 × 1.11	m ²	320.5
ワイヤーロープ	橋軸方向	m	1193.4
	下り線 21.90 + 25.40 × 2 + 26.13 × 2 + 25.40 × 6 + 18.12 = 295.48		
	上り線 21.86 + 25.40 × 2 + 26.09 × 2 + 25.40 × 6 + 18.08 = 295.32		
	橋軸直角方向 1.66 × (342 + 21) = 602.58		

【 P15~P24径間 】

道央自動車道 千歳川大橋(下り線)床版取替工事			
図面の種類	千歳川大橋(下り線) 転落防止網詳細図(1)		
縮 尺	図 示	図面番号	/
設計会社名	戸田建設株式会社		
施工会社名	戸田建設株式会社		
事務所名	東日本高速道路株式会社 北海道支社 札幌管理事務所		

千歳川大橋(下り線) P15-P24 転落防止網詳細図(2)

P18

平面図 S=1:50

ひし形金網 286100+655×4=288720

3#800=1600

2#835=1670

65

65

870

3#800=2400

224#800=179200

あと施工アンカーM20

新設インサートM20

ワイヤーロープ
下り線 24870+655=25525
上り線 24870+615=25485

ワイヤーロープ
下り線 24870+655=25525
上り線 24870+615=25485

側面図 S=1:50

800

650

650

650

650

110

111

655

(615)

6

7

8

9

10

11

12

13

14

15

112

120

2#800=670

2#800=2400

65

65

3#800=2400

670

224#800=179200

あと施工アンカーM20

新設インサートM20

P18

P24

610

600

650

800

650

550

4#800=3200

1000

75

あと施工アンカーM20

ワイヤーロープ
下り線 16860+655=17515
上り線 16860+615=17475

現場打ち壁高欄

ワイヤーロープ 6#24800=148800

140

340

342

655

(615)

16

17

18

19

20

21

610

600

650

800

650

550

4#800=3200

1000

75

あと施工アンカーM20


P24

道央自動車道 千歳川大橋（下り線）床版取替工事				
図面の種類	千歳川大橋（下り線） 転落防止網詳細図（2）			
縮 尺	図 示	図面番号	/	
設計会社名	戸田建設株式会社			
施工会社名	戸田建設株式会社			
事務所名	東日本高速道路株式会社 北海道支社 札幌管理事務所			


千歳川大橋（下り線）P15-P24 視線誘導標詳細図

視線誘導標設置図 S=1:10

[標準型]

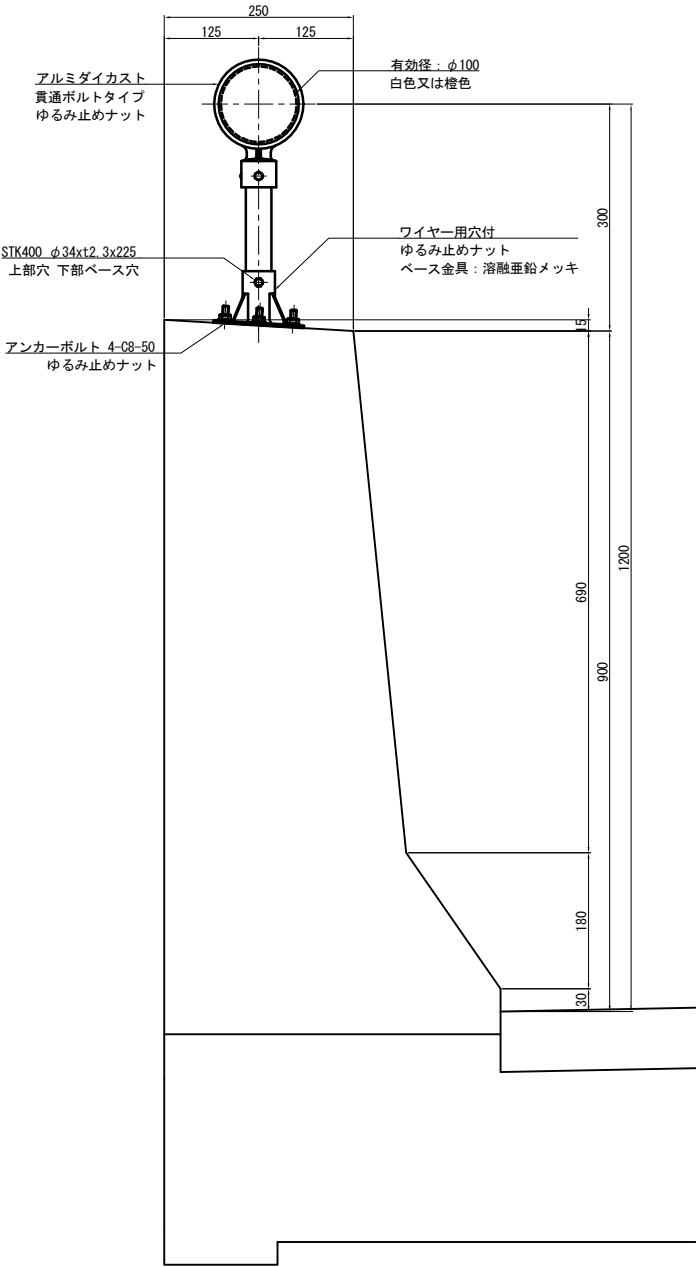


上面図 S=1:3

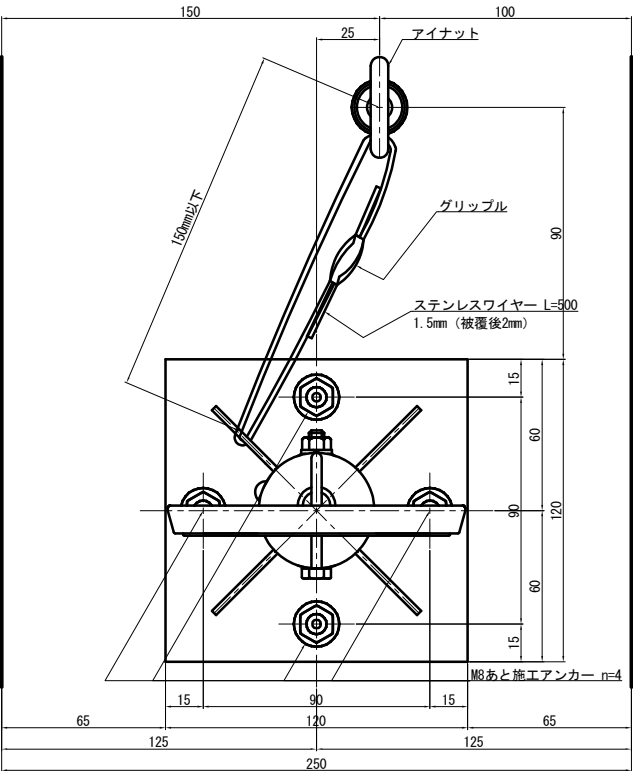


支柱詳細図 S=1:3


[標準型]

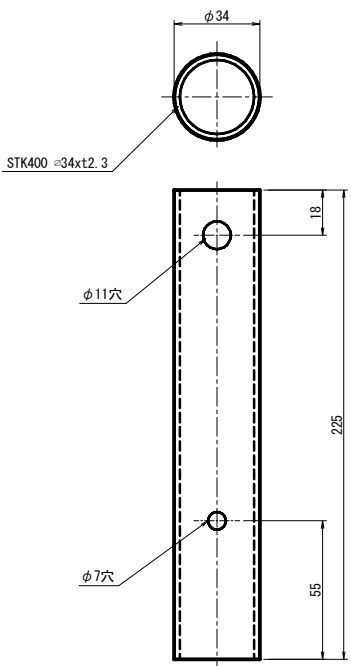


アイナット部詳細図 S=1:2

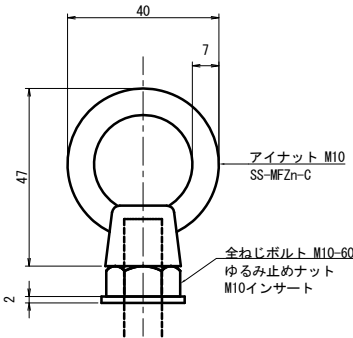

ワイヤー用穴部 S=1:2

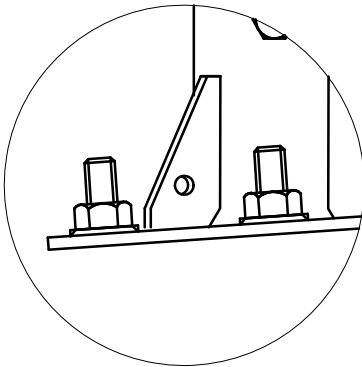

グリップル詳細図 S=1:2

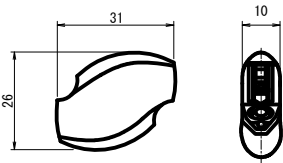

数量表

項目	単位	中分側	路肩側	計	備考
視線誘導標 【標準型】	箇所	0	5	5	



道央自動車道 千歳川大橋（下り線）床版取替工事			
図面の種類	千歳川大橋（下り線）P15-P24 視線誘導標詳細図		
縮尺	図示	図面番号	/
設計会社名	戸田建設株式会社		
施工会社名	戸田建設株式会社		
事務所名	東日本高速道路株式会社 北海道支社 札幌管理事務所		

千歳川大橋（下り線）P15-P24 標識サポート詳細図



[新設壁高欄設置タイプ]

可動アーム詳細図 S=1:8


可動アーム上部

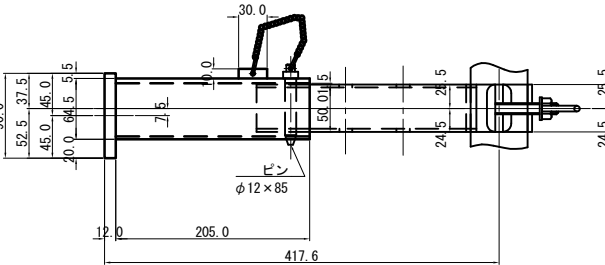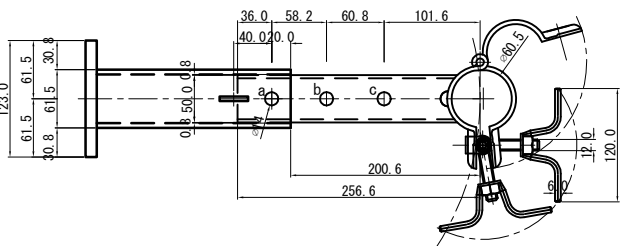

可動アーム下部

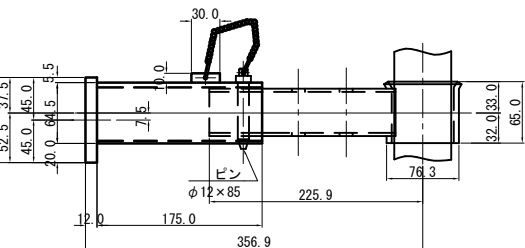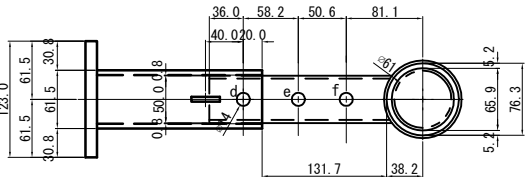

取付ベース詳細図 S=1:3

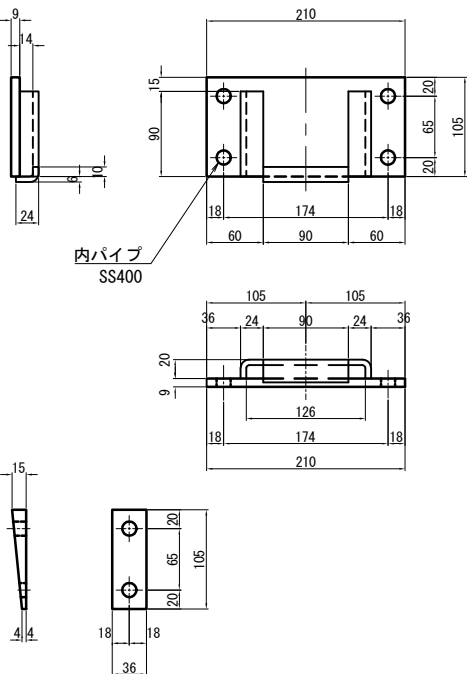

数 量 表

使用材料規格	上 部		下 部	
	数量	合計重量 (kg)	数量	合計重量 (kg)
PL-90x12x123 (AL)	1	0.37		
PL-191x5x205 (AL)	1	0.55		
PL-52x5x205 (AL)	1	0.15		
PL-10x5x30 (AL)	1	0.01	1	0.01
-50x50x3.2x233-	1	1.05		
PL-50x4.5x179	1	0.32		
デンデンボルト (SUS)	1	0.06		
ハンドル付ナット (SUS)	1	0.06		
RB-φ10x54 (SUS)	1	0.18		
B.N M8x30 (SUS)	1	0.02		
割ピンφ2.5 18L (SUS)	1	0.01		
ピン12x85 (SUS)	1	0.08	1	0.8
チェーン (SUS)	1	0.01	1	0.01
PL-90x12x123 (AL)			1	0.37
PL-191x5x175 (AL)			1	0.47
PL-52x5x175 (AL)			1	0.13
-50x50x3.2x198			1	0.89
Pipe φ76.3x5.2x65			1	0.60
小 計		2.87		2.56
合 計				5.43

材料表


製品名	使用材料規格	数量	合計重量 (kg)
側面取付ベース	PL-9x105x210	2	3.176
	PL-6x35x90	4	0.592
	PL-6x3x90	2	0.280
テーパー座金	PL-15x36x105 (AL)	4	0.360

取付材料



カットアンカー	#12CA (HDZT49)	8
B.W. SW	M12x35 (HDZT49)	4
B.W. SW	M12x40 (HDZT49)	4

* 上記に記載なき主要部材はJIS G 3101 (SS400) とする。
* 製品表面処理は溶融亜鉛めっきJIS H 8641 (HDZT77) とする。

断面図 S=1:8

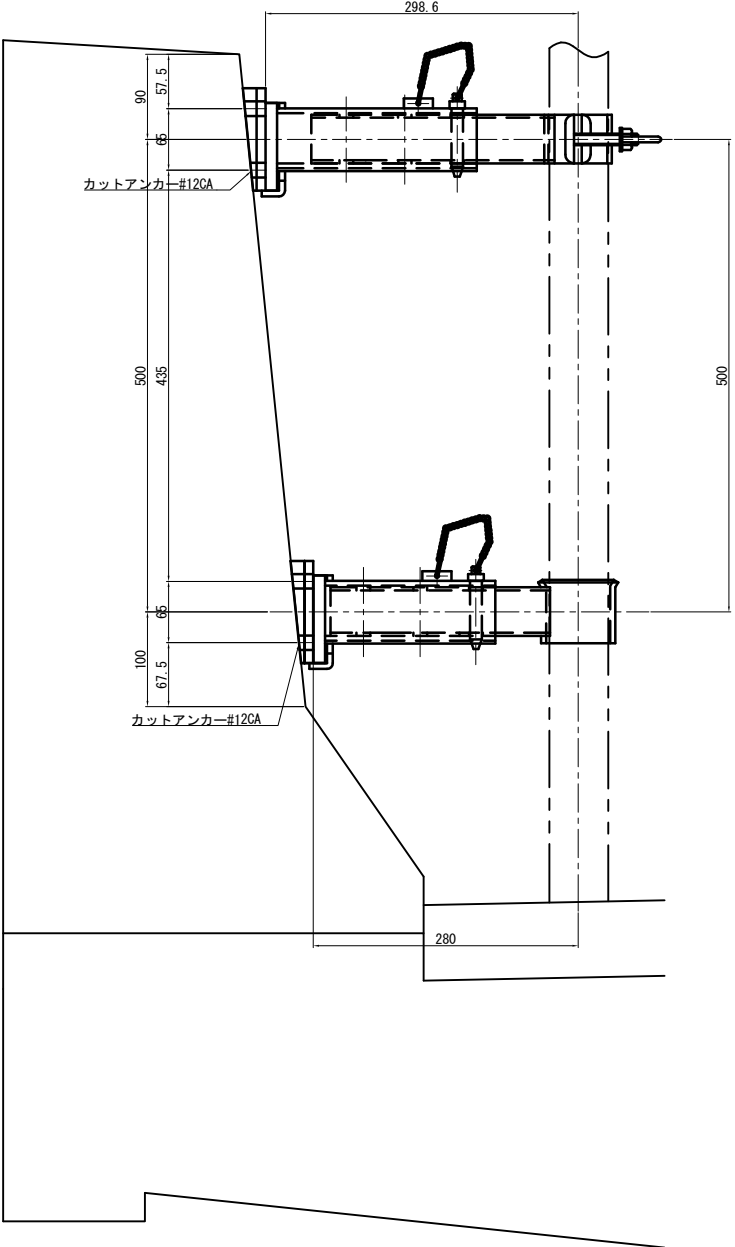



全体位置図 S=1:500

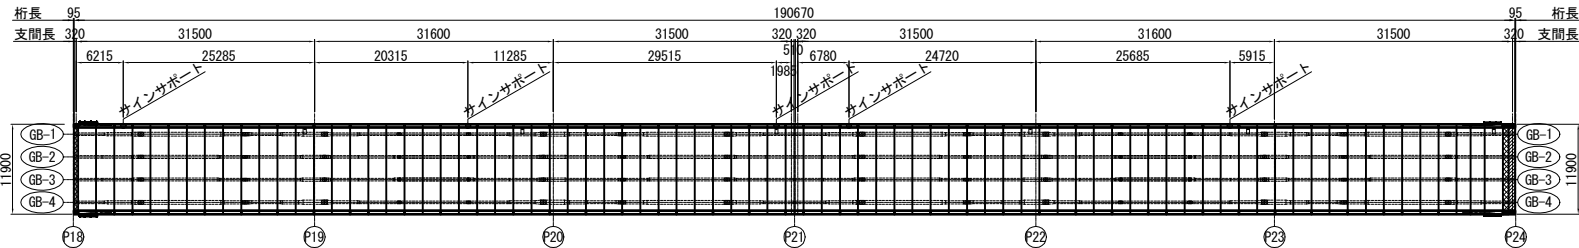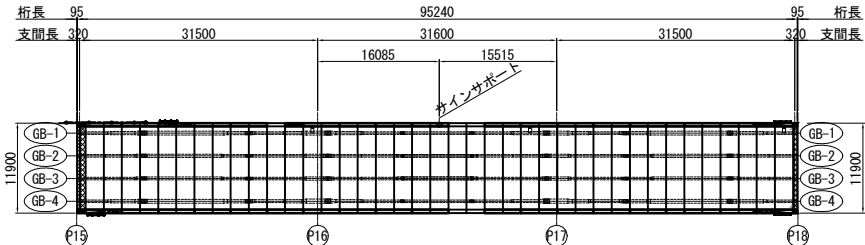


道央自動車道 千歳川大橋（下り線）床版取替工事			
図面の種類	千歳川大橋（下り線）P15-P24 標識サポート詳細図		
縮 尺	図 示	図面番号	/
設計会社名	戸田建設株式会社		
施工会社名	戸田建設株式会社		
事務所名	東日本高速道路株式会社 北海道支社 札幌管理事務所		

千歳川大橋（下り線）P15-P24 路面標示工詳細図

平面図 S=1:500

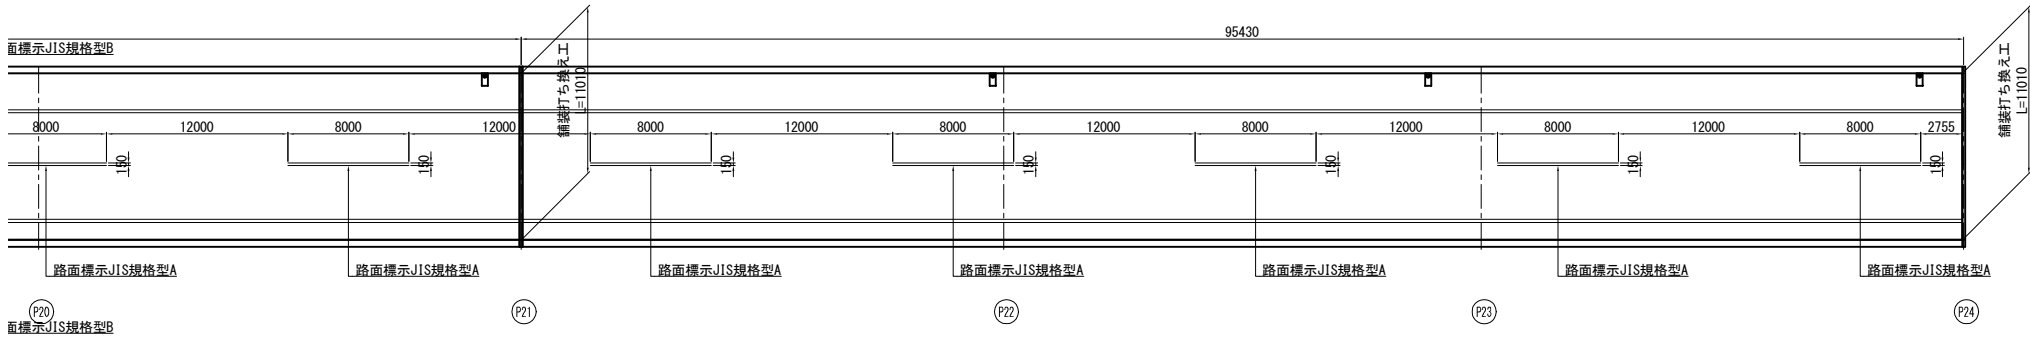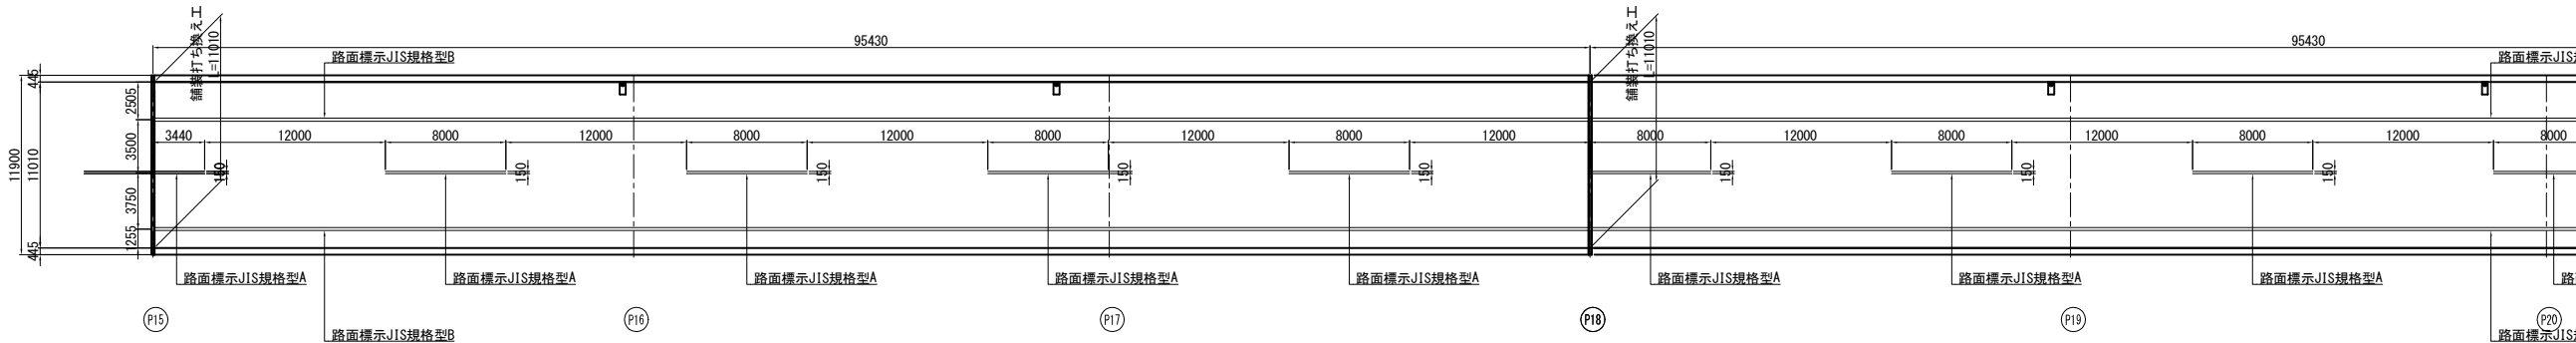

路面標示工断面図 S=1:100

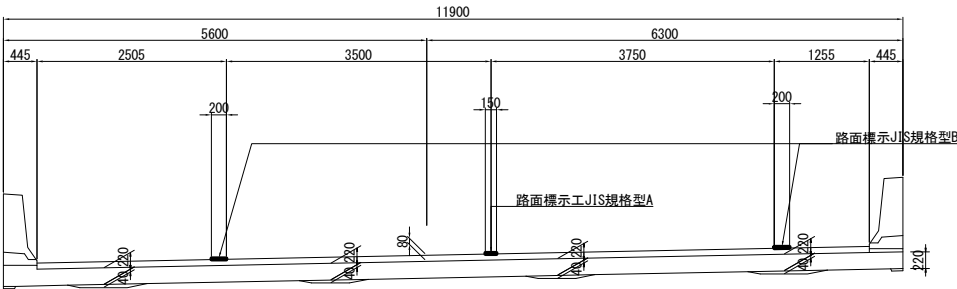


路面標示工 数量表

	単位	下り線			合計
		P15-18	P18-21	P21-24	
JIS規格型A1 (Y)	m	35.4	40.0	40.0	115.4
JIS規格型B1 (Y)	m	190.9	190.9	190.9	572.6

道央自動車道 千歳川大橋（下り線）床版取替工事			
図面の種類	千歳川大橋（下り線） P15-P24 路面標示工詳細図		
縮 尺	図 示	図面番号	/
設計会社名	戸田建設株式会社		
施工会社名	戸田建設株式会社		
事務所名	東日本高速道路株式会社 北海道支社 北広島管理事務所		


千歳川大橋（下り線）P15-P24 通信管路工詳細図（1） S=1:20

側面図
P15路肩側

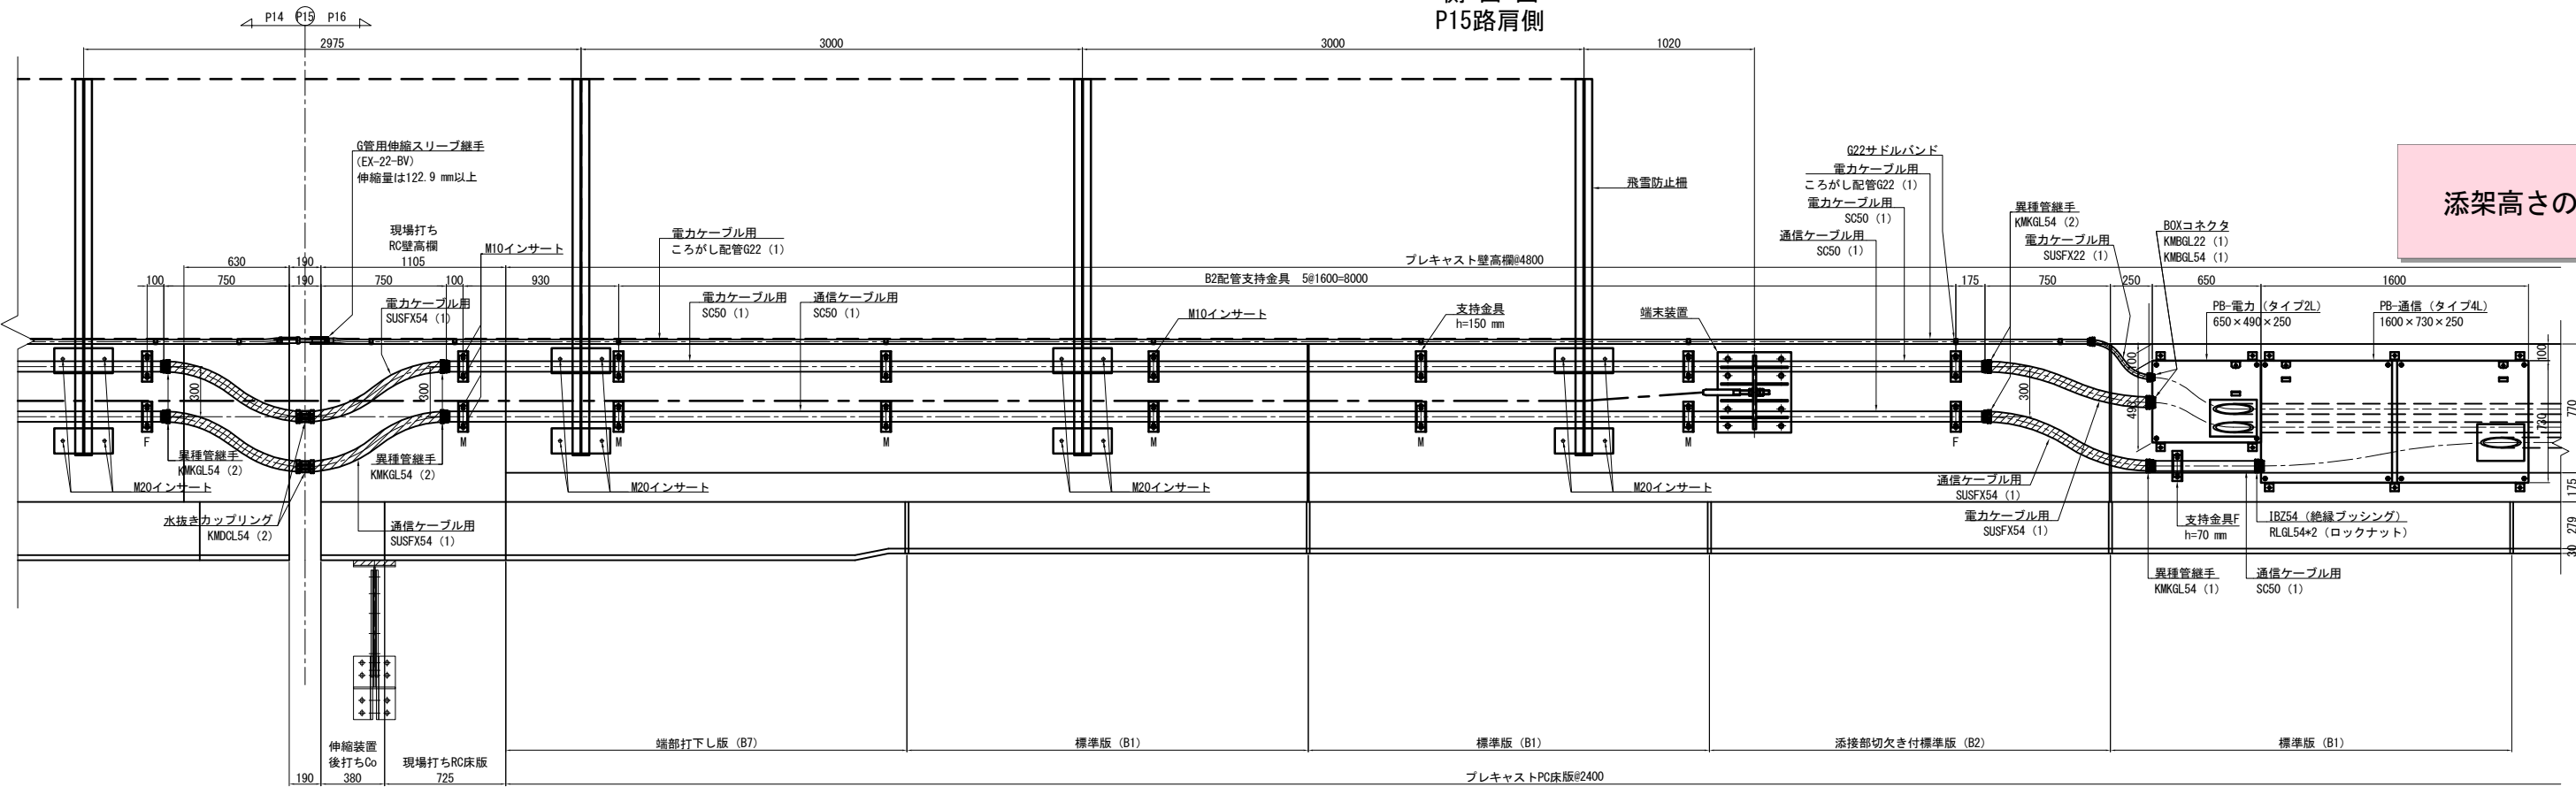

添架高さの変更


平面図

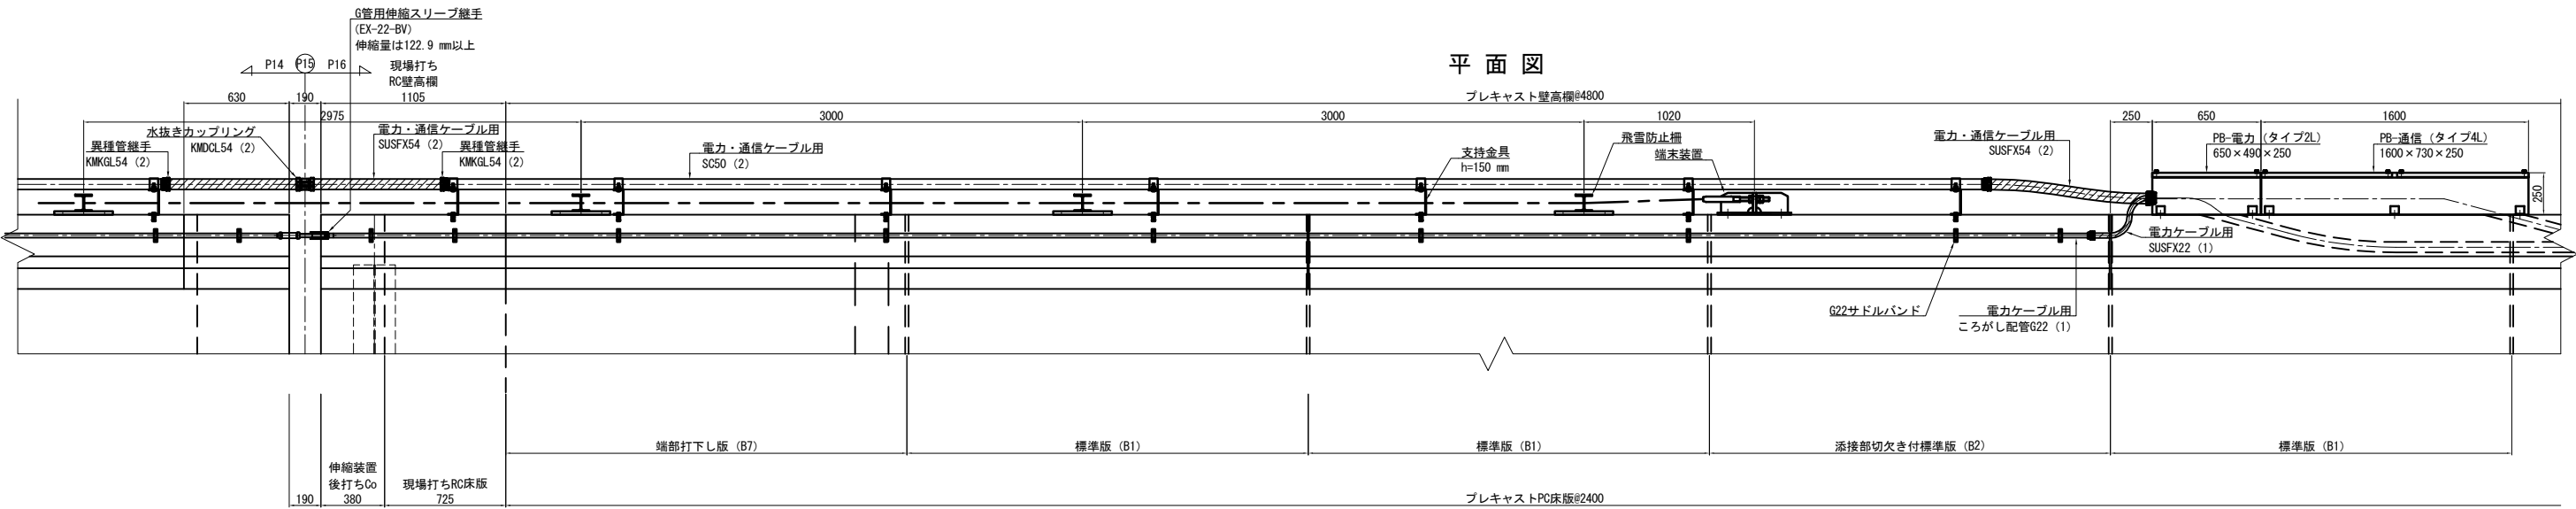


道央自動車道 千歳川大橋（下り線）床版取替工事			
図面の種類	千歳川大橋（下り線）P15-P24 通信管路工詳細図（1）		
縮 尺	図 示	図面番号	/
設計会社名	戸田建設株式会社		
施工会社名	戸田建設株式会社		
事務所名	東日本高速道路株式会社 北海道支社 札幌管理事務所		

千歳川大橋（下り線）P15-P24 通信管路工詳細図（2） S=1:20

側面図
P15中分側

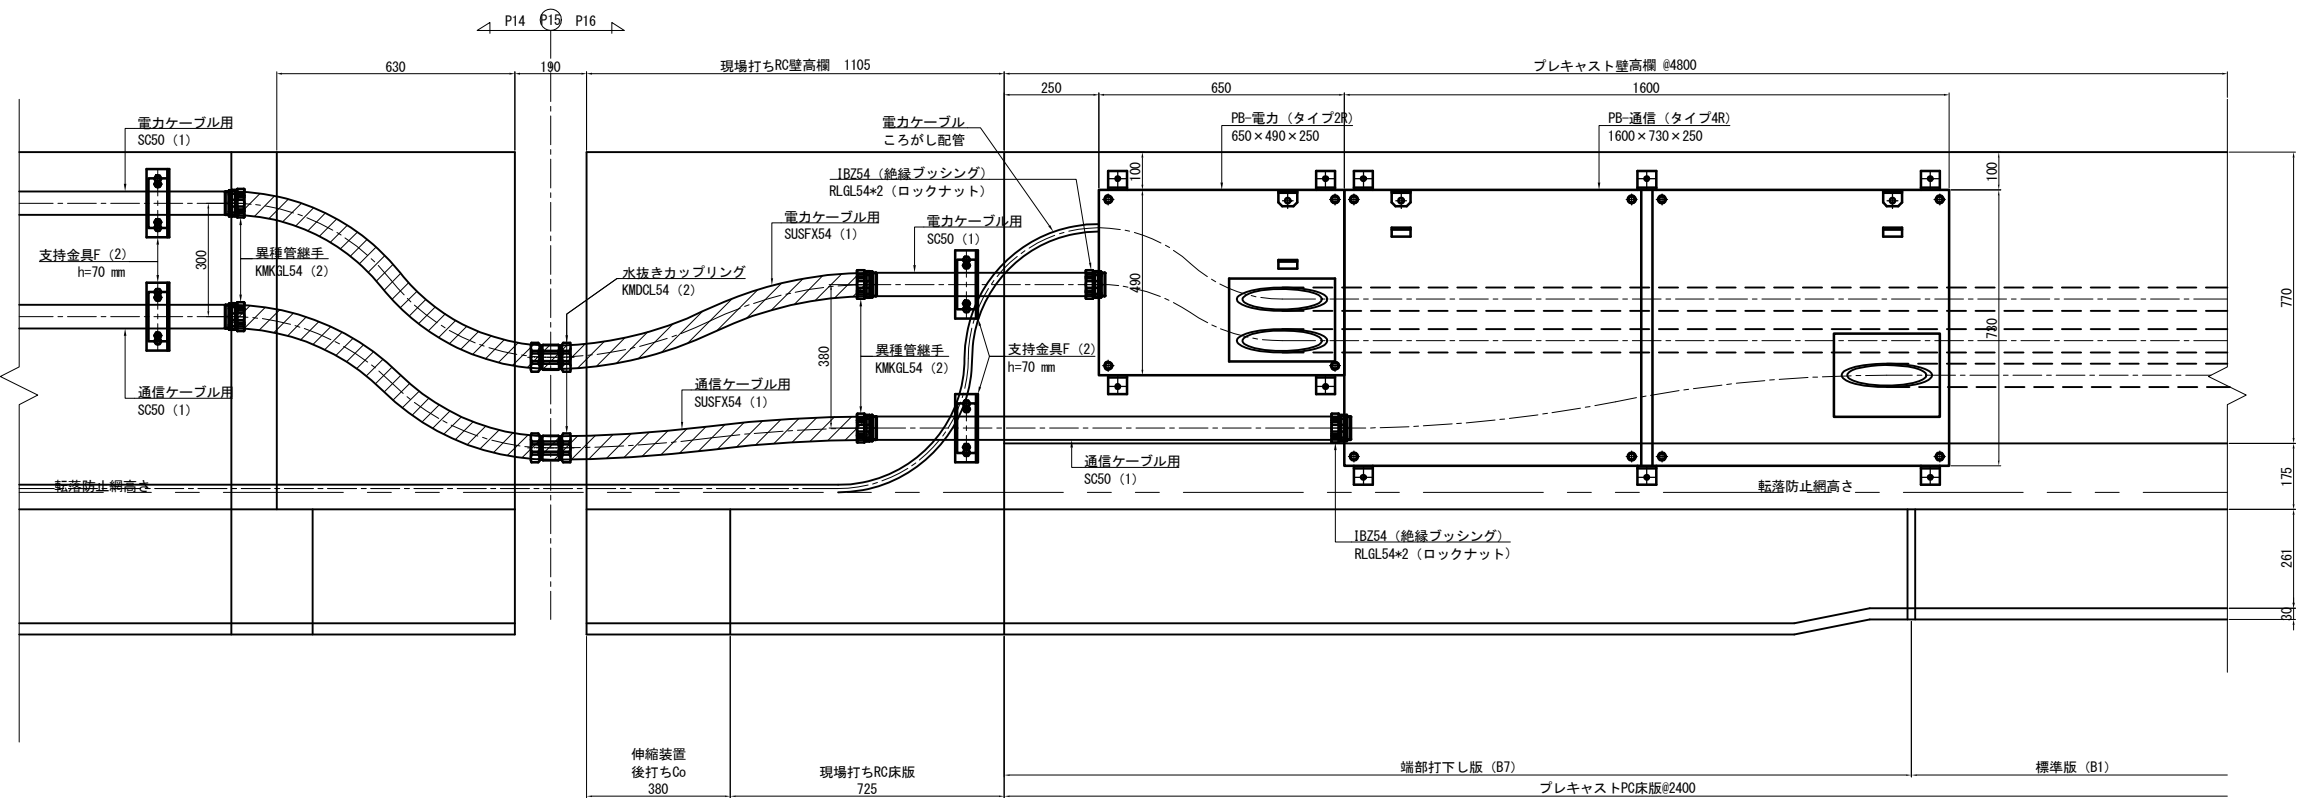


平面図

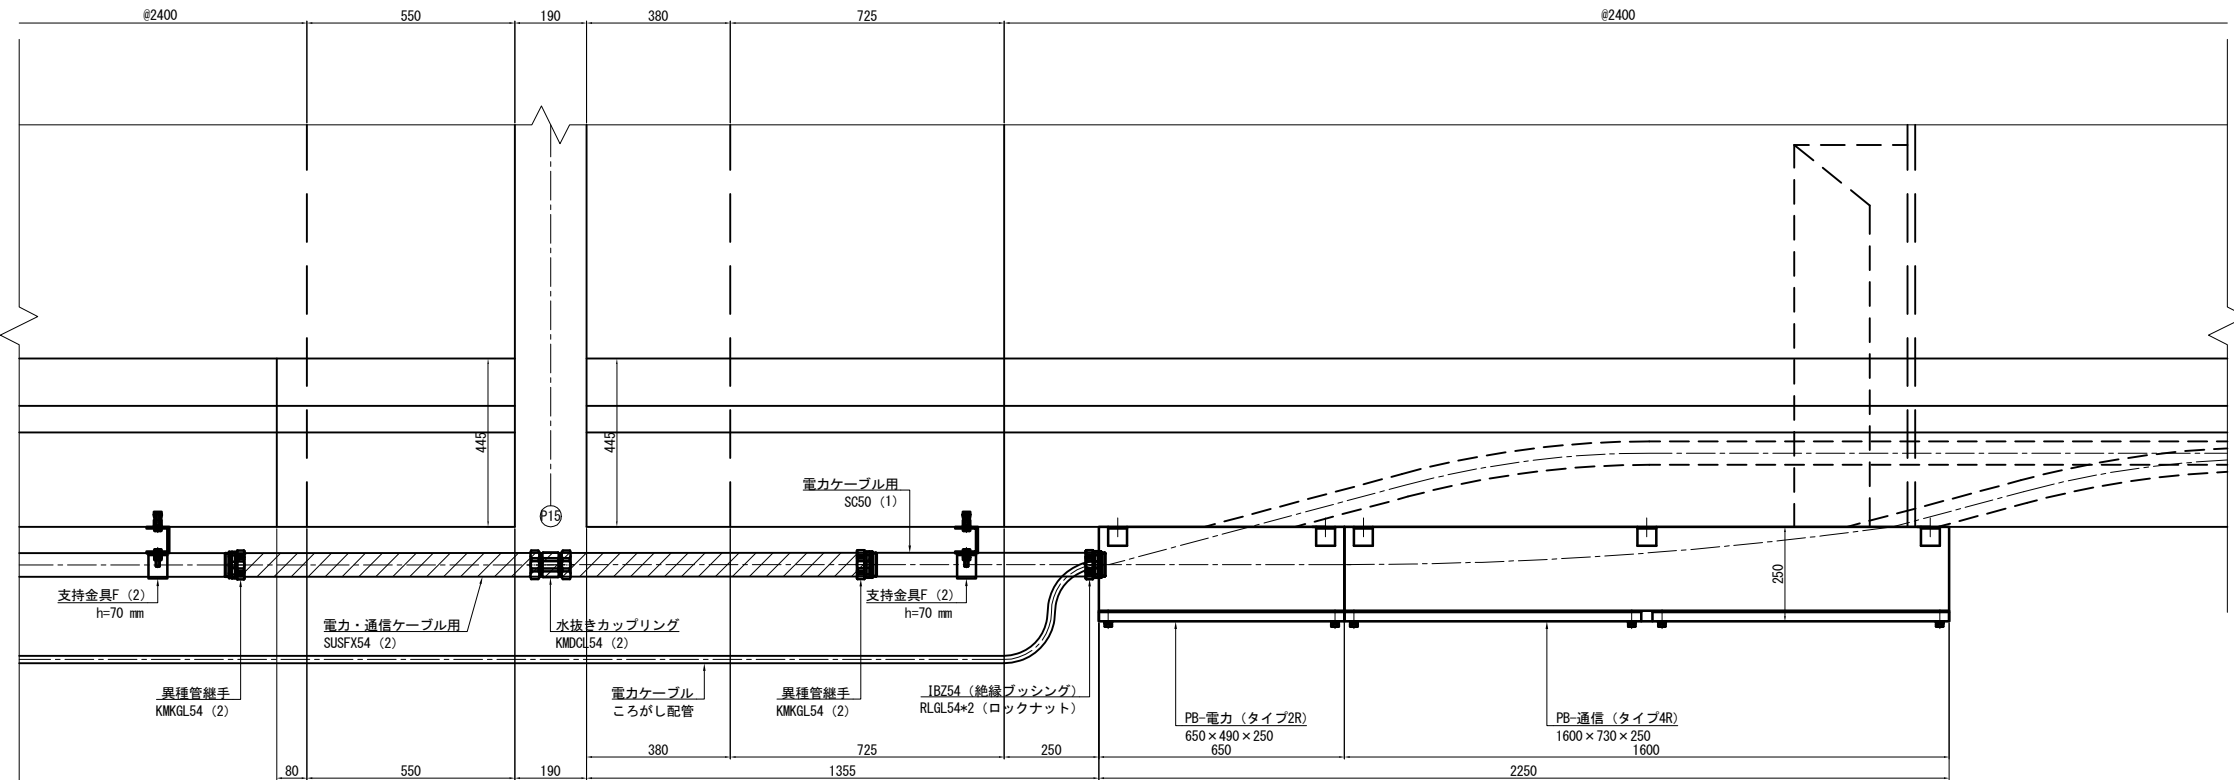


道央自動車道 千歳川大橋（下り線）床版取替工事			
図面の種類	千歳川大橋（下り線）P15-P24 通信管路工詳細図（2）		
縮尺	図示	図面番号	/
設計会社名	戸田建設株式会社		
施工会社名	戸田建設株式会社		
事務所名	東日本高速道路株式会社 北海道支社 札幌管理事務所		

千歳川大橋（下り線）P15-P24 通信管路工詳細図（3） S=1:20

側面図
P18路肩側

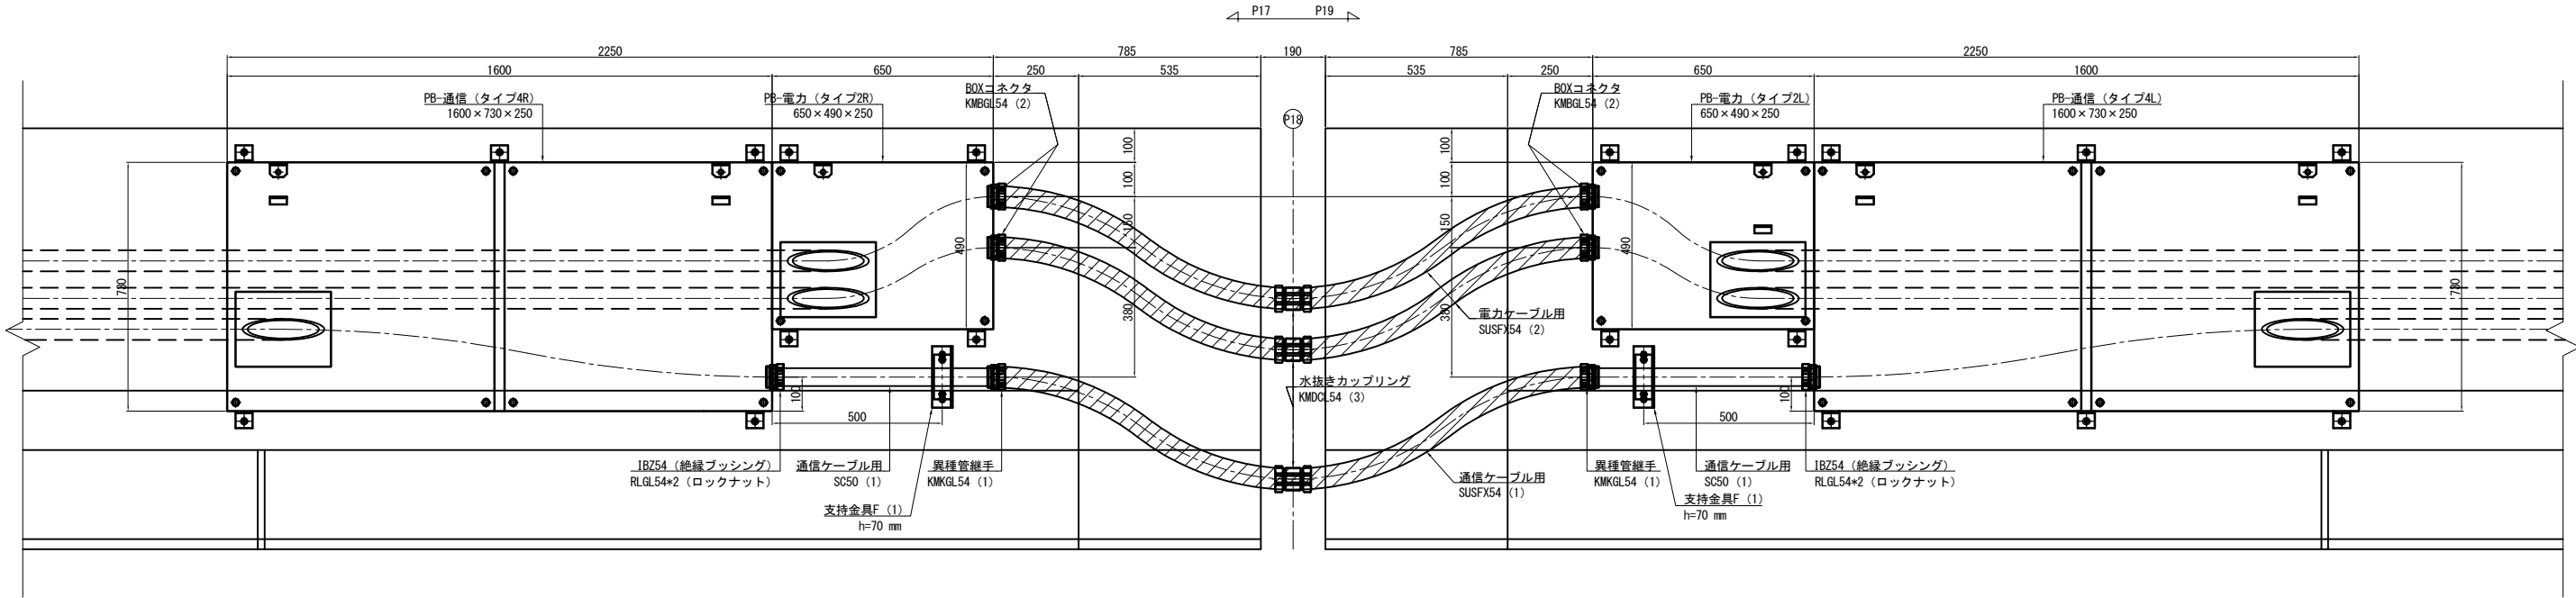


平面図

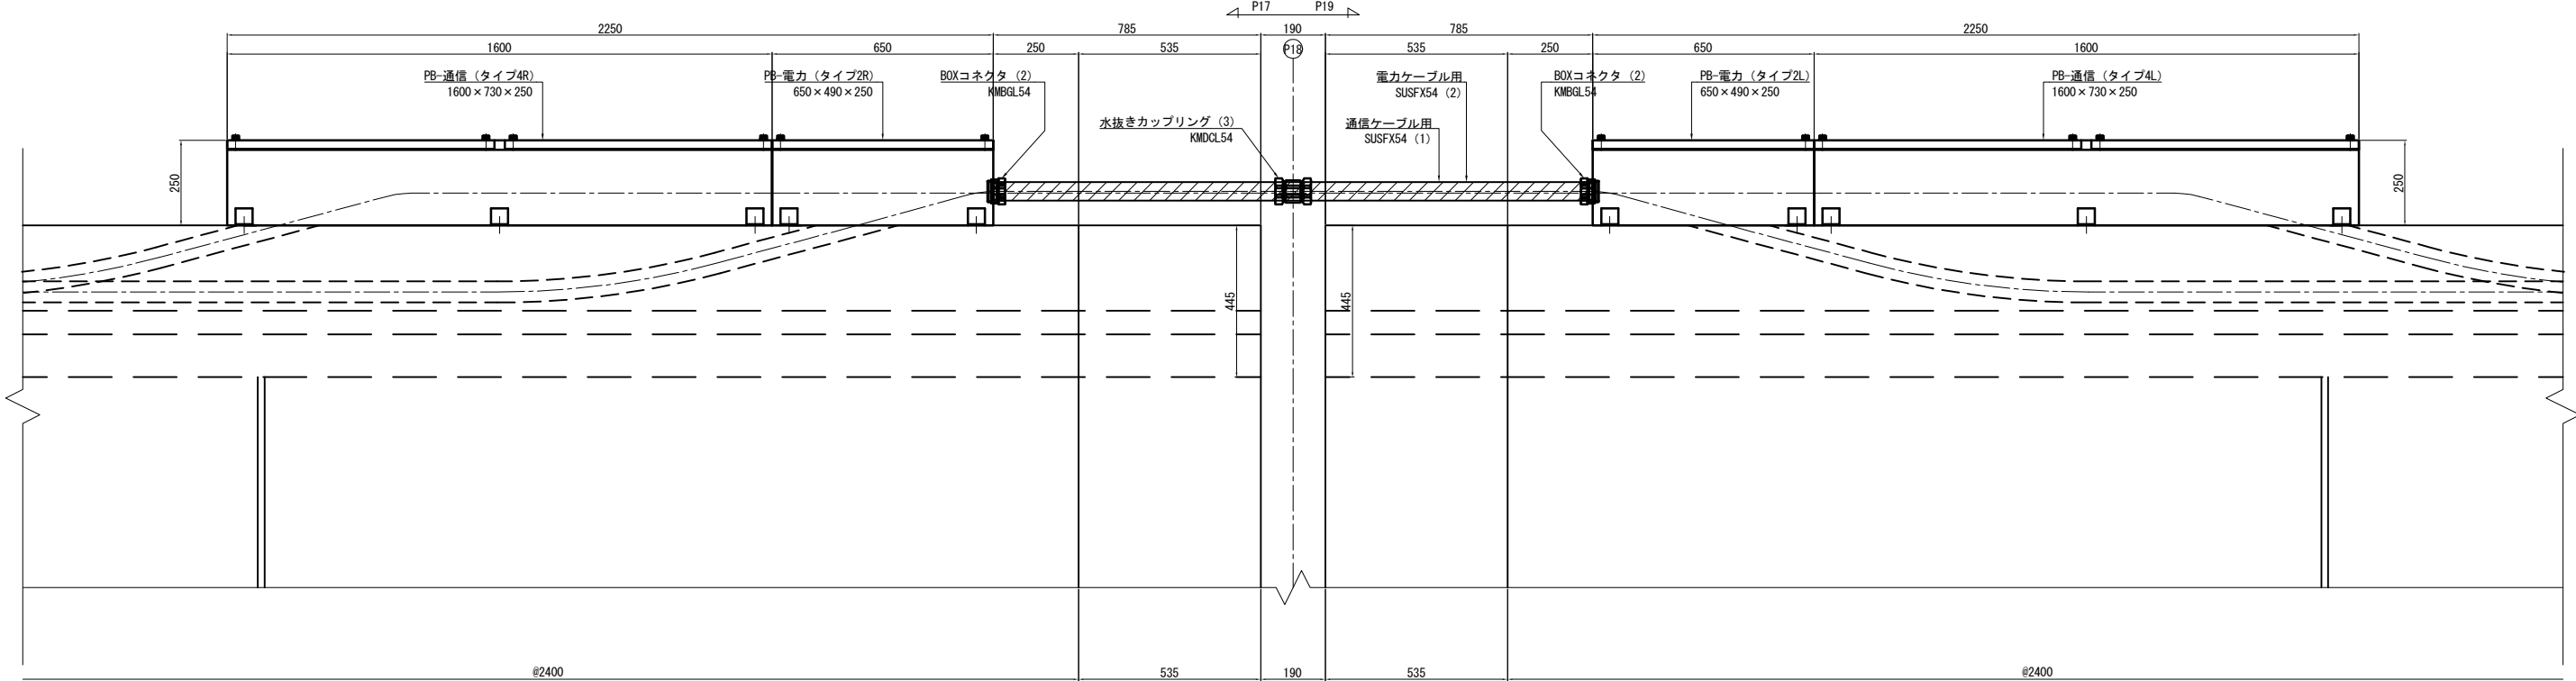


道央自動車道 千歳川大橋（下り線）床版取替工事			
図面の種類	千歳川大橋（下り線）P15-P24 通信管路工詳細図（3）		
縮 尺	図 示	図面番号	/
設計会社名	戸田建設株式会社		
施工会社名	戸田建設株式会社		
事務所名	東日本高速道路株式会社 北海道支社 札幌管理事務所		

千歳川大橋（下り線）P15-P24 通信管路工詳細図（4） S=1:20

側面図
P18中分側

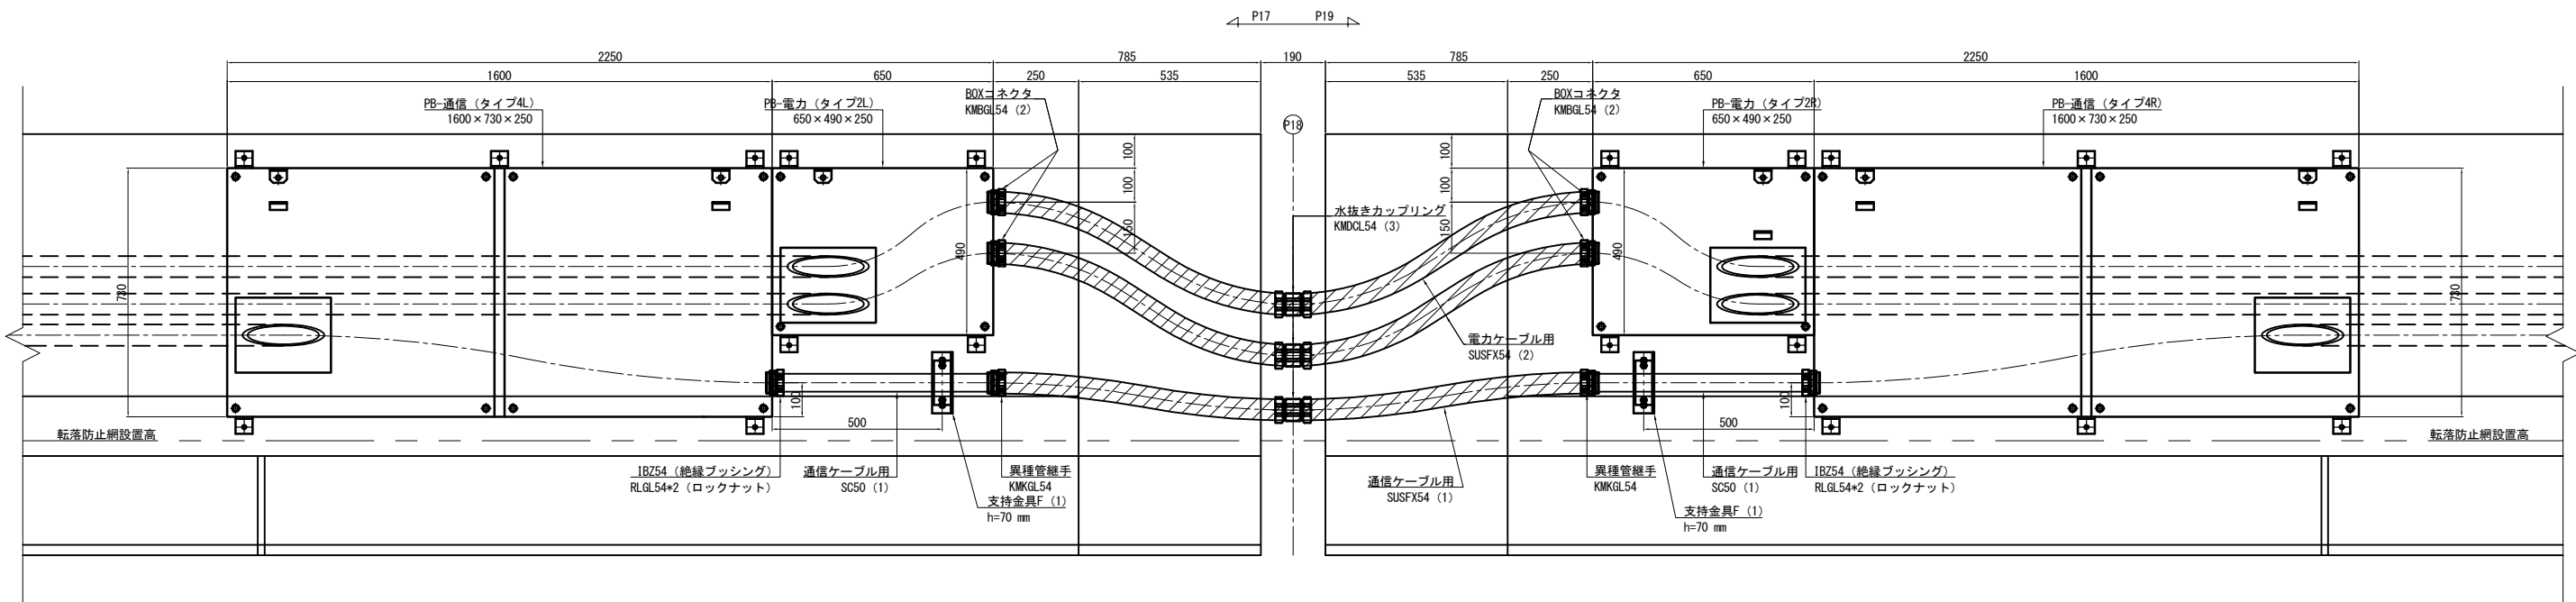


平面図

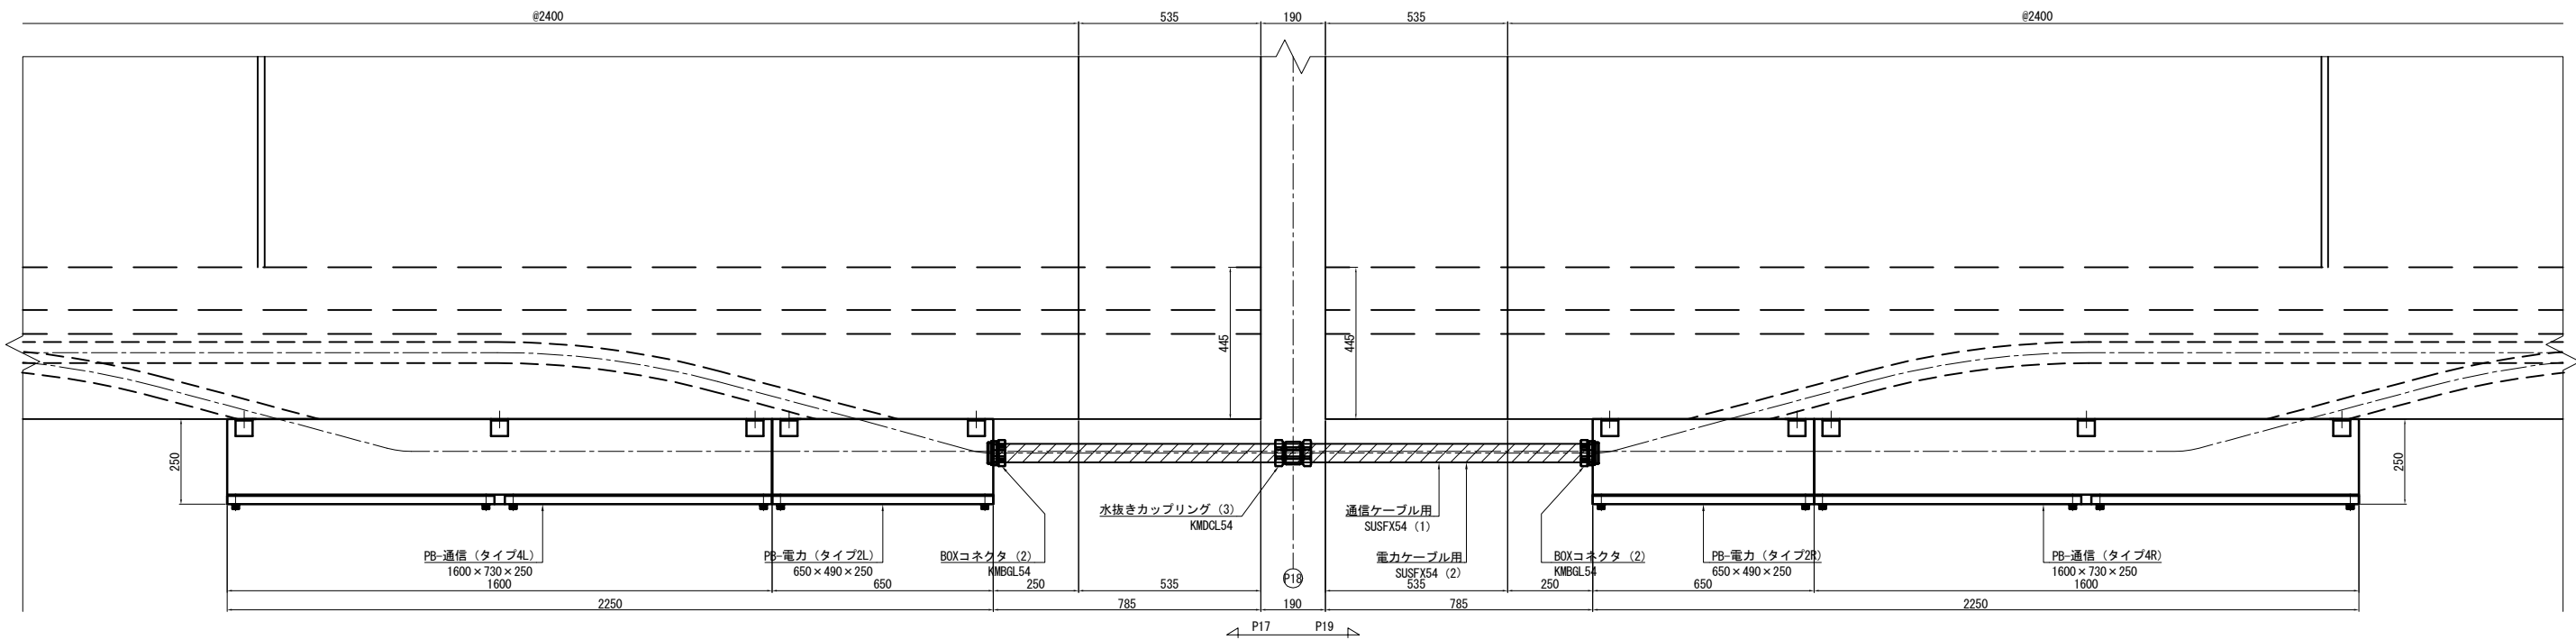


道央自動車道 千歳川大橋（下り線）床版取替工事			
図面の種類	千歳川大橋（下り線）P15-P24 通信管路工詳細図（4）		
縮尺	図示	図面番号	/
設計会社名	戸田建設株式会社		
施工会社名	戸田建設株式会社		
事務所名	東日本高速道路株式会社 北海道支社 札幌管理事務所		

千歳川大橋（下り線）P15-P24 通信管路工詳細図（5） S=1:20

側面図
P24路肩側

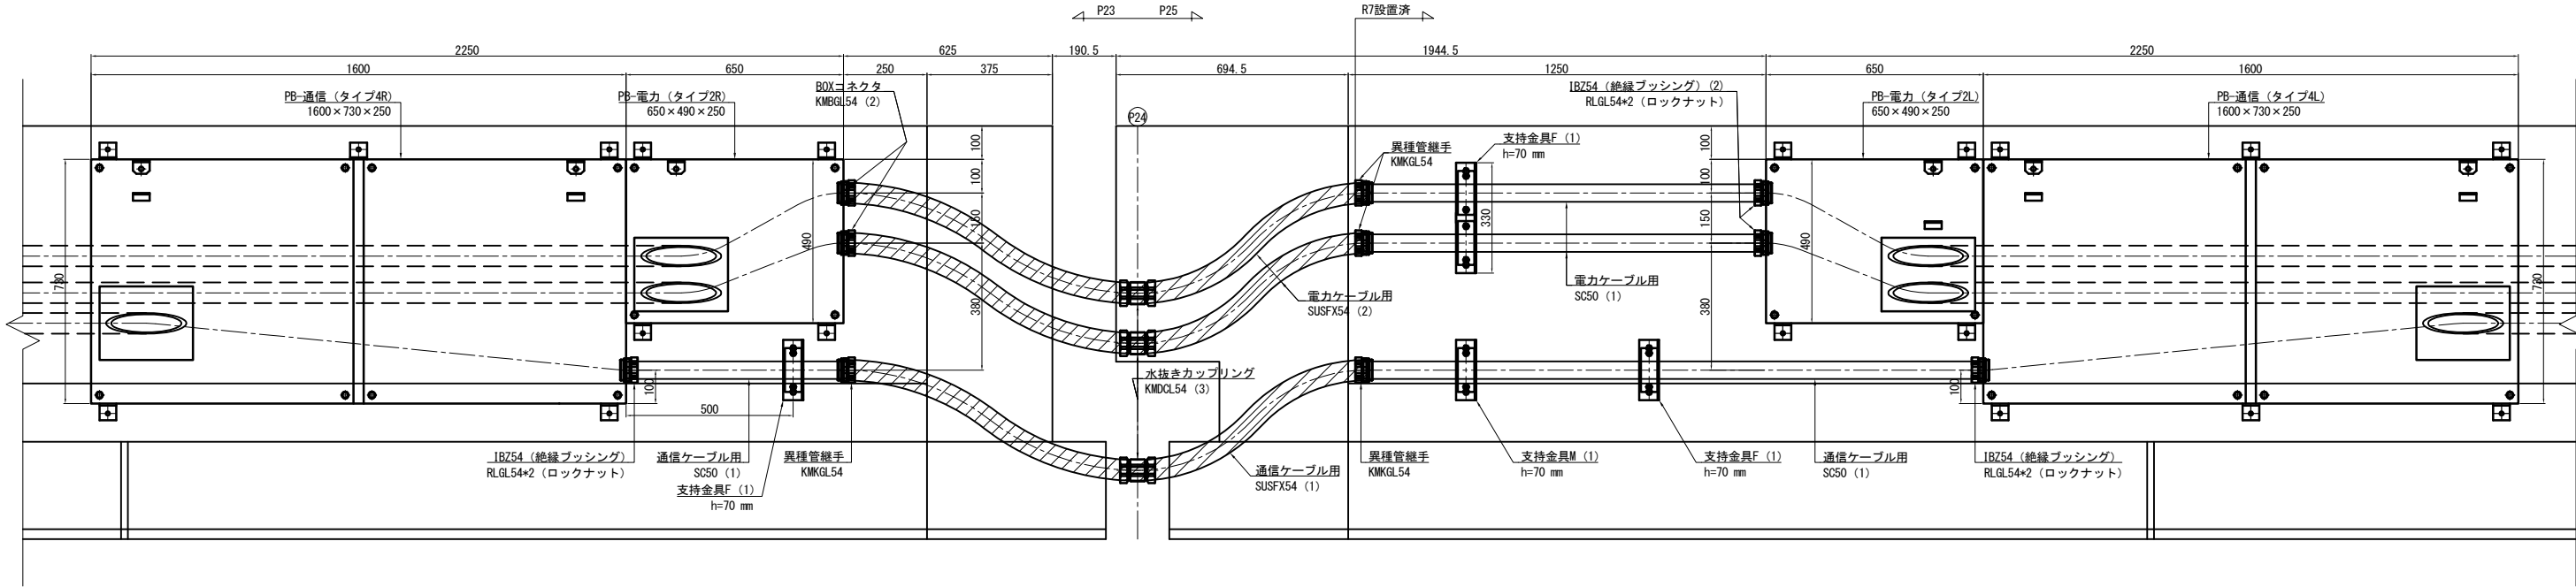


平面図

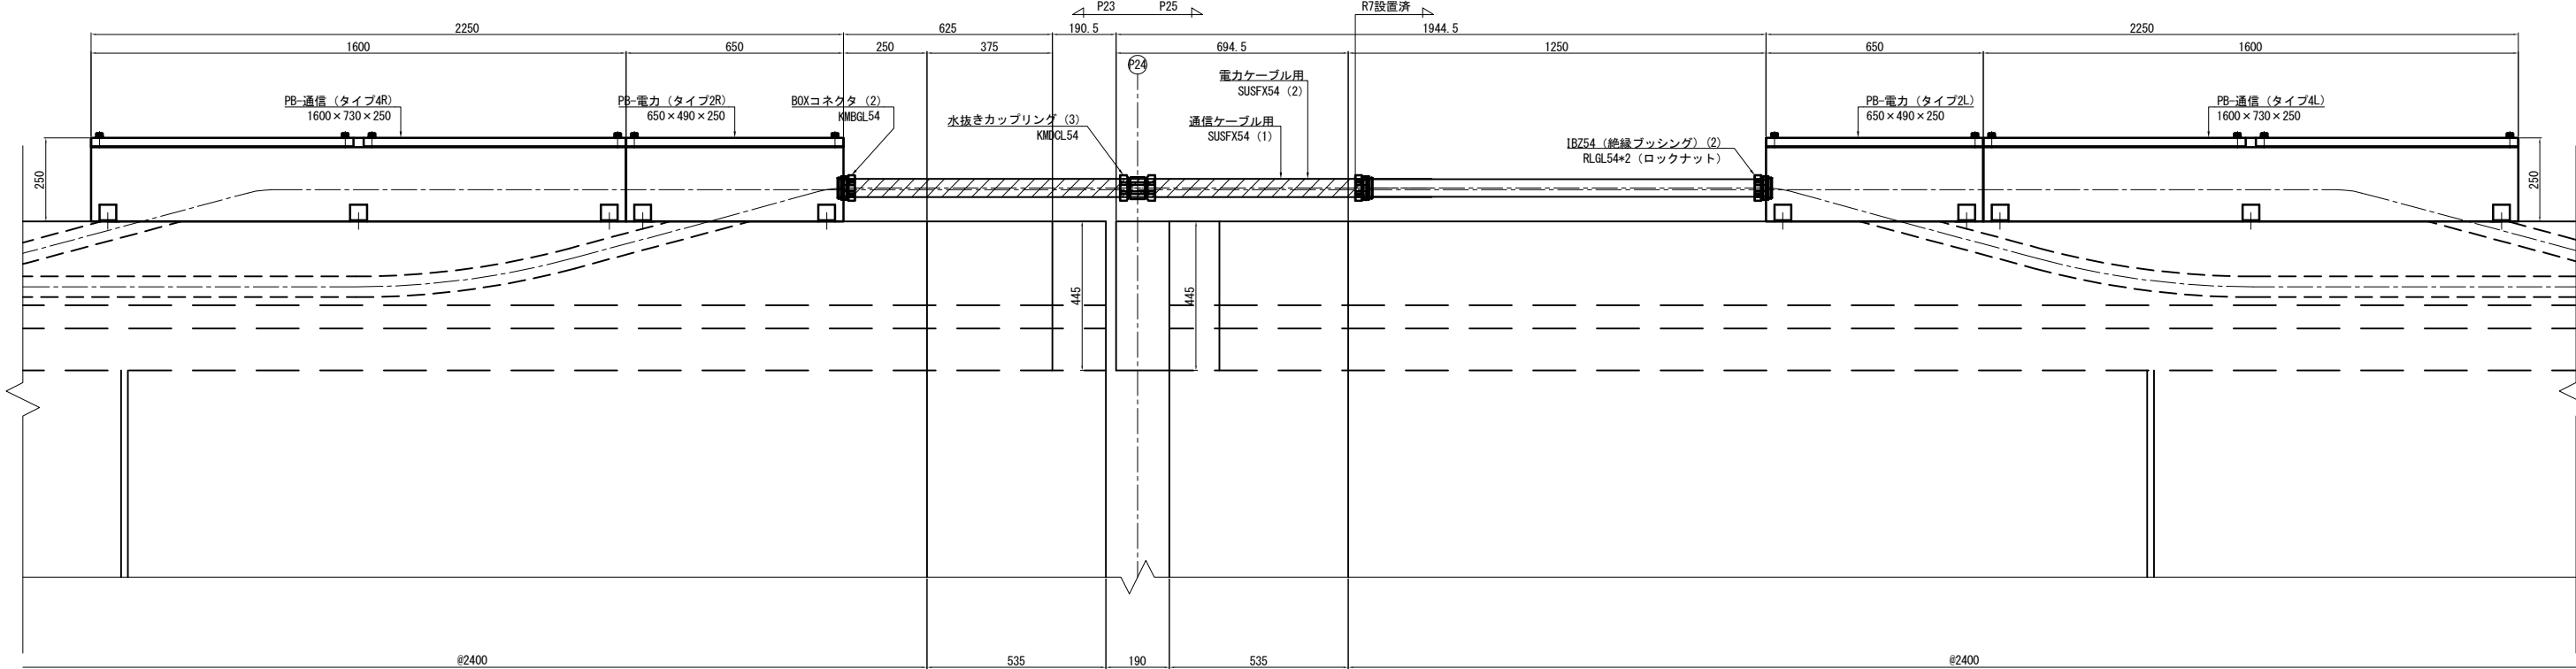


道央自動車道 千歳川大橋（下り線）床版取替工事			
図面の種類	千歳川大橋（下り線）P15-P24 通信管路工詳細図（5）		
縮 尺	図 示	図面番号	/
設計会社名	戸田建設株式会社		
施工会社名	戸田建設株式会社		
事務所名	東日本高速道路株式会社 北海道支社 札幌管理事務所		




側面図
P24中分側

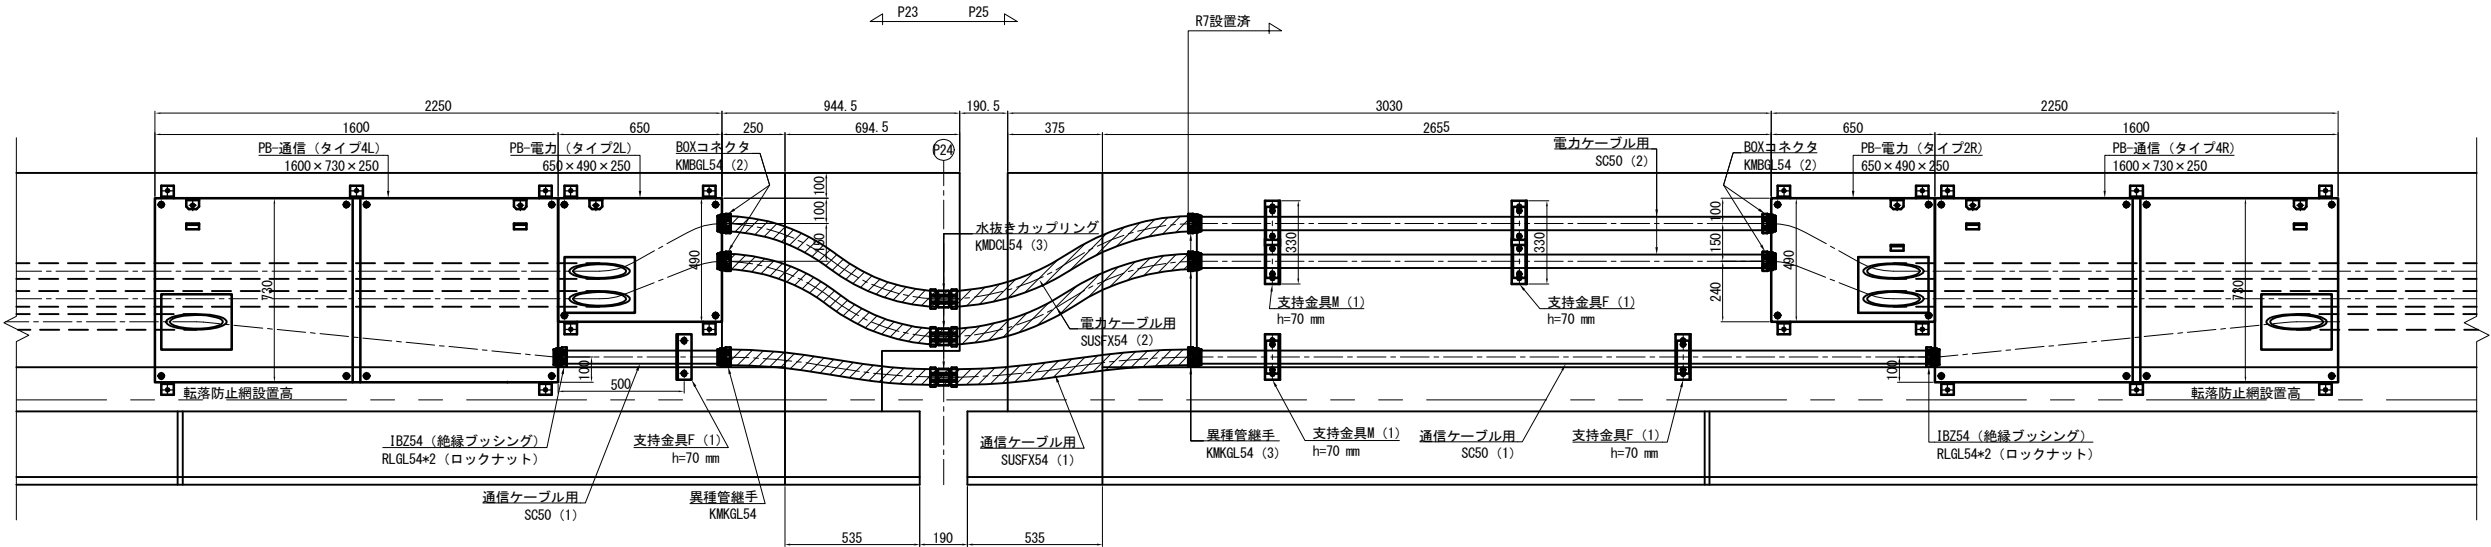

平面図

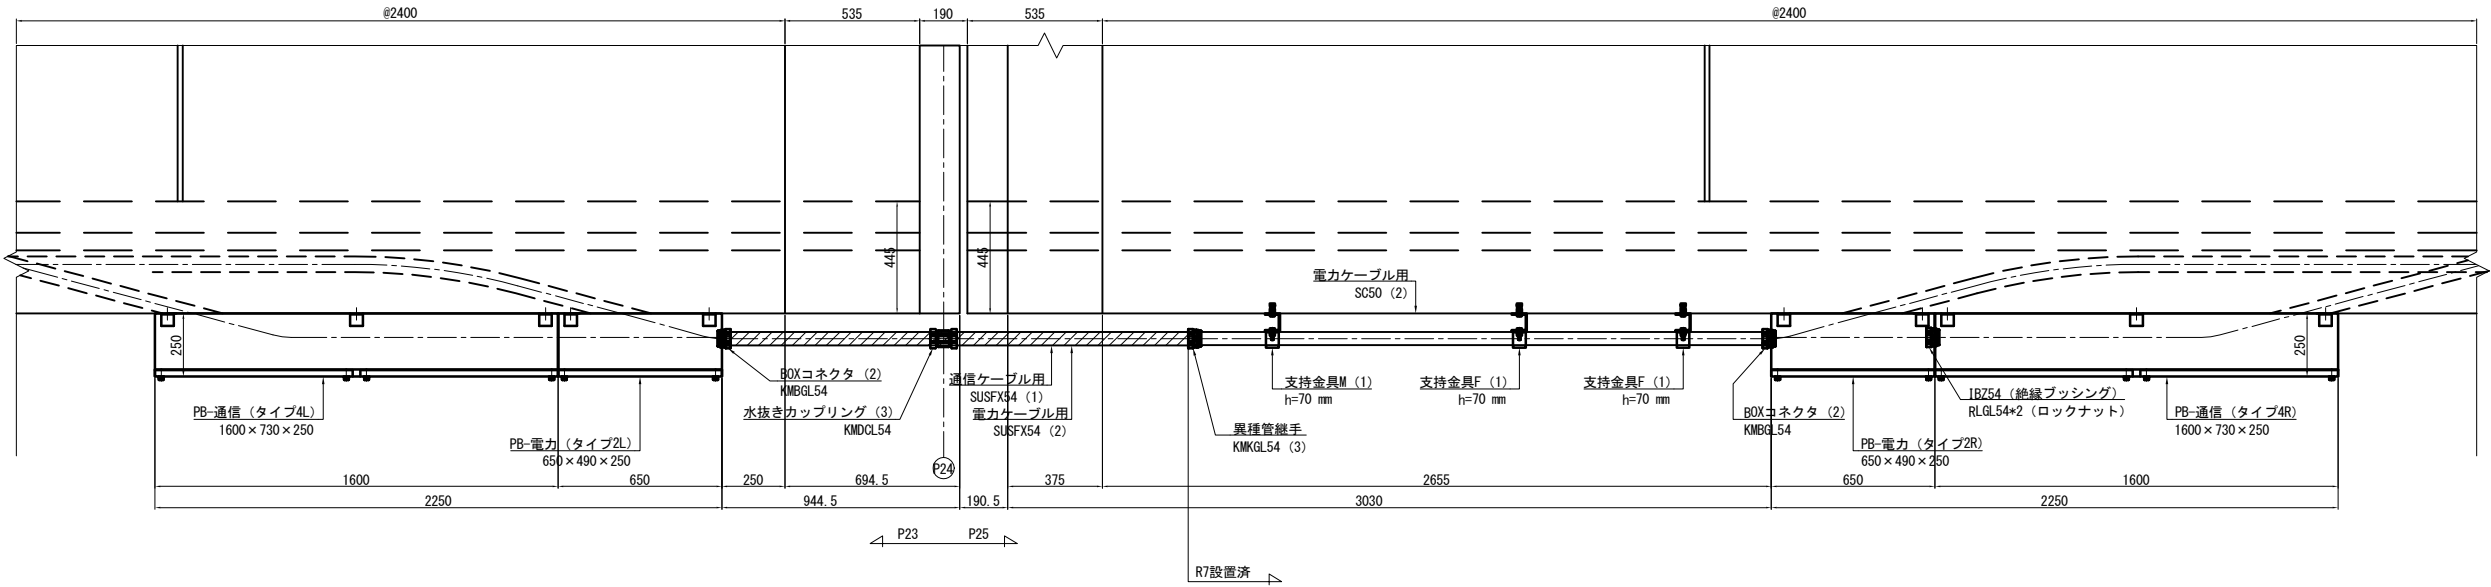


道央自動車道 千歳川大橋（下り線）床版取替工事			
図面の種類	千歳川大橋（下り線）P15-P24 通信管路工詳細図（6）		
縮 尺	図 示	図面番号	/
設計会社名	戸田建設株式会社		
施工会社名	戸田建設株式会社		
事務所名	東日本高速道路株式会社 北海道支社 札幌管理事務所		

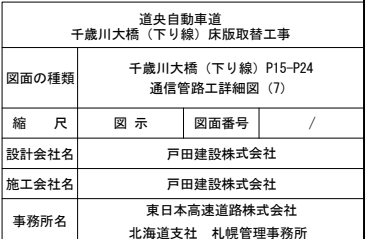

千歳川大橋（下り線）P15-P24 通信管路工詳細図（8） S=1:50


路肩側側面図

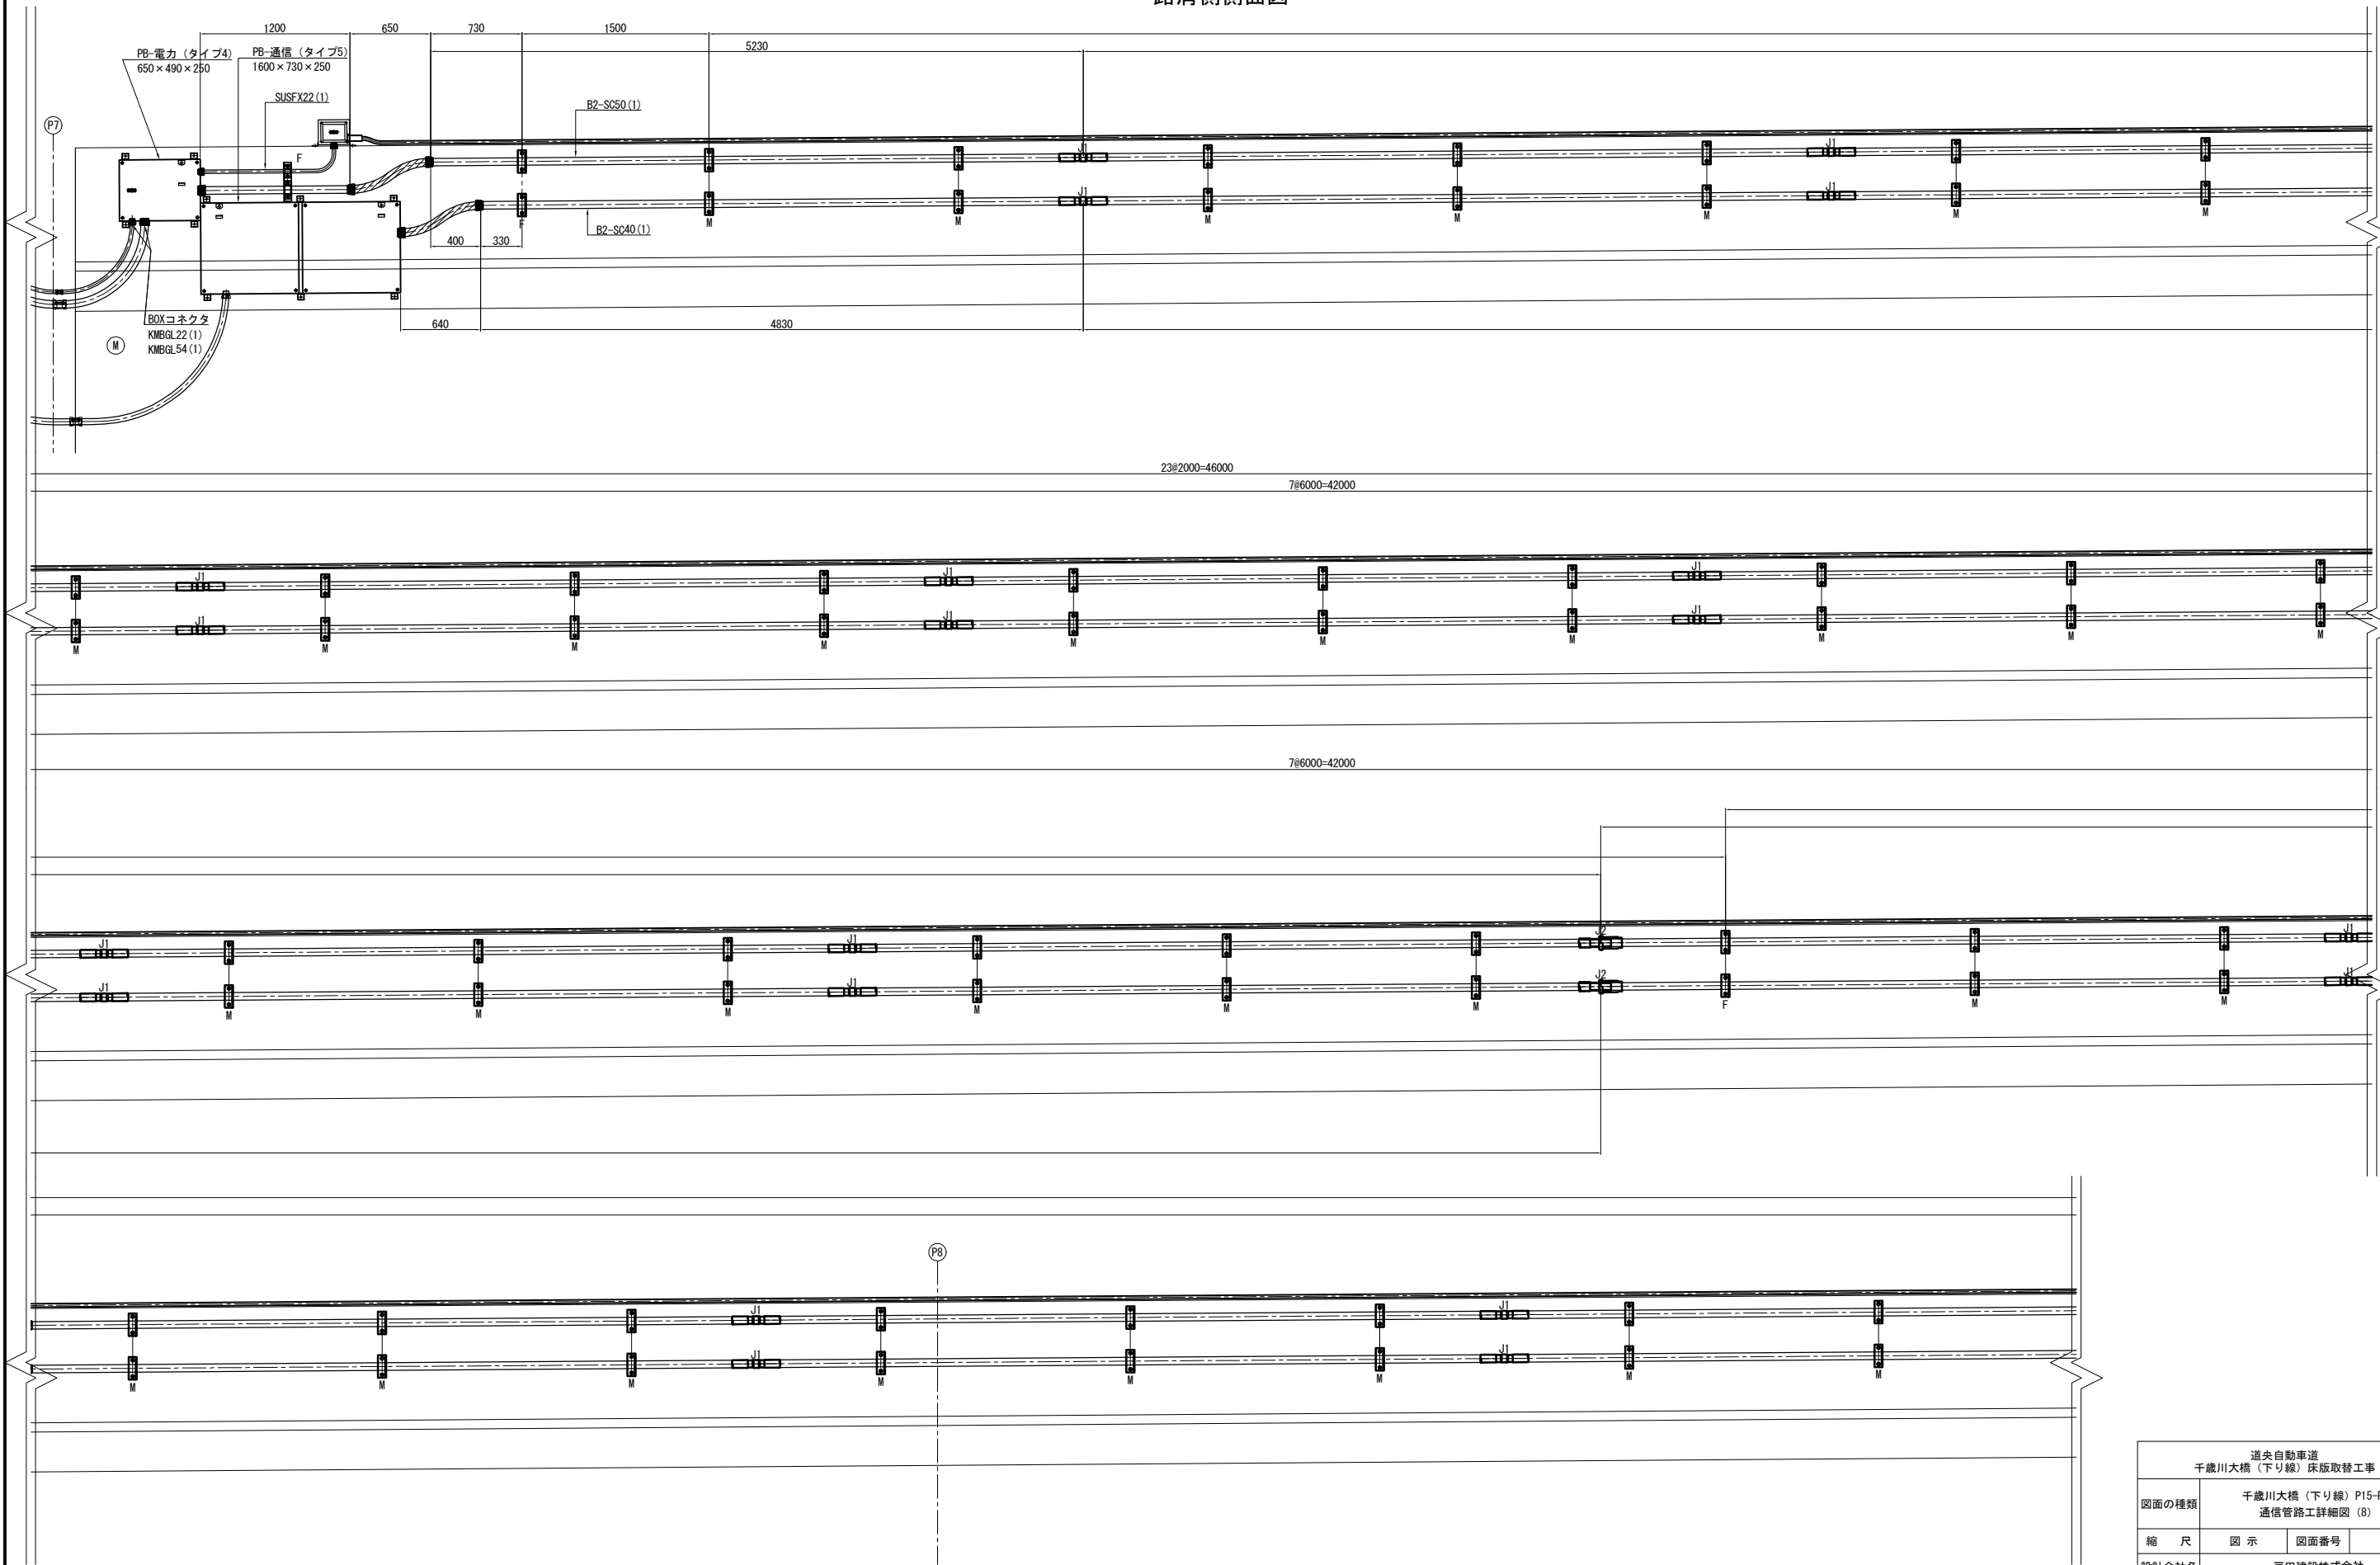

道央自動車道 千歳川大橋（下り線）床版取替工事			
図面の種類	千歳川大橋（下り線）P15-P24 通信管路工詳細図（8）		
縮 尺	図 示	図面番号	/
設計会社名	戸田建設株式会社		
施工会社名	戸田建設株式会社		
事務所名	東日本高速道路株式会社 北海道支社 札幌管理事務所		

千歳川大橋（下り線）P15-P24 通信管路工詳細図（9） S=1:50


路肩側側面図

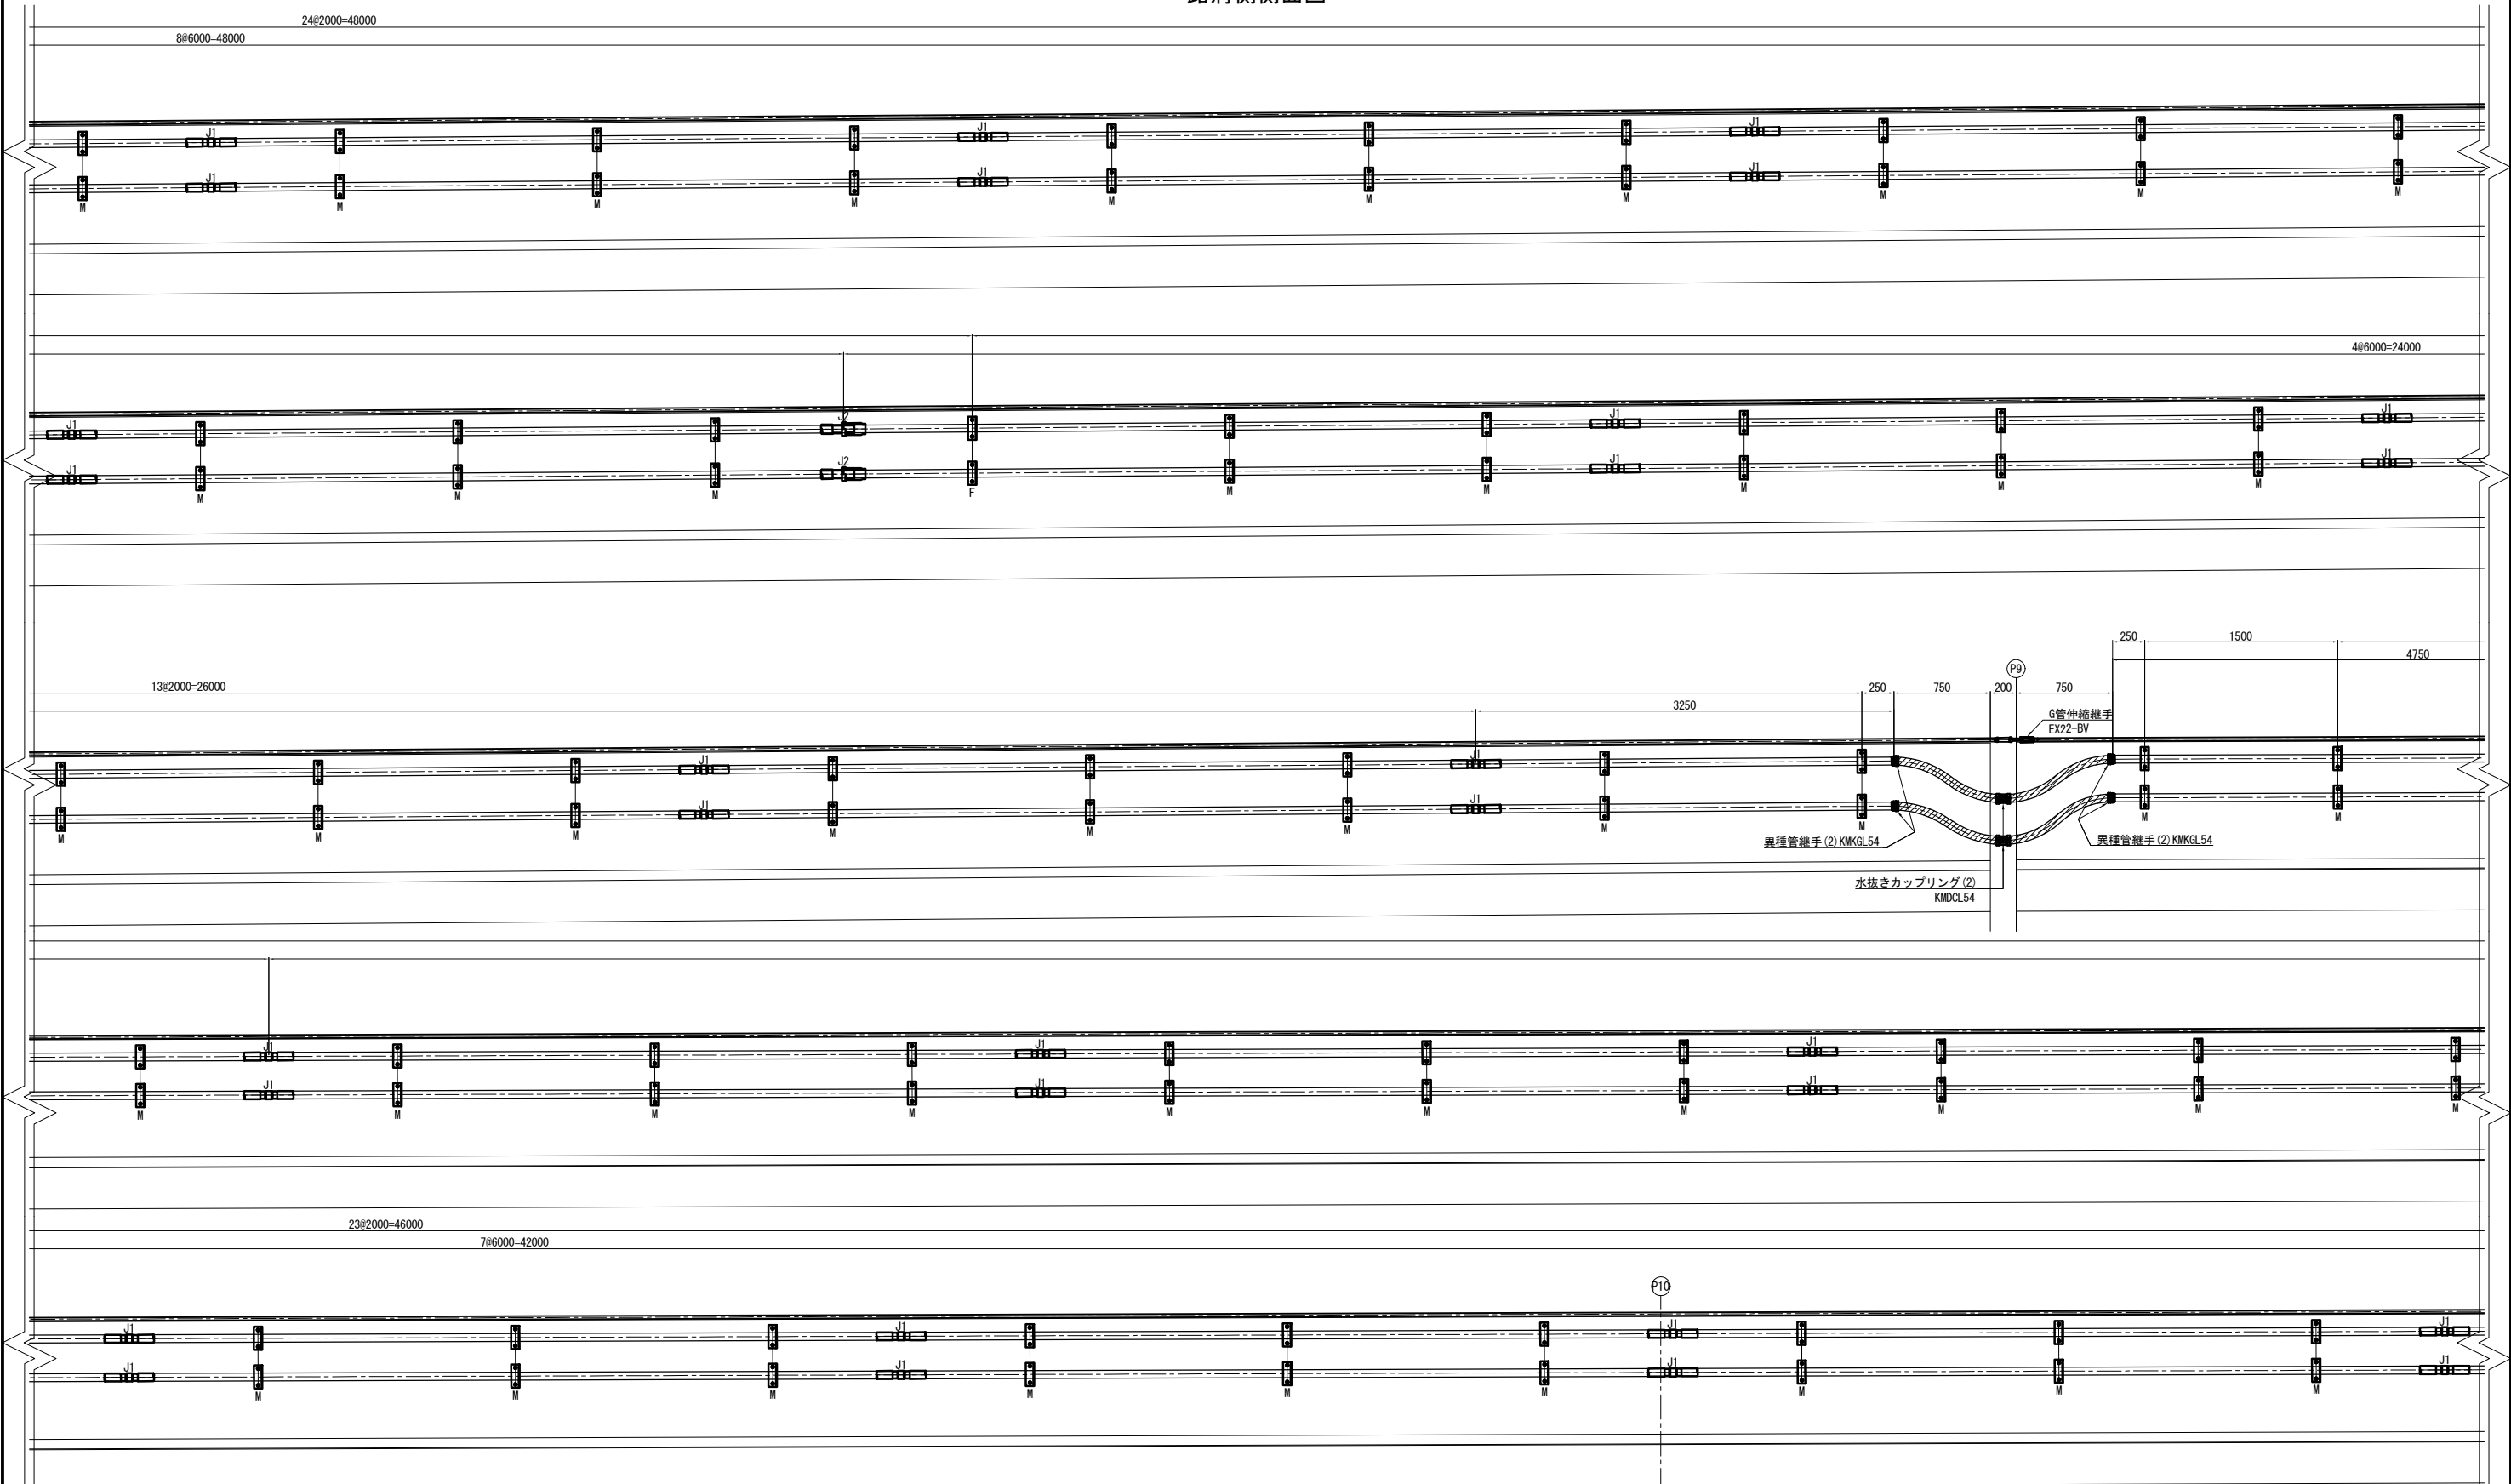

道央自動車道 千歳川大橋（下り線）床版取替工事			
図面の種類	千歳川大橋（下り線）P15-P24 通信管路工詳細図（9）		
縮 尺	図 示	図面番号	/
設計会社名	戸田建設株式会社		
施工会社名	戸田建設株式会社		
事務所名	東日本高速道路株式会社 北海道支社 札幌管理事務所		

千歳川大橋（下り線）P15-P24 通信管路工詳細図（10） S=1:50

路肩側側面図

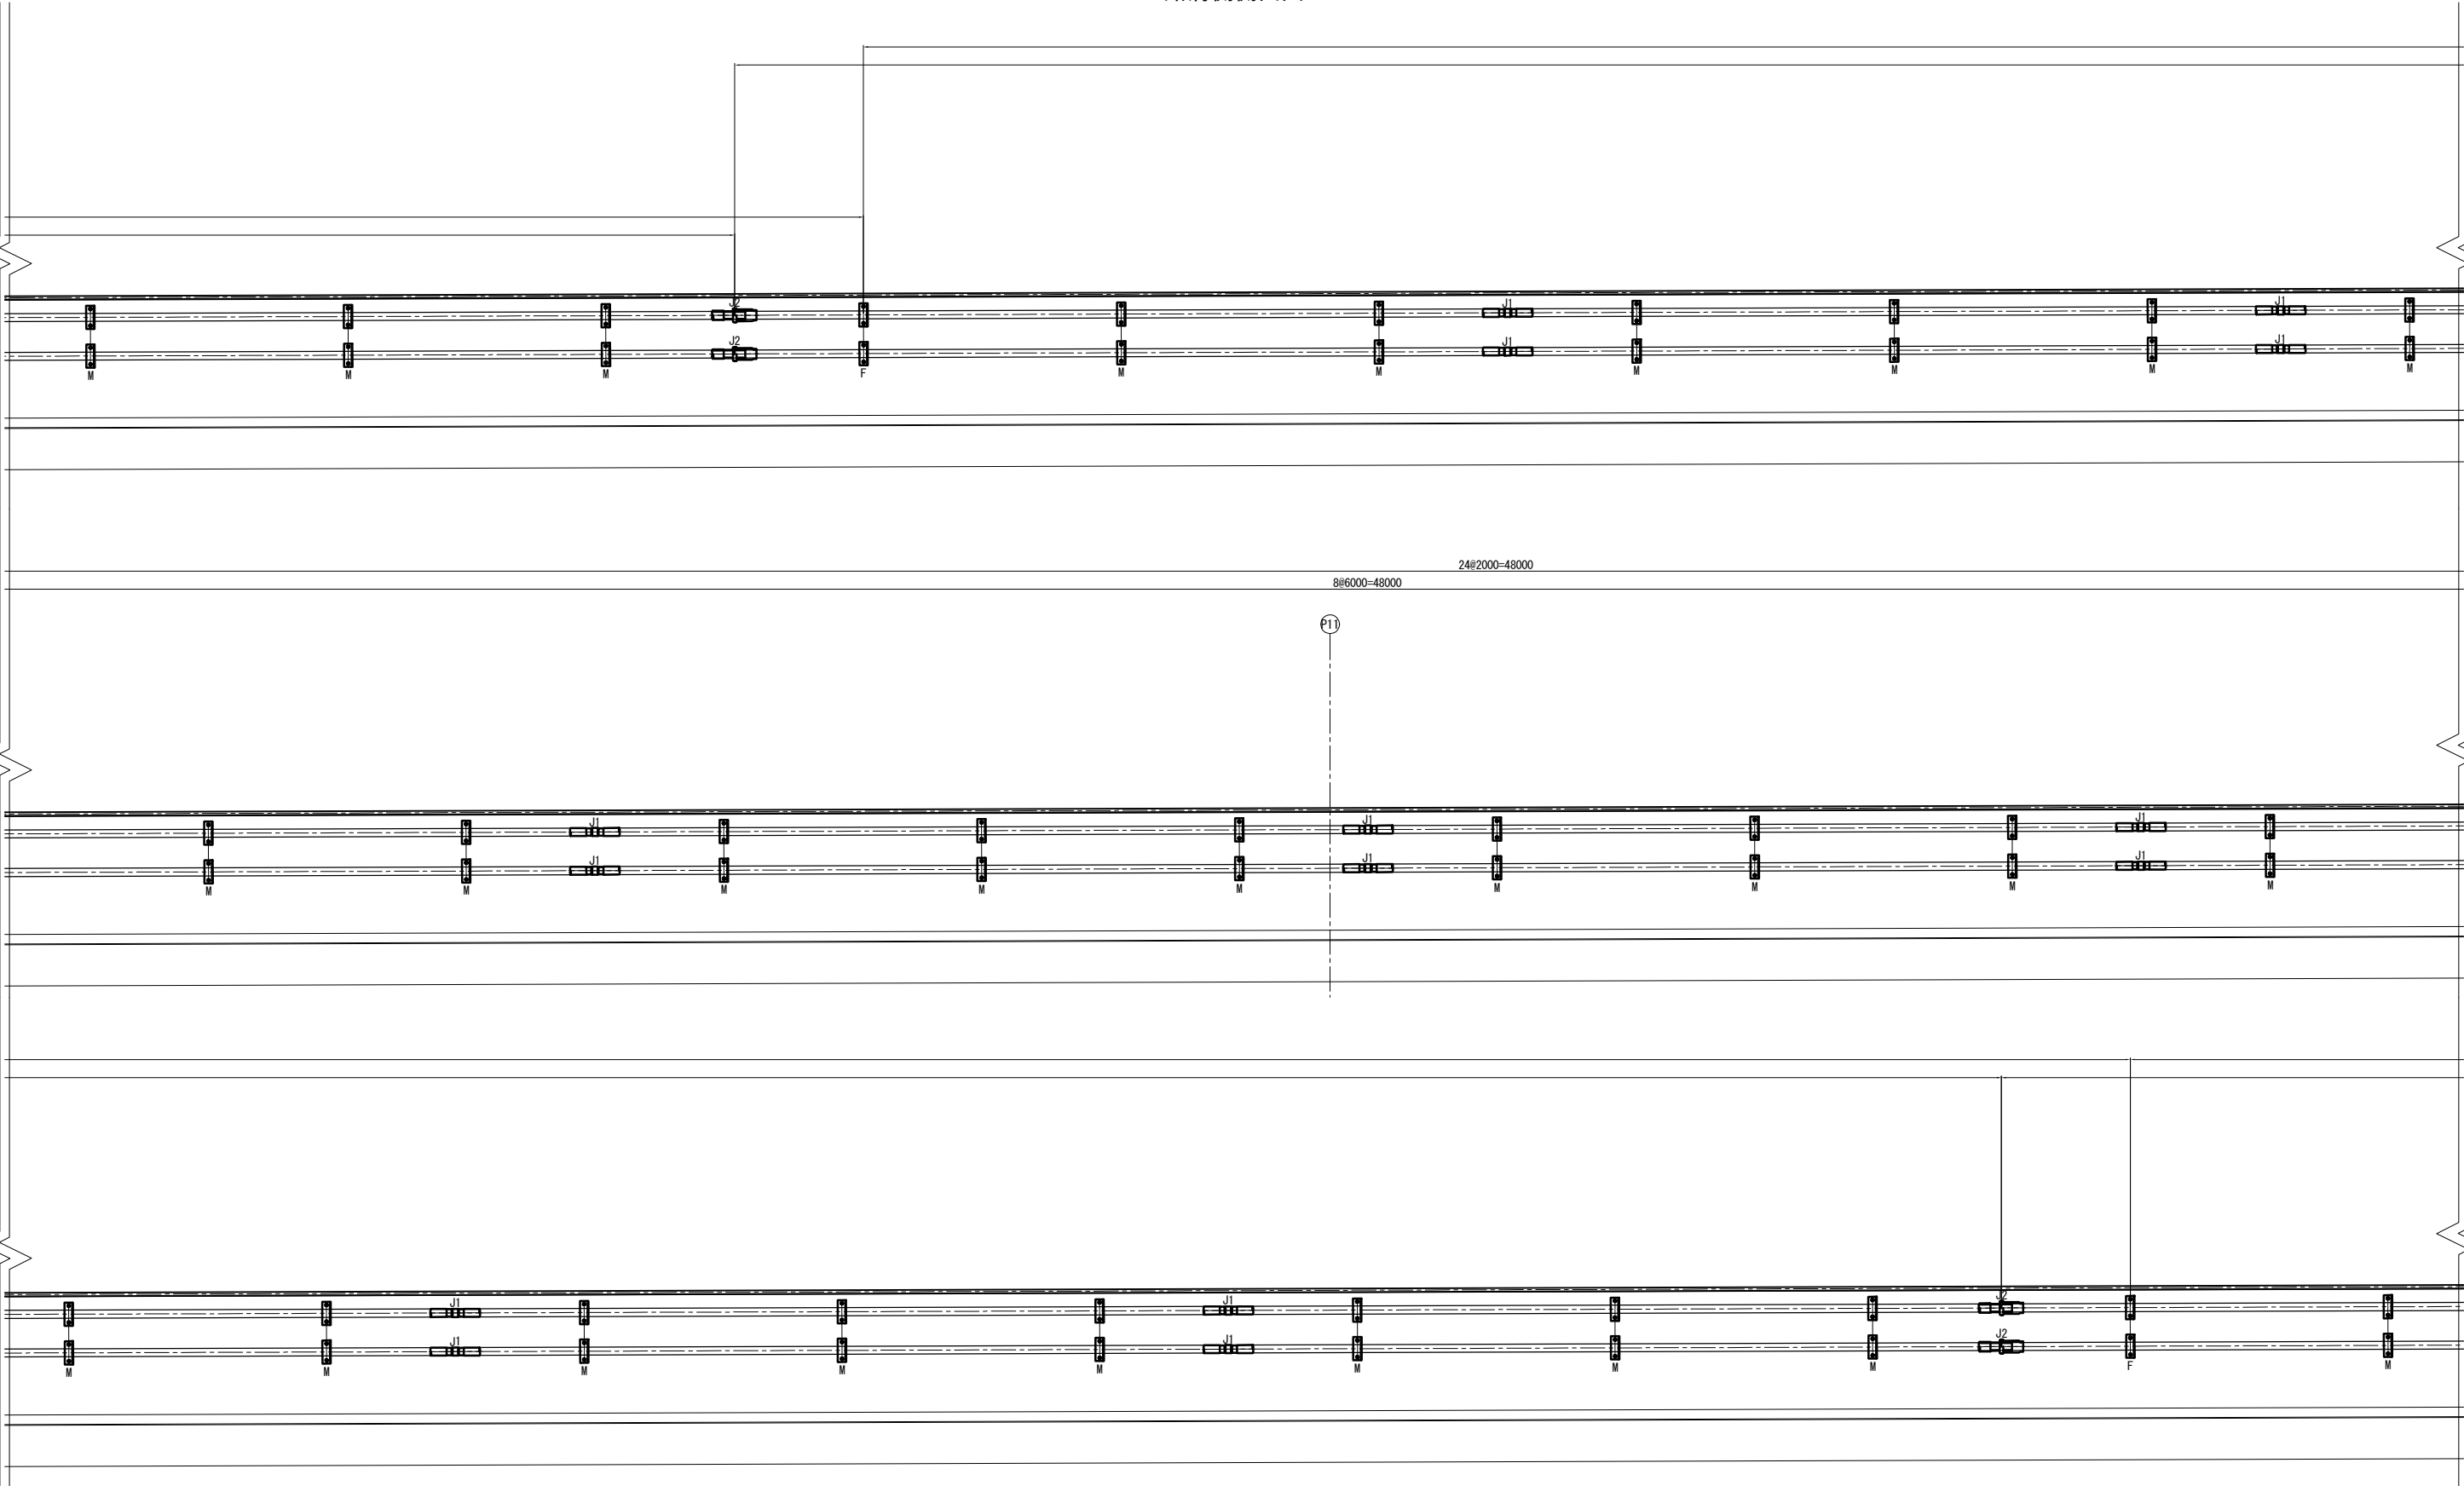

道央自動車道 千歳川大橋（下り線）床版取替工事			
図面の種類	千歳川大橋（下り線）P15-P24 通信管路工詳細図（10）		
縮 尺	図 示	図面番号	/
設計会社名	戸田建設株式会社		
施工会社名	戸田建設株式会社		
事務所名	東日本高速道路株式会社 北海道支社 札幌管理事務所		

千歳川大橋（下り線）P15-P24 通信管路工詳細図（11）S=1:50









路肩側側面図



道央自動車道 千歳川大橋（下り線）床版取替工事			
図面の種類	千歳川大橋（下り線）P15-P24 通信管路工詳細図（11）		
縮 尺	図 示	図面番号	/
設計会社名	戸田建設株式会社		
施工会社名	戸田建設株式会社		
事務所名	東日本高速道路株式会社 北海道支社 札幌管理事務所		

千歳川大橋（下り線）P15-P24 通信管路工詳細図（12）S=1:50


路肩側側面図

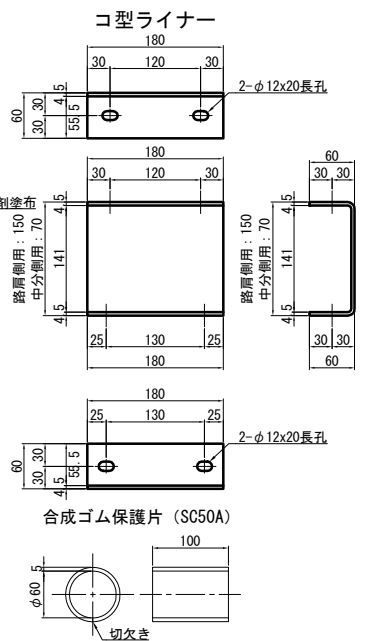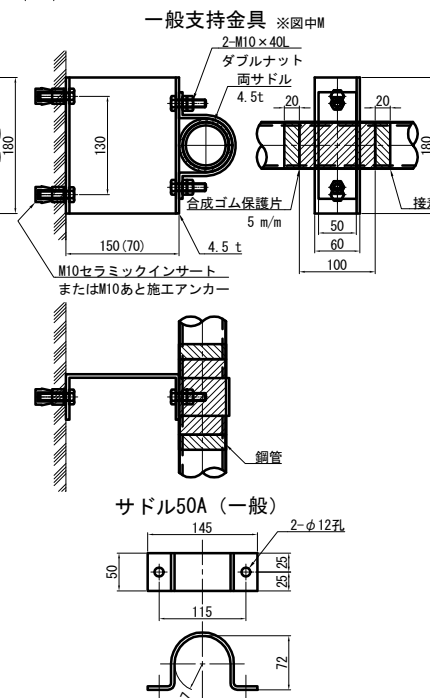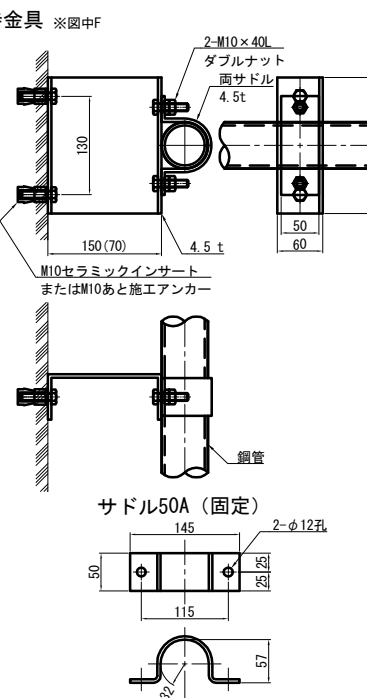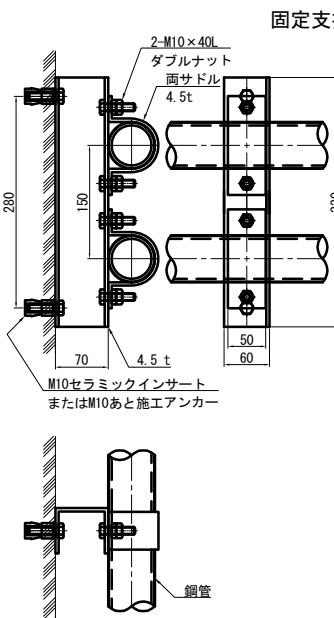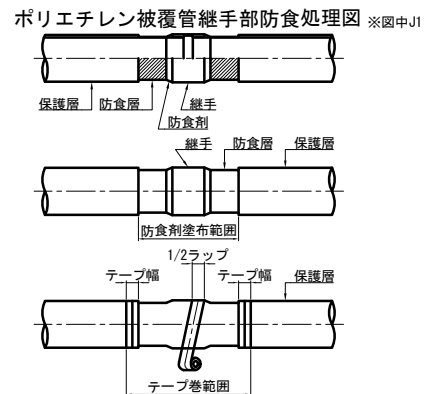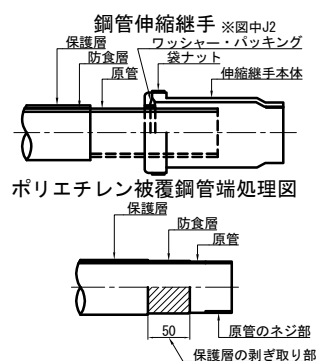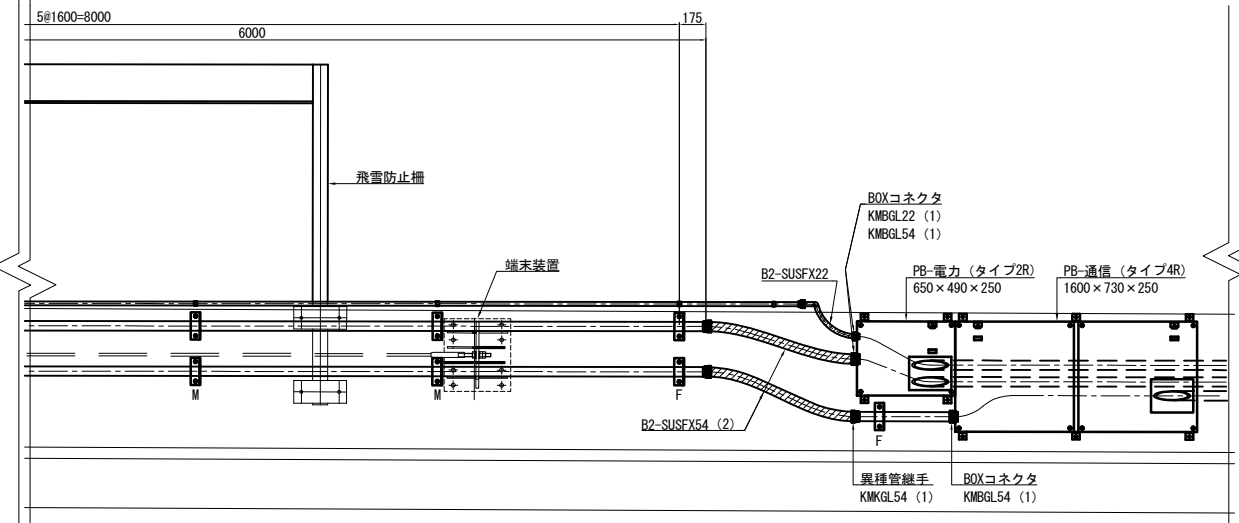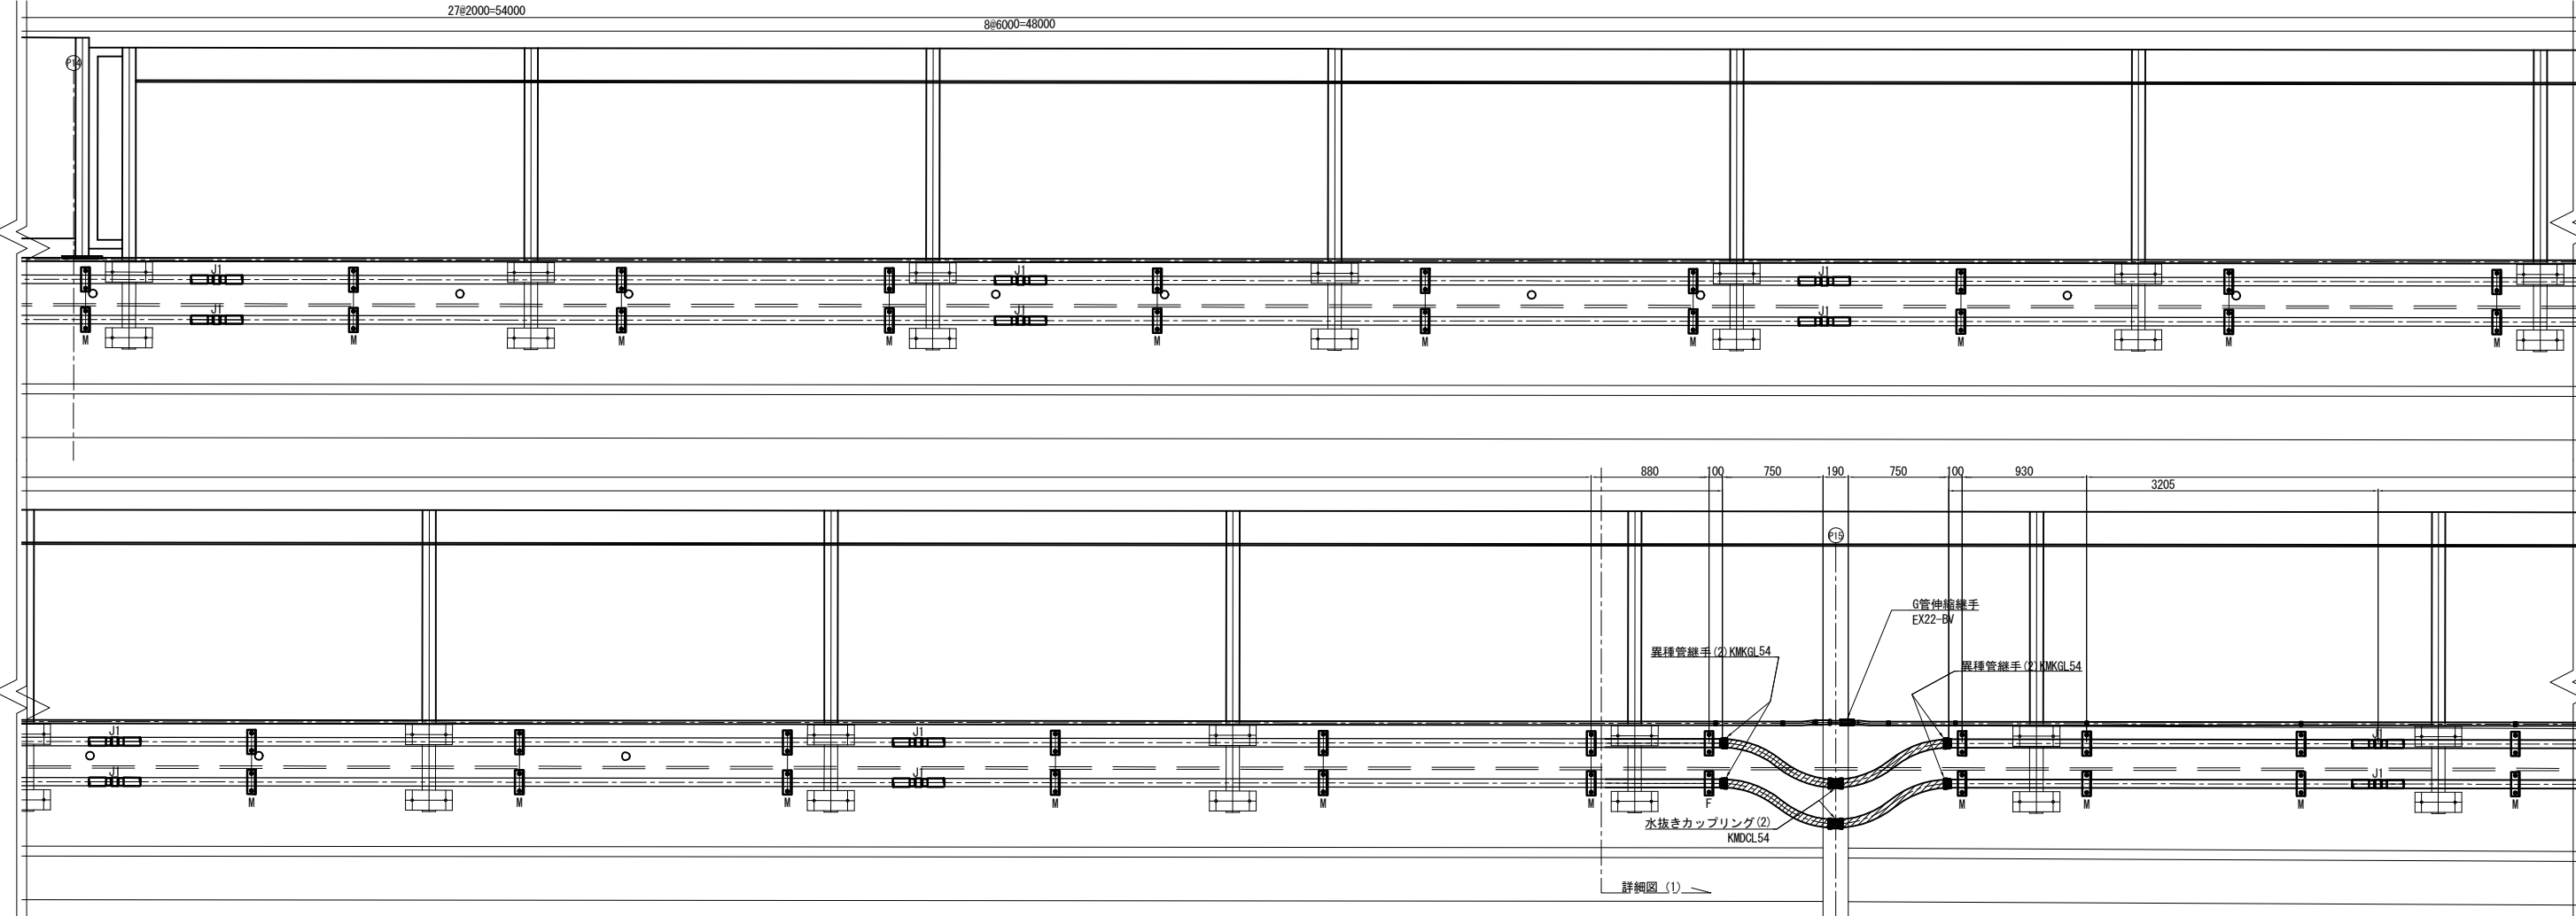


道央自動車道 千歳川大橋（下り線）床版取替工事			
図面の種類	千歳川大橋（下り線）P15-P24 通信管路工詳細図（12）		
縮 尺	図 示	図面番号	/
設計会社名	戸田建設株式会社		
施工会社名	戸田建設株式会社		
事務所名	東日本高速道路株式会社 北海道支社 札幌管理事務所		

千歳川大橋（下り線）P15-P24 通信管路工詳細図（13） S=1:50

中分側側面図

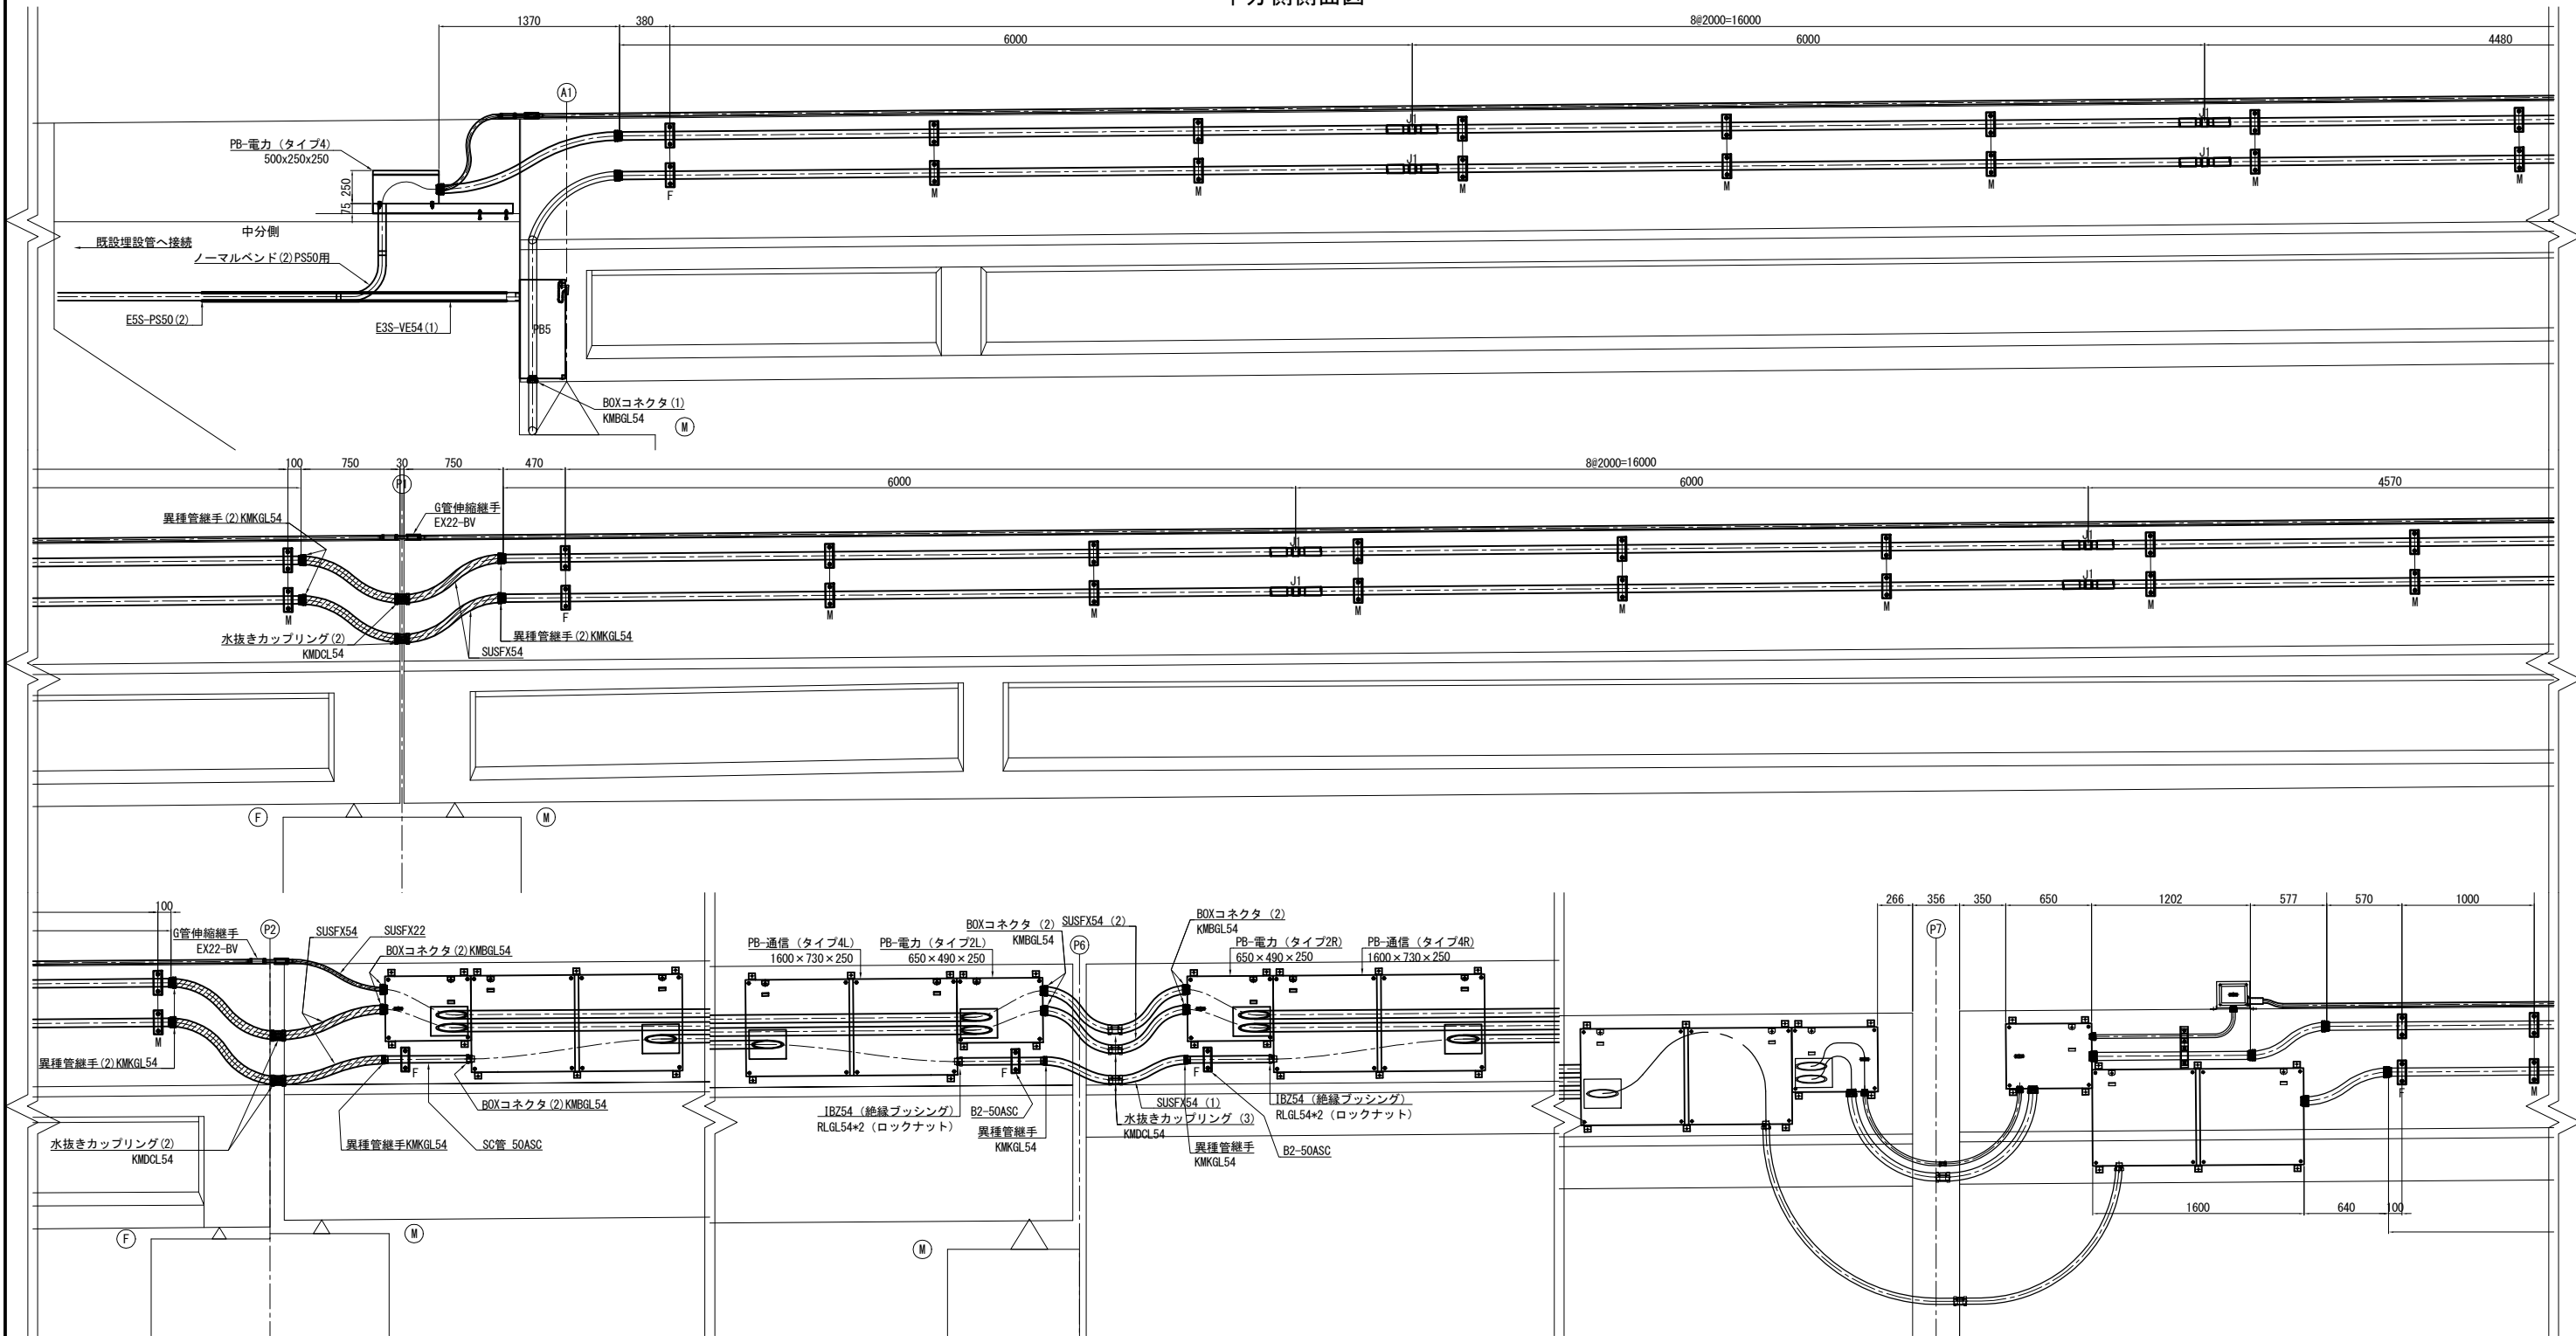


A1橋台正面図

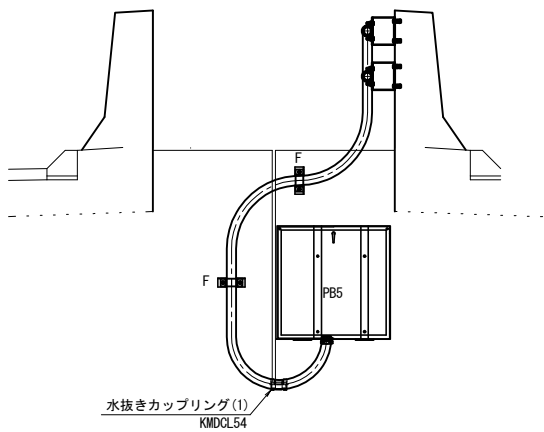

道央自動車道 千歳川大橋（下り線）床版取替工事			
図面の種類	千歳川大橋（下り線）P15-P24 通信管路工詳細図（13）		
縮 尺	図 示	図面番号	/
設計会社名	戸田建設株式会社		
施工会社名	戸田建設株式会社		
事務所名	東日本高速道路株式会社 北海道支社 札幌管理事務所		

千歳川大橋（下り線）P15-P24 通信管路工詳細図（14） S=1:50


中分側側面図

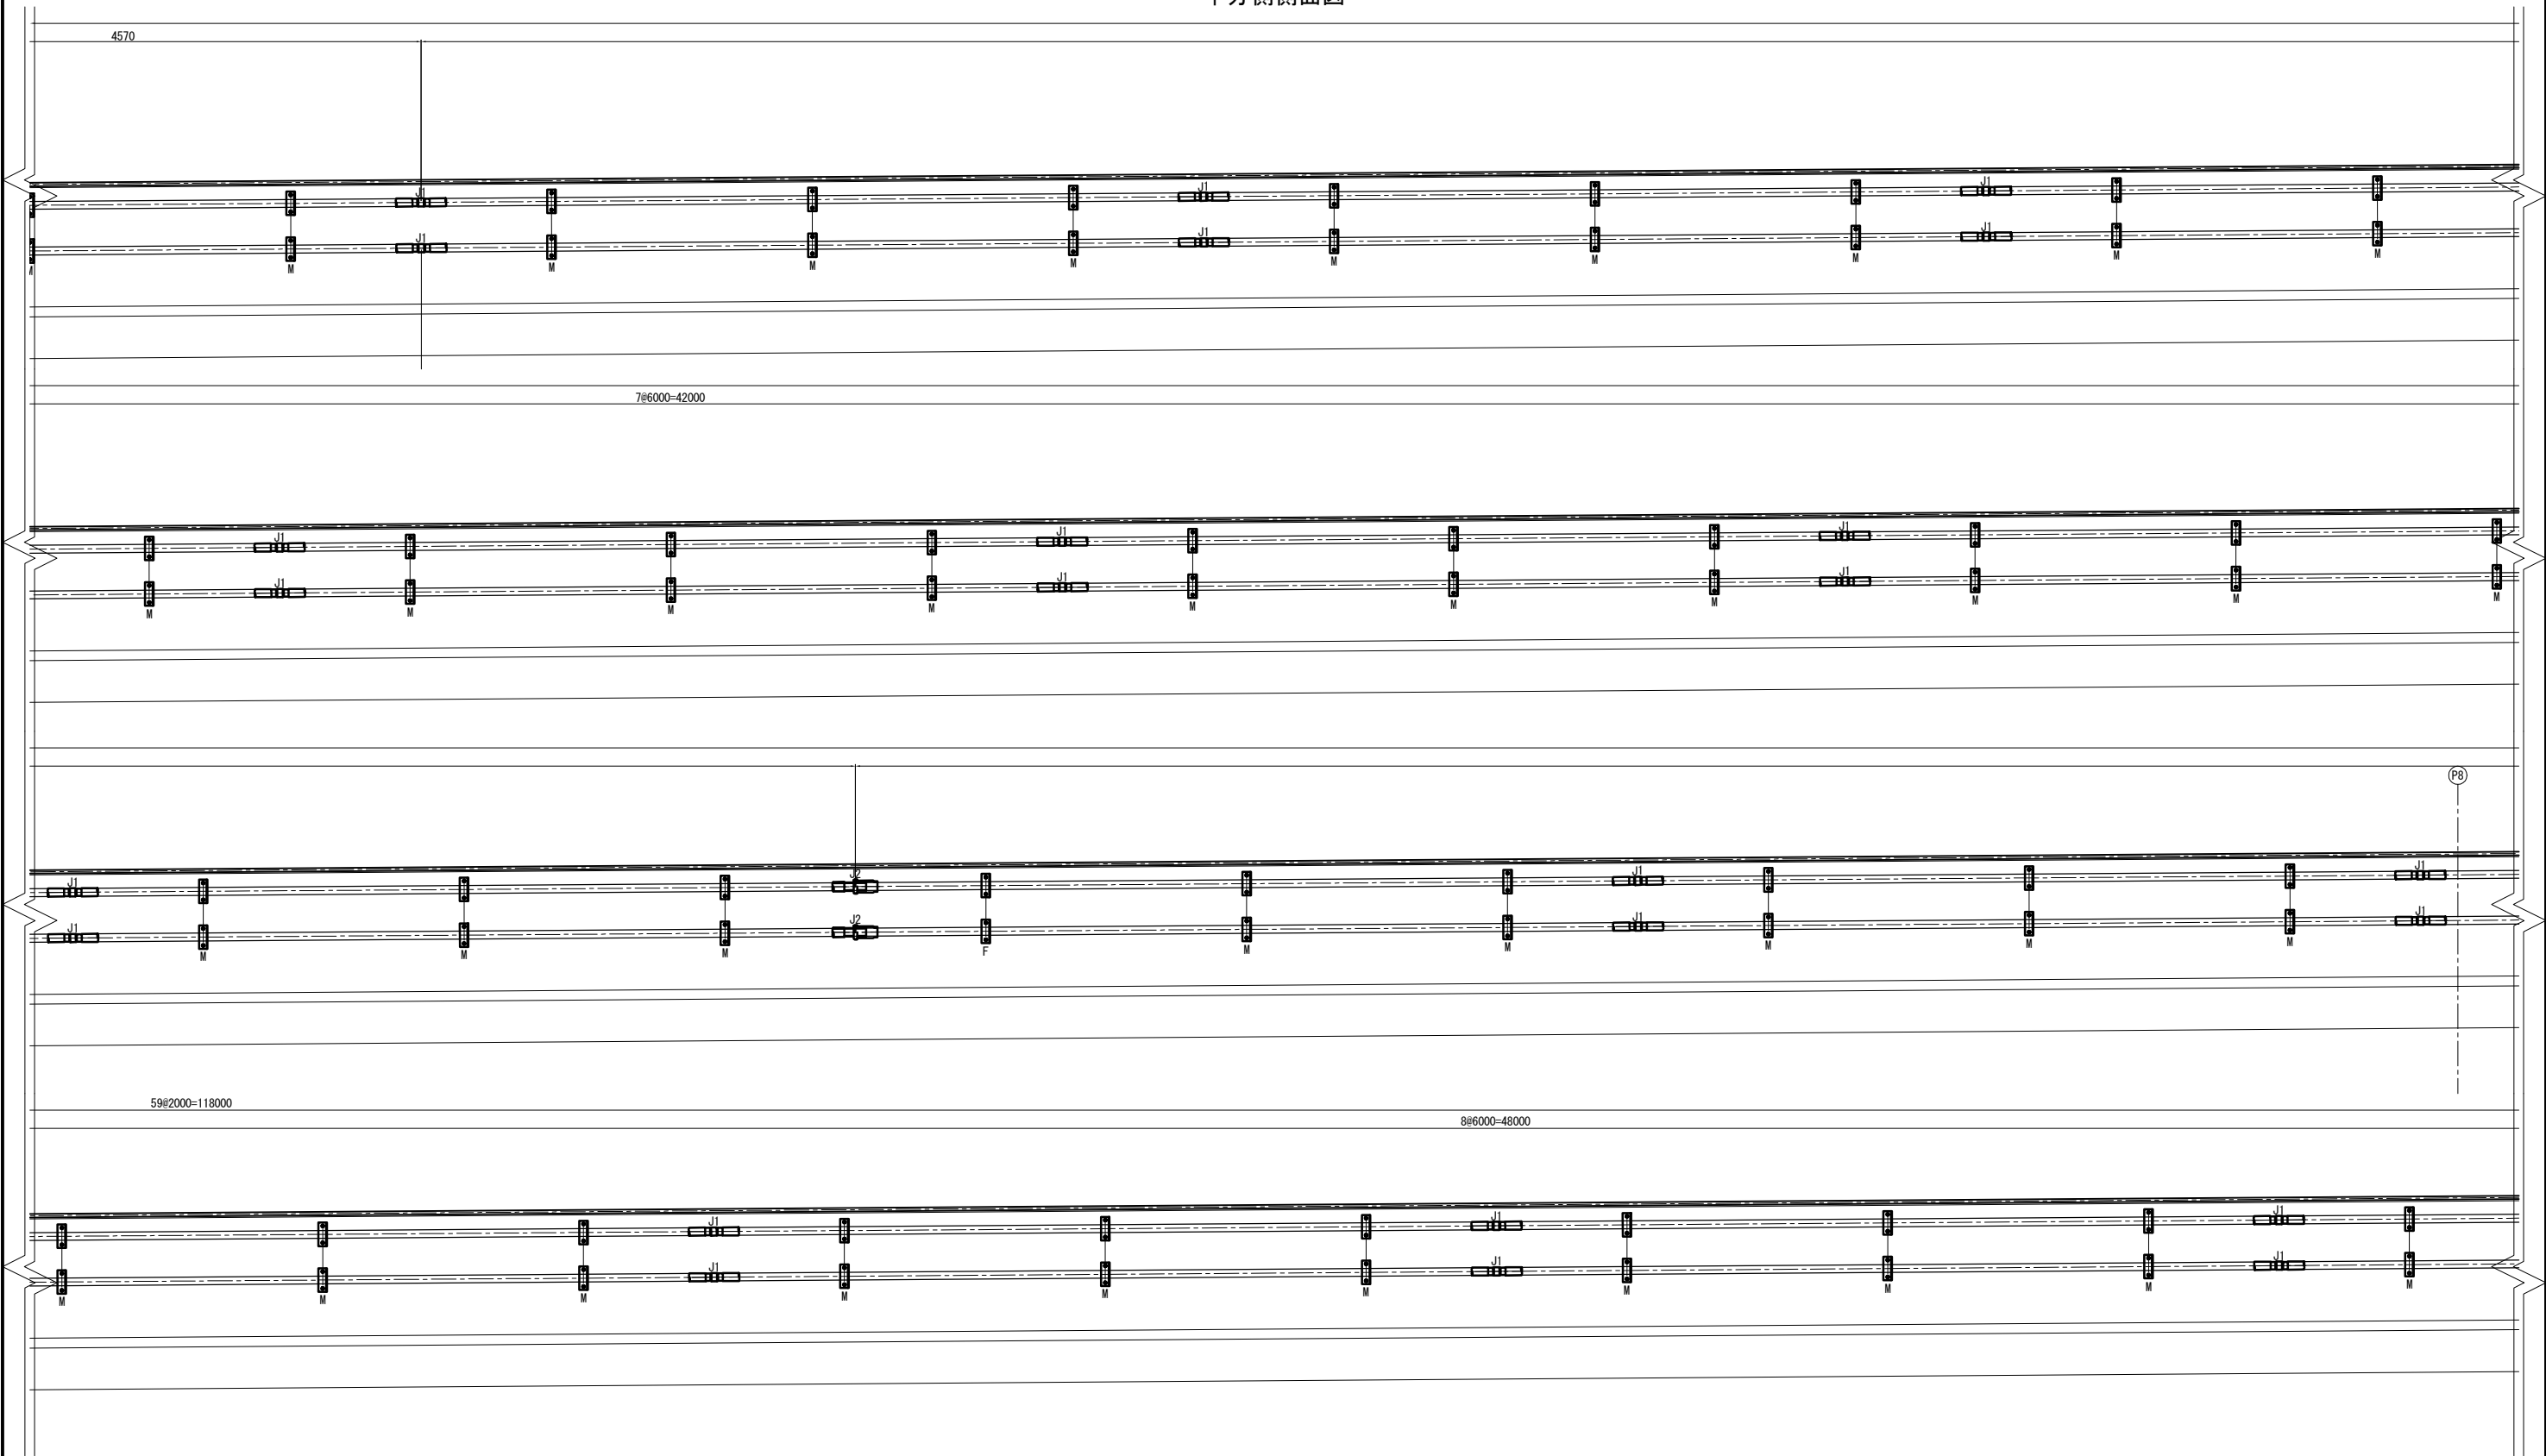

道央自動車道 千歳川大橋（下り線）床版取替工事			
図面の種類	千歳川大橋（下り線）P15-P24 通信管路工詳細図（14）		
縮 尺	図 示	図面番号	/
設計会社名	戸田建設株式会社		
施工会社名	戸田建設株式会社		
事務所名	東日本高速道路株式会社 北海道支社 札幌管理事務所		


千歳川大橋（下り線）P15-P24 通信管路工詳細図（15） S=1:50

中分側側面図

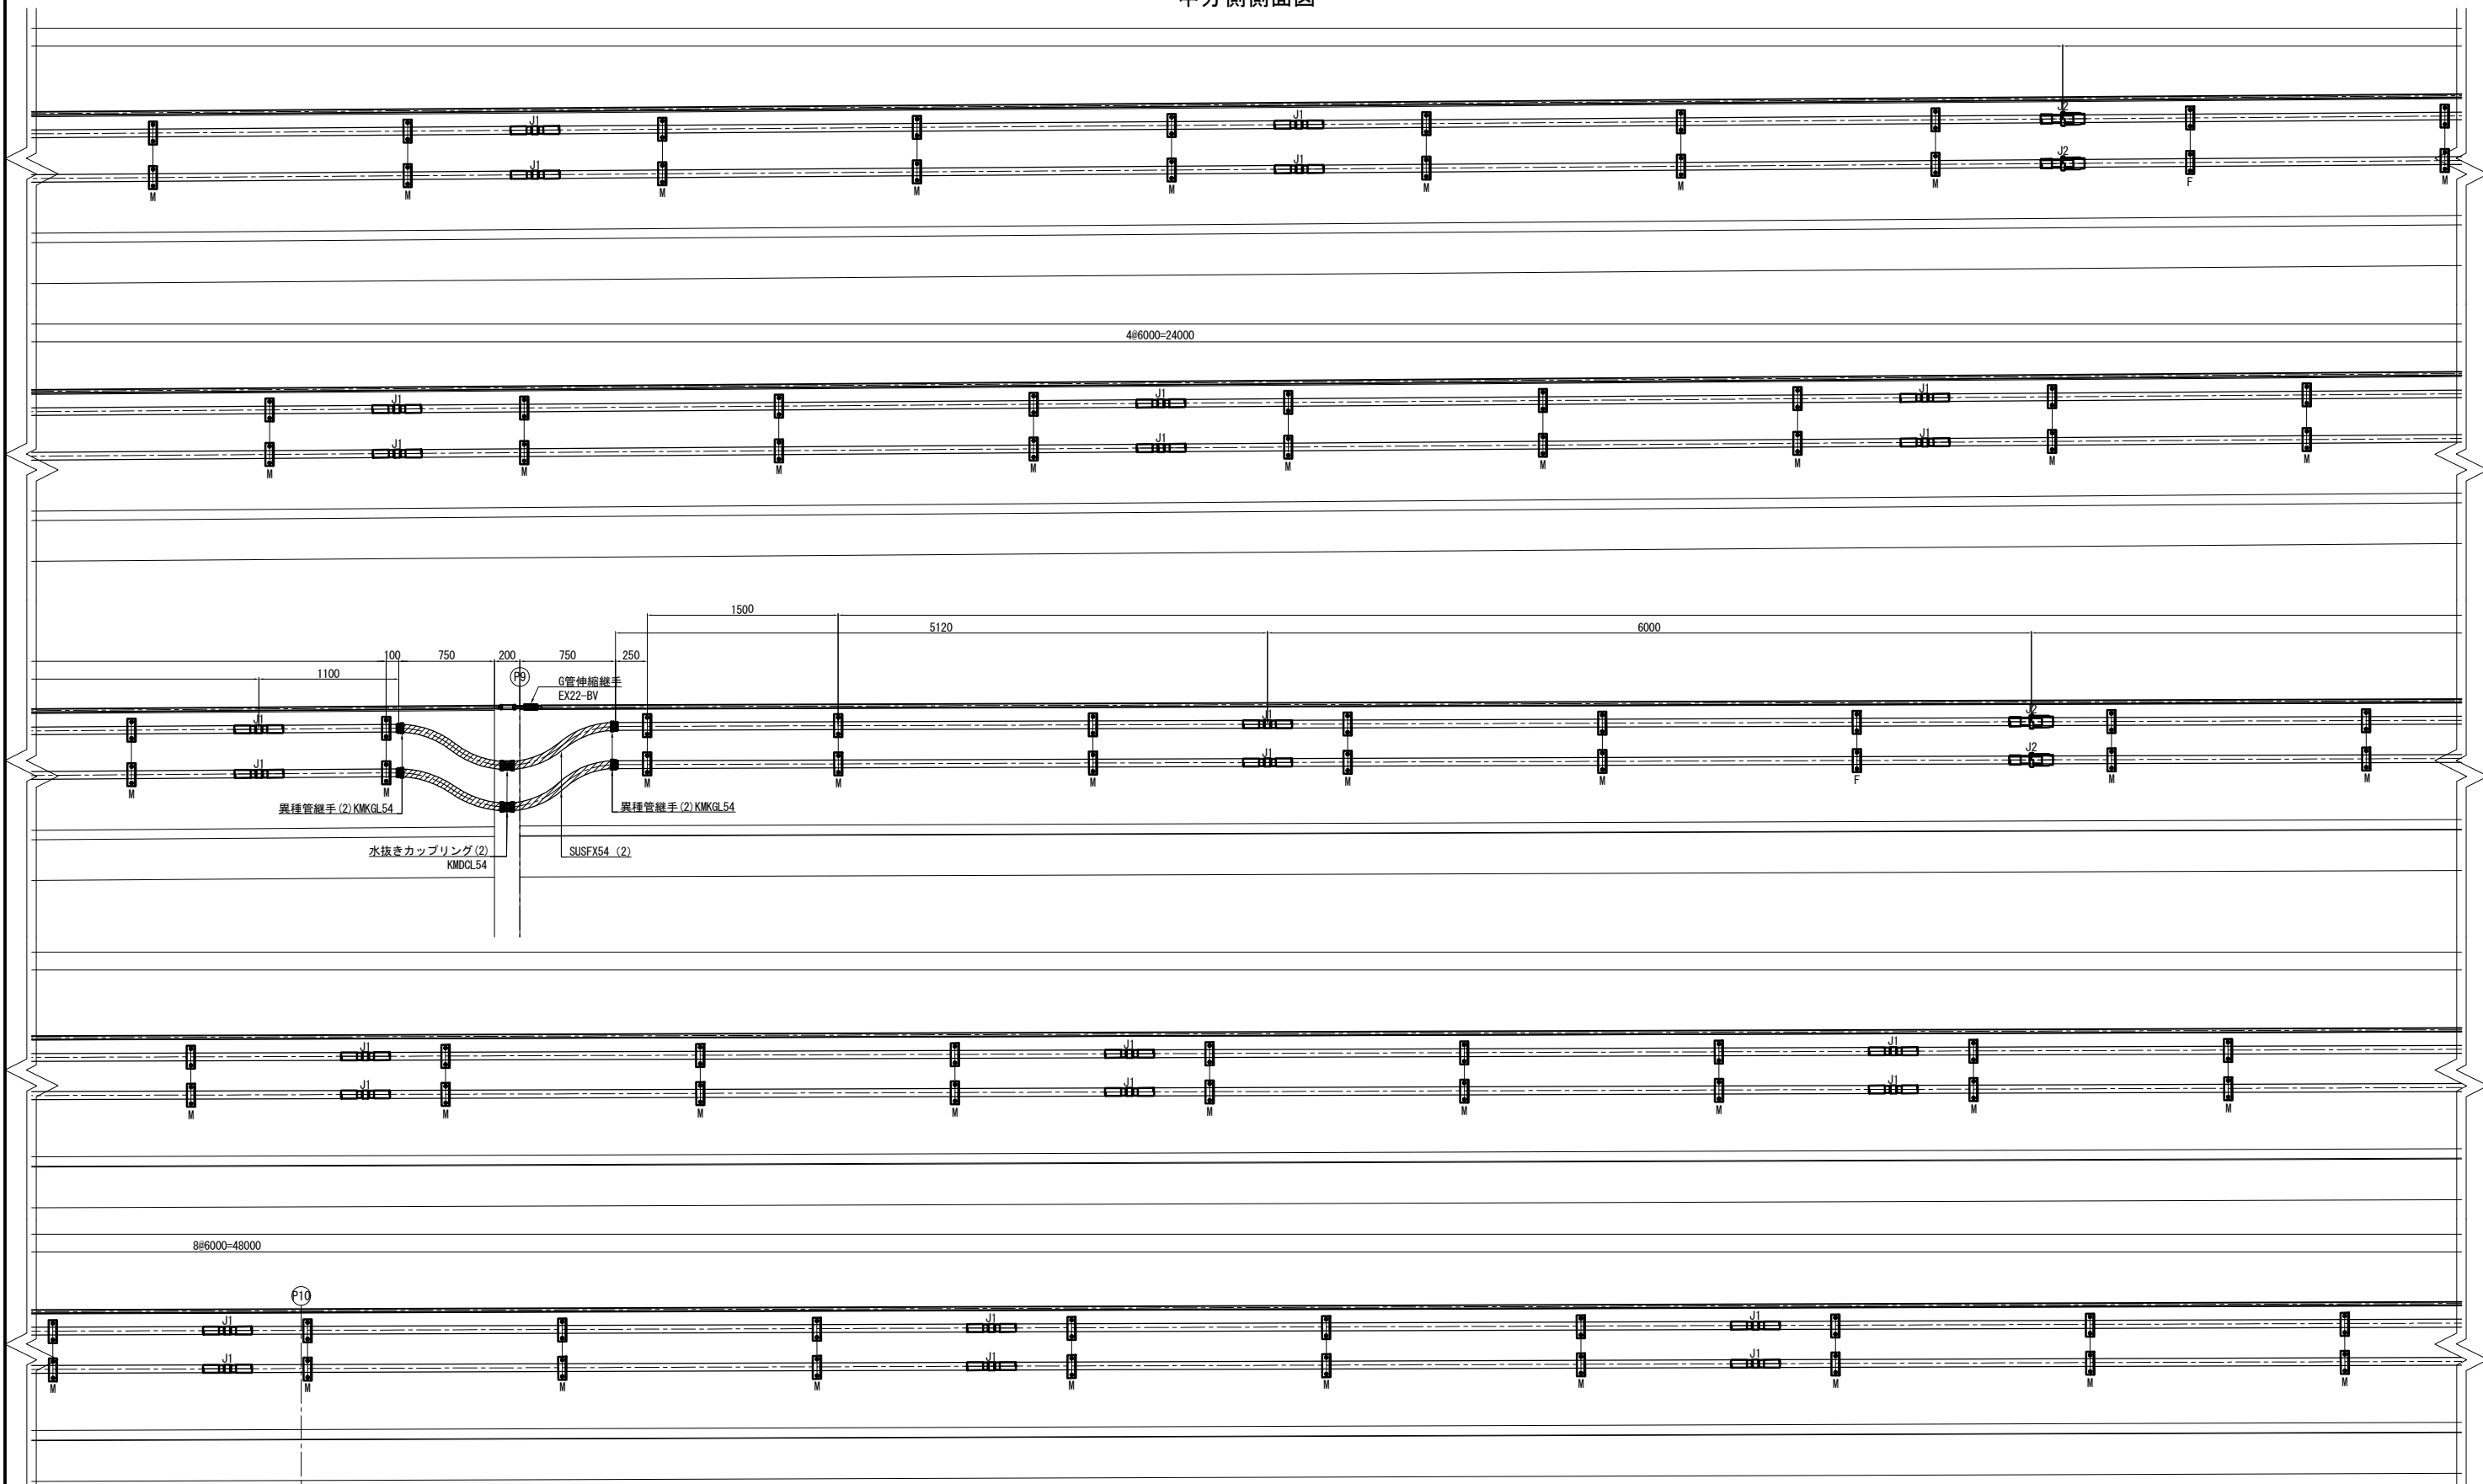

道央自動車道 千歳川大橋（下り線）床版取替工事			
図面の種類	千歳川大橋（下り線）P15-P24 通信管路工詳細図（15）		
縮 尺	図 示	図面番号	/
設計会社名	戸田建設株式会社		
施工会社名	戸田建設株式会社		
事務所名	東日本高速道路株式会社 北海道支社 札幌管理事務所		


千歳川大橋（下り線）P15-P24 通信管路工詳細図（16） S=1:50
中分側側面図

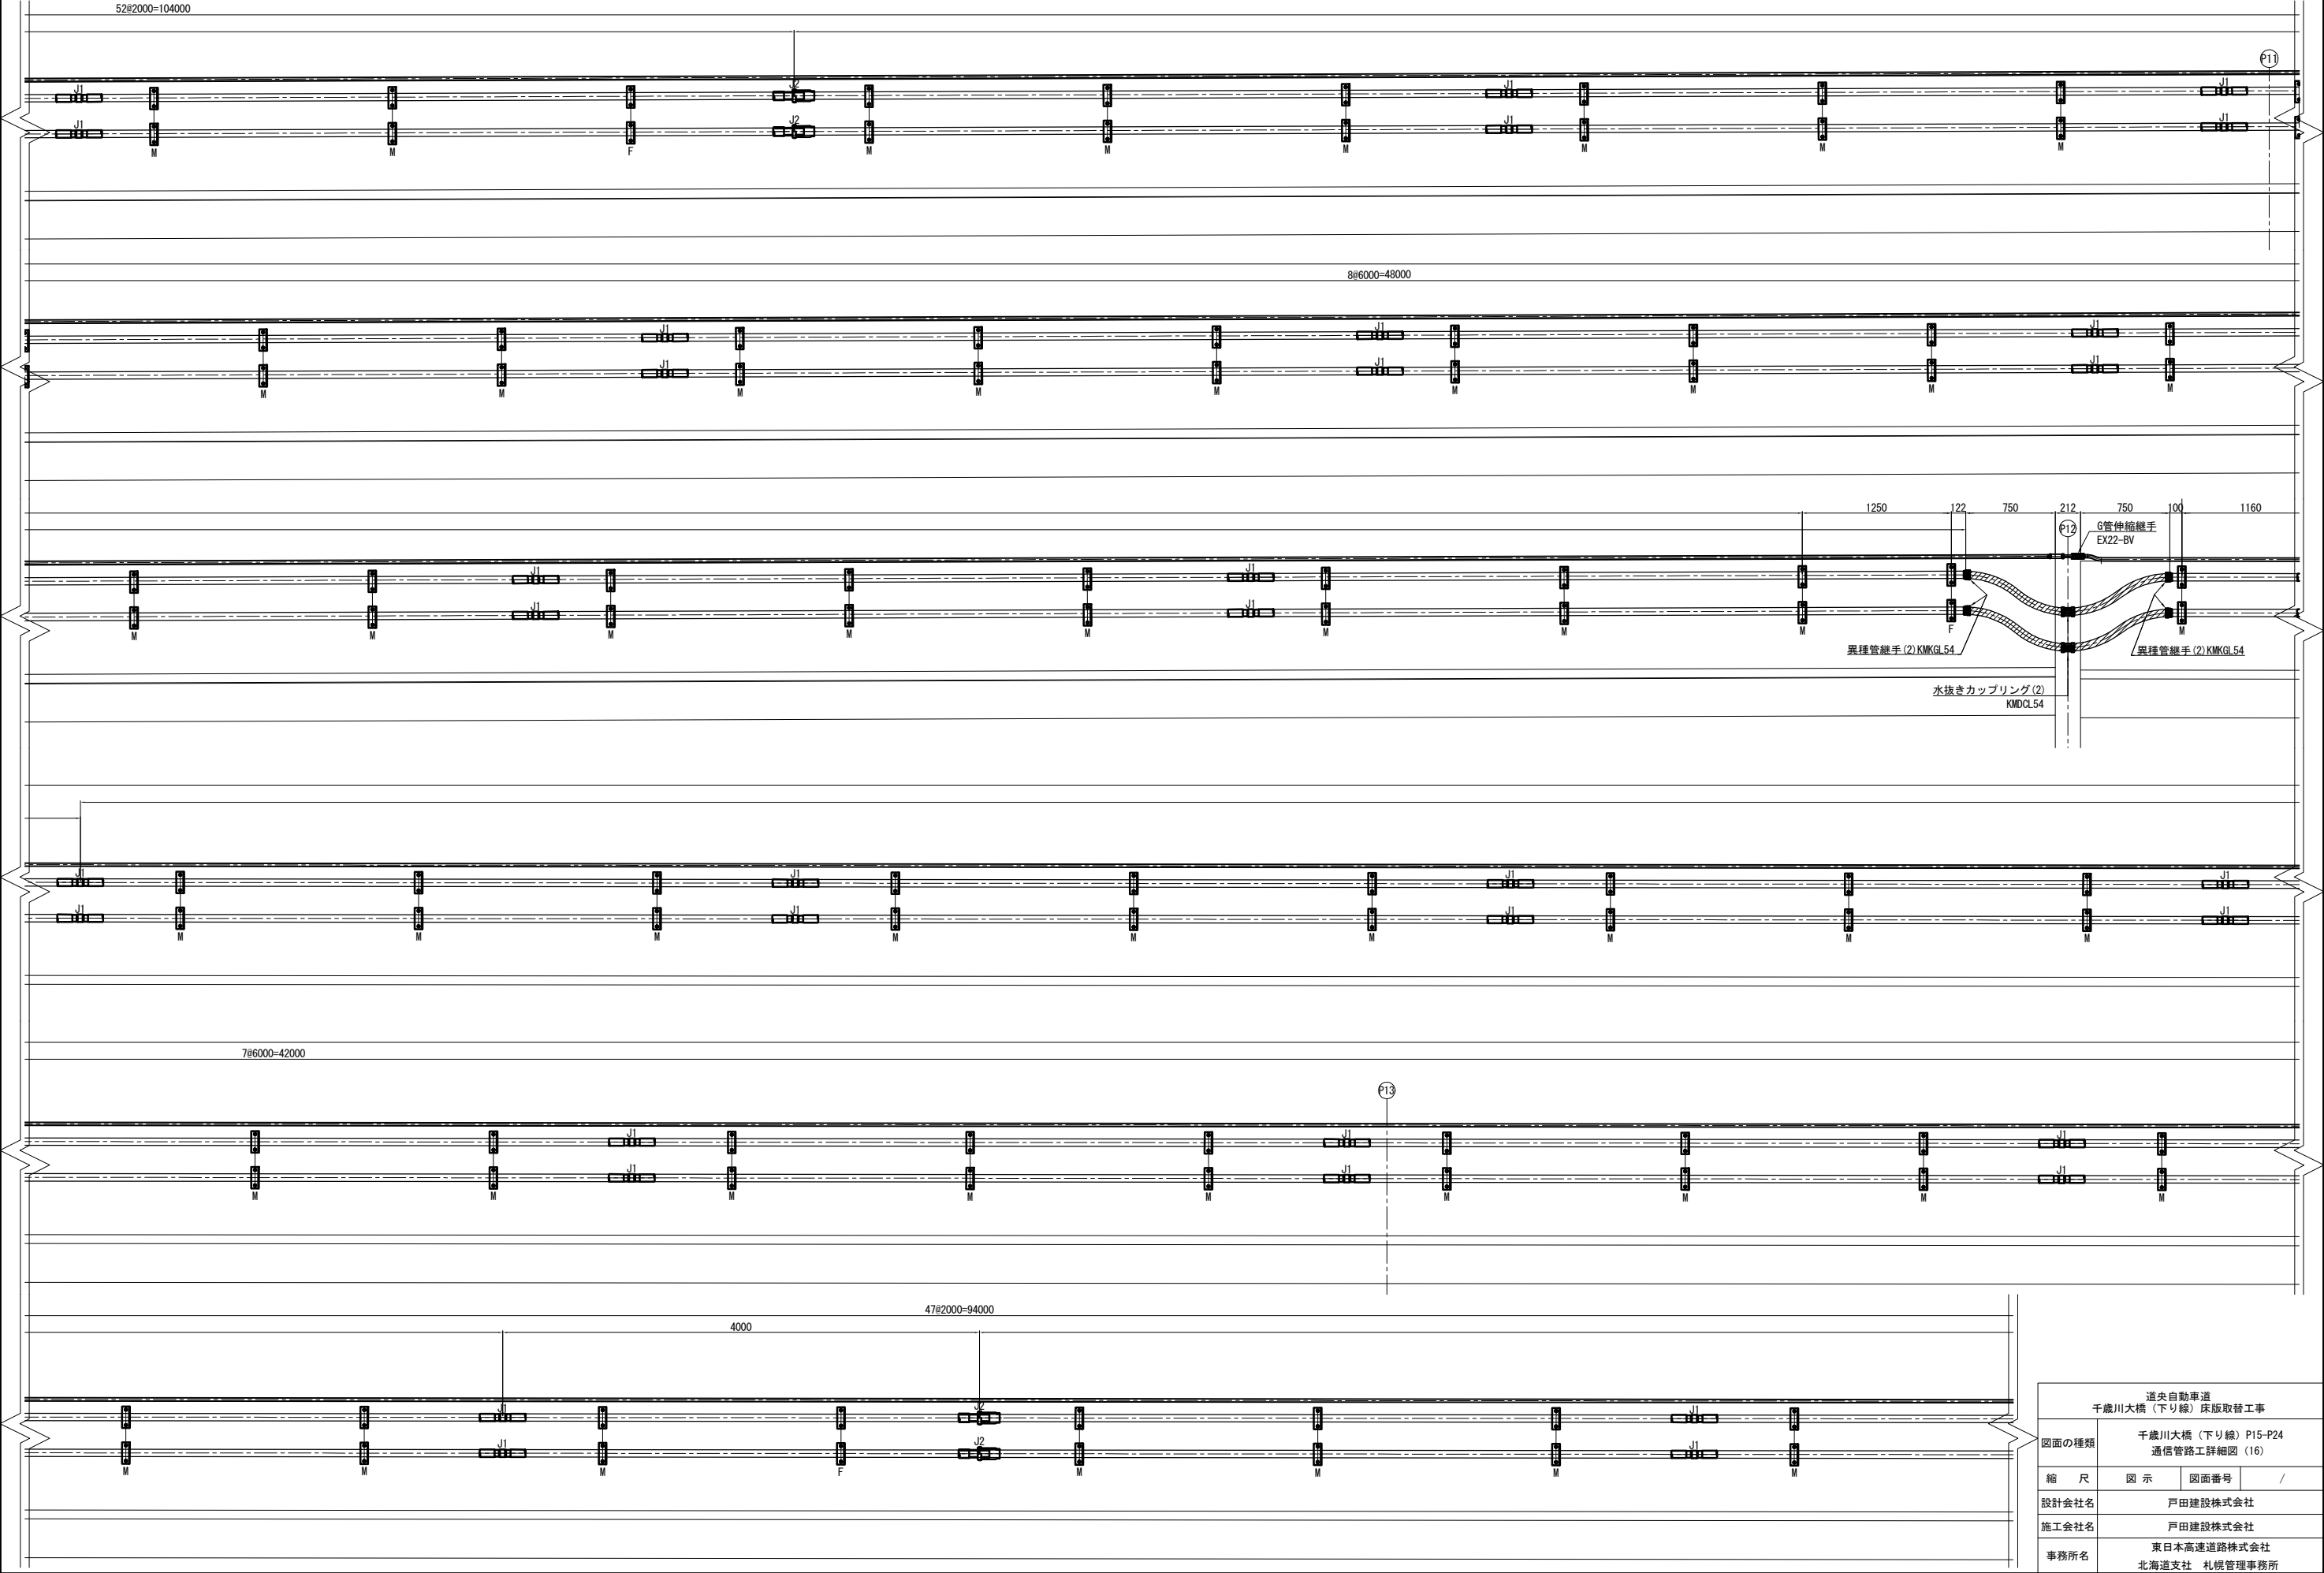

道央自動車道 千歳川大橋（下り線）床版取替工事			
図面の種類	千歳川大橋（下り線）P15-P24 通信管路工詳細図（16）		
縮 尺	図 示	図面番号	/
設計会社名	戸田建設株式会社		
施工会社名	戸田建設株式会社		
事務所名	東日本高速道路株式会社 北海道支社 札幌管理事務所		

千歳川大橋（下り線）P15-P24 通信管路工詳細図（17） S=1:50

中分側側面図

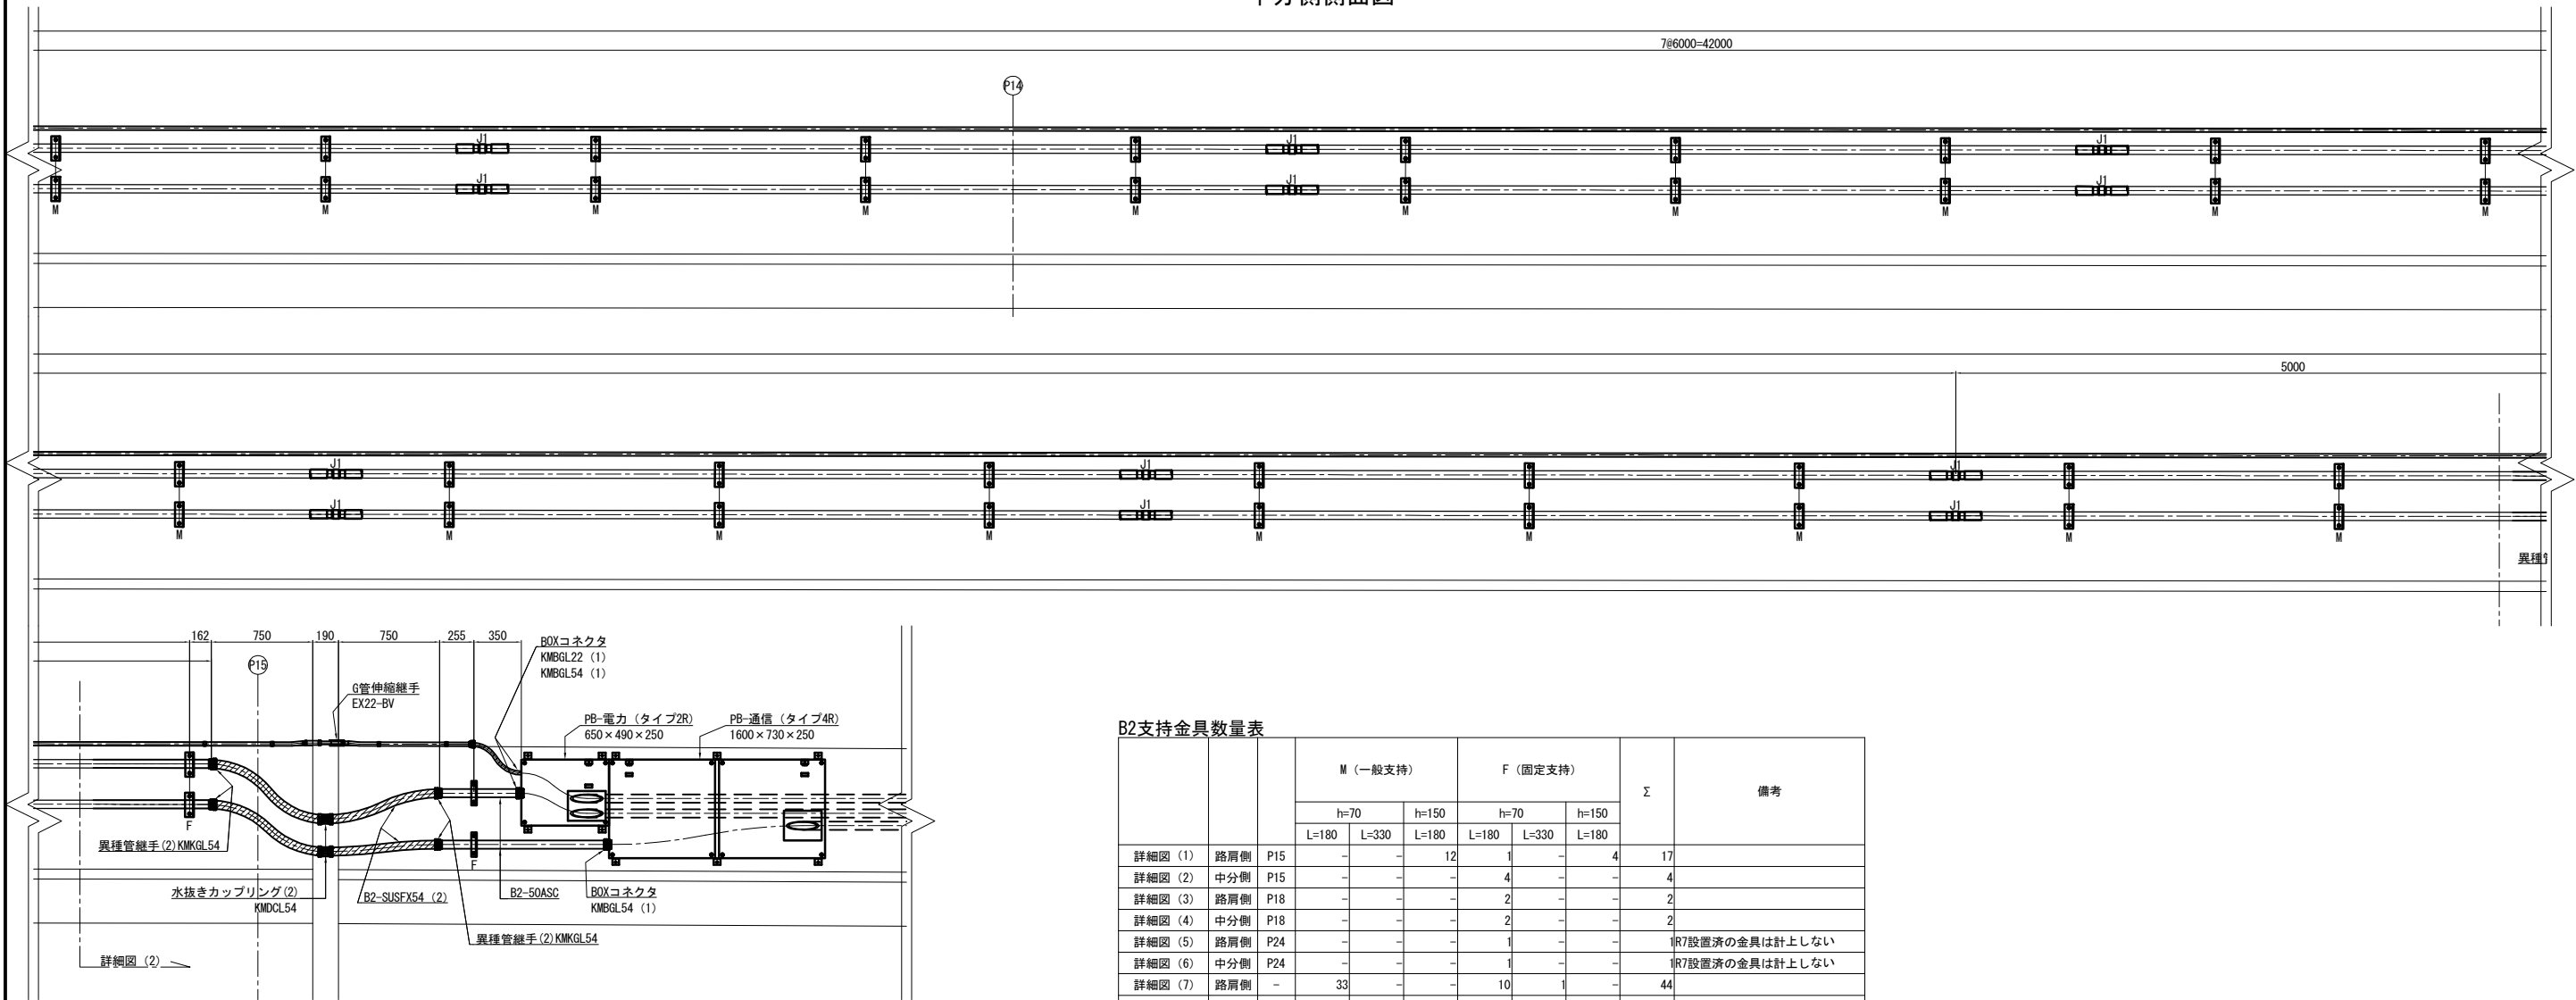

B2支持金具数量表

			M（一般支持）			F（固定支持）			Σ	備考
			h=70		h=150	h=70		h=150		
			L=180	L=330		L=180	L=330			
詳細図（1）	路肩側	P15	-	-	12	1	-	4	17	
詳細図（2）	中分側	P15	-	-	-	4	-	-	4	
詳細図（3）	路肩側	P18	-	-	-	2	-	-	2	
詳細図（4）	中分側	P18	-	-	-	2	-	-	2	
詳細図（5）	路肩側	P24	-	-	-	1	-	-		R7設置済の金具は計上しない
詳細図（6）	中分側	P24	-	-	-	1	-	-		R7設置済の金具は計上しない
詳細図（7）	路肩側	-	33	-	-	10	1	-	44	
詳細図（8）	路肩側	-	66	-	-	4	1	-	71	
詳細図（9）	路肩側	-	94	-	-	2	-	-	96	
詳細図（10）	路肩側	-	54	-	-	4	-	-	58	
詳細図（11）	路肩側	-	14	-	116	-	-	2	132	
詳細図（12）	路肩側	-	-	-	32	0	-	0	32	詳細図（1）分を控除
詳細図（13）	中分側	-	32	-	-	9	-	-	41	
詳細図（14）	中分側	-	74	-	-	4	-	-	78	
詳細図（15）	中分側	-	92	-	-	4	-	-	96	
詳細図（16）	中分側	-	102	-	-	6	-	-	108	
詳細図（17）	中分側	-	38	-	-	0	-	-	38	詳細図（2）分を控除
		Σ	599	0	160	54	2	6	821	


道央自動車道 千歳川大橋（下り線）床版取替工事			
図面の種類	千歳川大橋（下り線）P15-P24 通信管路工詳細図（17）		
縮 尺	図 示	図面番号	/
設計会社名	戸田建設株式会社		
施工会社名	戸田建設株式会社		
事務所名	東日本高速道路株式会社 北海道支社 札幌管理事務所		

千歳川大橋（下り線）P15-P24 ハンドホール詳細図（1） S=1:10





[HH-FE(電力用2条)]



アンカー部詳細 S=1:2

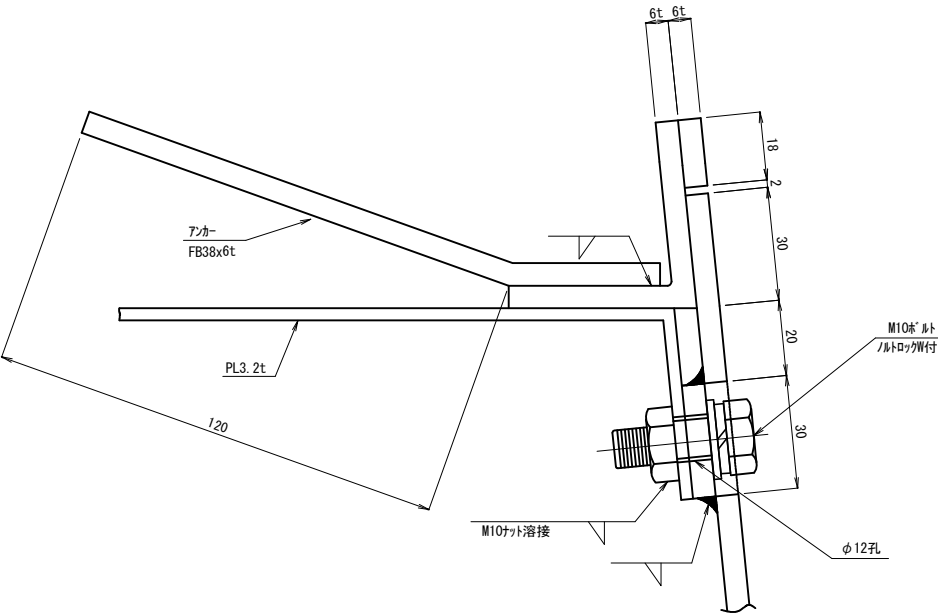

取手部詳細 S=1:2

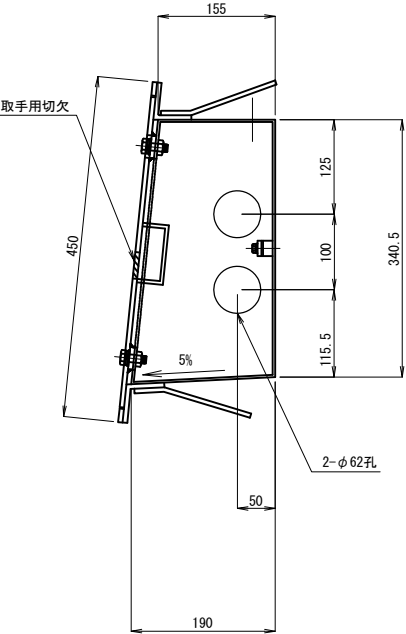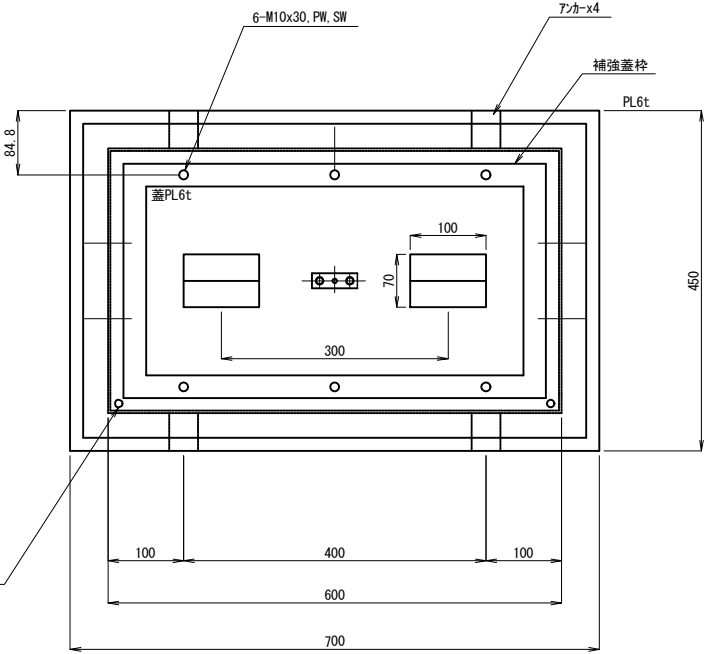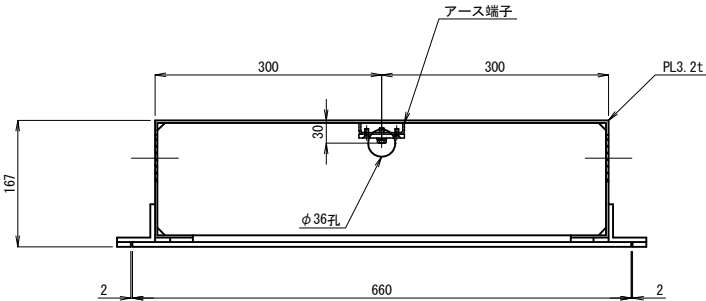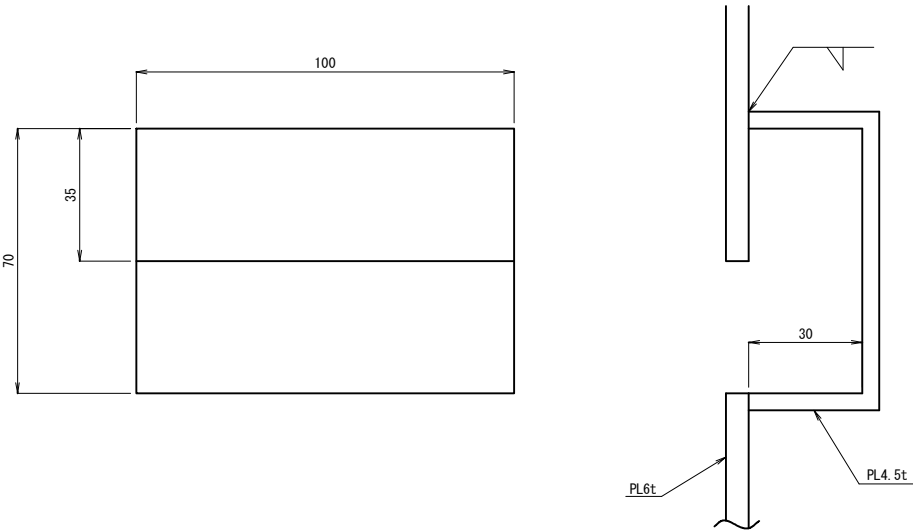


道央自動車道 千歳川大橋（下り線）床版取替工事			
図面の種類	千歳川大橋（下り線）P15-P24 ハンドホール詳細図（1）		
縮 尺	S=1:10	図面番号	/
設計会社名	戸田建設株式会社		
施工会社名	戸田建設株式会社		
事務所名	東日本高速道路株式会社 北海道支社 札幌管理事務所		

千歳川大橋（下り線）P15-P24 ハンドホール詳細図（2） S= 図示


[HH-F4(通信用3条)]

本体図 S=1:10


平面図

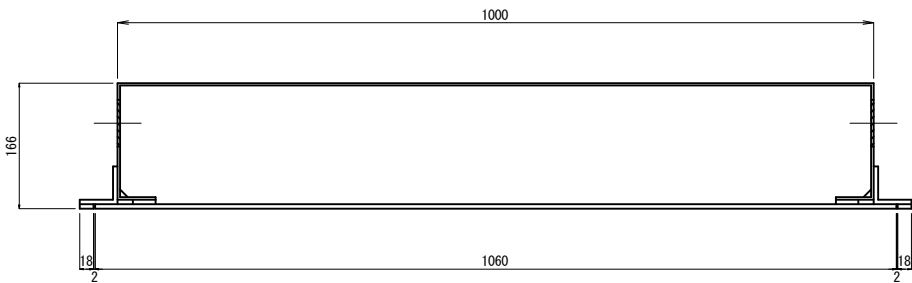


正面図

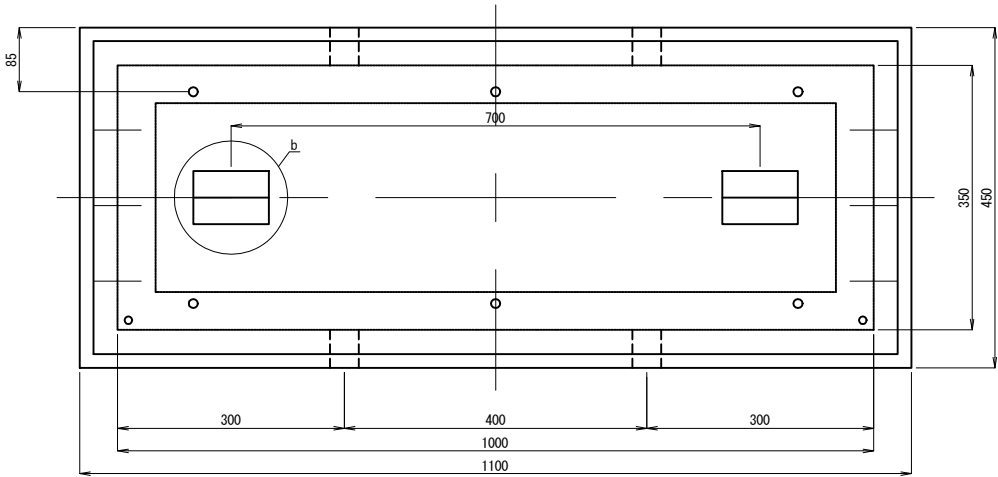

断面図

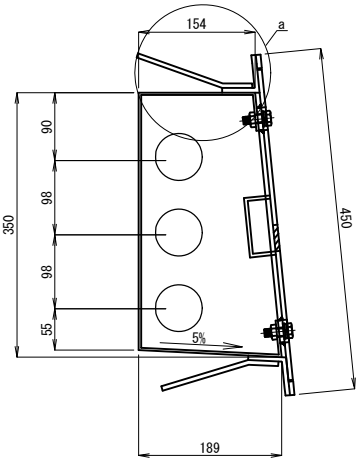


a部詳細図 S=1:4

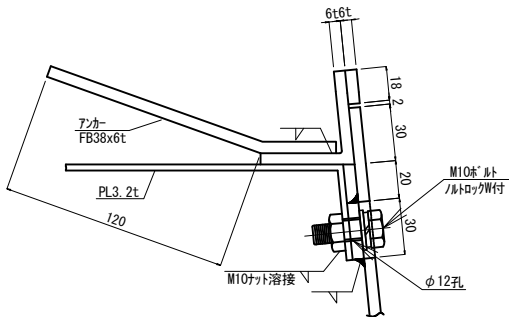


b部詳細図 S=1:4

正面図

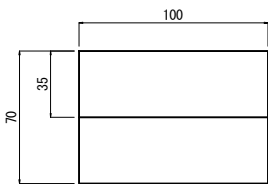

断面図


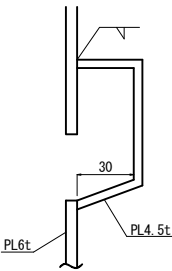


道央自動車道 千歳川大橋（下り線）床版取替工事			
図面の種類	千歳川大橋（下り線）P15-P24 ハンドホール詳細図（2）		
縮 尺	図 示	図面番号	/
設計会社名	戸田建設株式会社		
施工会社名	戸田建設株式会社		
事務所名	東日本高速道路株式会社 北海道支社 札幌管理事務所		


千歳川大橋（下り線）P15-P24 ハンドホール詳細図（3） S=1:10

[ハンドホール OB-A]


OB-A

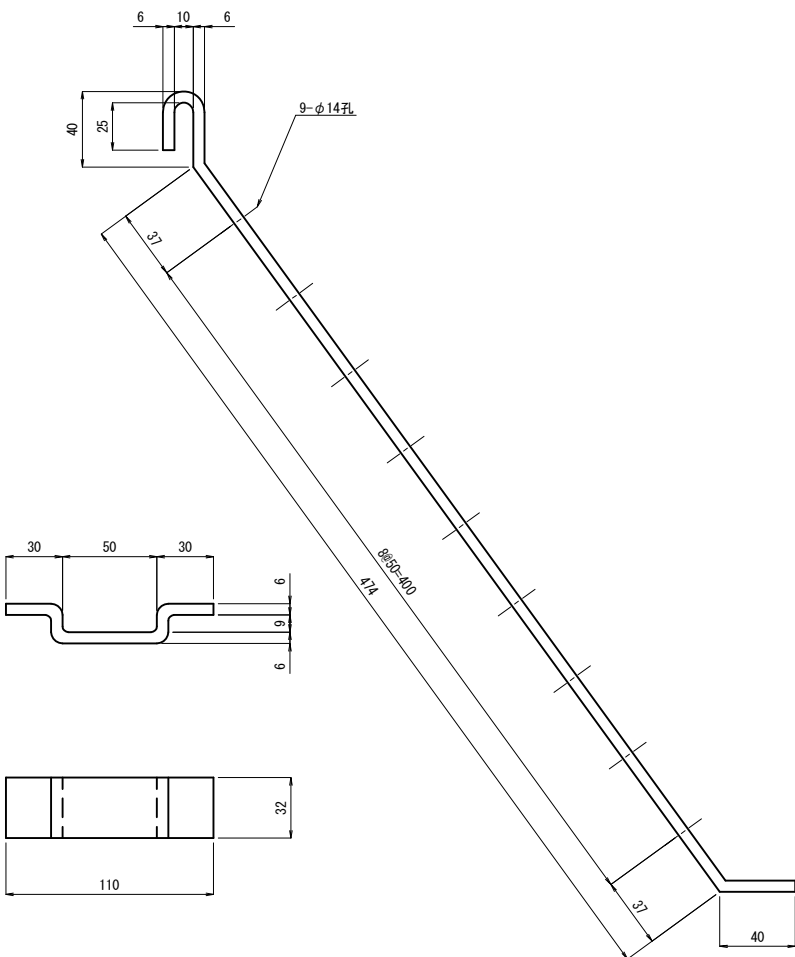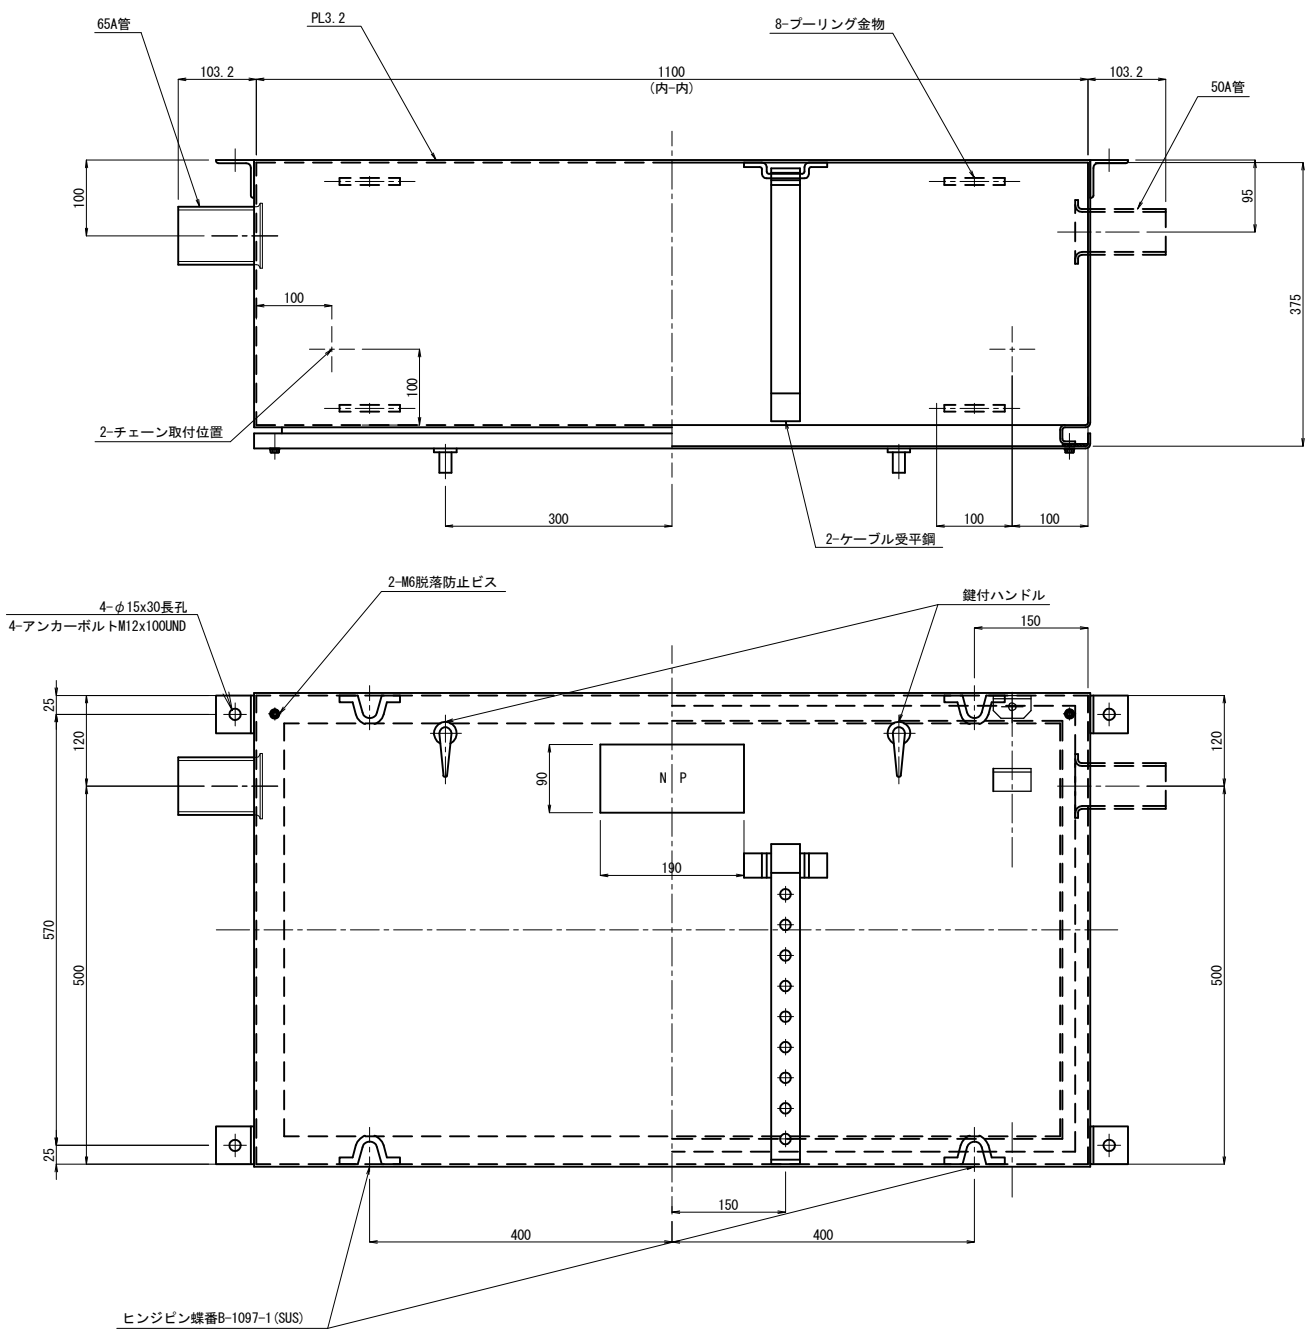


断面図 S=1:4

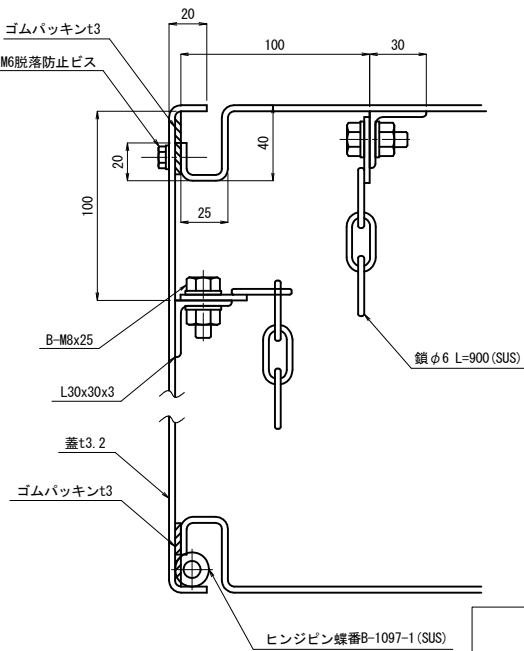

ブーリング金物 S=1:4

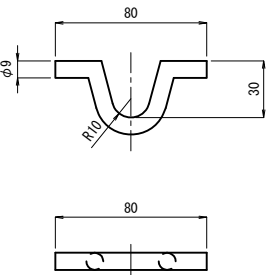


道央自動車道 千歳川大橋（下り線）床版取替工事			
図面の種類	千歳川大橋（下り線）P15-P24 ハンドホール詳細図（3）		
縮 尺	図 示	図面番号	/
設計会社名	戸田建設株式会社		
施工会社名	戸田建設株式会社		
事務所名	東日本高速道路株式会社 北海道支社 札幌管理事務所		

 

※…管出口孔をφ30で製作


遺失自動車道 千歳川大橋（下り線）床版取替工事			
図面の種類	千歳川大橋（下り線）P15～P24 ブルボックス詳細図（通信タイプ4）		
縮 尺	図 示	図面番号	/
設計会社名	戸田建設株式会社		
施工会社名	戸田建設株式会社		
事務所名	東日本高速道路株式会社 北海道支社 札幌管理事務所		

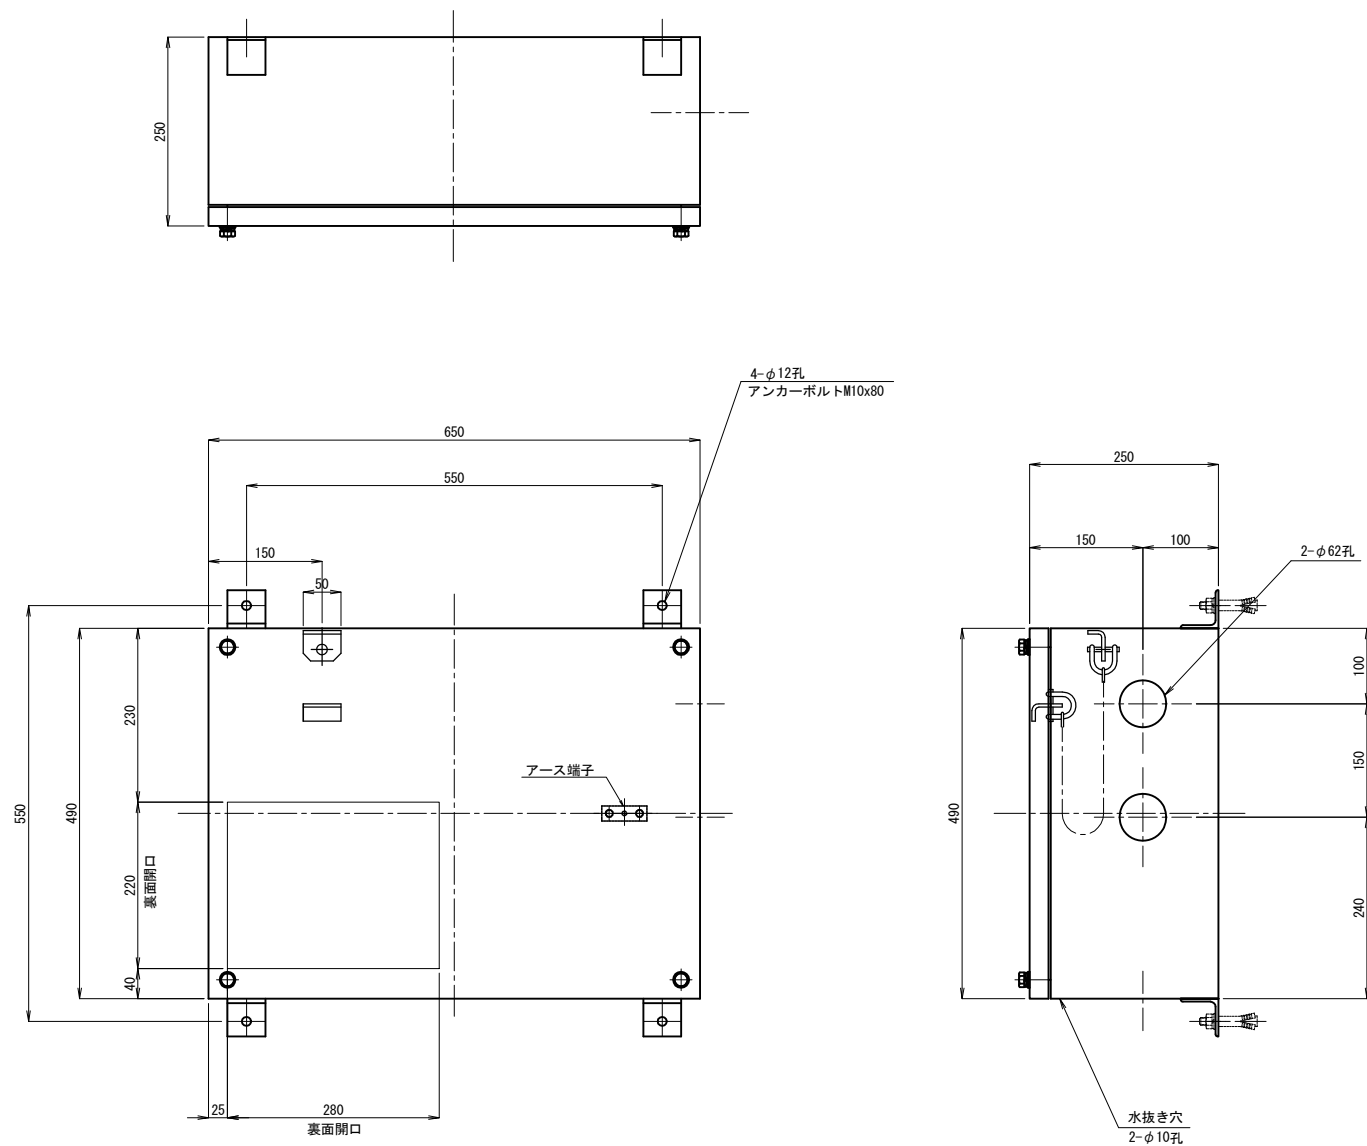

		P15		P18		P24	
		終点側	起点側	終点側	起点側	終点側	起点側
路肩側	PB-通信	タイプ4L	タイプ4R	タイプ4L	タイプ4R	タイプ4L	タイプ4R
	PB-電力	タイプ2L※	タイプ2R	タイプ2L	タイプ2R	タイプ2L	タイプ2R
中分側	PB-通信	タイプ4R	タイプ4L	タイプ4R	タイプ4L	タイプ4R	タイプ4L
	PB-電力	タイプ2R※	タイプ2L	タイプ2R	タイプ2L	タイプ2R	タイプ2L

※…管出口孔をφ30で製作

蓋部詳細図 S=1:2



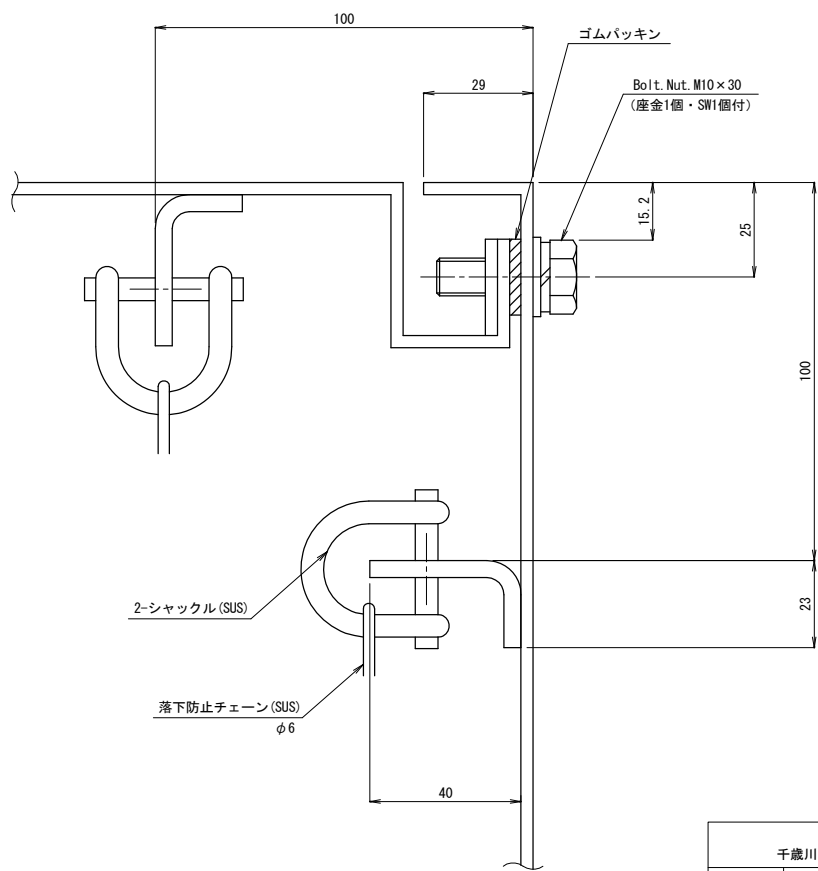


※勝手違い：PB-電力(タイプ2R)


道央自動車道 千歳川大橋（下り線）床版取替工事			
図面の種類	千歳川大橋（下り線）P15-P24 プルボックス詳細図（電力タイプ2）		
縮 尺	図 示	図面番号	/
設計会社名	戸田建設株式会社		
施工会社名	戸田建設株式会社		
事務所名	東日本高速道路株式会社 北海道支社 札幌管理事務所		

千歳川大橋（下り線）P15-P24 プルボックス詳細図（電力タイプ3） S=1:10

[電力(タイプ3)]

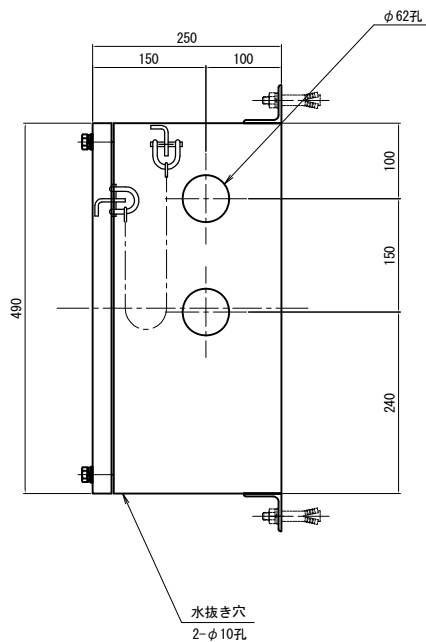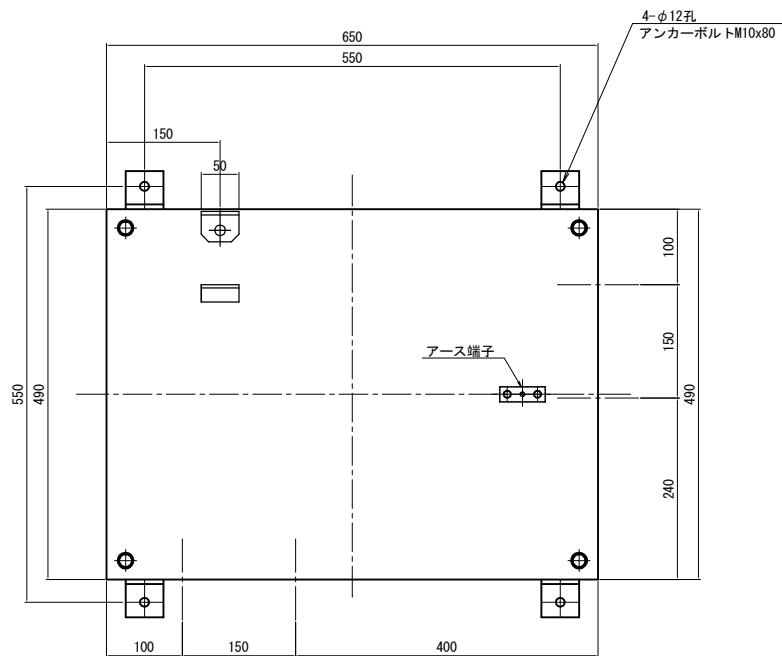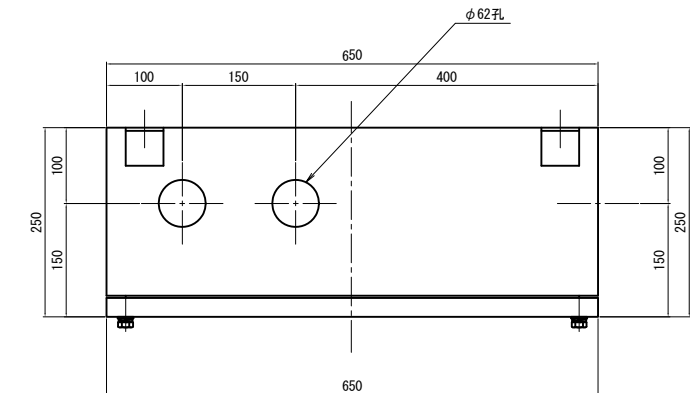

蓋部詳細図 S=1:2

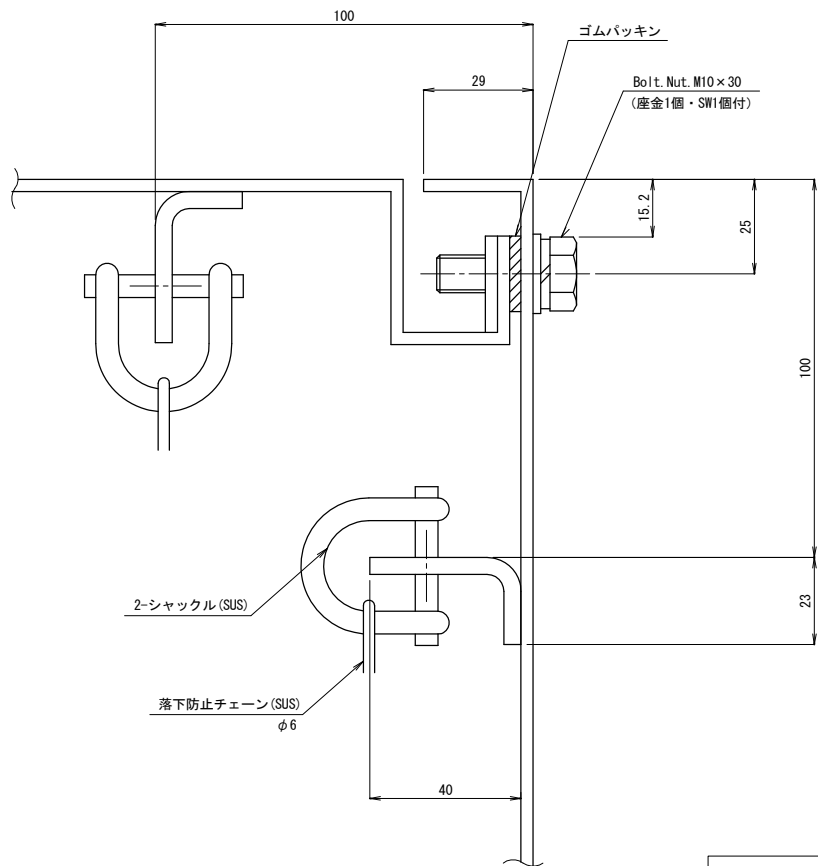


道央自動車道 千歳川大橋（下り線）床版取替工事			
図面の種類	千歳川大橋（下り線）P15-P24 プルボックス詳細図（電力タイプ3）		
縮 尺	図 示	図面番号	/
設計会社名	戸田建設株式会社		
施工会社名	戸田建設株式会社		
事務所名	東日本高速道路株式会社 北海道支社 札幌管理事務所		

千歳川大橋（下り線）P15-P24 プルボックス詳細図（電力タイプ4）S=1:15


[電力(タイプ4)]

設置図

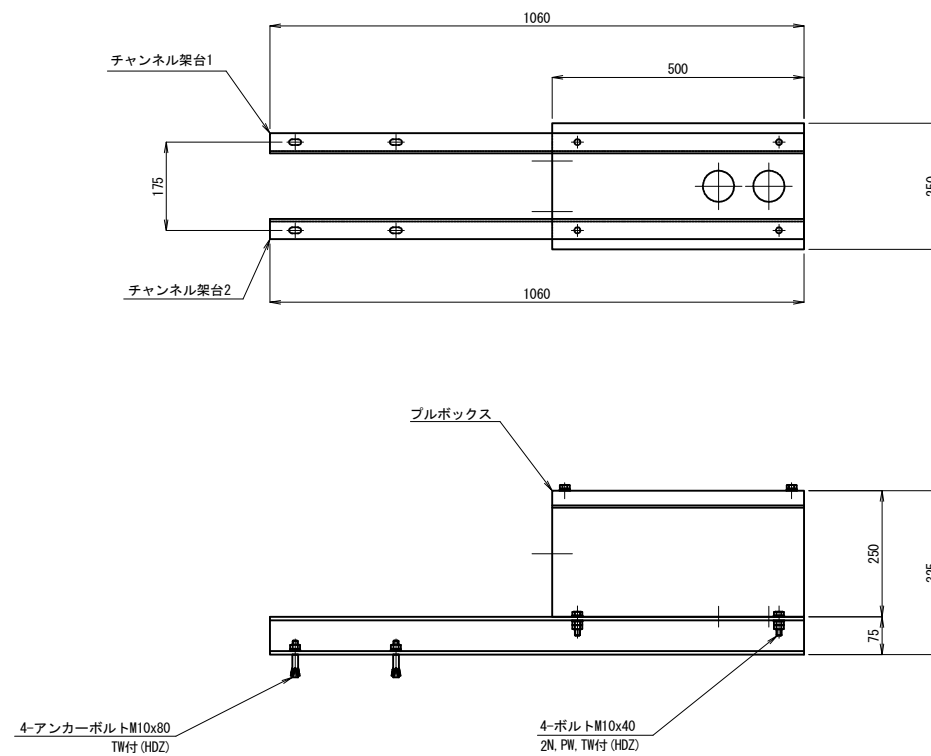


蓋部詳細図

S=1:3

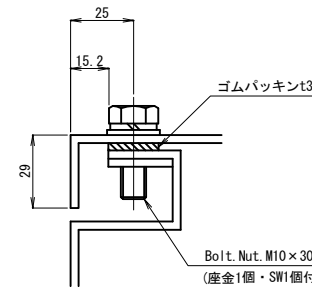


プルボックス

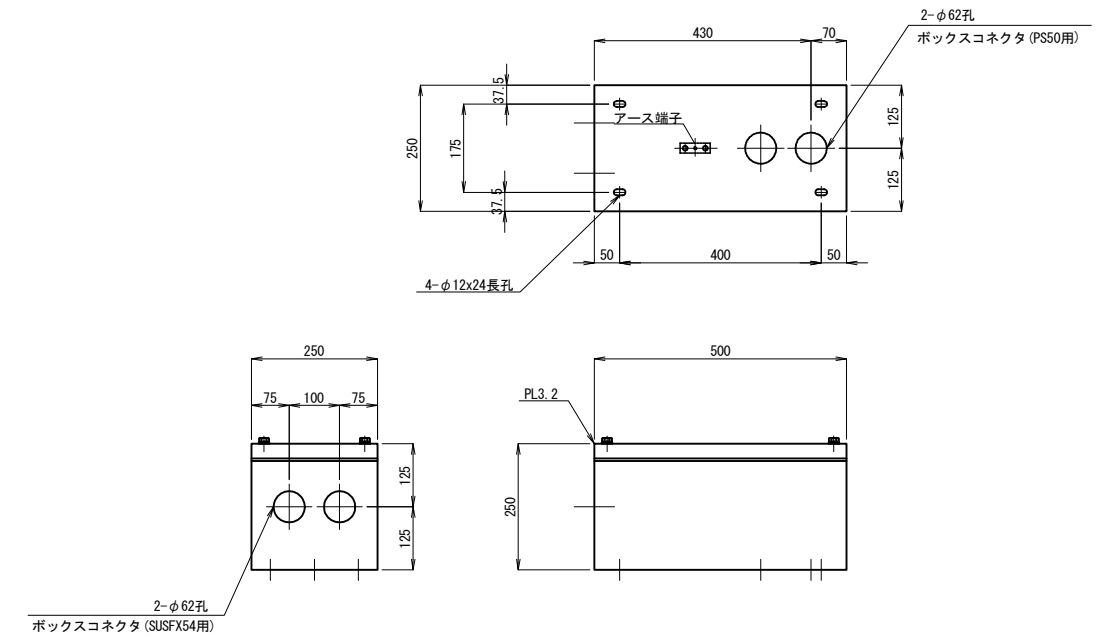

チャンネル架台1

反転：チャンネル架台2

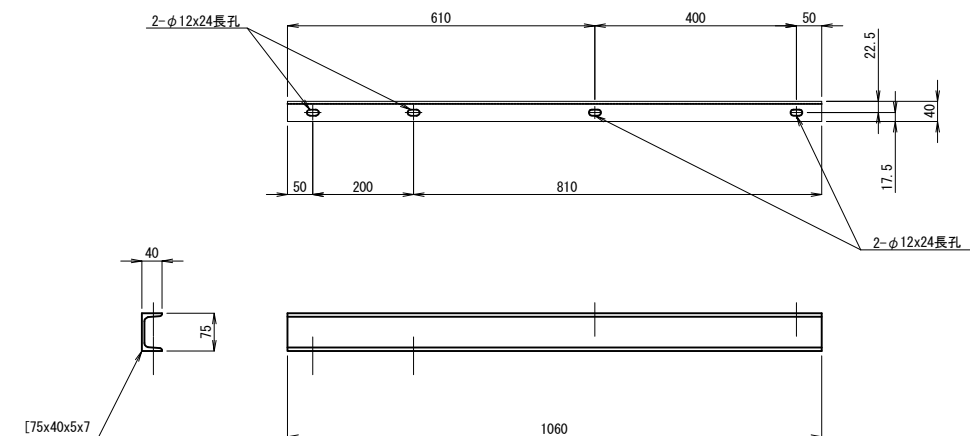

道央自動車道 千歳川大橋（下り線）床版取替工事			
図面の種類	千歳川大橋（下り線）P15-P24 プルボックス詳細図（電力タイプ4）		
縮 尺	S=1:10	図面番号	/
設計会社名	戸田建設株式会社		
施工会社名	戸田建設株式会社		
事務所名	東日本高速道路株式会社 北海道支社 札幌管理事務所		